上接㉓段

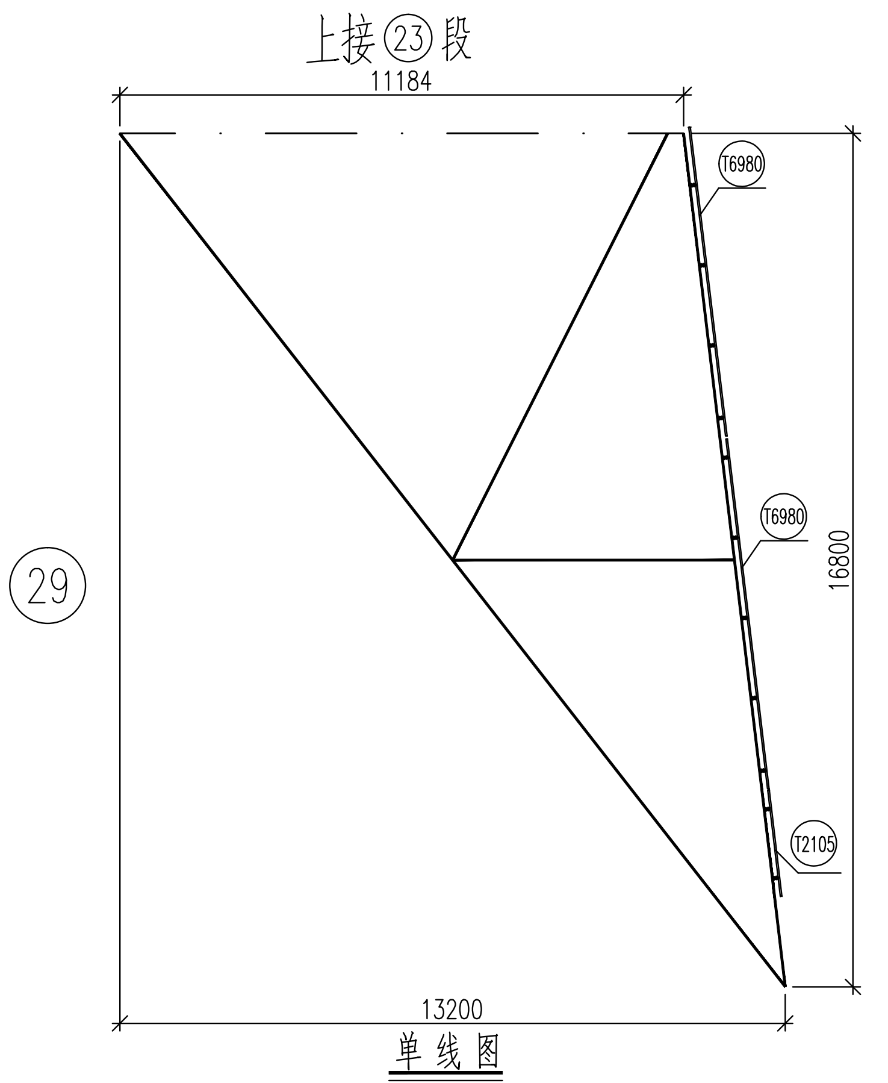

11184
16800
13200
㉙
T6980
T6980
T2105

单线图
1:150

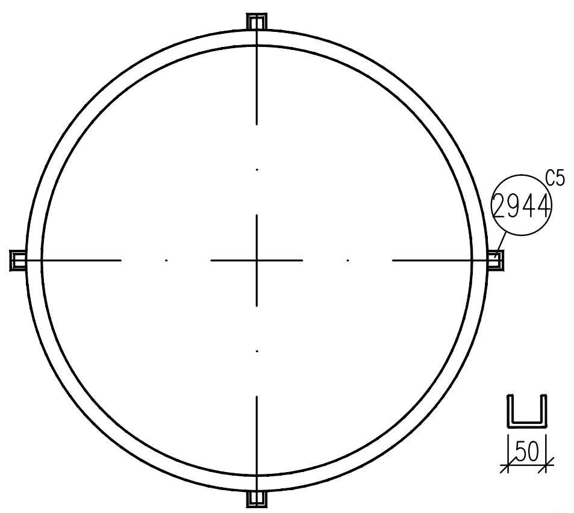

安全带挂点示意
扶手设置示意

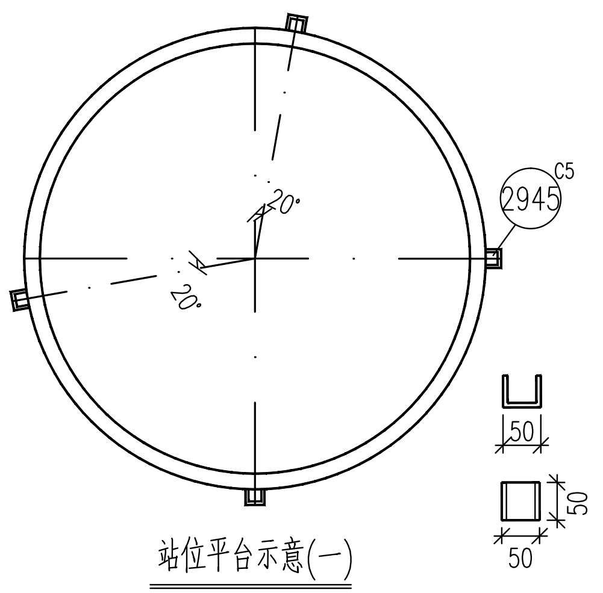

2945
C5
20°
50

站位平台示意(一)

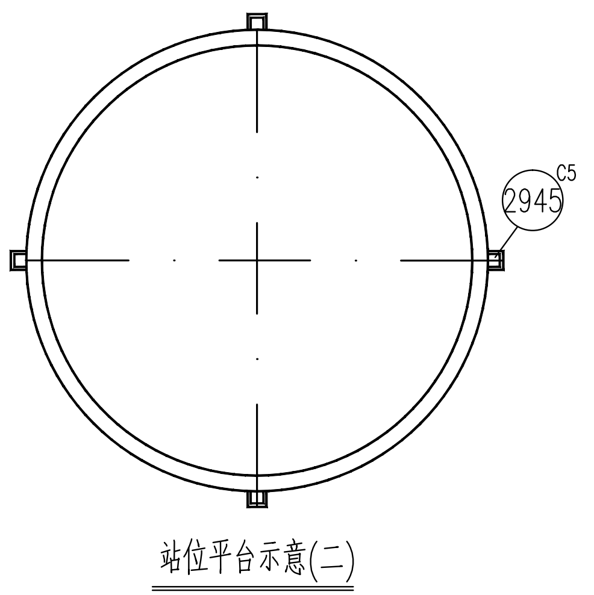

站位平台示意(二)

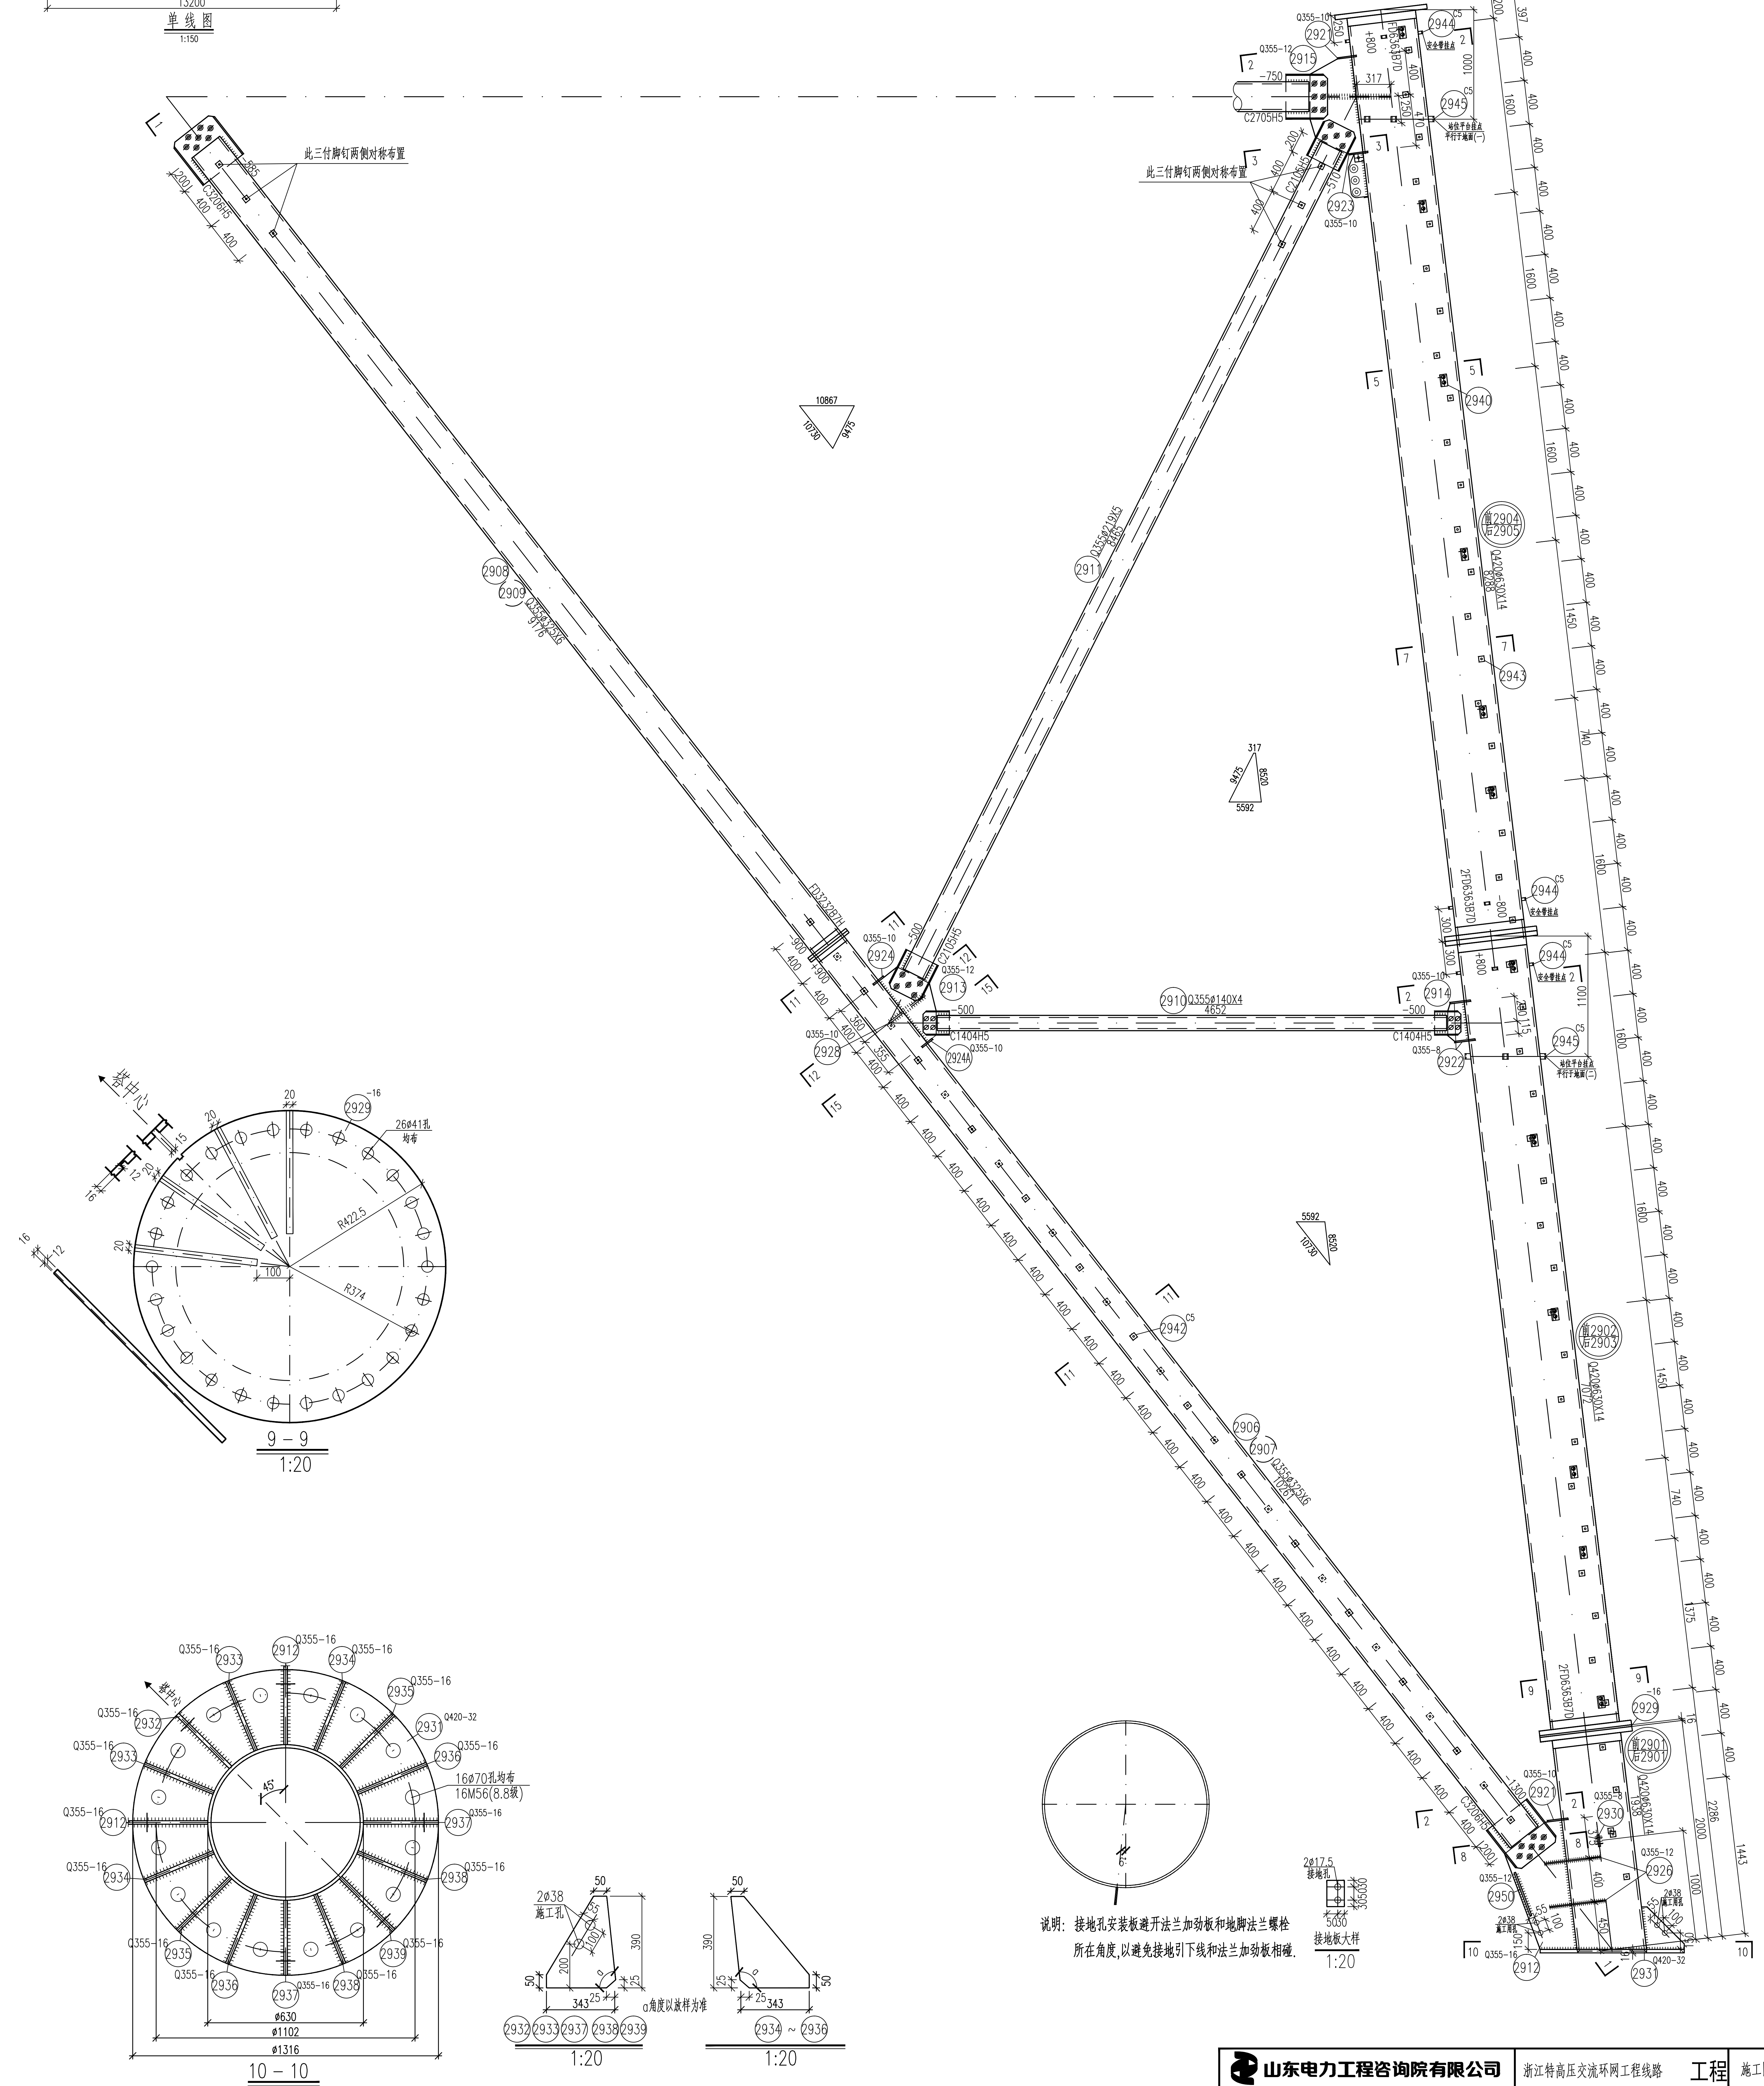

此三付脚钉两侧对称布置
C3206H5
Q355-10
2921
Q355-12
2915
-750
C2705H5
317
2944
安全带挂点
2945
站位平台挂点
平行于地面(一)
C2105H5
2923
FD6363B7D
+800
1000
1600
400
2940
2911
Q355Φ219X5
10867
10930
9475
2908
2909
Q355Φ325X6
2904
2905
Q420Φ630X14
2943
317
8520
5592
1450
740
FD3202H
2924
2913
C2105H5
Q355-10
Q355-12
2910
Q355Φ140X4
4652
C1404H5
-500
2914
2922
Q355-8
2928
2924A
2906
2907
2942
2902
2903
2FD6363B7D
2929
2901
2921
2930
2926
2950
2912
2931
Q420-32
Q355-16
C3206H5
2286
2000
1443
1375

说明：接地孔安装板避开法兰加劲板和地脚法兰螺栓
所在角度,以避免接地引下线和法兰加劲板相碰.

2Ø17.5
接地孔
5030
305030

接地板大样
1:20

塔中心
20
-16
2929
26Ø41孔
均布
R422.5
R374
100
15
16
12

9 - 9
1:20

塔中心
Q355-16
2933
2912
2934
2935
2932
2931
Q420-32
2936
2937
2938
2939
16Ø70孔均布
16M56(8.8级)
45°
ø630
ø1102
ø1316

10 - 10
1:20

2Ø38
施工孔
50
390
200
100
125
25
343

50
390
25
343

α角度以放样为准

2932 2933 2937 2938 2939
1:20

2934 ~ 2936
1:20

			山东电力工程咨询院有限公司				浙江特高压交流环网工程线路 工程 施工图 设计阶段
			批 准	雷强	校 核	马一丹	SZK31102A双回路直线塔 90.0-1.5m塔腿结构图(1/3) 93.0-4.5m塔腿结构图(1/3) ㉙
			审 核	高锡鹏			
电 气	赵庆周	2026.08			设计/勘测	潘继光	
专 业	会 签	日 期	比 例		日 期	2026年 08月	图 号 37-SA36901S-T0121-057 版本