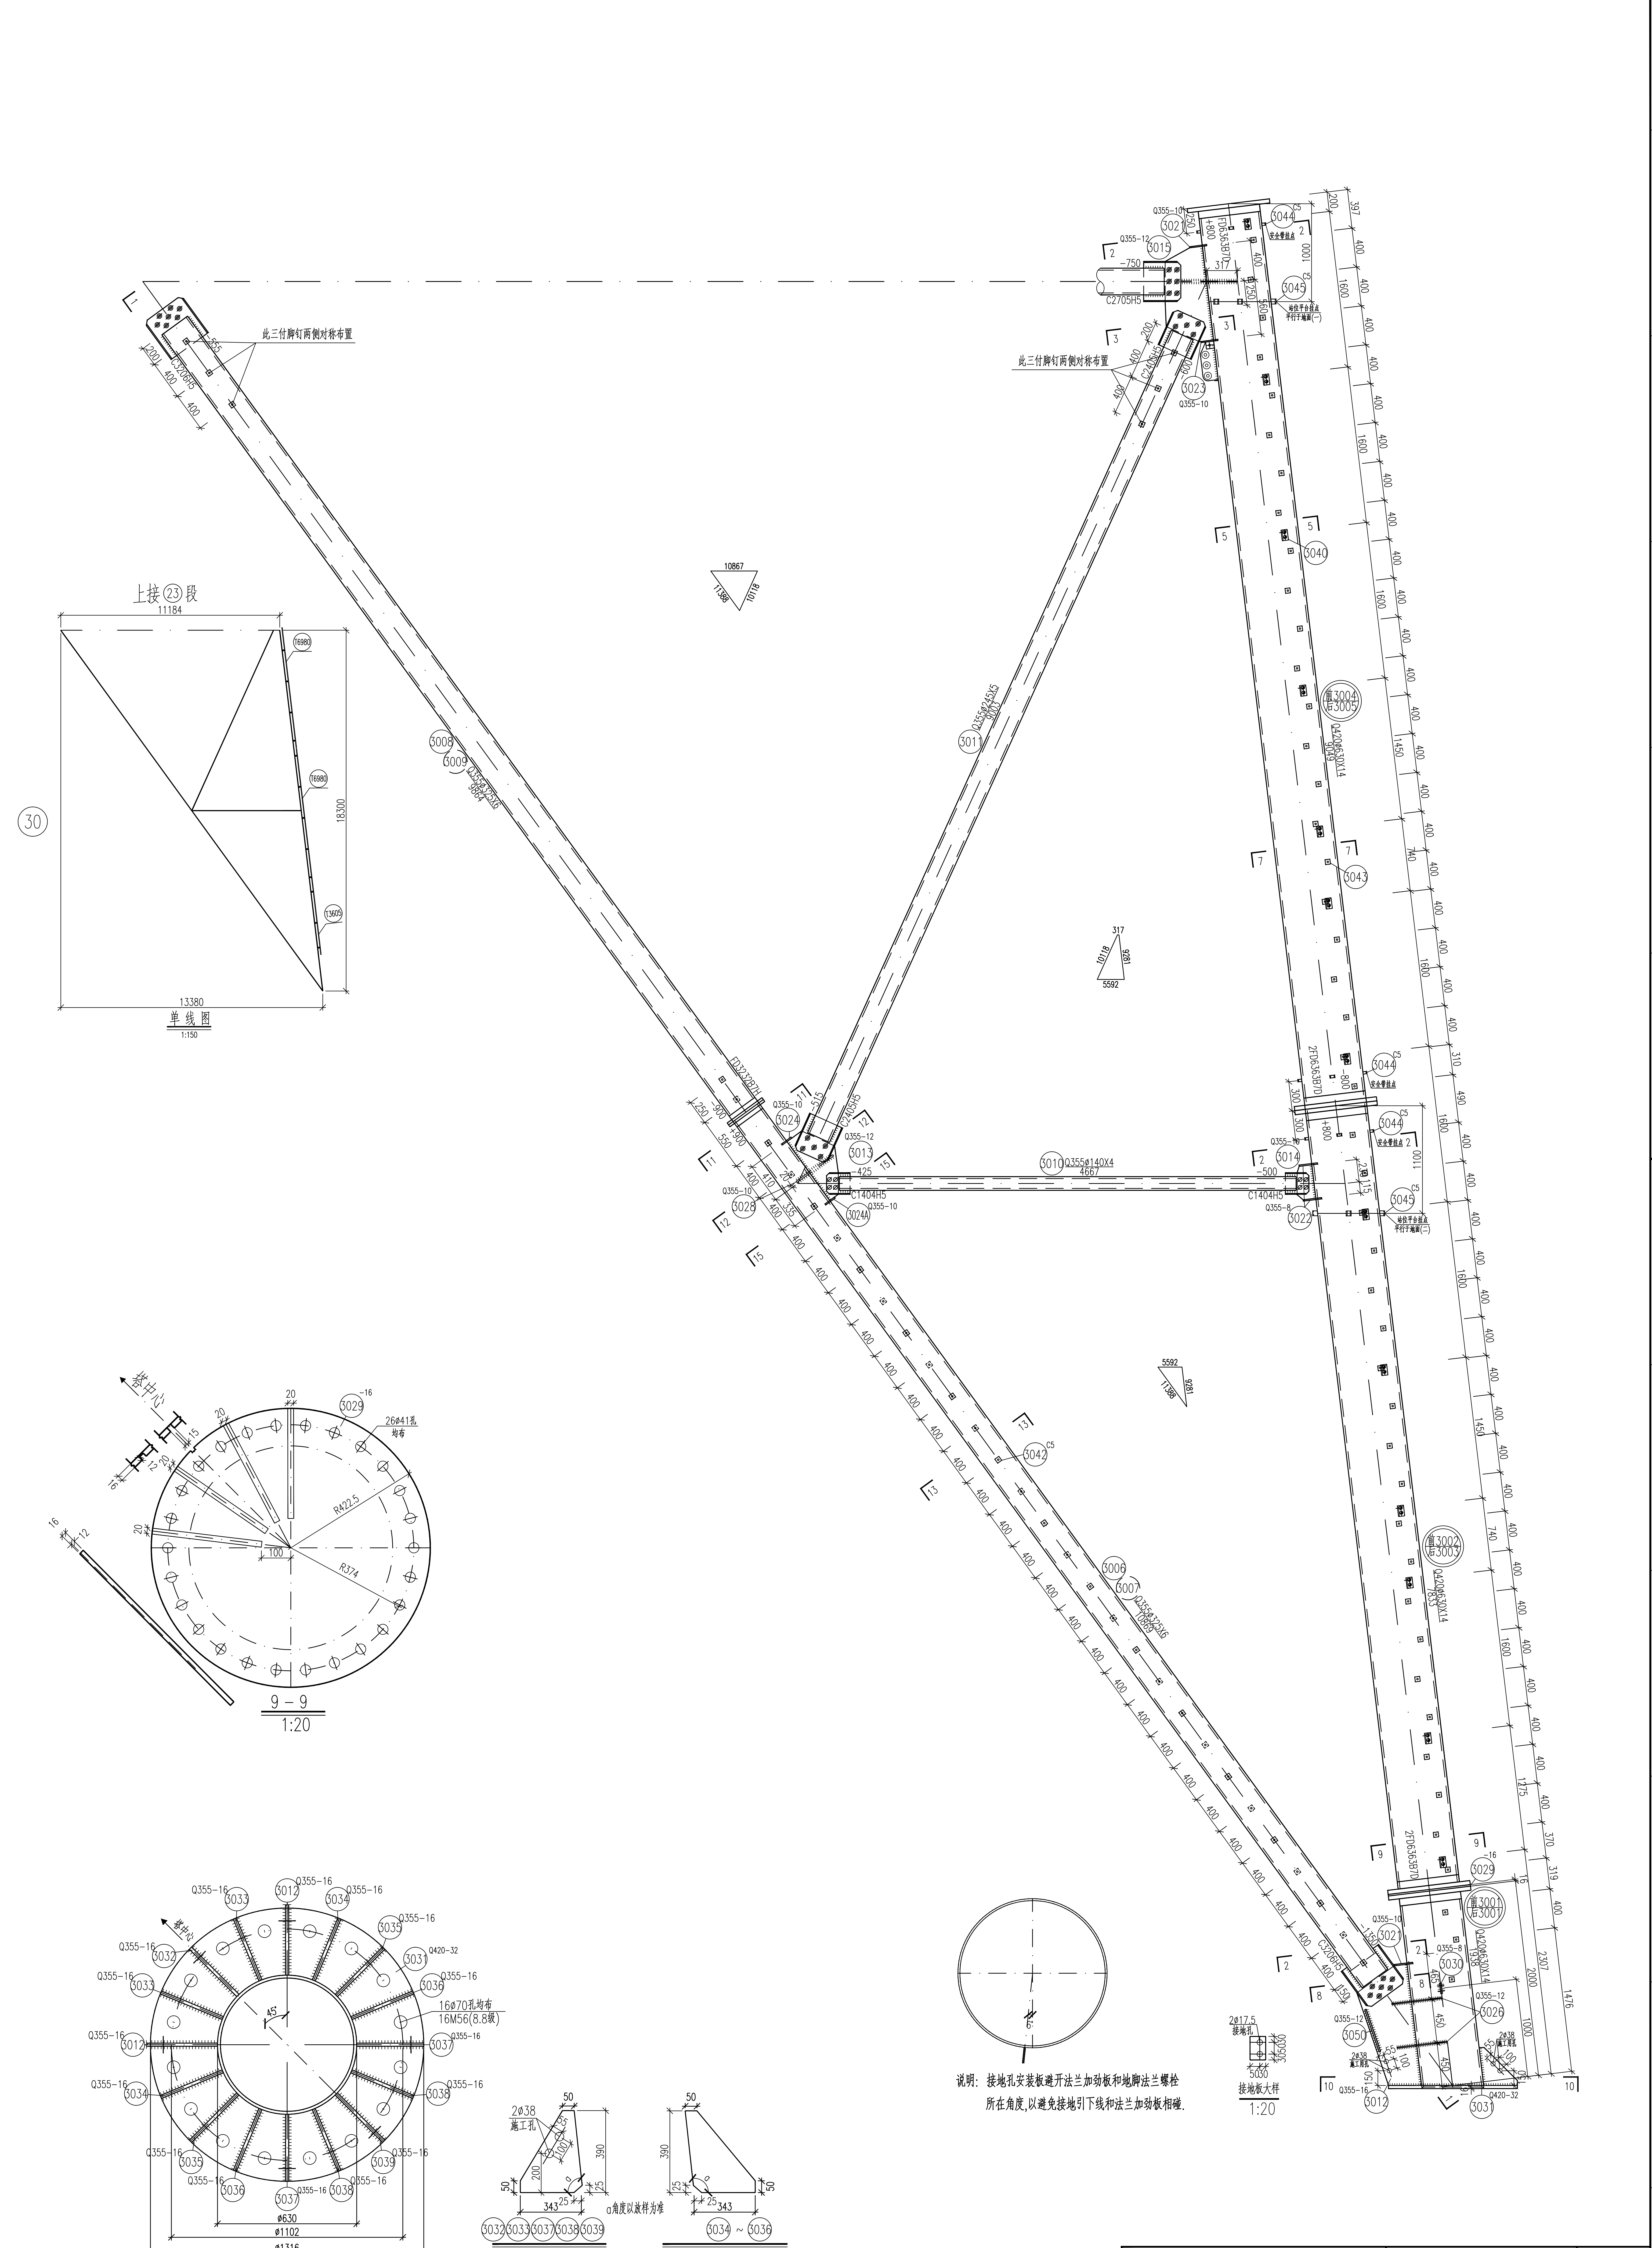

单线图

1:150

9－9

1:20

10－10

1:20

3032 3033 3037 3038 3039

1:20

3034 ～ 3036

1:20

说明：接地孔安装板避开法兰加劲板和地脚法兰螺栓所在角度，以避免接地引下线和法兰加劲板相碰.

接地板大样

1:20

			山东电力工程咨询院有限公司			浙江特高压交流环网工程线路 工程	施工图	设计阶段
			批 准	雷强	校 核	马一丹	SZK31102A双回路直线塔 90.0−0.0m塔腿结构图(1/3) 93.0−3.0m塔腿结构图(1/3)	㉚
电 气	赵庆周	2026.08	审 核	高锡鹏	设计/勘测	潘胜克		
专 业	会 签	日 期	比 例		日 期	2026年 08月	图 号 37−SA36901S−T0121−060	版本