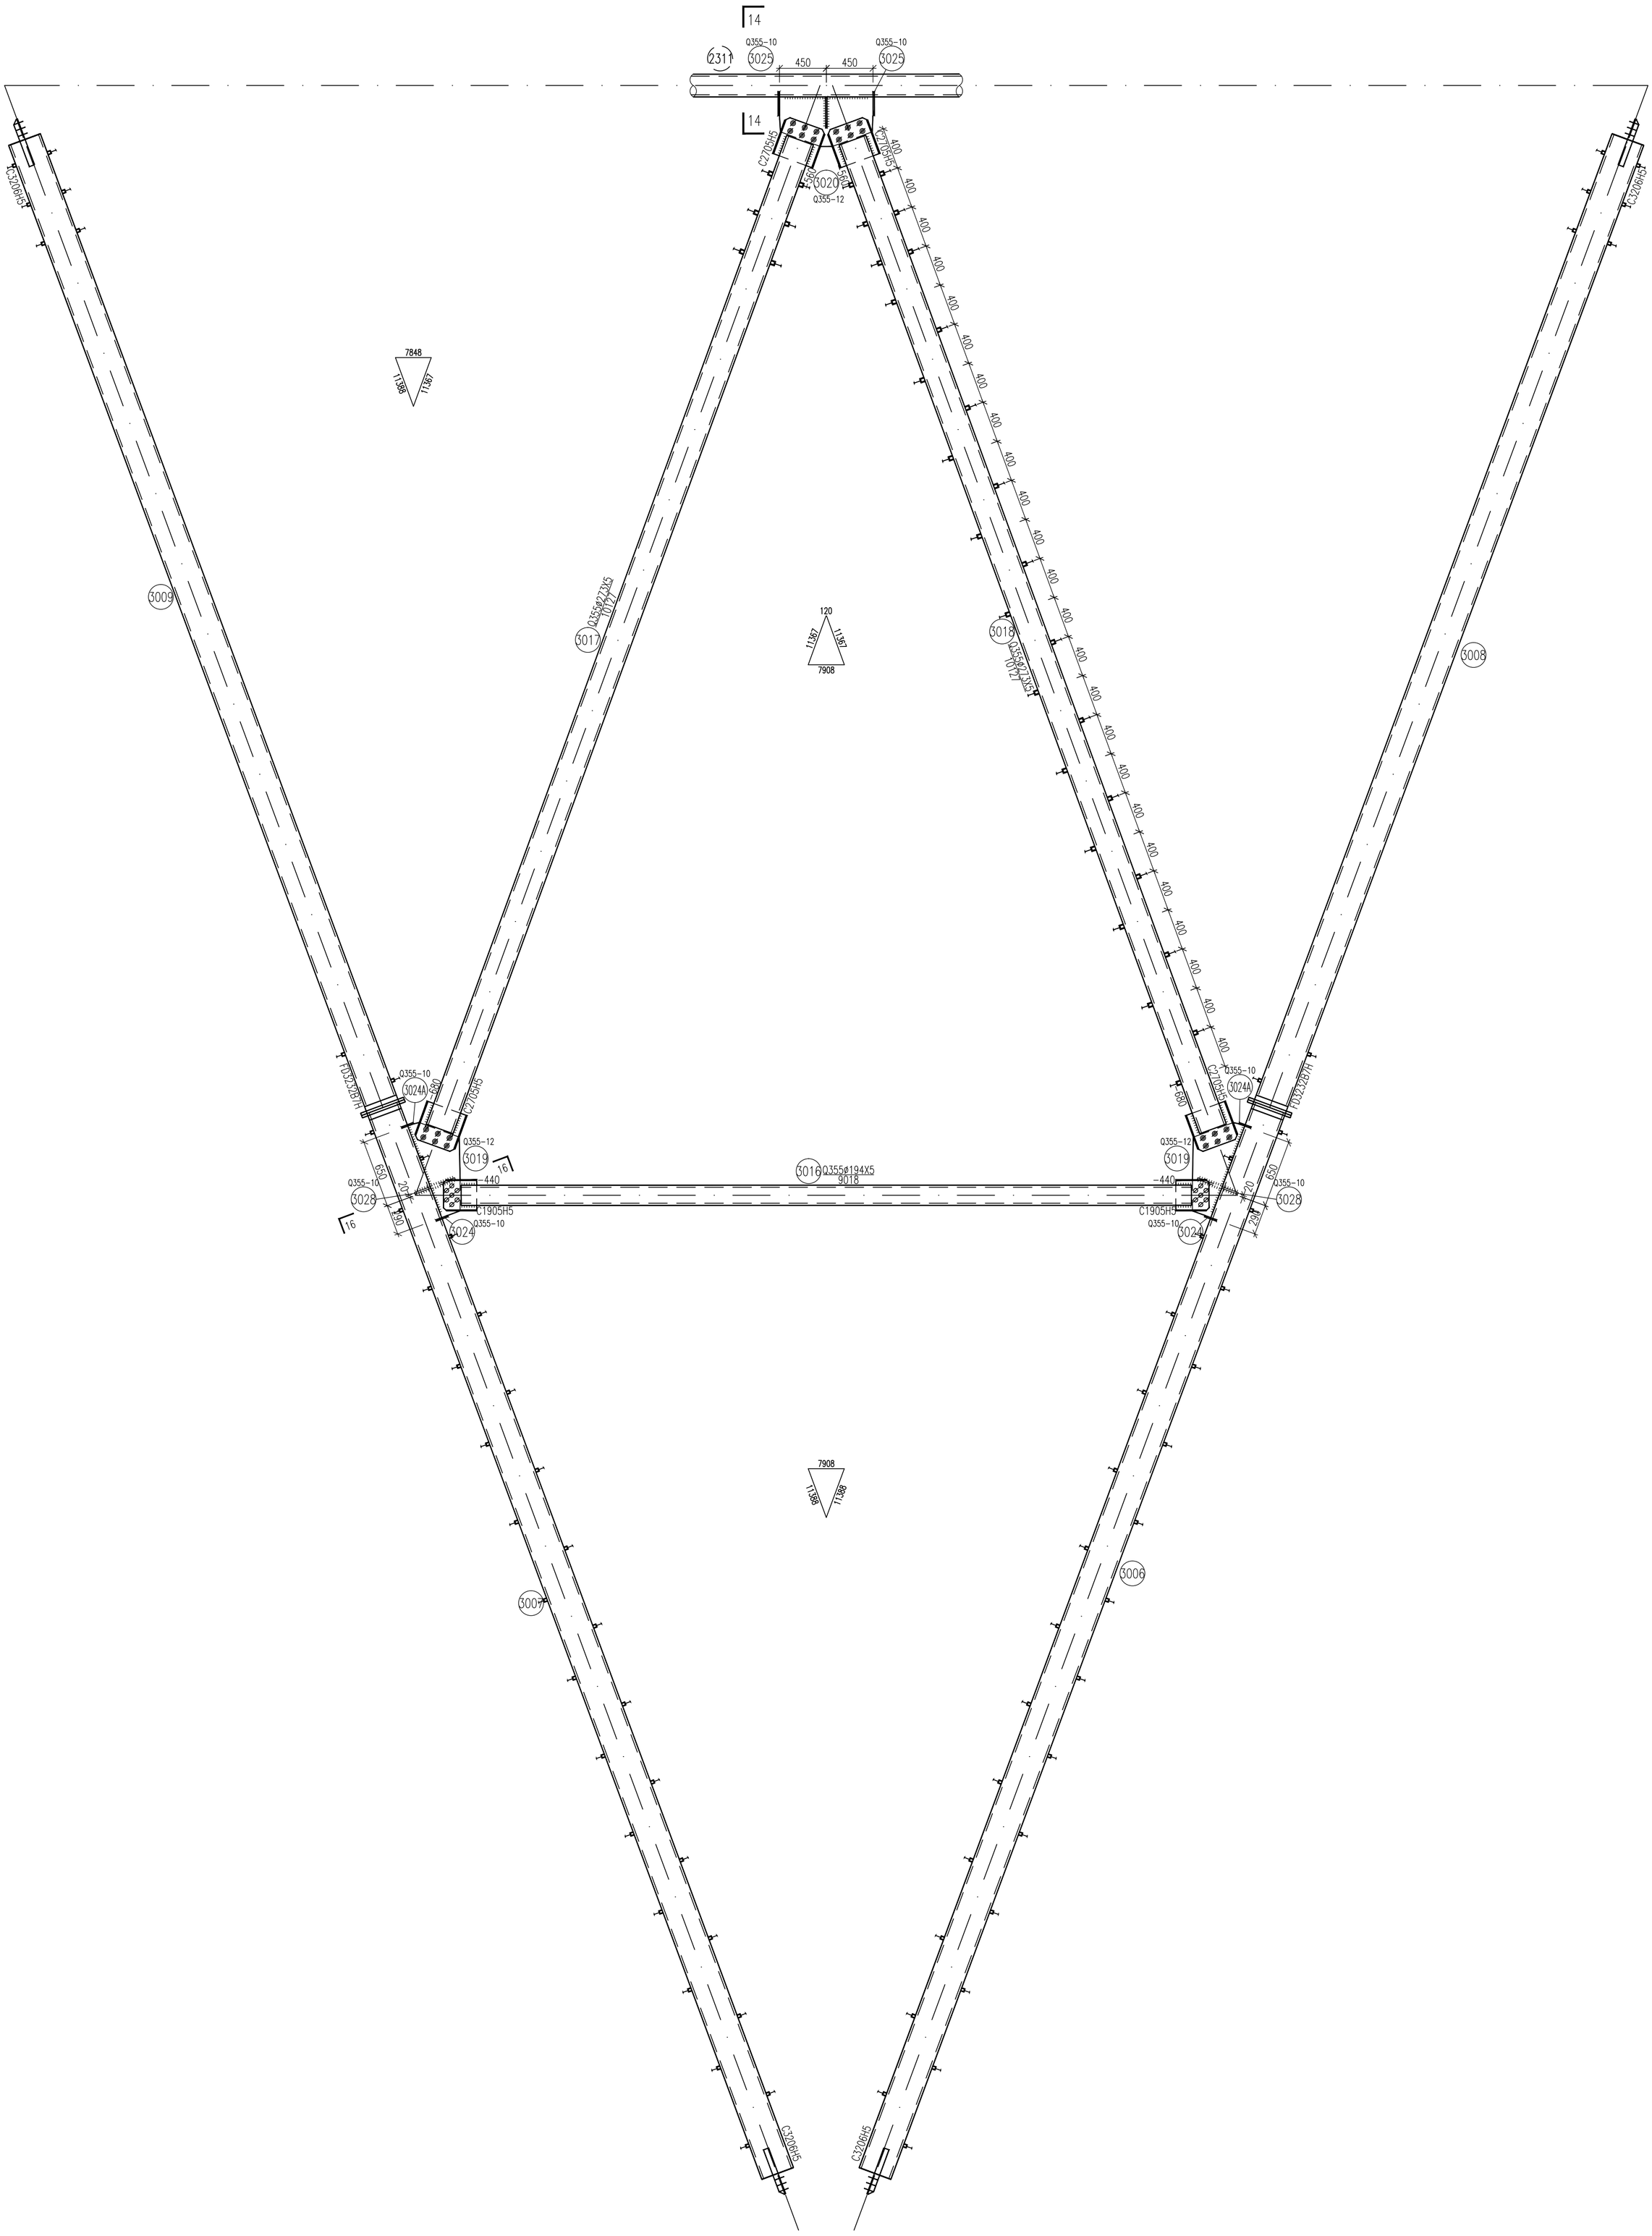


山东电力工程咨询院有限公司			浙江特高压交流环网工程线路 工程	施工图 设计阶段
批 准	雷强	校 核	习一丹	SZK31102A双回路直线塔 90.0-0.0m塔腿结构图(2/3) 93.0-3.0m塔腿结构图(2/3) 30
审 核	高鹏鹏	设计/勘测	潘胜龙	
比 例		日 期	2026年 08月	图 号 37-SA36901S-T0121-061 版本