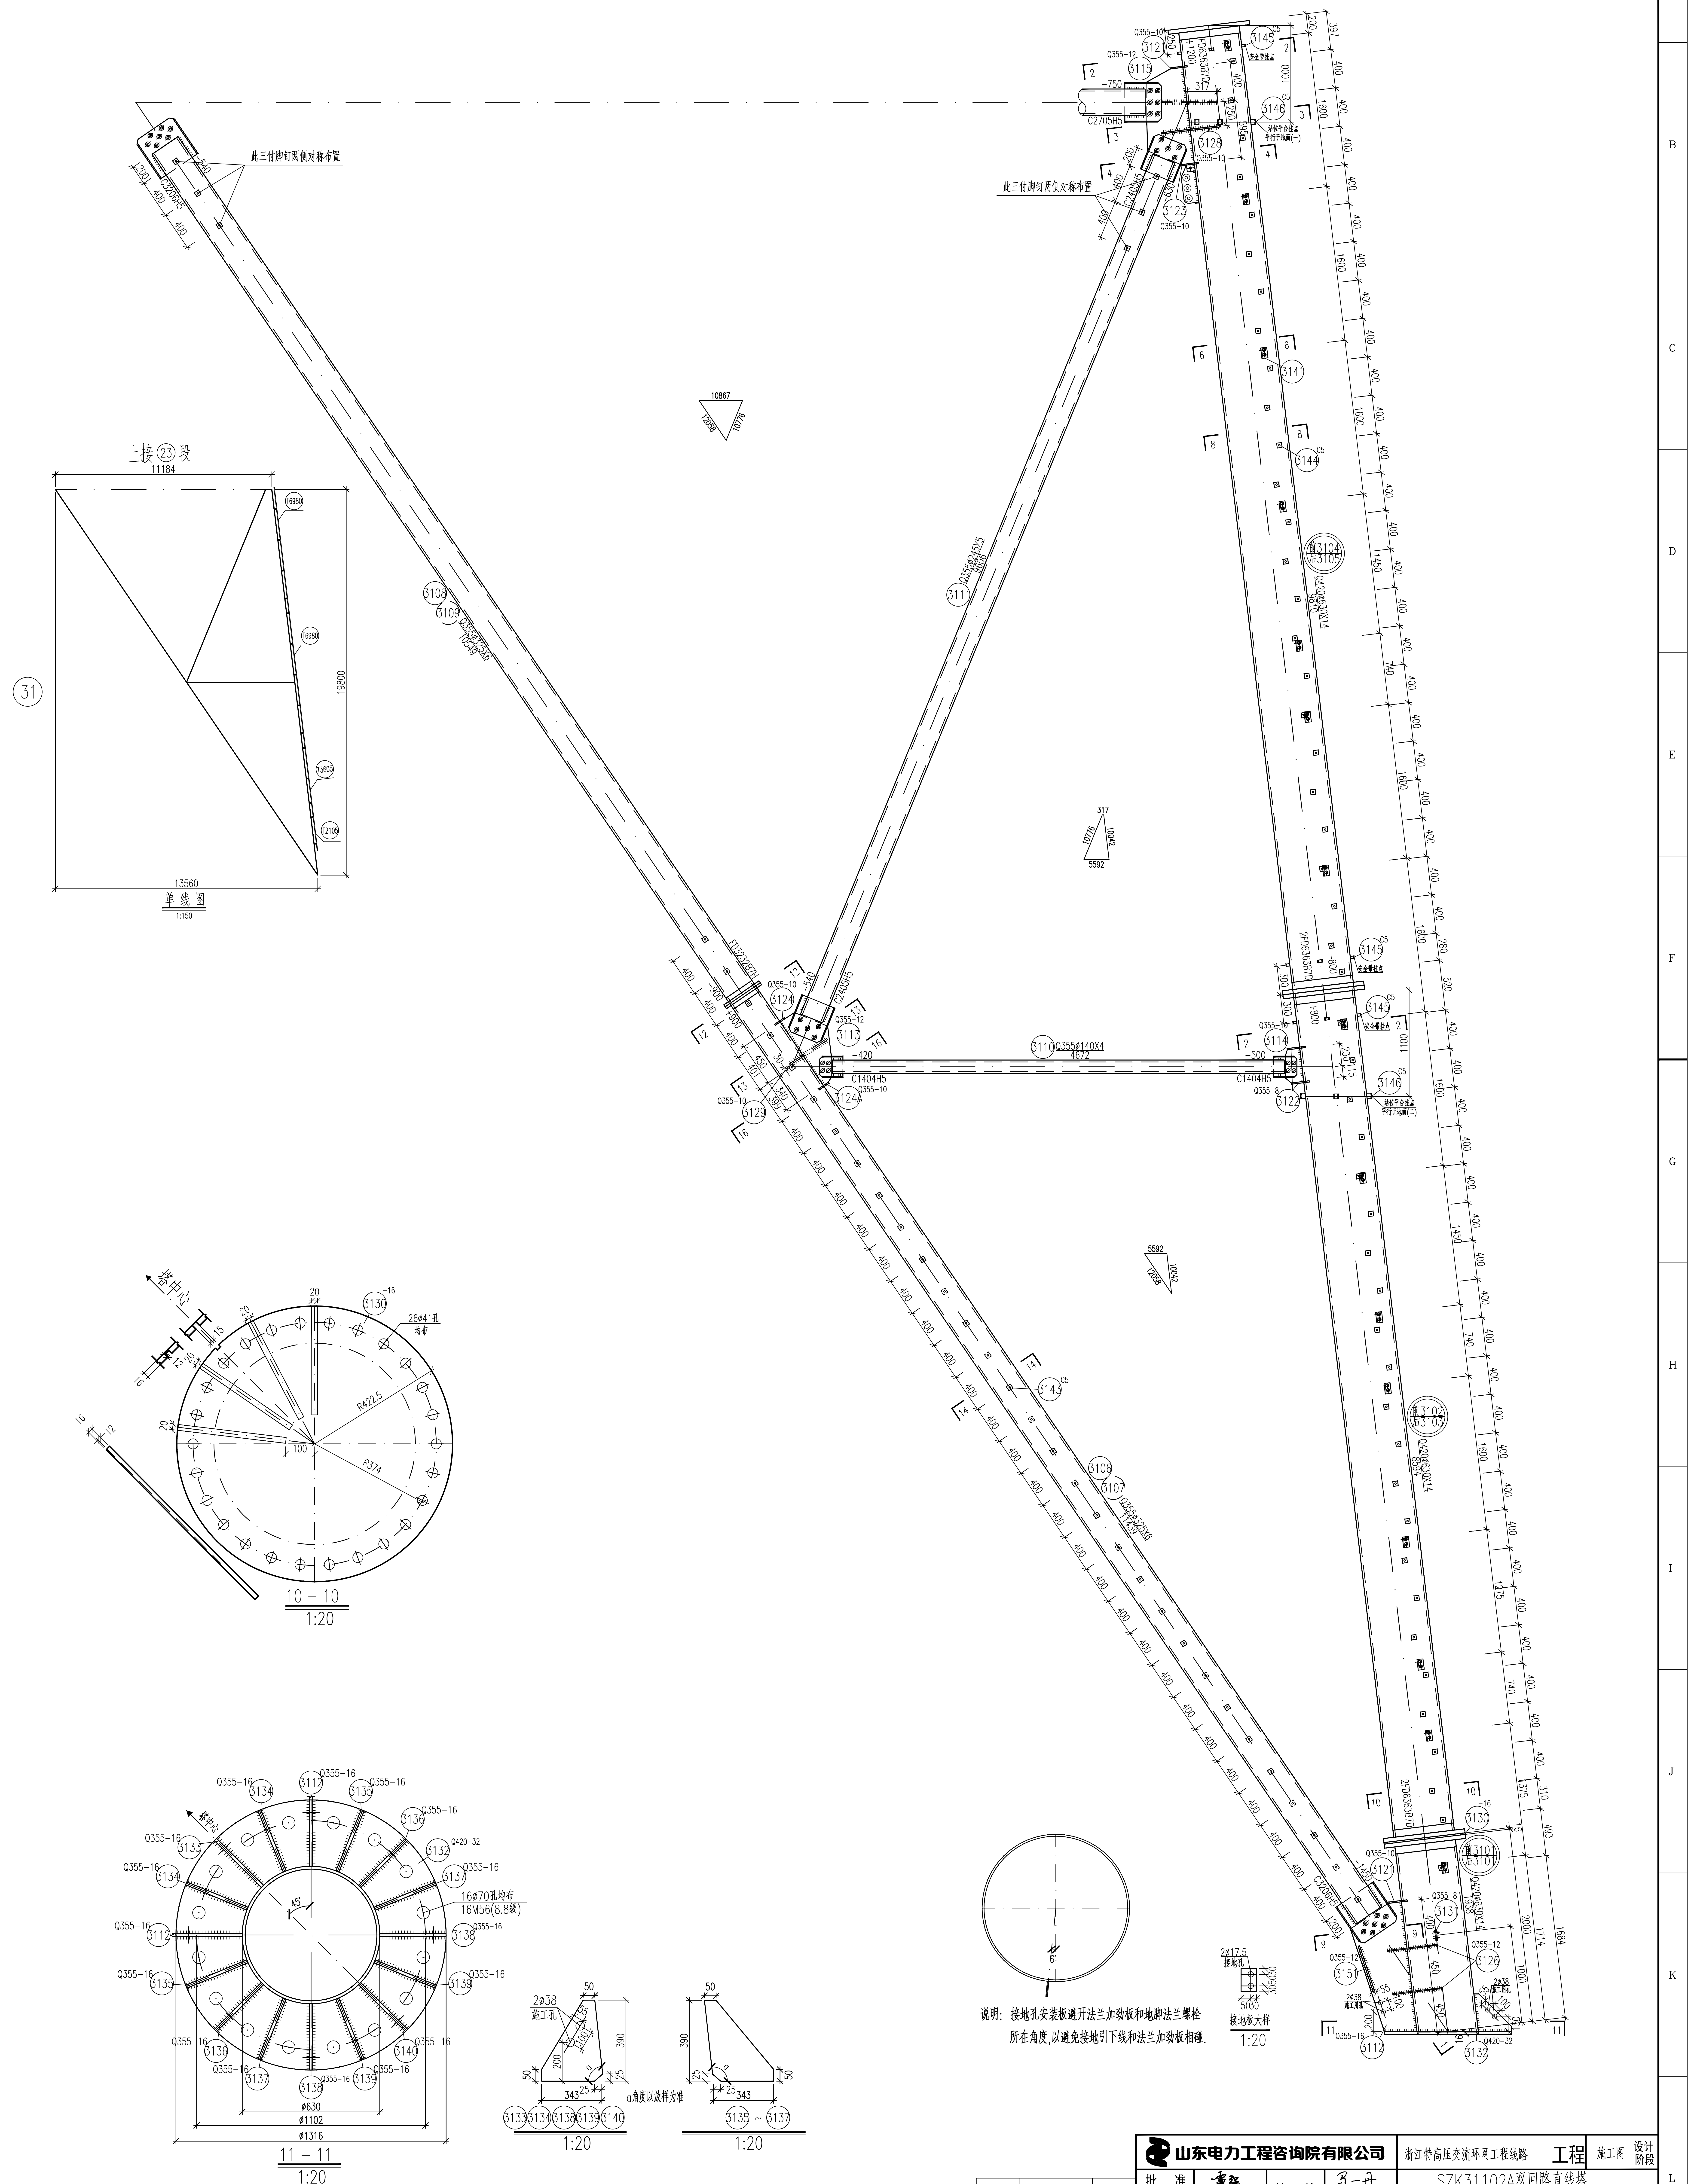

说明：接地孔安装板避开法兰加劲板和地脚法兰螺栓所在角度，以避免接地引下线和法兰加劲板相碰。

山东电力工程咨询院有限公司

浙江特高压交流环网工程线路 工程 | 施工图 | 设计阶段

批 准	雷强	校 核	马一丹
审 核	高锡鹏	设计/勘测	潘胜先
比 例		日 期	2026年 08月

电气	赵庆周	2026.08
专业	会签	日期

SZK31102A双回路直线塔
93.0-1.5m塔腿结构图(1/3)
96.0-4.5m塔腿结构图(1/3)
㉛

图 号 37-SA36901S-T0121-063 版本