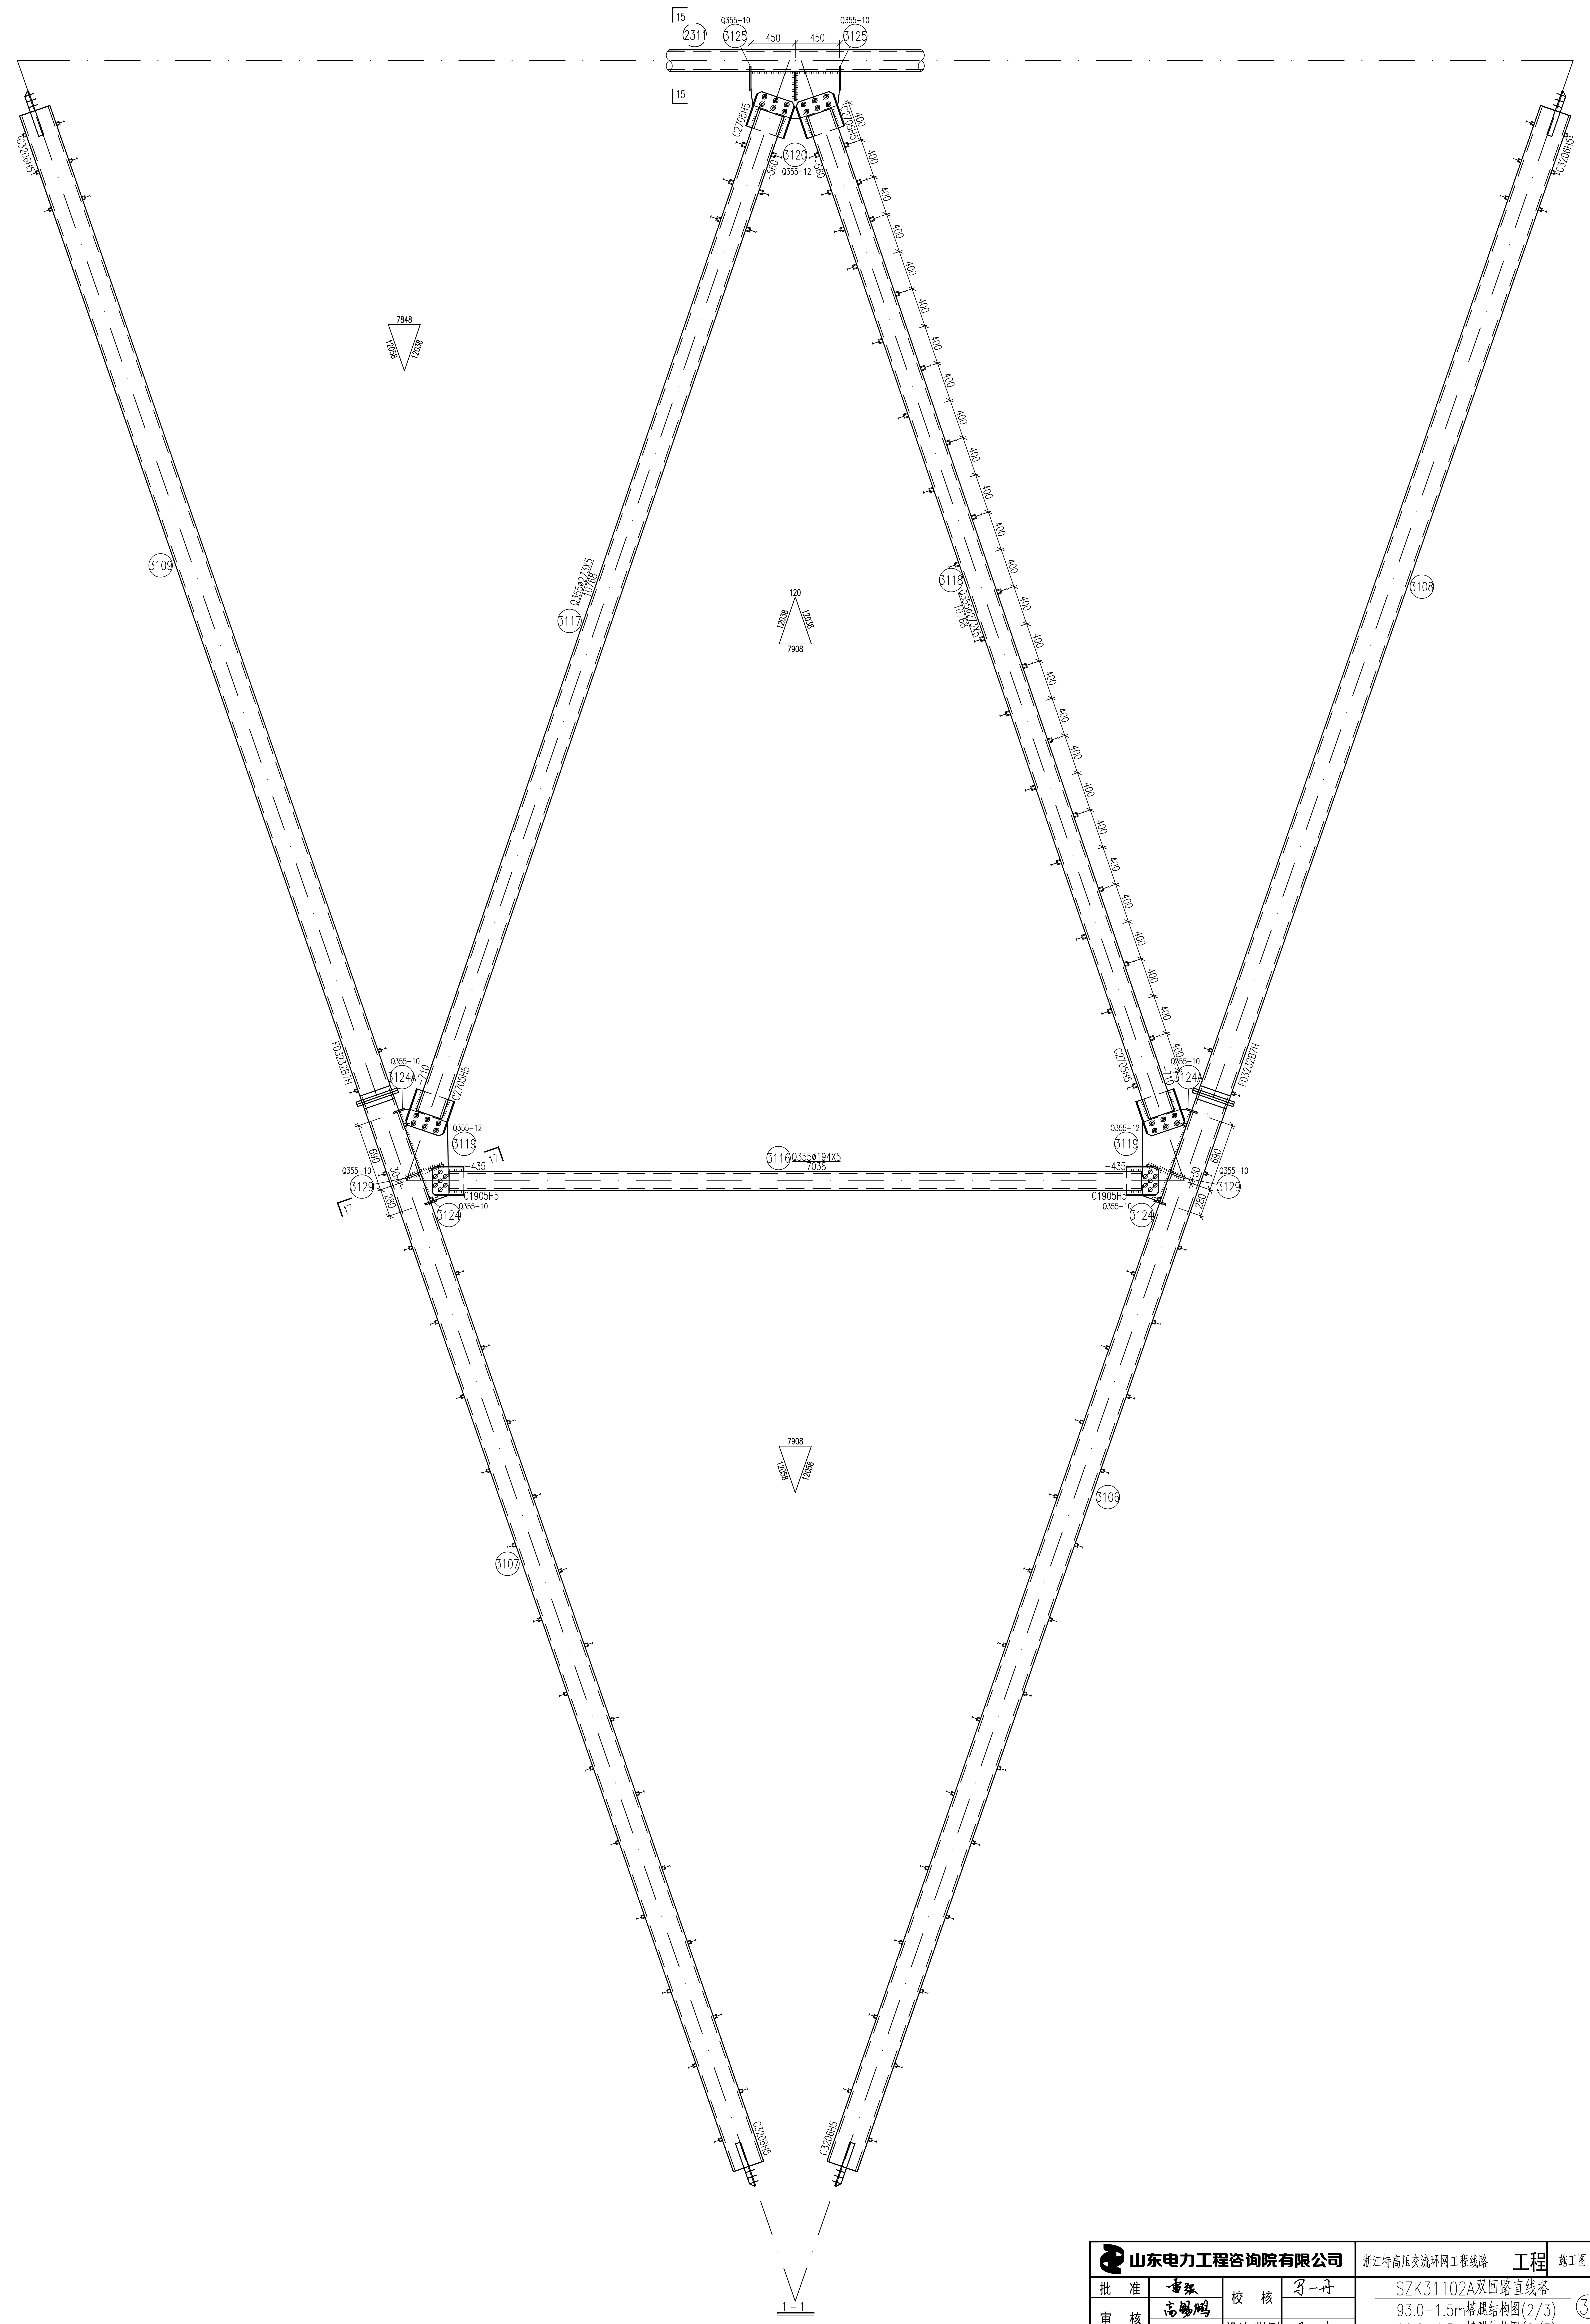
15
2311
Q355-10
3125
450
450
Q355-10
3125
15
C2705H5
C2705H5
3120
Q355-12
560
560
400
C3206H5
C3206H5
7848
12058
12038
3109
3117
Q355Ø273X5
10768
120
12038
12038
7908
3118
Q355Ø273X5
10768
3108
FD3232B7H
Q355-10
3124A
710
C2705H5
Q355-12
3119
17
3116
Q355Ø194X5
7038
435
Q355-10
3129
690
30
280
C1905H5
Q355-10
3124
17
FD3232B7H
Q355-10
3124A
710
C2705H5
Q355-12
3119
435
690
30
Q355-10
3129
280
C1905H5
Q355-10
3124
7908
12058
12058
3107
3106
C3206H5
C3206H5
1-1

山东电力工程咨询院有限公司				浙江特高压交流环网工程线路 工程	施工图 设计阶段
批 准	雷强	校 核	马一丹	SZK31102A双回路直线塔 93.0-1.5m塔腿结构图(2/3) 96.0-4.5m塔腿结构图(2/3)	㉛
审 核	高锡鹏				
		设计/勘测	潘旺光		
比 例		日 期	2026年 08月	图 号 37-SA36901S-T0121-064	版本