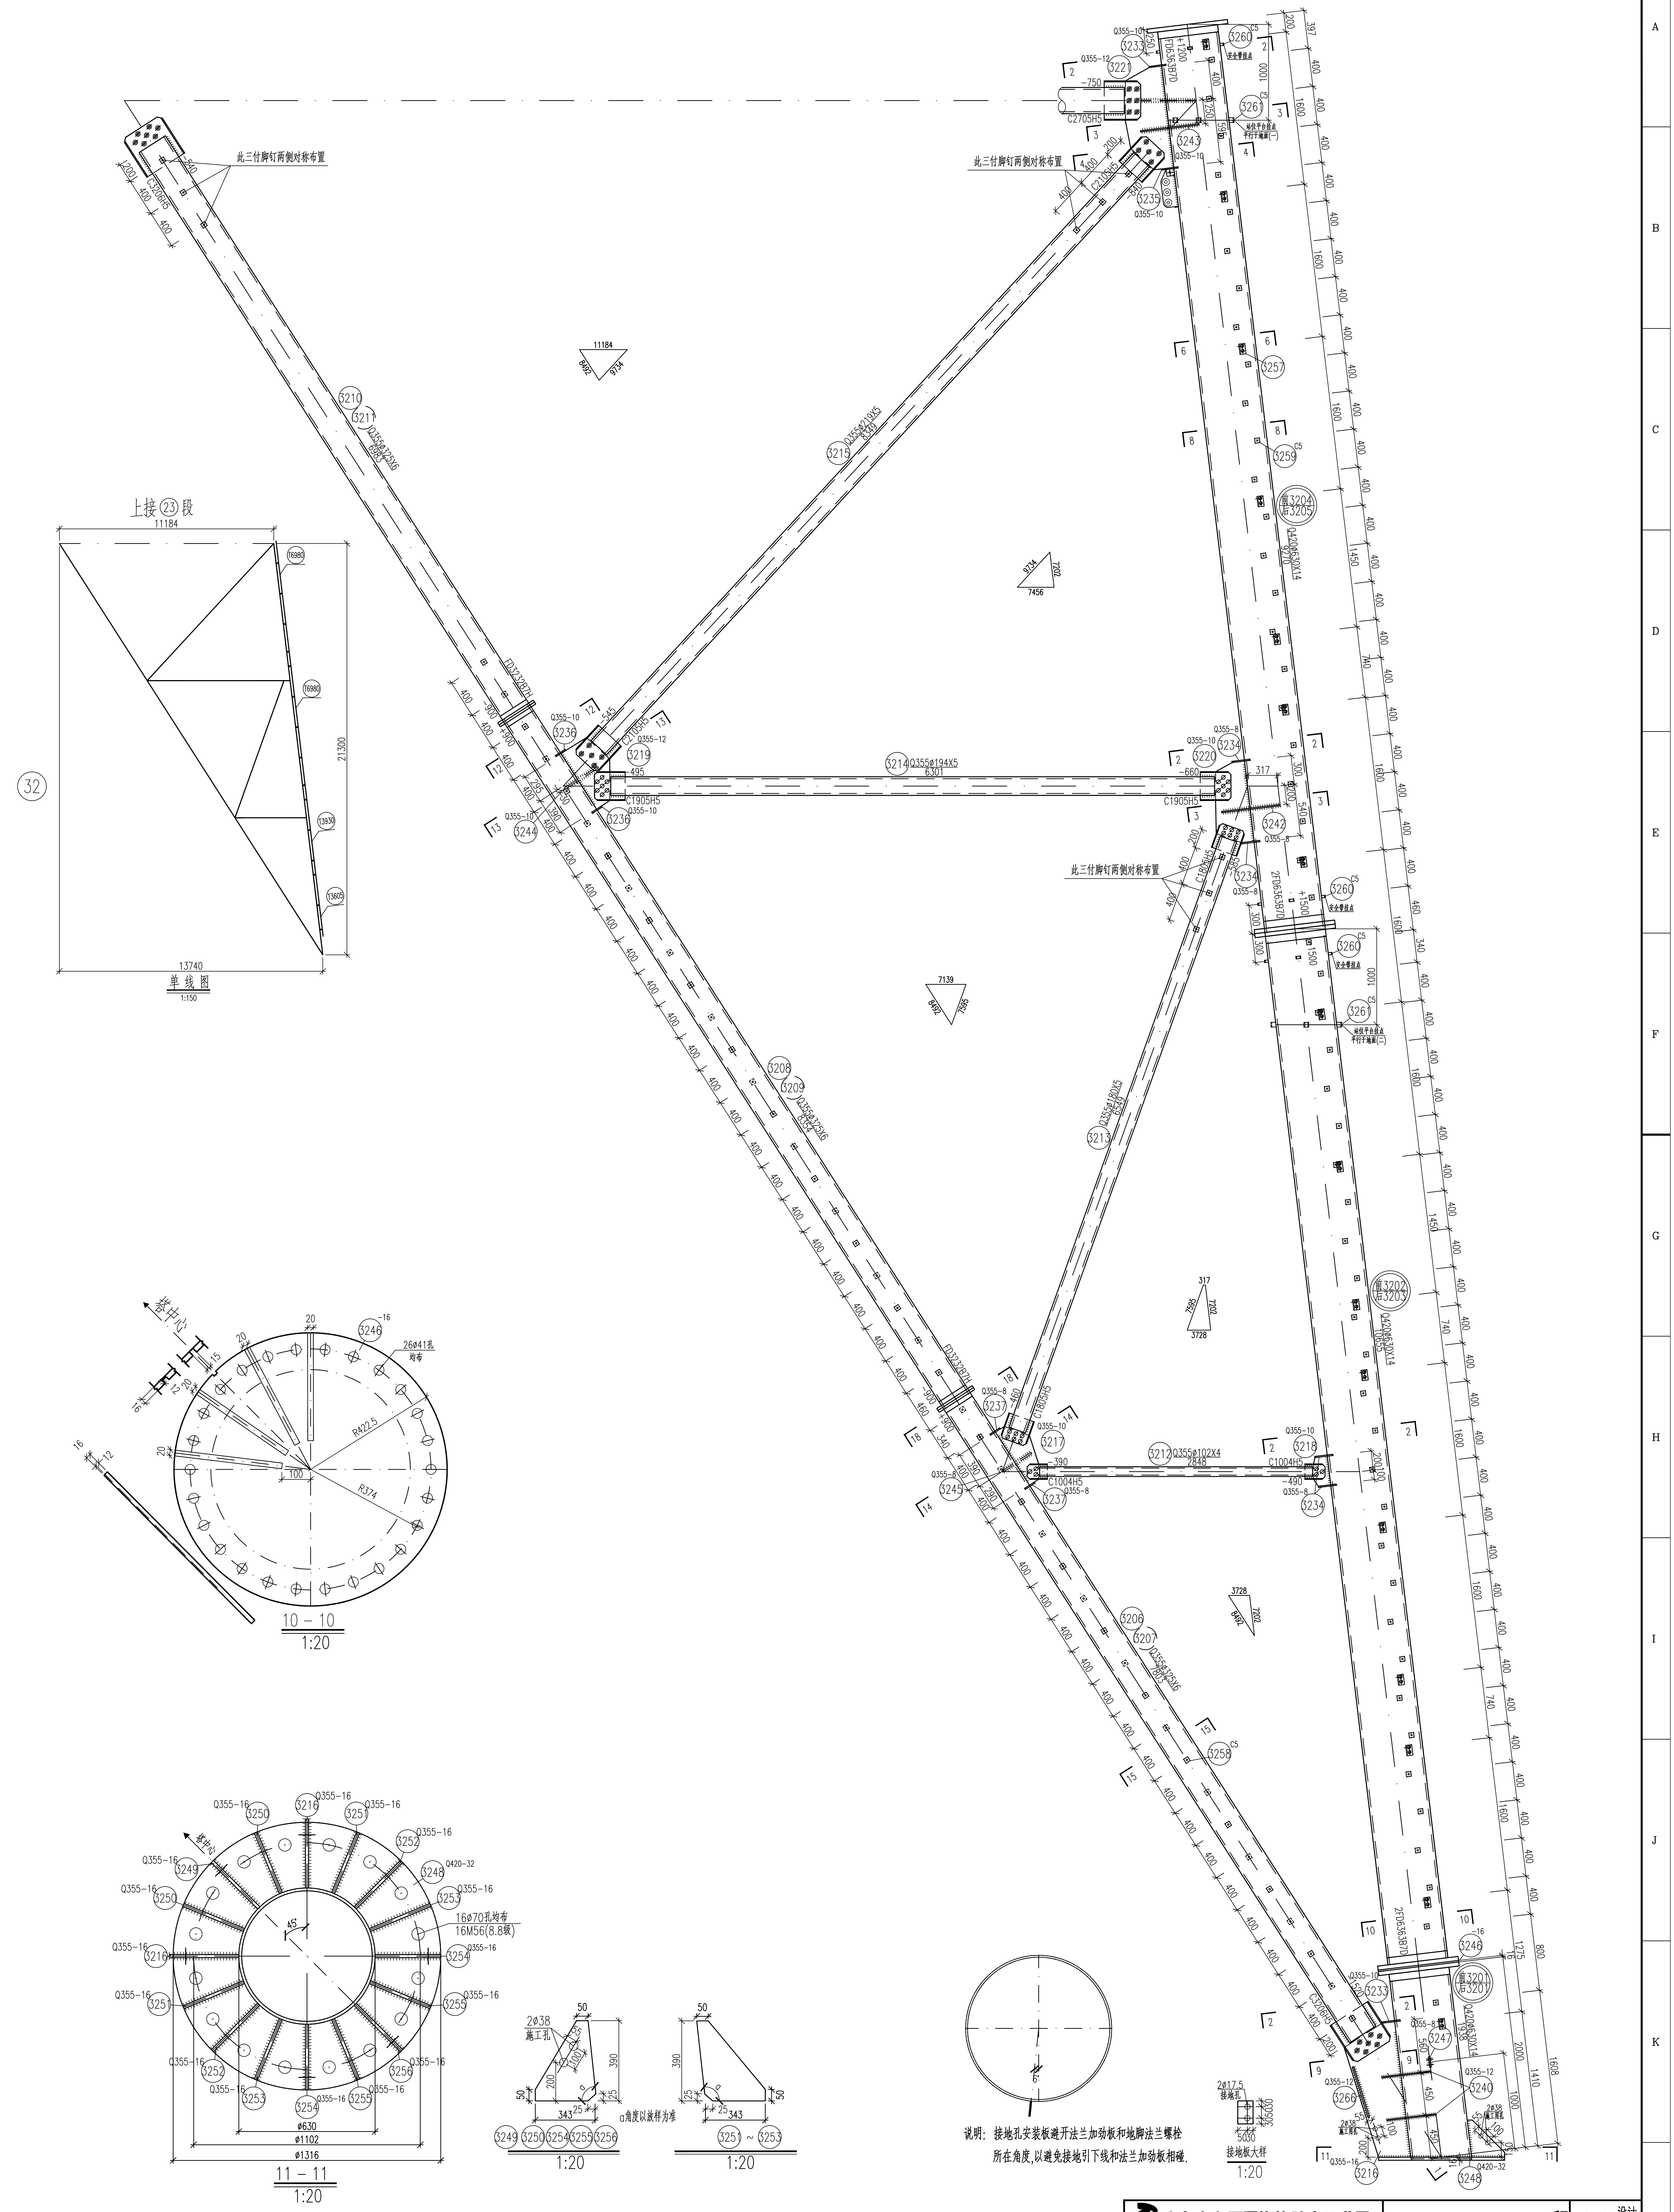

上接㉓段

单线图 1:150

10－10 1:20

11－11 1:20

3249 3250 3254 3255 3256 1:20

3251 ~ 3253 1:20

接地板大样 1:20

说明：接地孔安装板避开法兰加劲板和地脚法兰螺栓所在角度,以避免接地引下线和法兰加劲板相碰.

			山东电力工程咨询院有限公司				浙江特高压交流环网工程线路 工程	施工图	设计阶段
			批准	雷强	校核	马一丹	SZK31102A双回路直线塔 93.0-0.0m塔腿结构图(1/3) 96.0-3.0m塔腿结构图(1/3)	㉜	
			审核	高锡鹏					
电气	赵庆周	2026.08			设计/勘测	潘桂先			
专业	会签	日期	比例		日期	2026年 08月	图号	37-SA36901S-T0121-066	版本