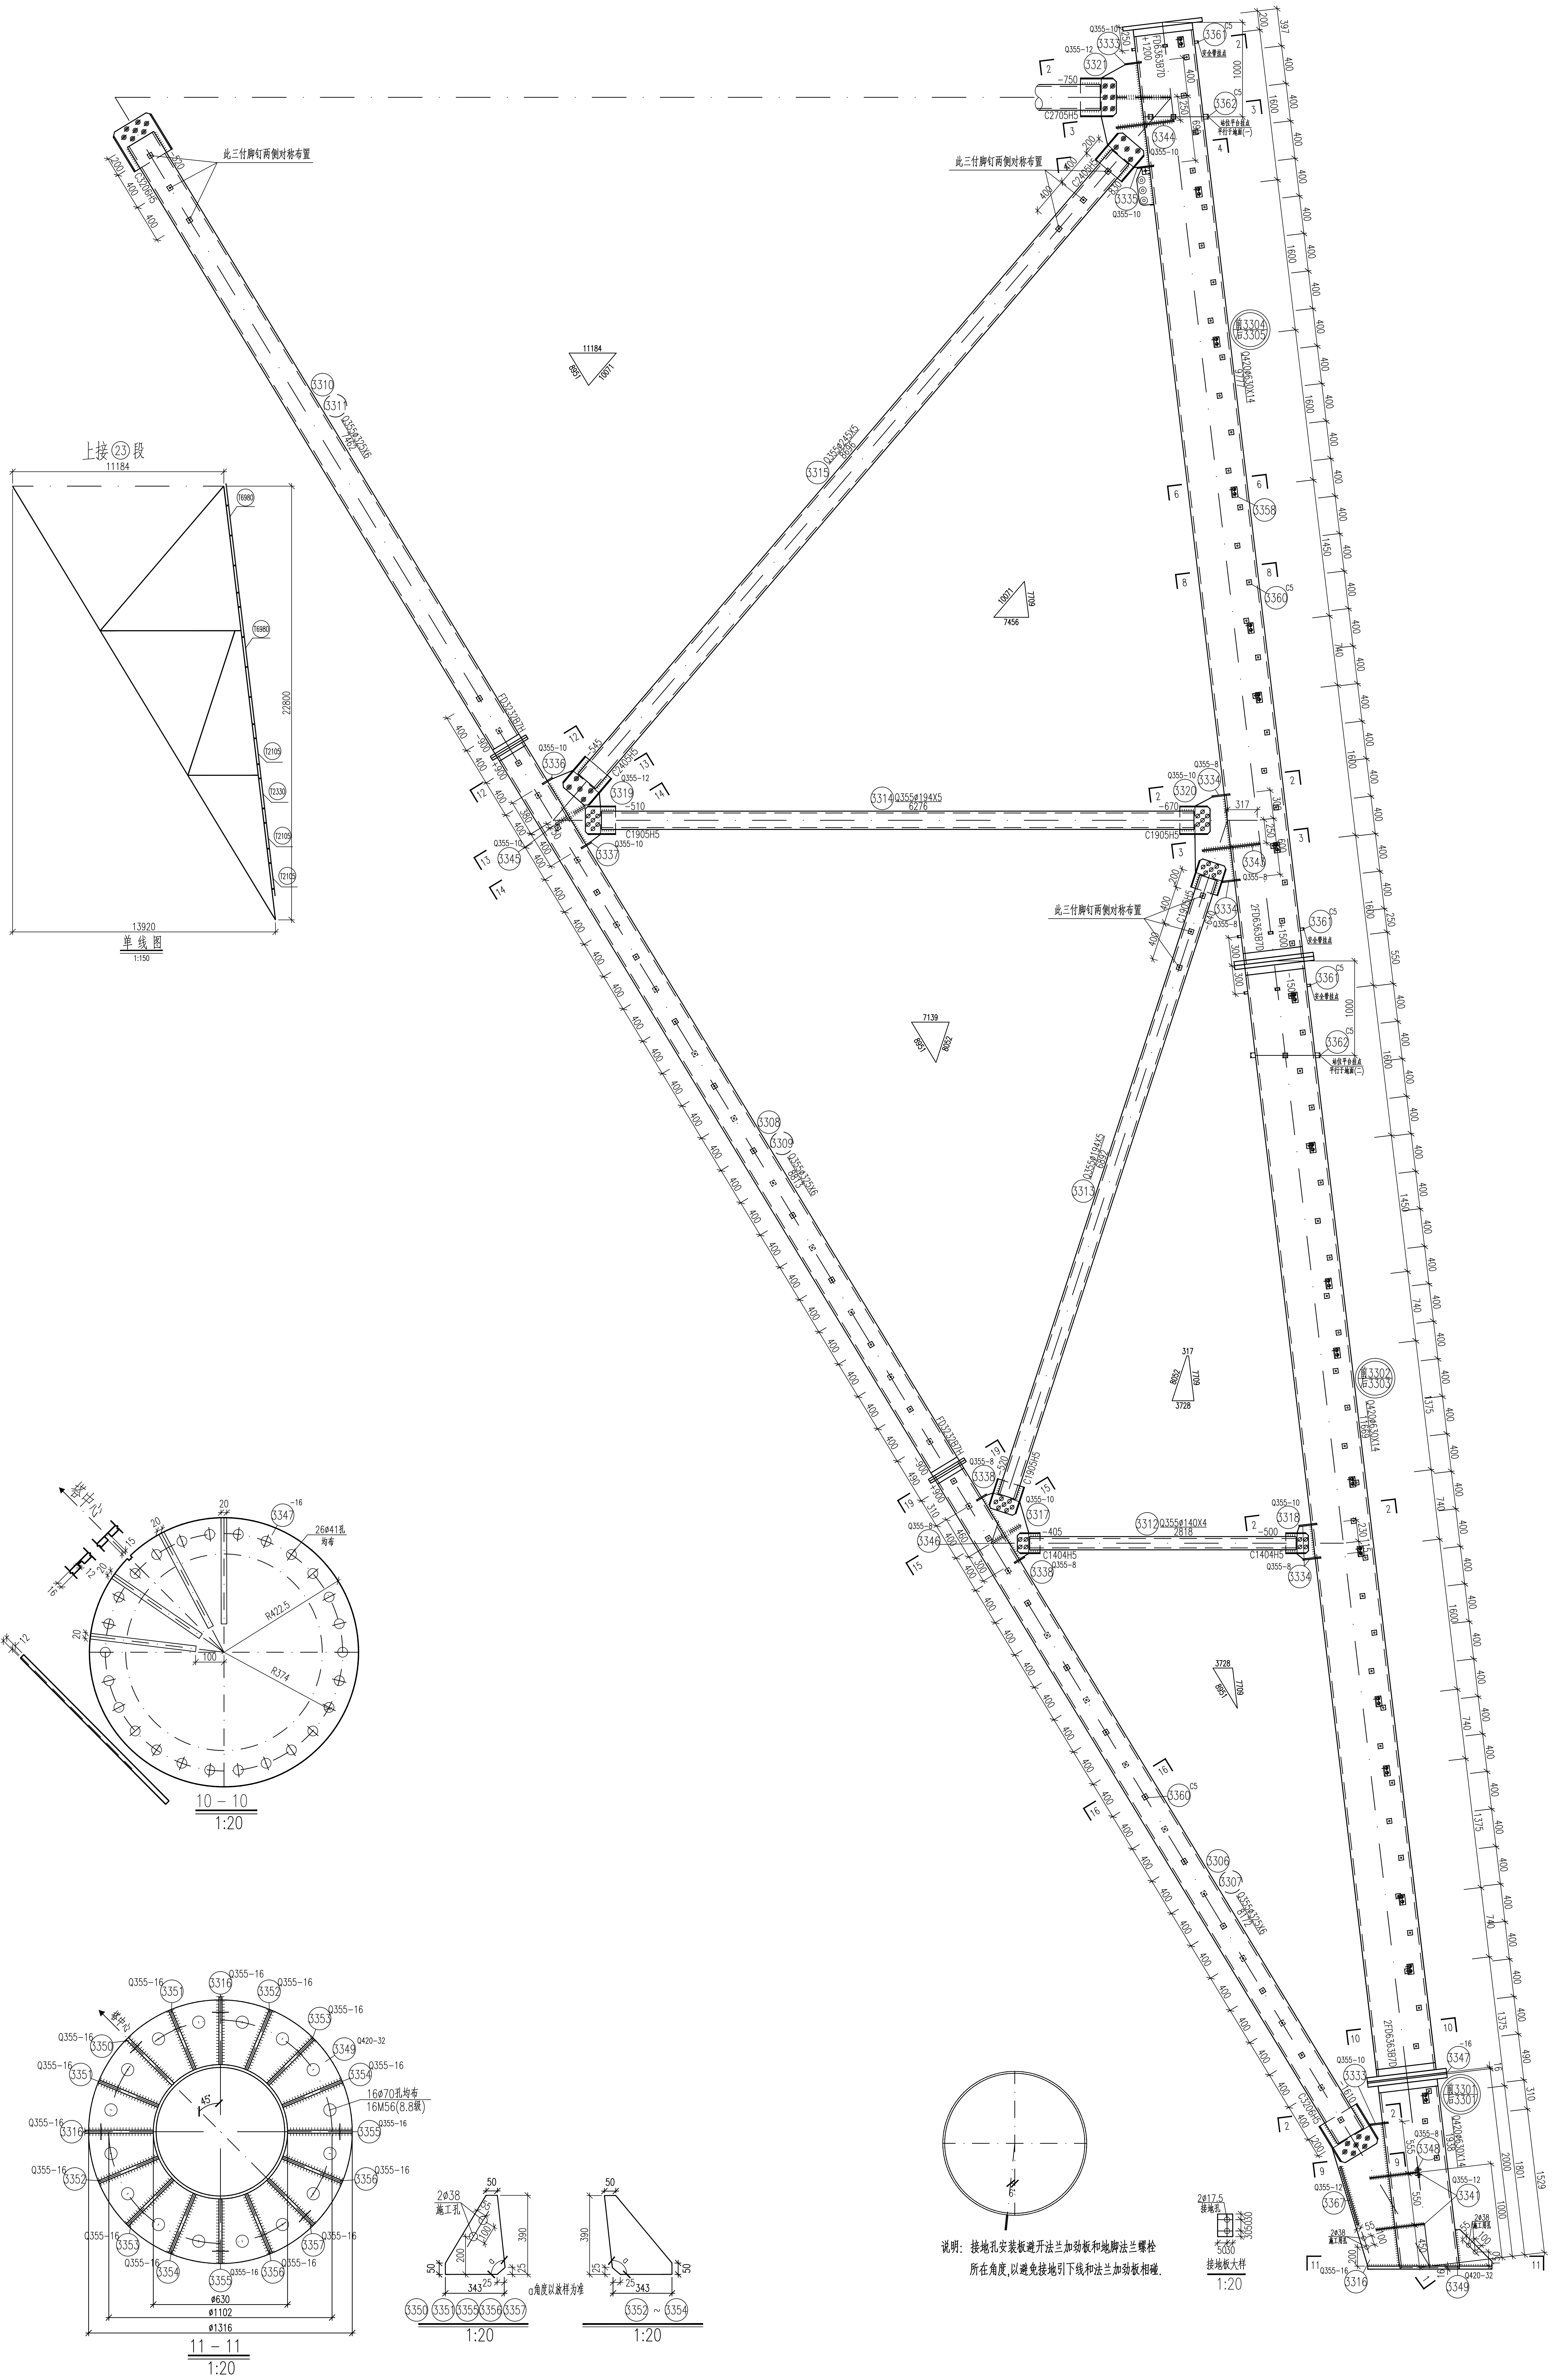

说明：接地孔安装板避开法兰加劲板和地脚法兰螺栓
所在角度,以避免接地引下线和法兰加劲板相碰.

电气	赵庆周	2026.08
专业	会签	日期

山东电力工程咨询院有限公司

浙江特高压交流环网工程线路 工程 | 施工图 | 设计阶段

批　准	雷强	校　核	马一丹
审　核	高锡鹏		
		设计/勘测	潘旭光
比　例		日　期	2026年 08月

SZK31102A双回路直线塔
96.0-1.5m塔腿结构图(1/3) ㉝

图　号 37-SA36901S-T0121-069 版本