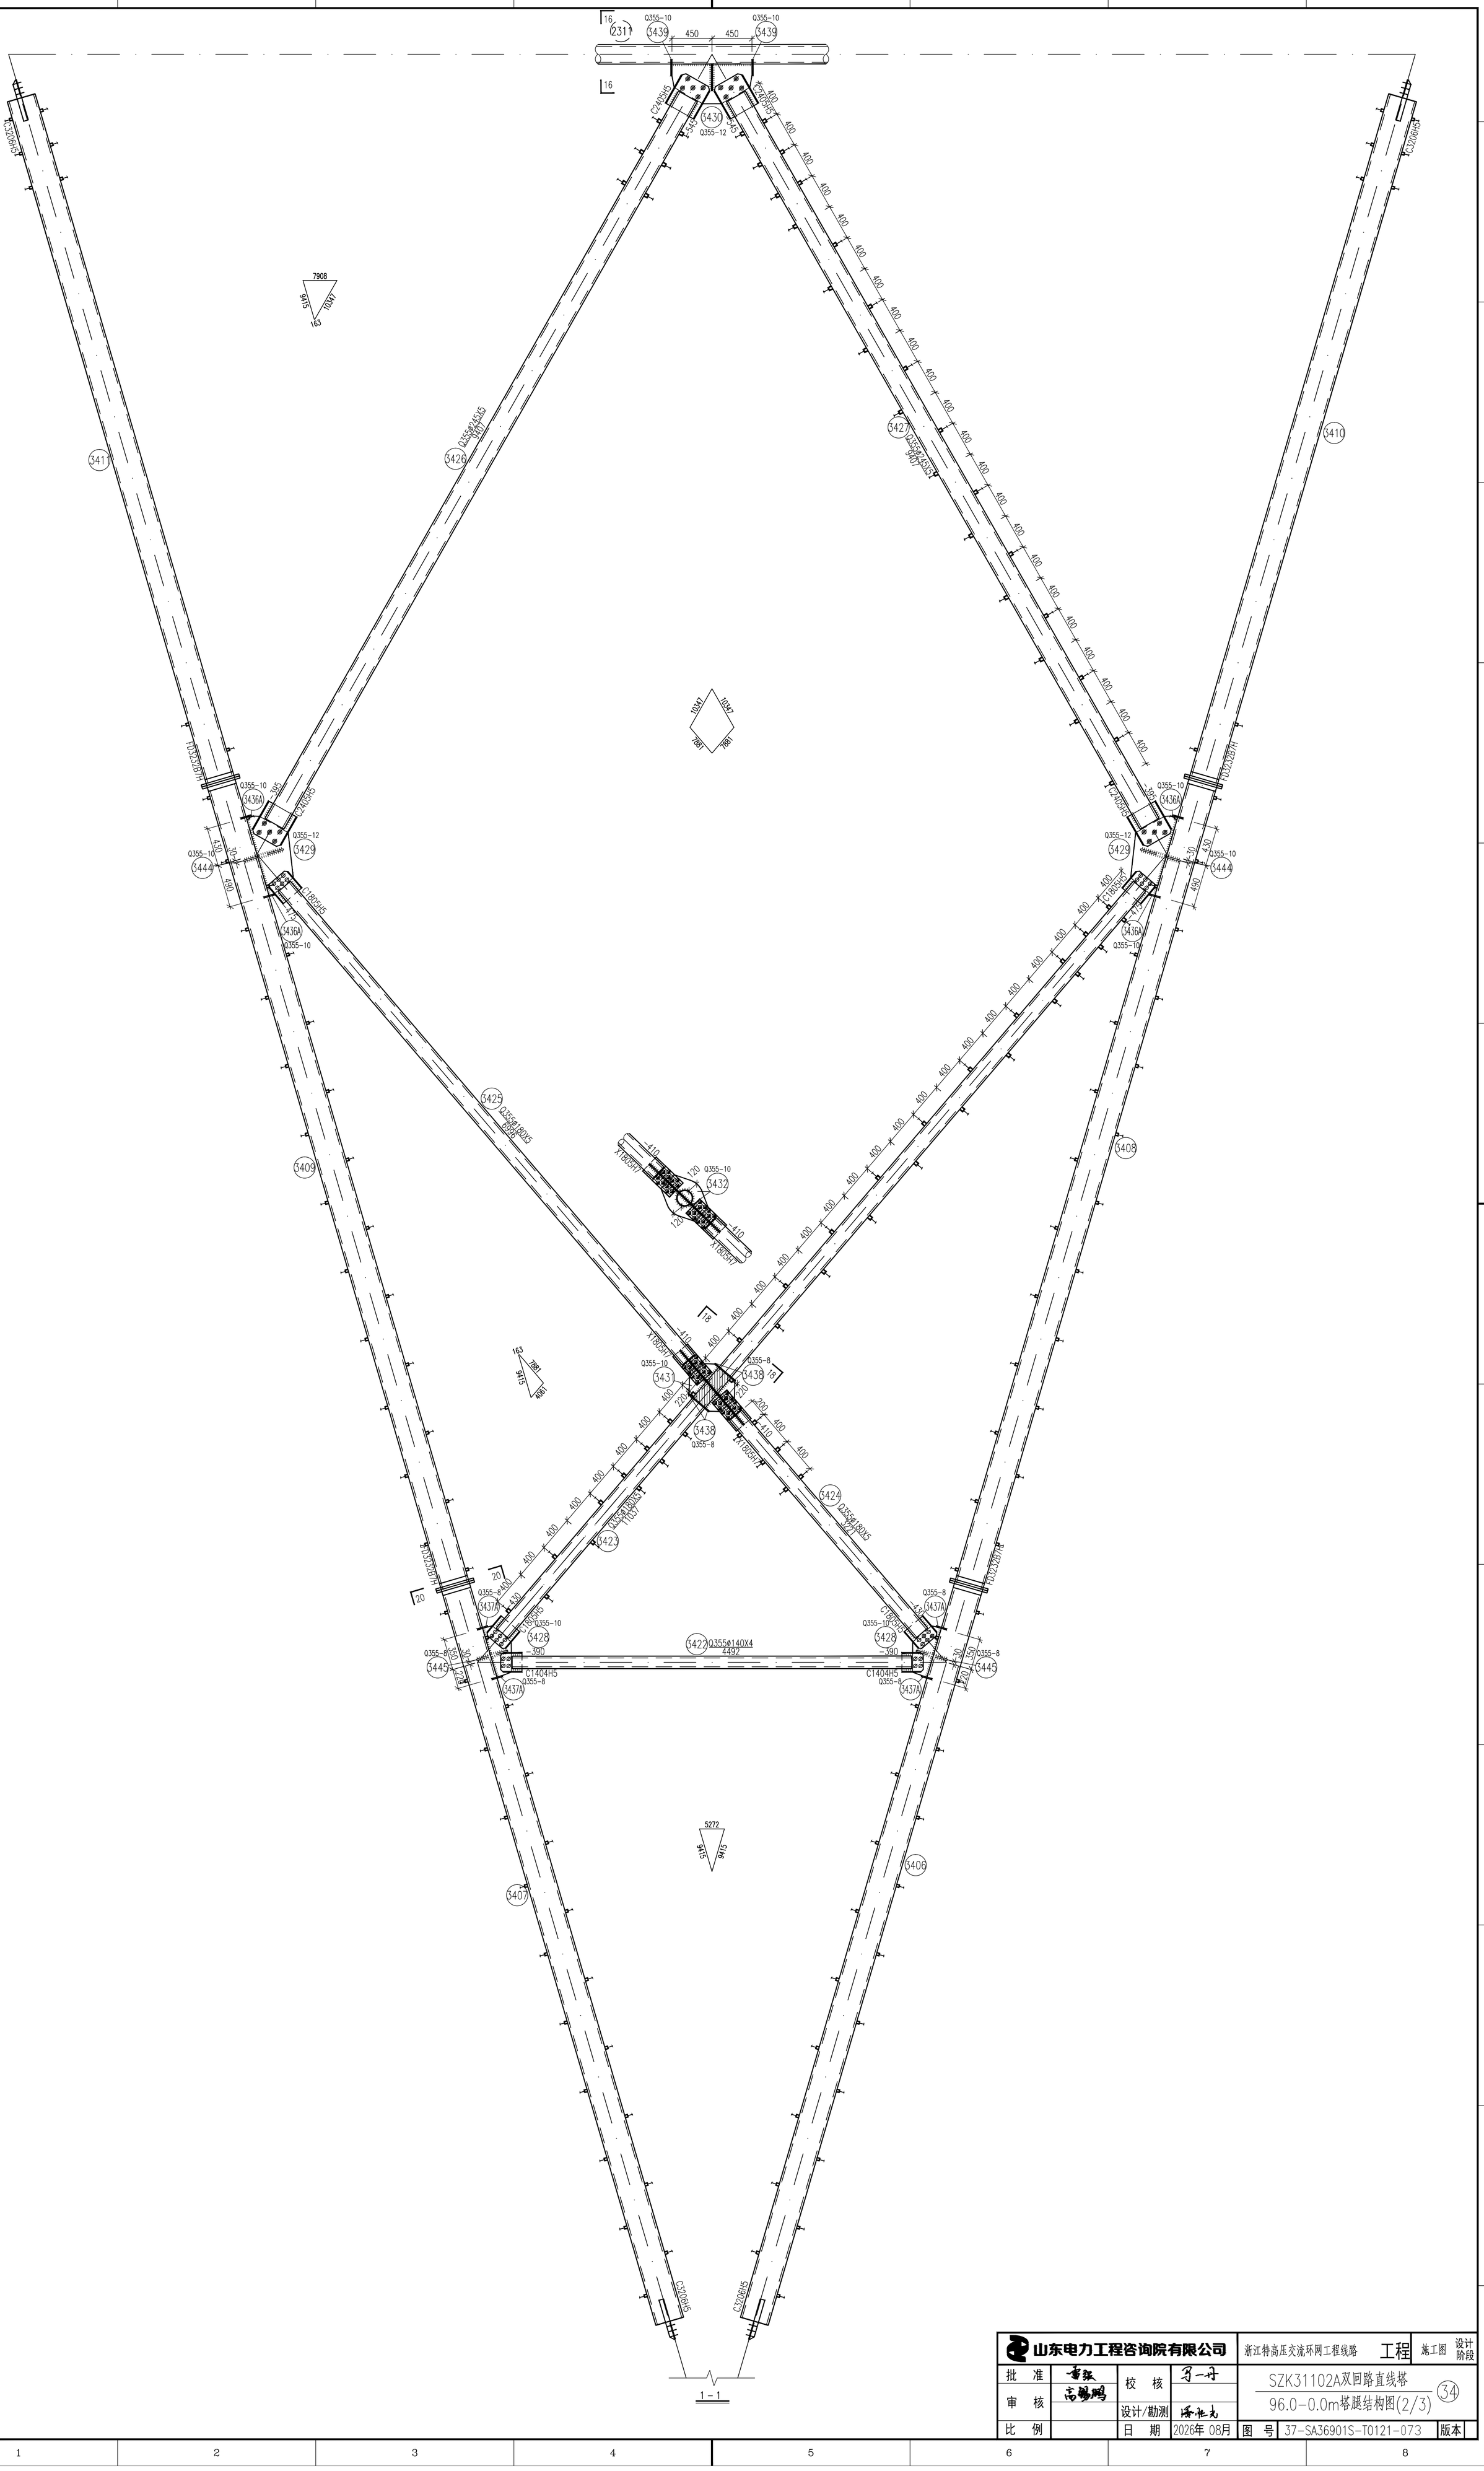


山东电力工程咨询院有限公司				浙江特高压交流环网工程线路 工程	施工图 设计阶段
批 准	重张	校 核	习一丹	SZK31102A双回路直线塔	
审 核	高鹏鹏			96.0-0.0m塔腿结构图(2/3)	34
		设计/勘测	潘胜龙		
比 例		日 期	2026年 08月	图 号 37-SA36901S-T0121-073	版本