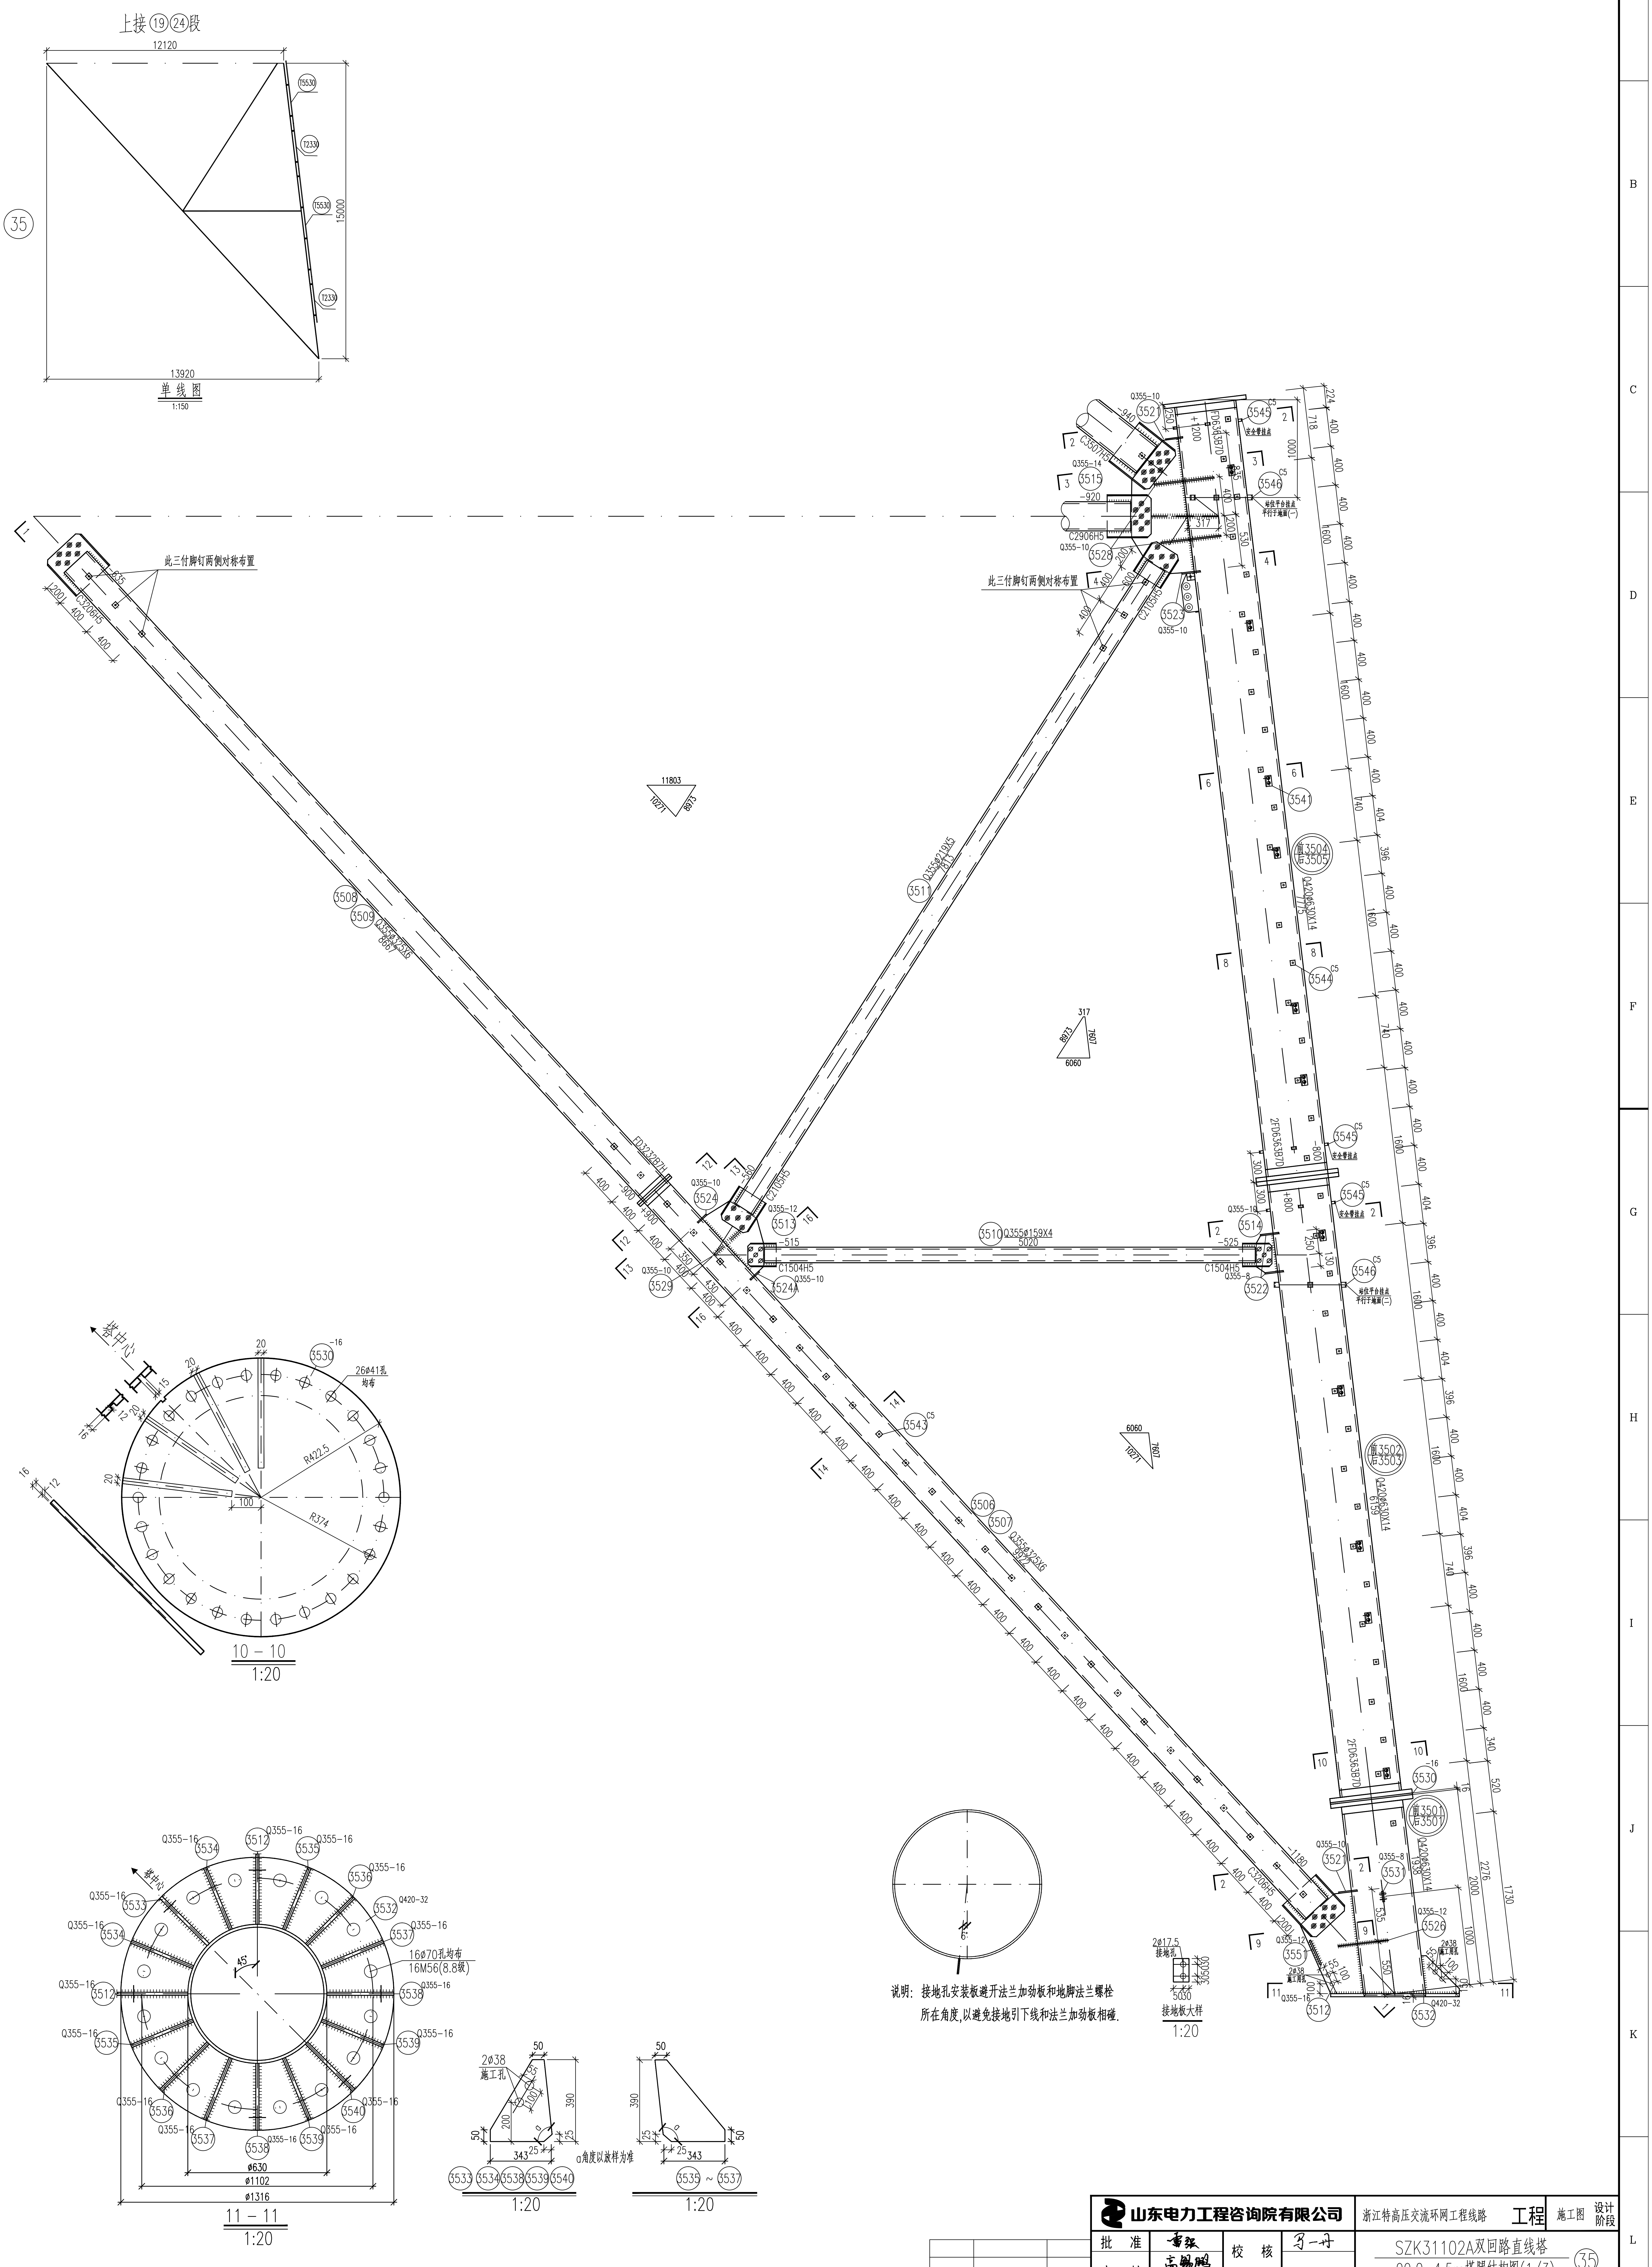
上接⑲㉔段
12120
15000
13920
㉟
单线图
1:150
此三付脚钉两侧对称布置
3508
3509
3511
3510
Q355⌀159X4
5020
3506
3507
3502
3503
3504
3505
3501
3521
3515
3526
3523
3524
3513
3529
3524A
3514
3522
3541
3543
3544
3545
3546
3530
3531
3526
3551
3512
3532
C1504H5
C2105H5
C2906H5
C3206H5
C3507H5
Q355-10
Q355-12
Q355-14
Q355-16
Q420-32
安全警挂点
11803
6060
317
10-10
1:20
R422.5
R374
26⌀41孔均布
塔中心
11-11
1:20
16⌀70孔均布
16M56(8.8级)
⌀630
⌀1102
⌀1316
2⌀38
施工孔
α角度以放样为准
343
390
3533 3534 3538 3539 3540
3535 ~ 3537
2⌀17.5
接地孔
5030
305030
接地板大样
1:20

说明：接地孔安装板避开法兰加劲板和地脚法兰螺栓所在角度,以避免接地引下线和法兰加劲板相碰.

山东电力工程咨询院有限公司

浙江特高压交流环网工程线路 工程　施工图　设计阶段

SZK31102A双回路直线塔
99.0-4.5m塔腿结构图(1/3)　㉟

			批　准	雷强	校　核	习一丹
			审　核	高锡鹏		
电　气	赵庆周	2026.08			设计/勘测	潘胜杰
专　业	会　签	日　期	比　例		日　期	2026年 08月

图　号　37-SA36901S-T0121-075　版本