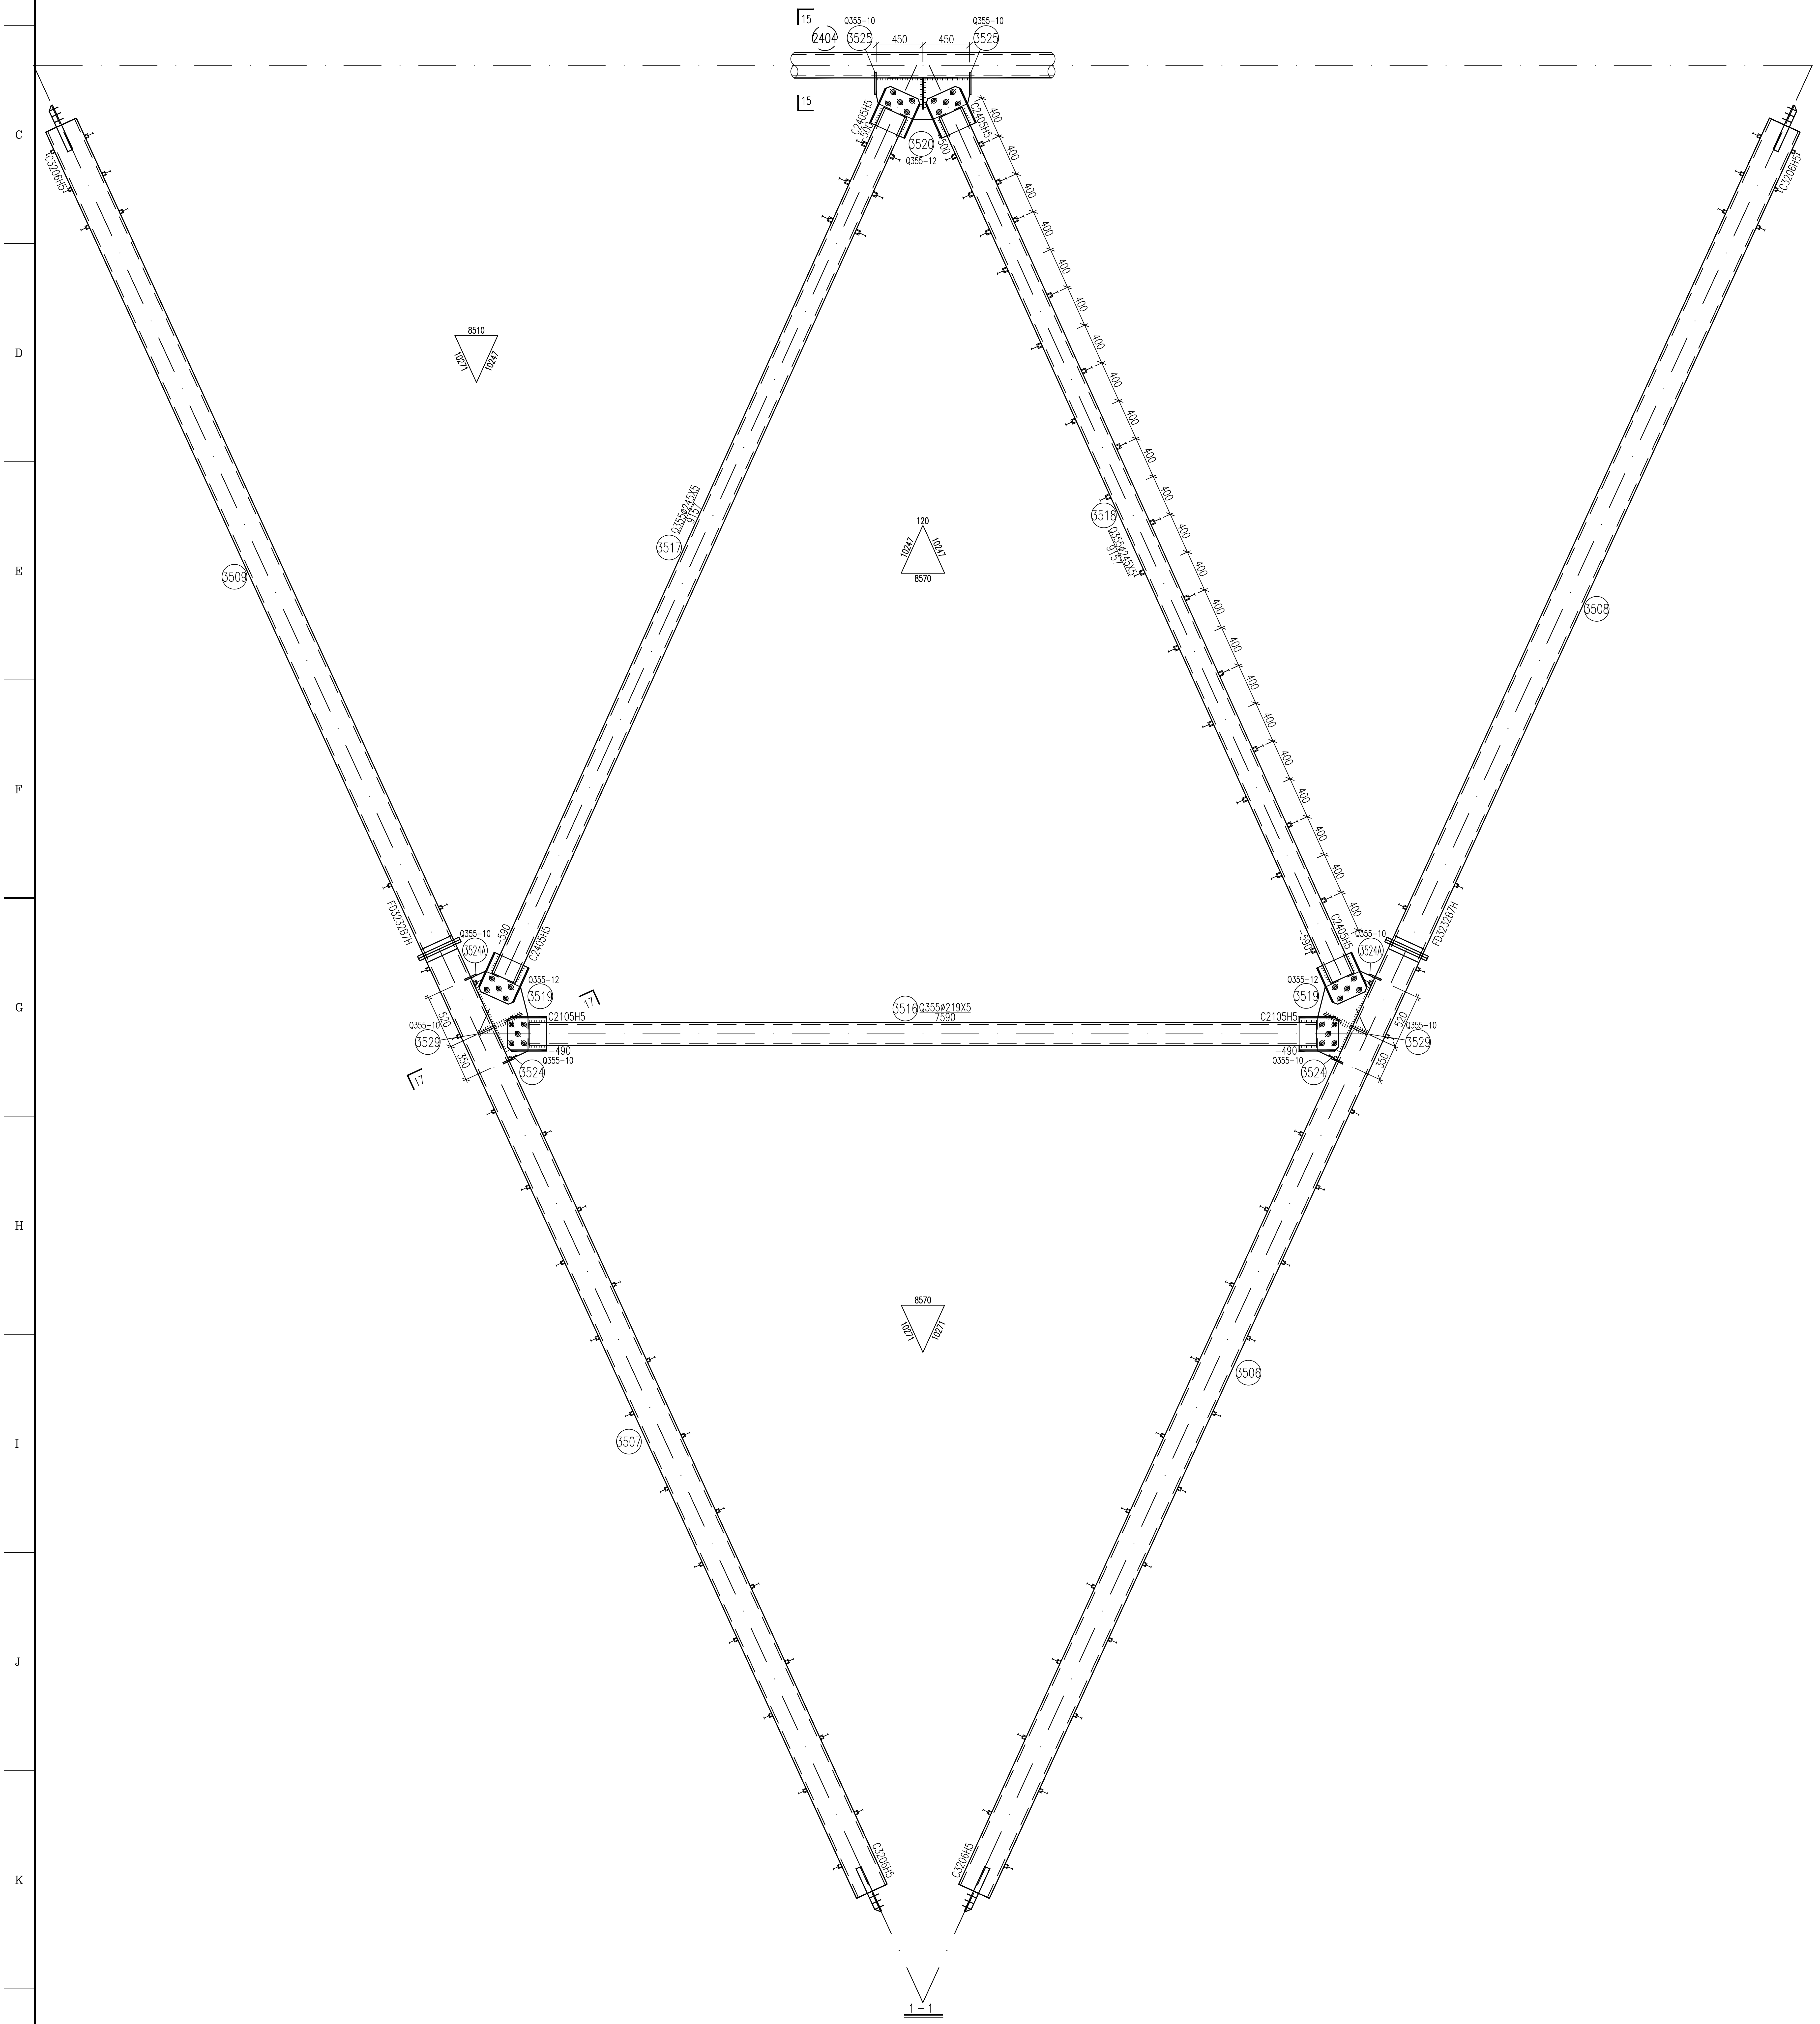
15
15
2404
Q355-10
3525
450
450
Q355-10
3525
C2405H5
500
3520
Q355-12
500
C2405H5
400
400
400
400
400
400
400
400
400
400
400
400
400
400
400
400
400
400
400
400
C3206H5
C3206H5
8510
10271
10247
3509
3517
Q355φ245X5
9157
120
10247
10247
8570
3518
Q355φ245X5
9157
3508
FD3232B7H
Q355-10
3524A
-590
C2405H5
Q355-12
3519
17
C2105H5
3516
Q355φ219X5
7590
Q355-10
3529
520
350
-490
Q355-10
3524
17
FD3232B7H
C2405H5
-590
Q355-10
3524A
Q355-12
3519
C2105H5
520
Q355-10
3529
-490
Q355-10
3524
350
8570
10271
10271
3506
3507
C3206H5
C3206H5
1-1

山东电力工程咨询院有限公司				浙江特高压交流环网工程线路 工程	施工图	设计阶段
批准	雷强	校核	马一丹	SZK31102A双回路直线塔 99.0-4.5m塔腿结构图(2/3)	㉟	
审核	高锡鹏					
		设计/勘测	潘旭光			
比例		日期	2026年 08月	图号 37-SA36901S-T0121-076	版本	