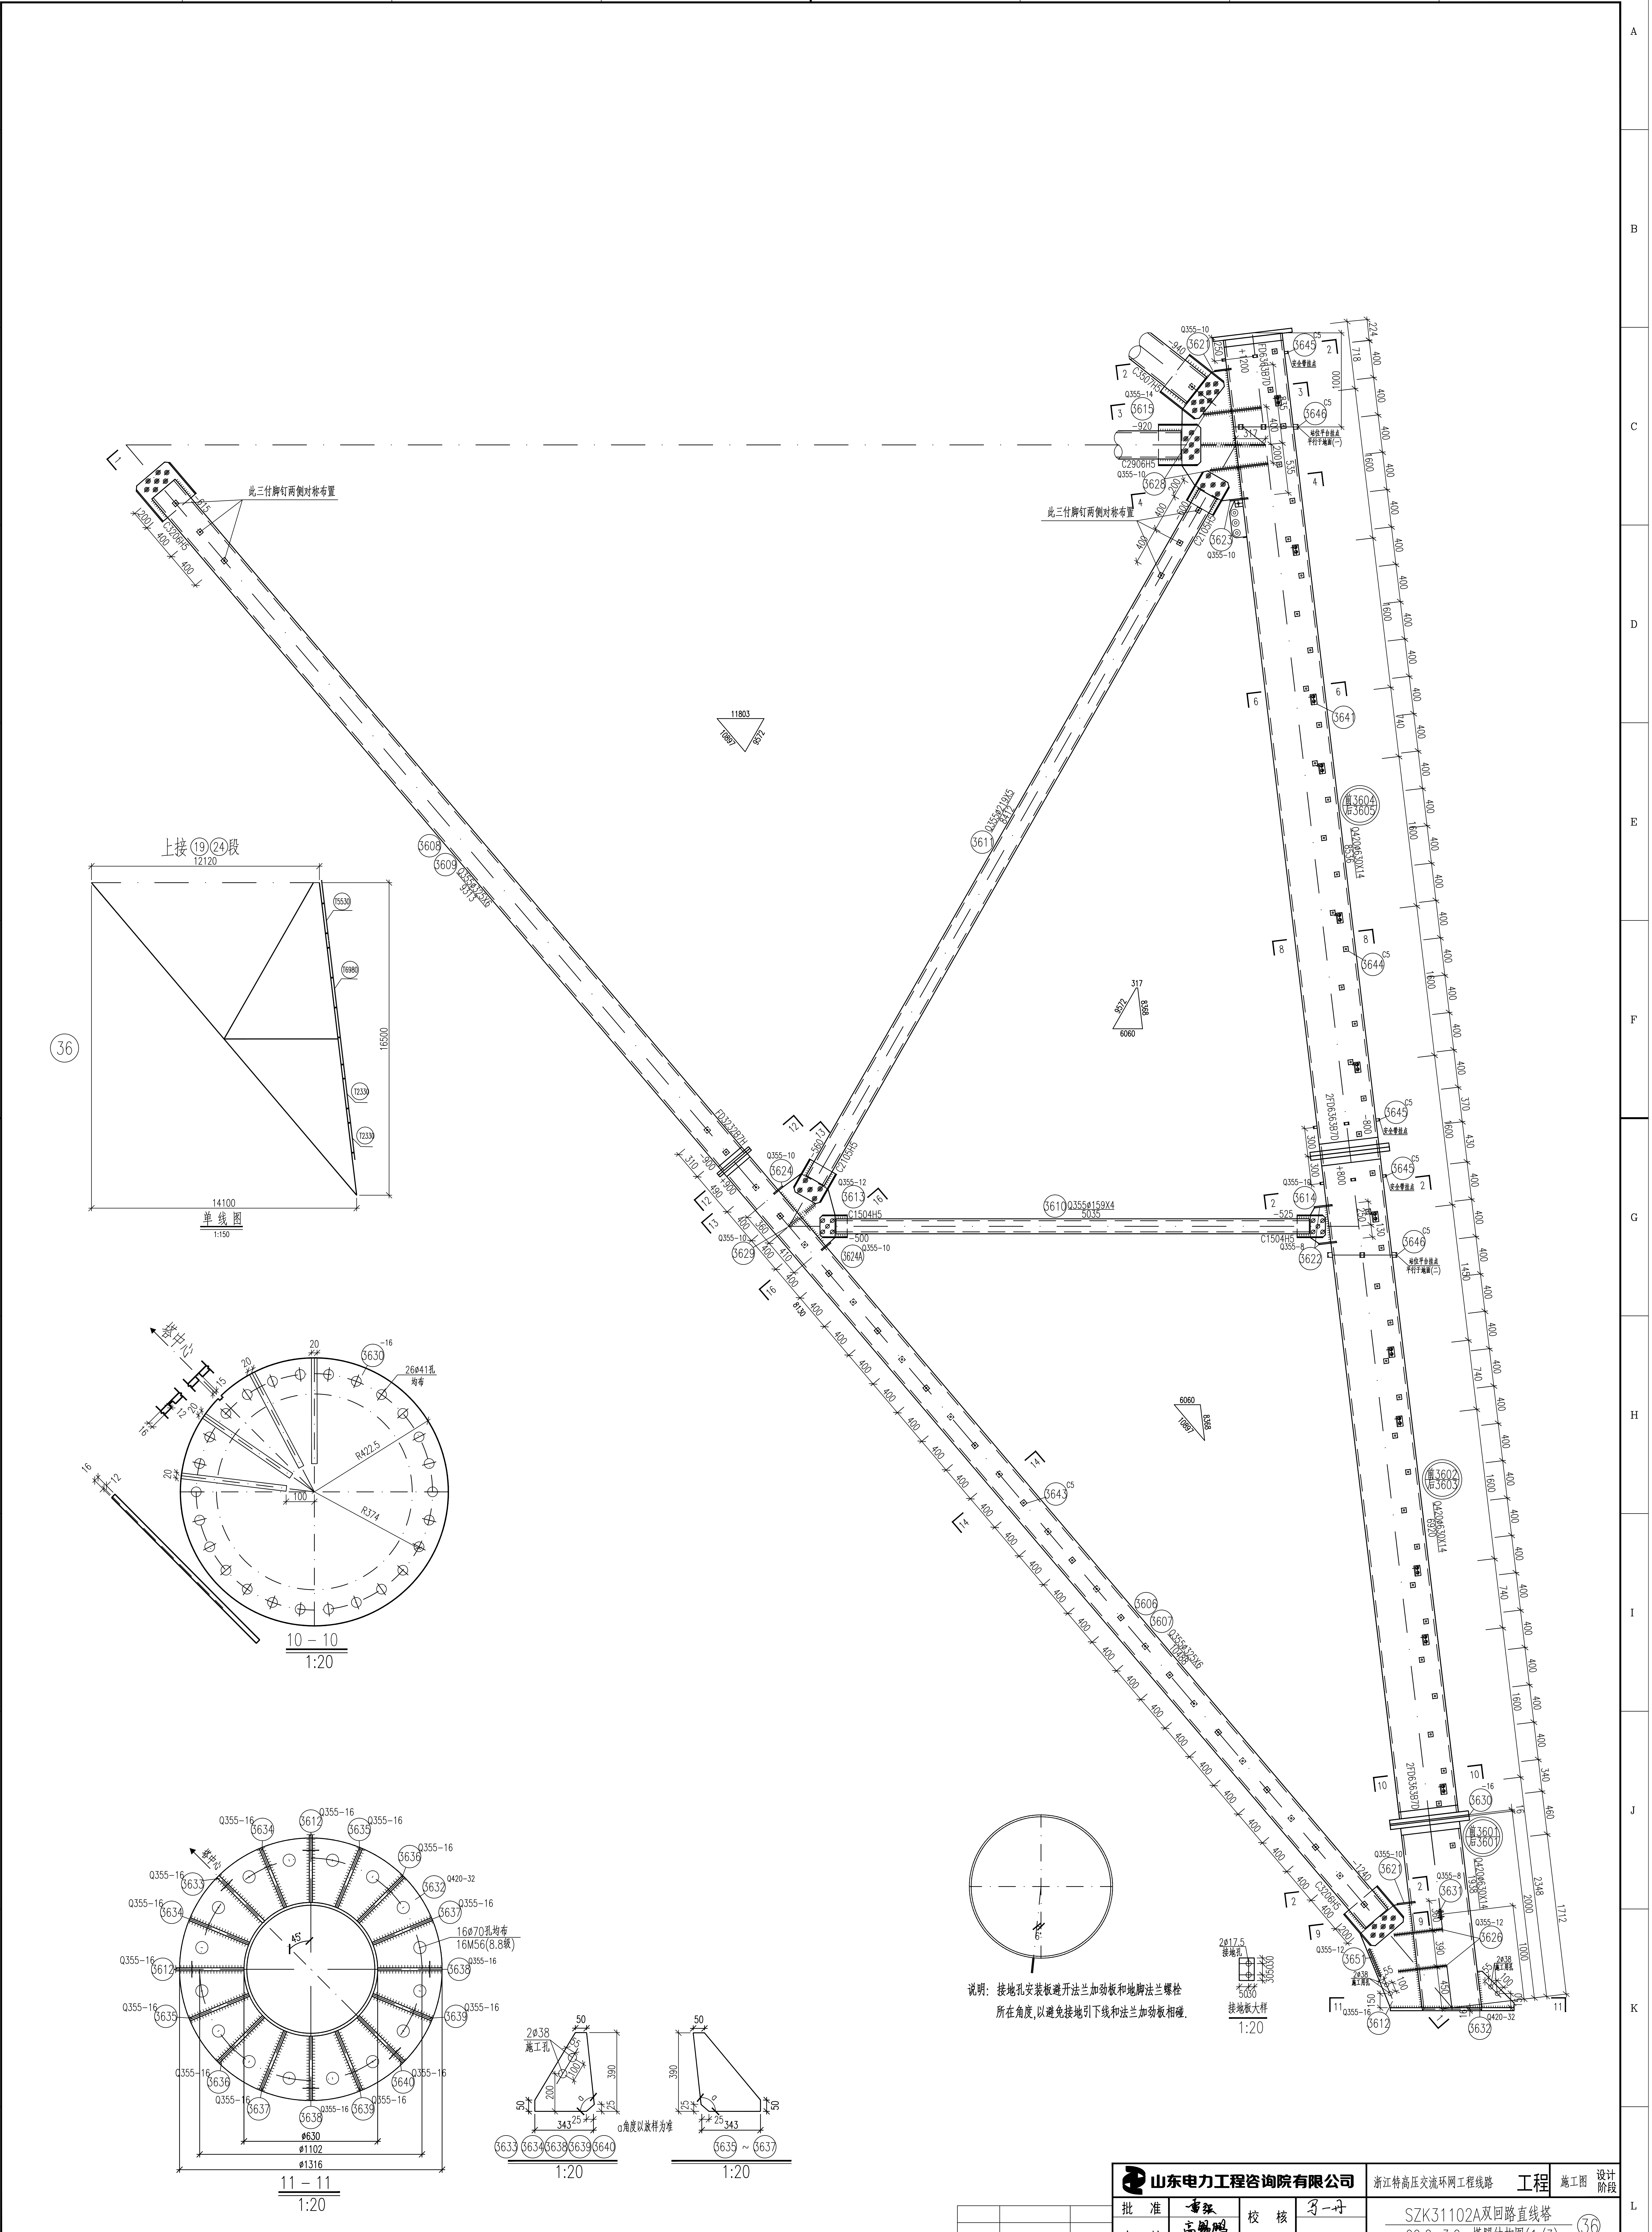
此三付脚钉两侧对称布置
上接⑲㉔段
12120
16500
14100
36
单线图
1:150
10－10
1:20
11－11
1:20
塔中心
26ø41孔均布
16ø70孔均布
16M56(8.8级)
R422.5
R374
ø630
ø1102
ø1316
2ø38 施工孔
α角度以放样为准
3633 3634 3638 3639 3640
3635 ~ 3637
1:20
2ø17.5 接地孔
接地板大样
1:20
3601
3602 3603
3604 3605
3606 3607
3608 3609
3610 Q355ø159X4
3611 Q355ø219X5
3612
3613
3614
3615
3621
3622
3623
3624
3624A
3626
3628
3629
3630
3631
3632
3641
3643
3644
3645
3646
3651

说明：接地孔安装板避开法兰加劲板和地脚法兰螺栓所在角度，以避免接地引下线和法兰加劲板相碰。

山东电力工程咨询院有限公司				浙江特高压交流环网工程线路 工程	施工图	设计阶段
批准		校核		SZK31102A双回路直线塔 99.0−3.0m塔腿结构图(1/3)	㊱	
审核	高锡鹏	设计/勘测				
比例		日期	2026年 08月	图号	37−SA36901S−T0121−078	版本

电气	赵庆周	2026.08
专业	会签	日期