

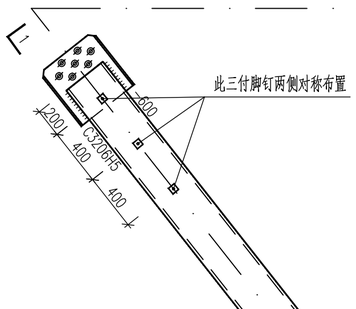


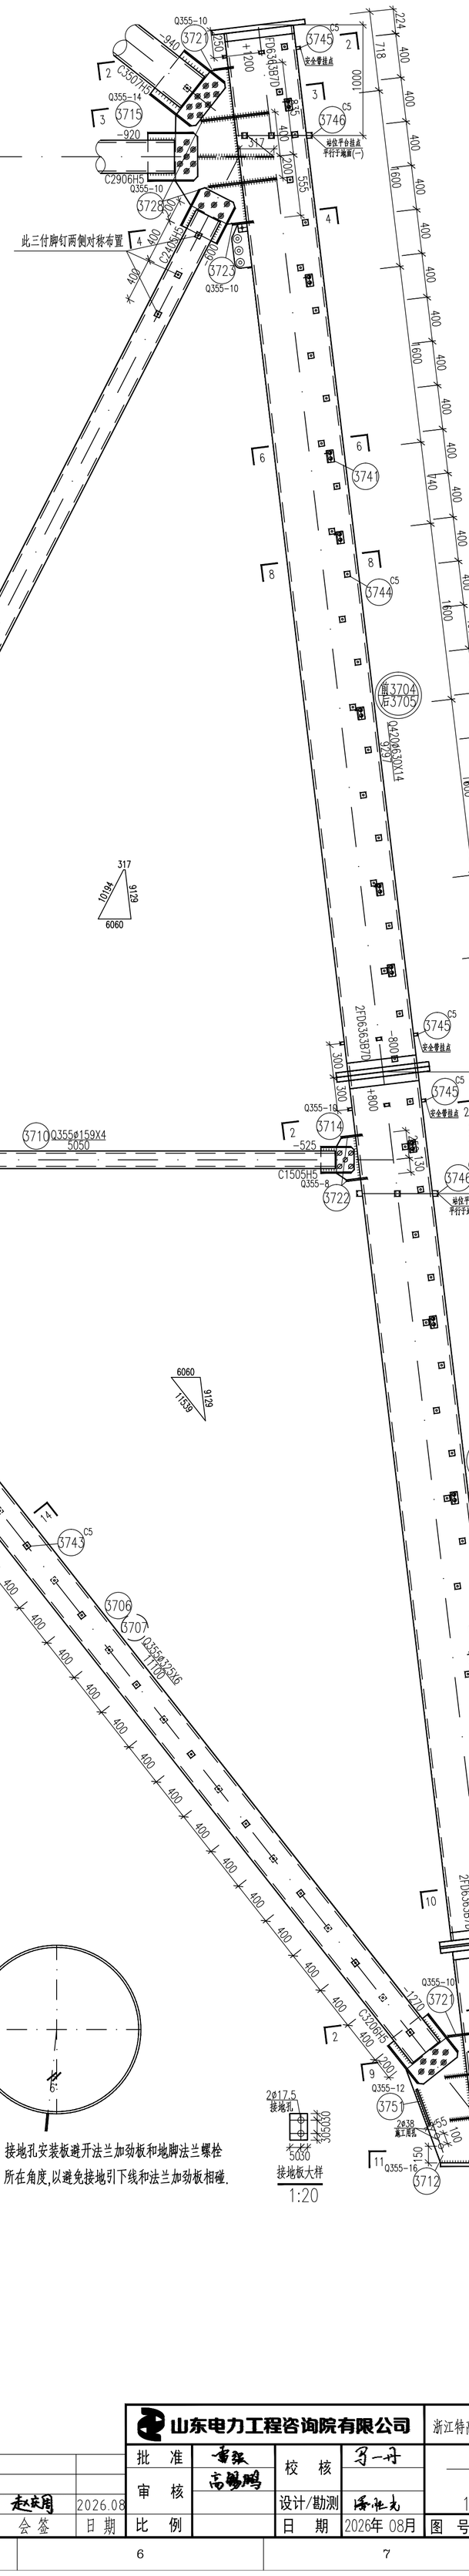


上接⑲㉔段

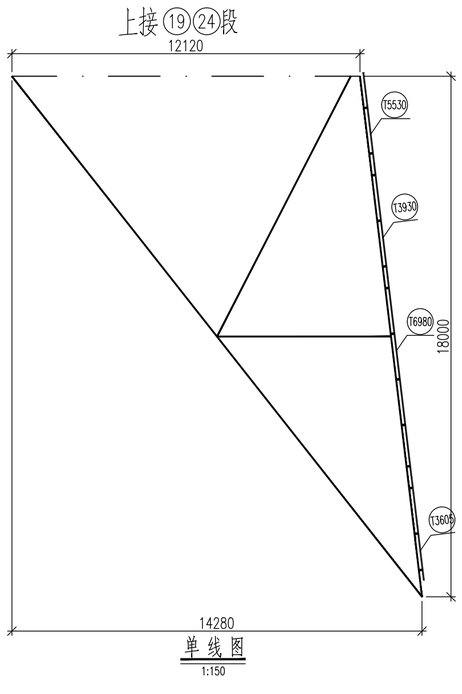

37


单线图
1:150

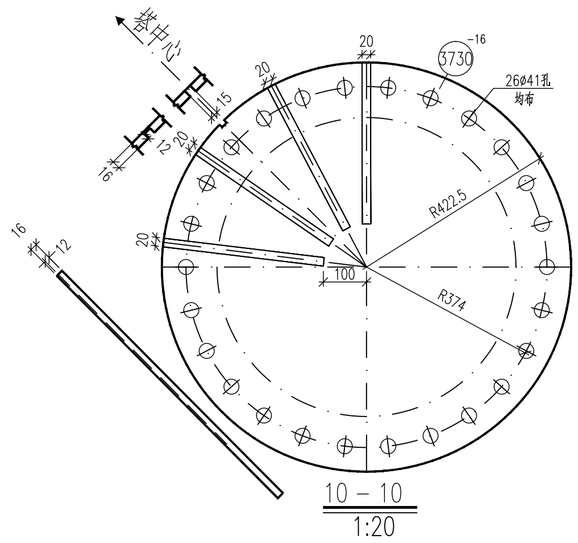

10 – 10
1:20

11 – 11
1:20

1:20

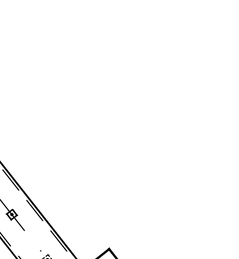

6:

				山东电力工程咨询院有限公司		浙江特高压交流环网工程线路 工程	施工图 设计阶段
				批 准	雷强 高锡鹏	校 核	习一舟	SZK31102A双回路直线塔	
				审 核		设计/勘测	潘世龙	99.0-1.5m塔腿结构图(1/3)	37
电 气	赵庆周	2026.08						102.0-4.5m塔腿结构图(1/3)	
专 业	会 签	日 期		比 例		日 期	2026年 08月	图 号 37-SA36901S-T0121-081	版本