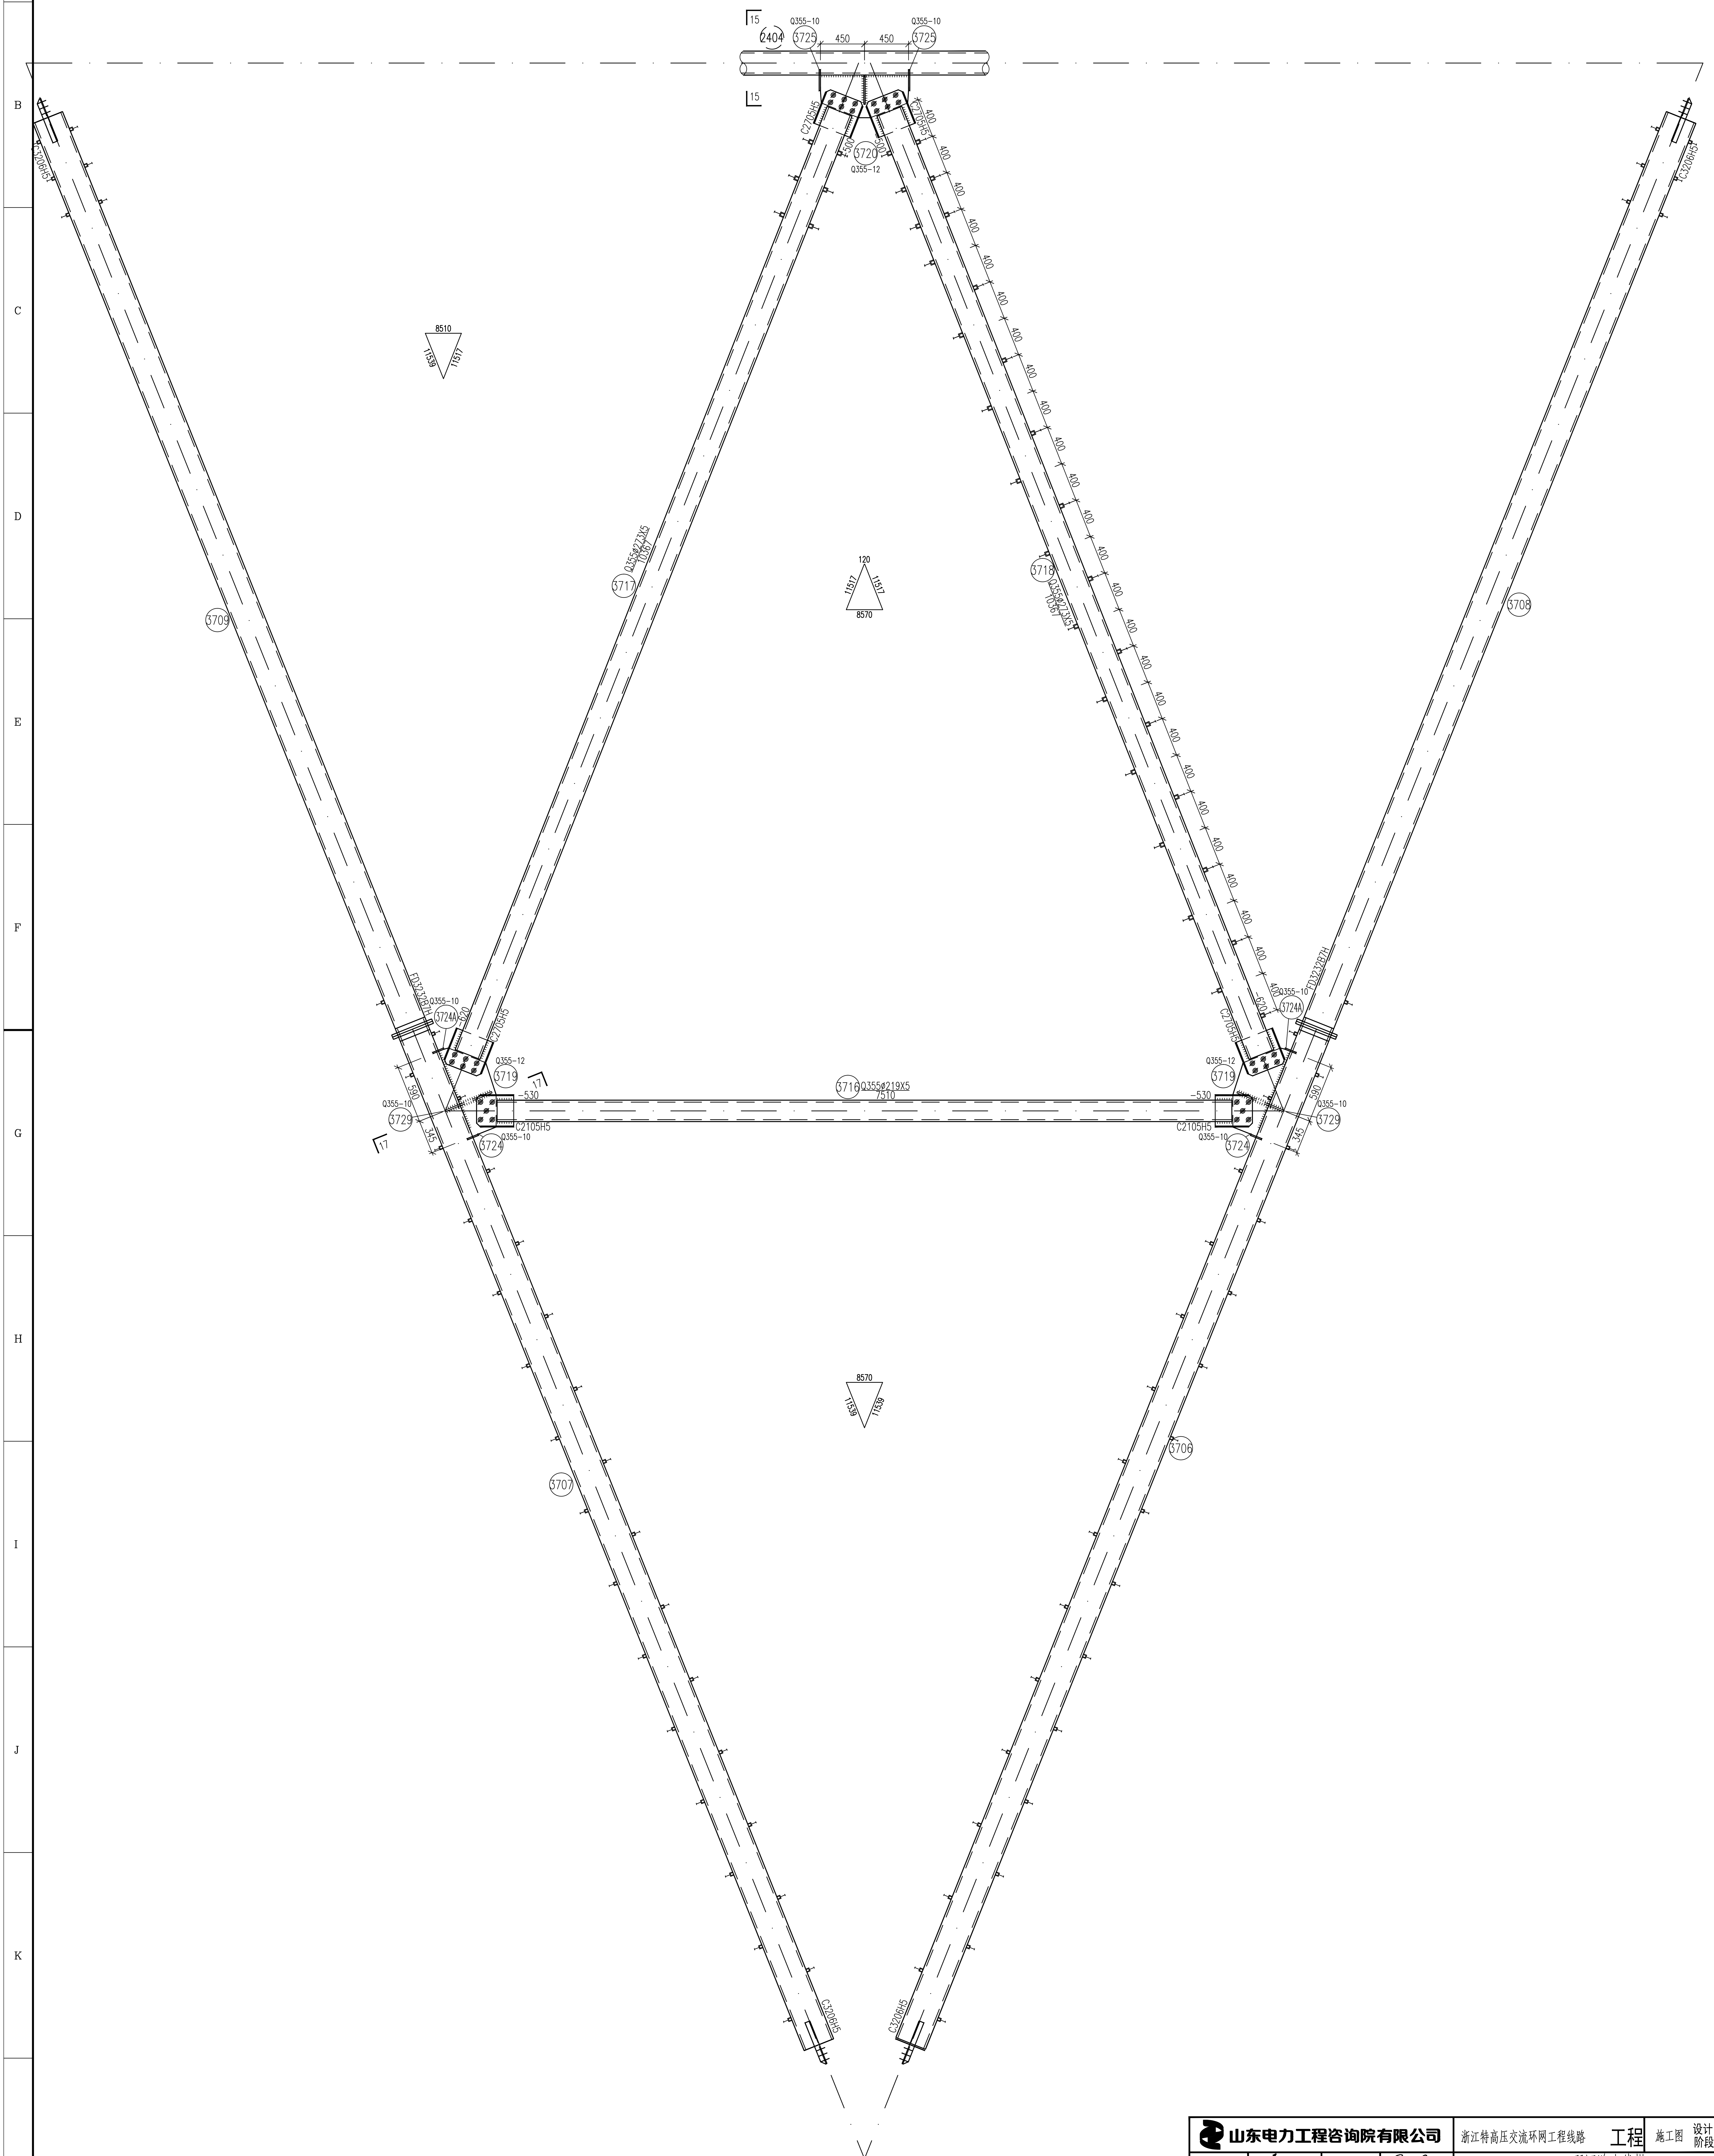

1-1

山东电力工程咨询院有限公司				浙江特高压交流环网工程线路 工程	施工图 设计阶段
批 准	雷强	校 核	马一丹	SZK31102A双回路直线塔 99.0-1.5m塔腿结构图(2/3) 102.0-4.5m塔腿结构图(2/3)	㊲
审 核	高锡鹏				
		设计/勘测	潘胜克		
比 例		日 期	2026年 08月	图 号 37-SA36901S-T0121-082	版本