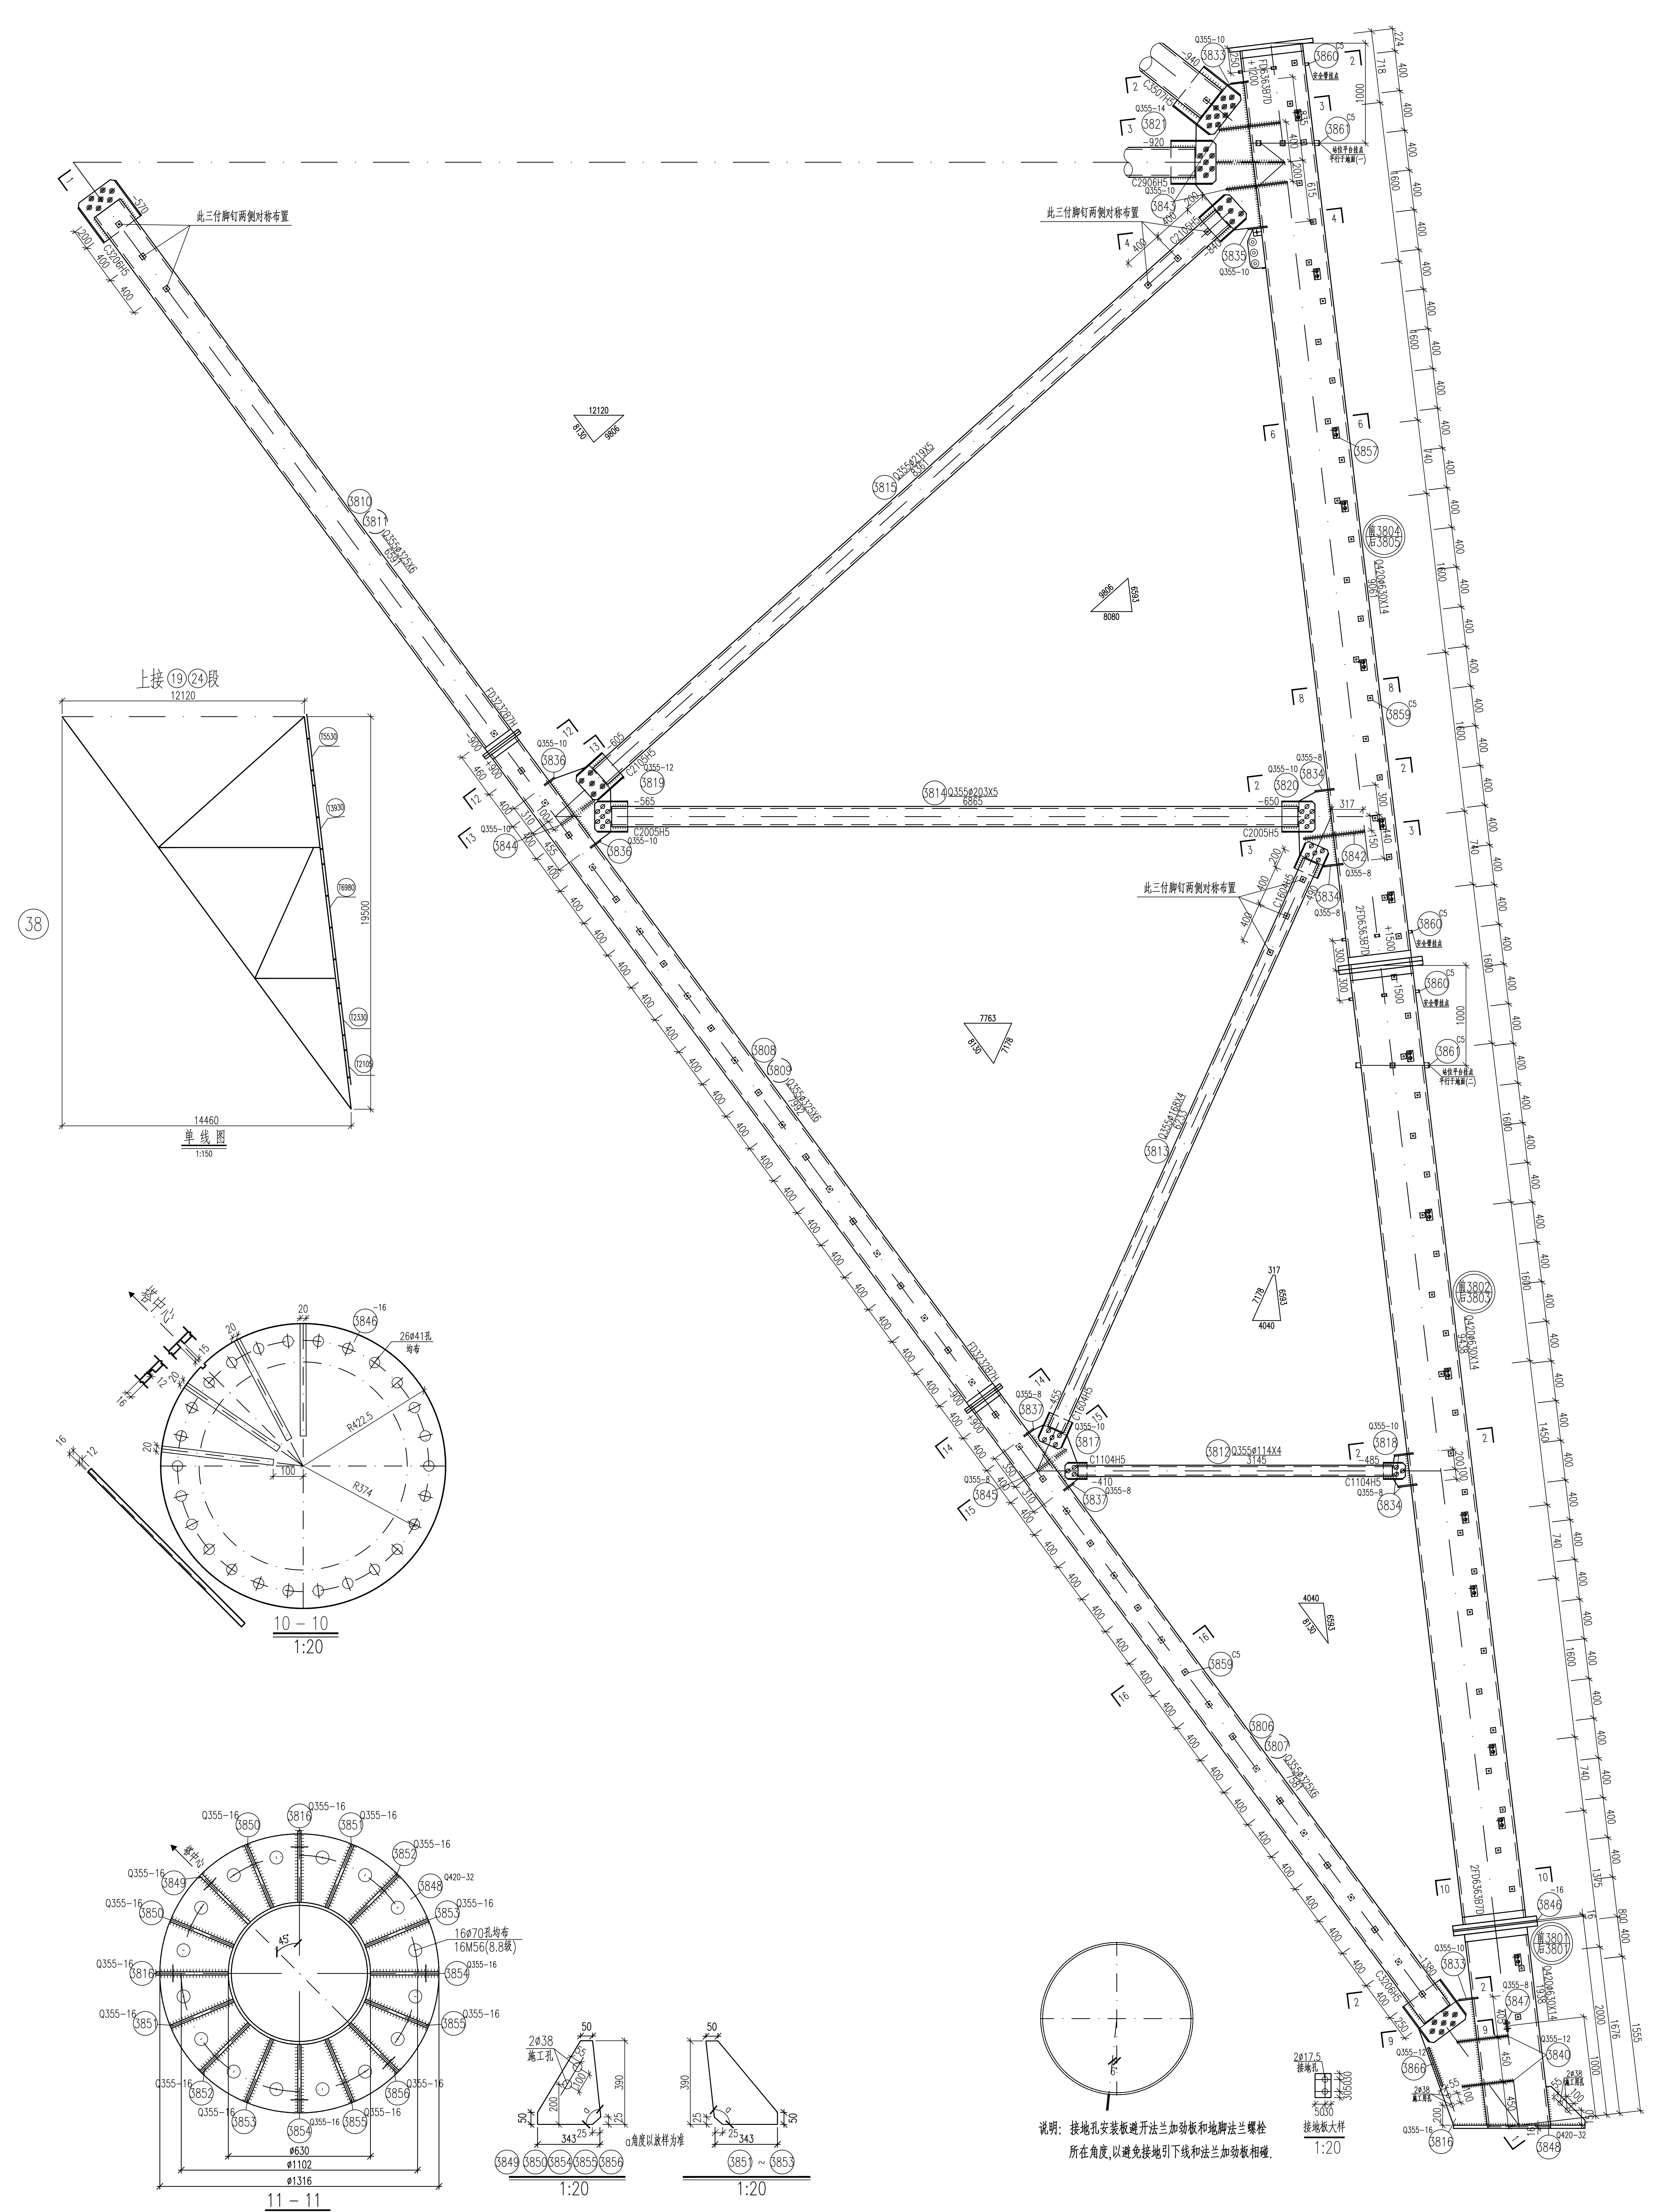
上接⑲㉔段
12120
19500
14460
㊳
此三付脚钉两侧对称布置
安全帽挂点
Q355ø273X6
Q355ø219X5
Q355ø203X5
Q355ø168X4
Q355ø114X4
Q420ø630X14
FD323S87H
2FD63S87D
C2005H5
C1104H5
3801
3802
3803
3804
3805
3806
3807
3808
3809
3810
3811
3812
3813
3814
3816
3817
3818
3819
3820
3821
3833
3834
3836
3837
3840
3842
3844
3845
3846
3847
3848
3857
3859
3860
3861
3866
26ø41孔均布
R422.5
R374
16ø70孔均布
16M56(8.8级)
ø630
ø1102
ø1316
2ø38 施工孔
α角度以放样为准
2ø17.5 接地孔
塔中心

单线图
1:150

10－10
1:20

11－11
1:20

3849 3850 3854 3855 3856
1:20

3851 ~ 3853
1:20

接地板大样
1:20

说明：接地孔安装板避开法兰加劲板和地脚法兰螺栓
所在角度,以避免接地引下线和法兰加劲板相碰.

			山东电力工程咨询院有限公司			浙江特高压交流环网工程线路 工程	施工图 设计阶段
			批 准		校 核	SZK31102A双回路直线塔 99.0－0.0m塔腿结构图(1/3) 102.0－3.0m塔腿结构图(1/3)	㊳
			审 核	高锡鹏			
电 气	赵庆周	2026.08			设计/勘测		
专 业	会 签	日 期	比 例		日 期 2026年 08月	图 号 37－SA36901S－T0121－084	版本