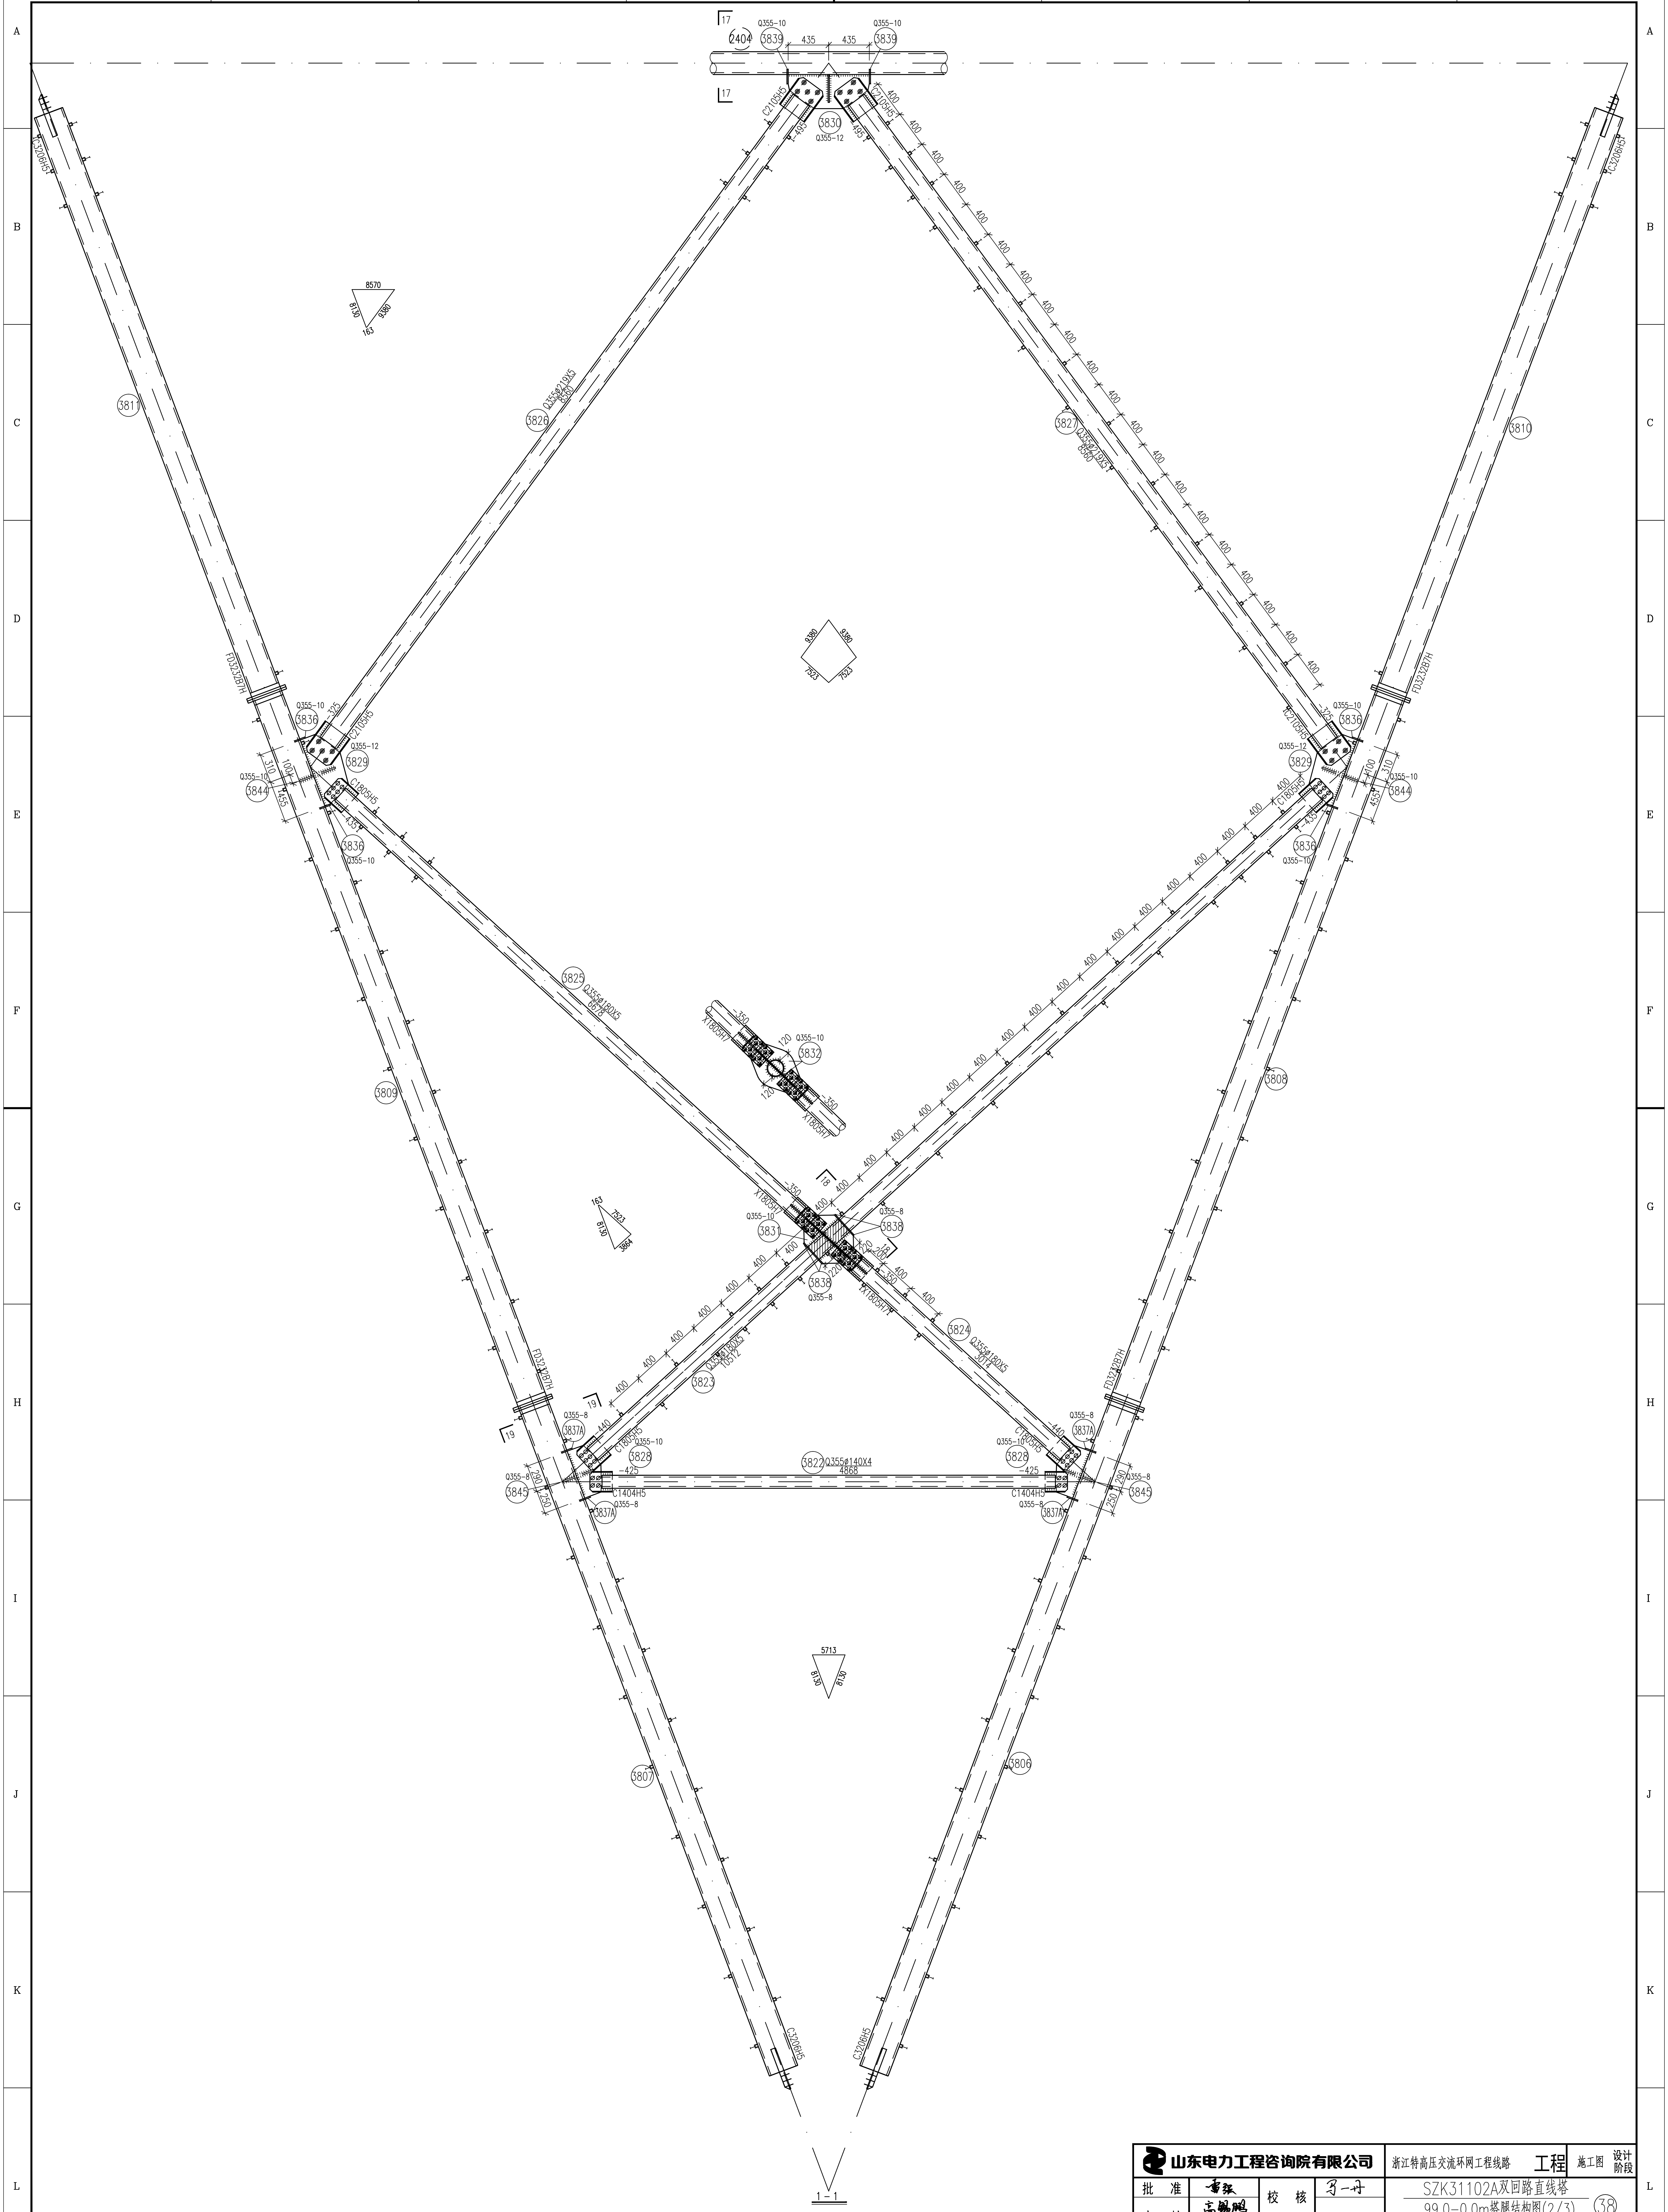
17
2404
Q355-10
3839
435
435
Q355-10
3839
17
C210
3830
Q355-12
C210
400
3811
C320
8570
8130
9380
163
3826
Q355φ219X5
3827
Q355φ219X5
3810
C320
9380
9380
7523
7523
FD322
FD322
Q355-10
3836
3829
Q355-12
Q355-10
3844
C180
3836
Q355-10
Q355-10
3836
Q355-12
3829
Q355-10
3844
C180
3836
Q355-10
3825
Q355φ180X5
X180
350
120
Q355-10
3832
120
350
X180
3809
3808
163
7523
8130
3864
X180
350
Q355-10
3831
Q355-8
3838
3838
Q355-8
X180
3824
Q355φ180X5
3823
Q355φ180X5
FD322
FD322
19
Q355-8
3837A
C180
Q355-10
3828
3822
Q355φ140X4
4868
Q355-10
3828
C180
Q355-8
3837A
Q355-8
3845
C140
Q355-8
3837A
C140
Q355-8
3837A
Q355-8
3845
5713
8130
8130
3807
3806
C320
C320
1-1

山东电力工程咨询院有限公司				浙江特高压交流环网工程线路 工程	施工图 设计阶段
批　准	雷张	校　核	马一丹	SZK31102A双回路直线塔 99.0-0.0m塔腿结构图(2/3) 102.0-3.0m塔腿结构图(2/3)	㊳
审　核	高锡鹏				
		设计/勘测	潘胜克		
比　例		日　期	2026年 08月	图　号 37-SA36901S-T0121-085	版本