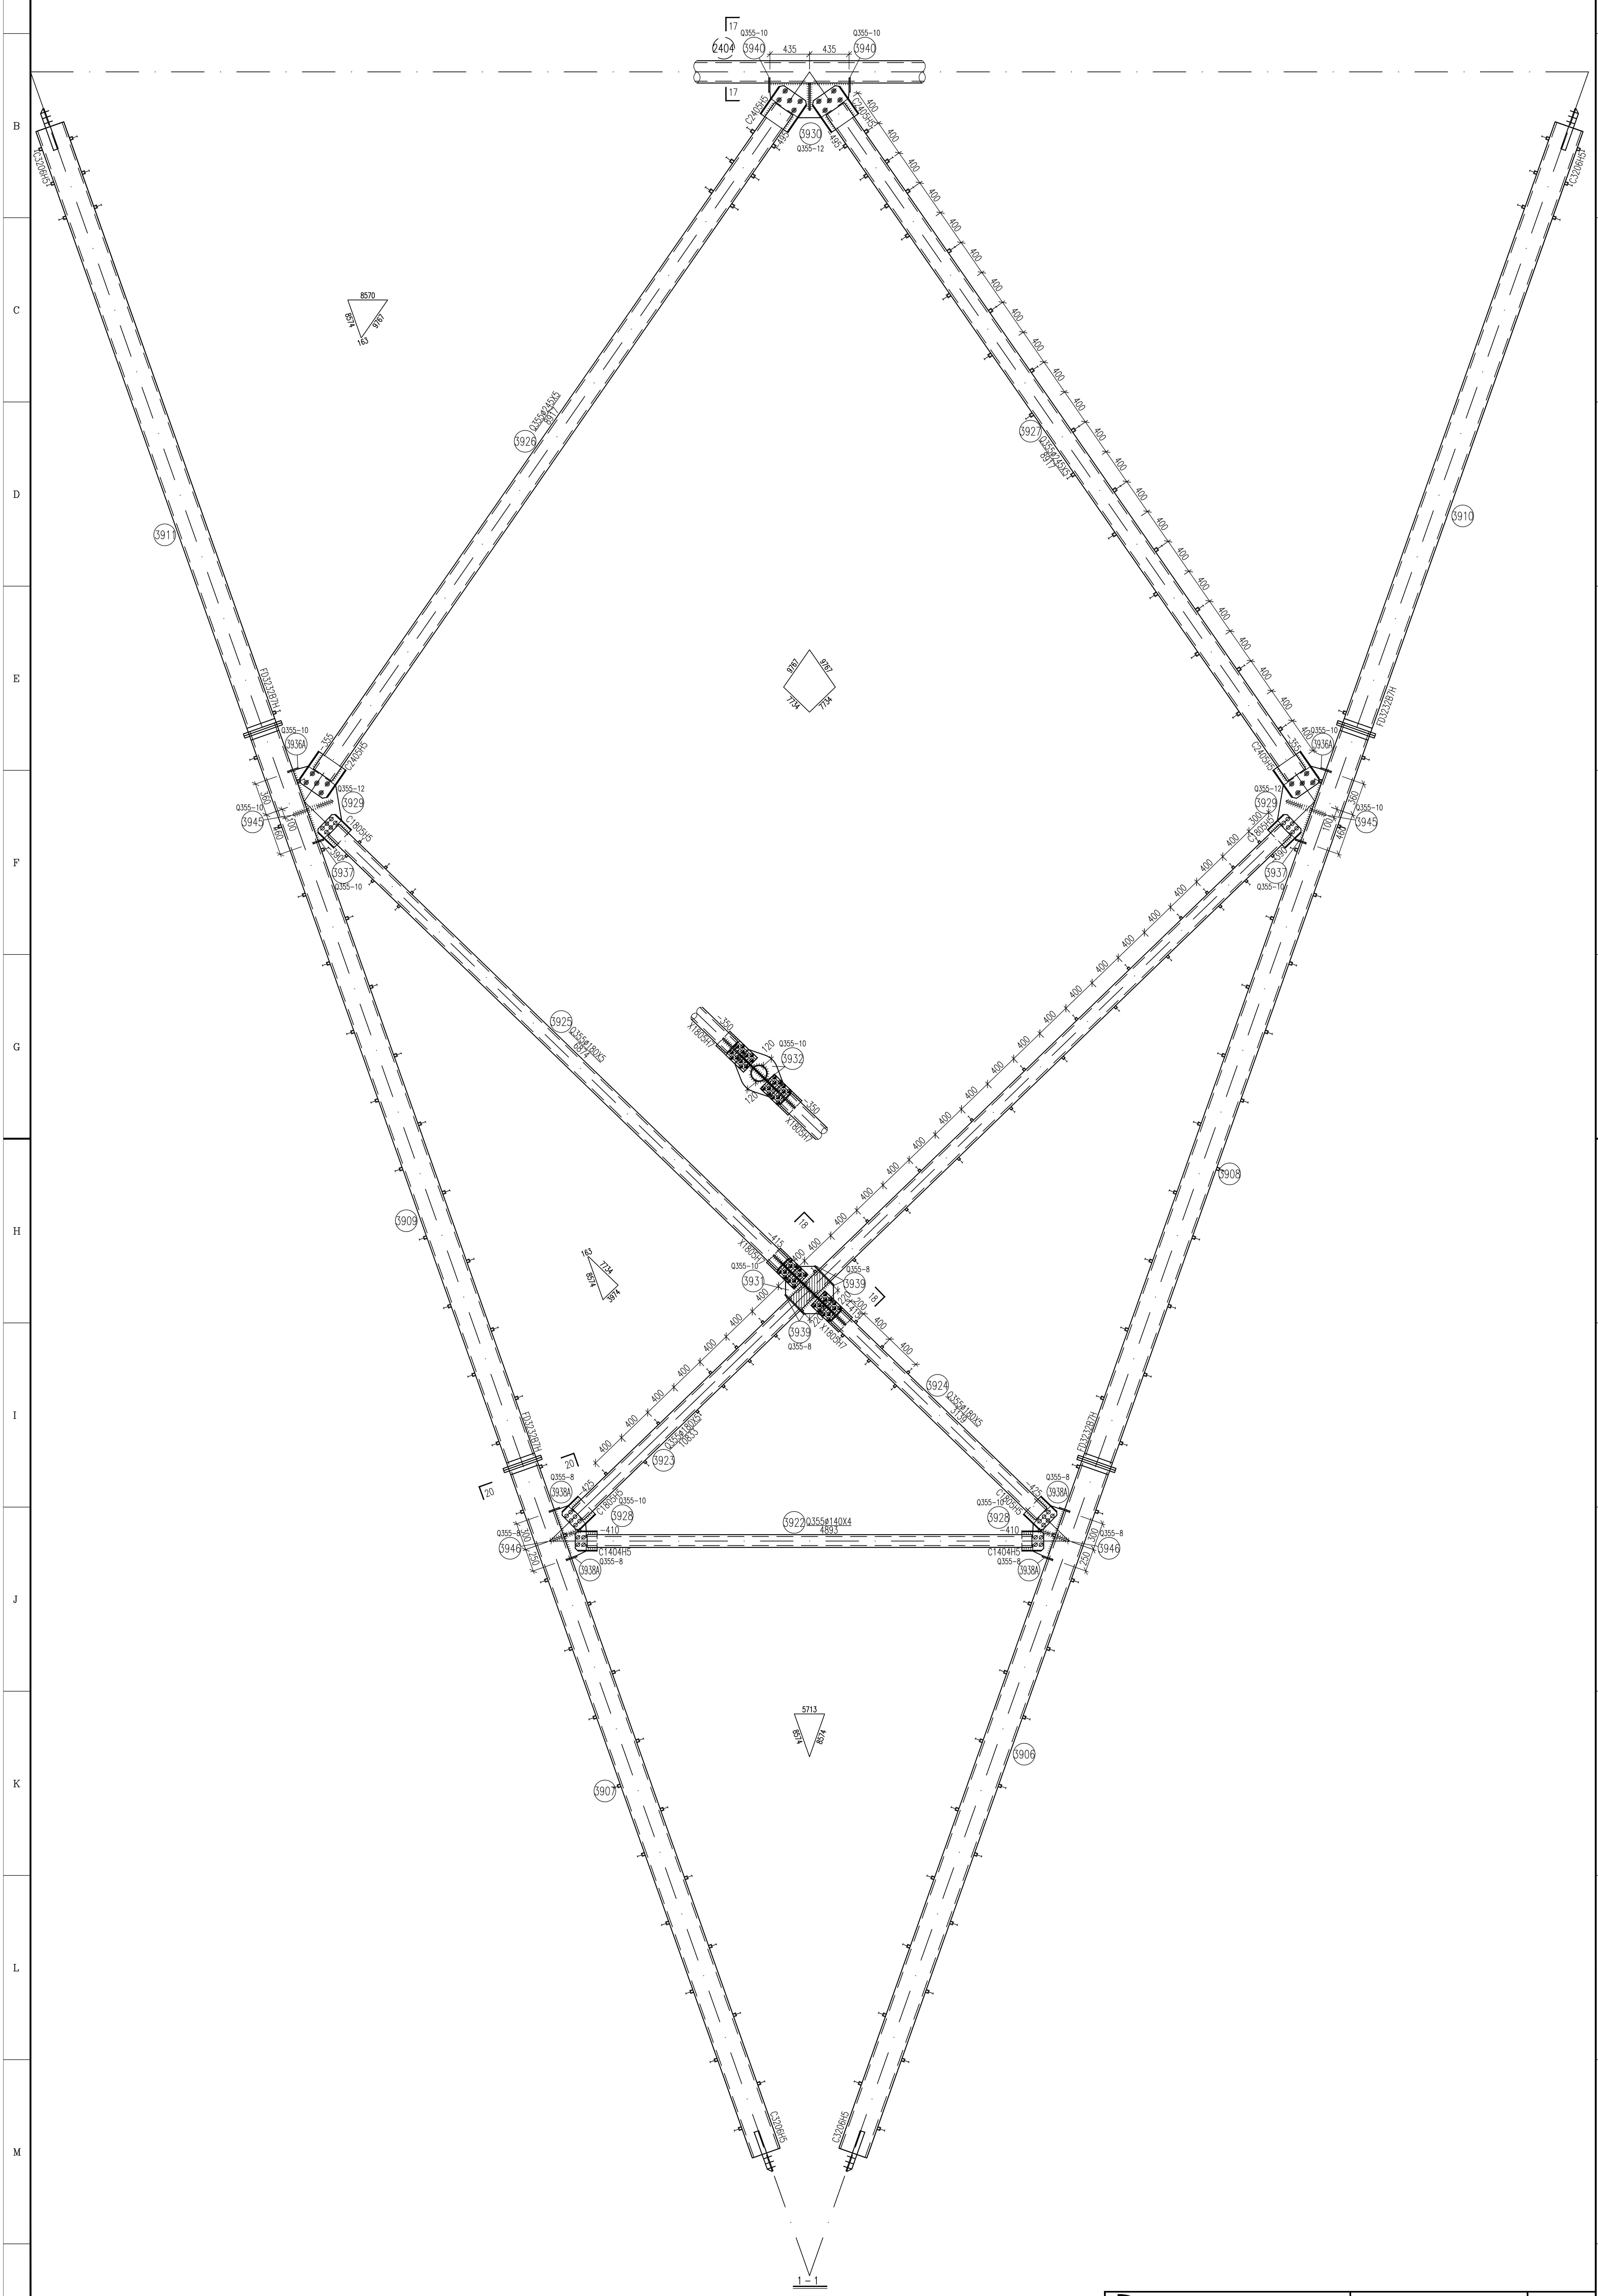

2404
3940
Q355-10
435
435
3940
Q355-10
17
17
C2405H5
C2405H5
495
495
3930
Q355-12
400
3926
Q355φ245X5
8917
3927
Q355φ245X5
8917
C3206H5
C3206H5
8570
8574
9767
163
9767
9767
7734
7734
3911
3910
FD3232B7H
FD3232B7H
Q355-10
3936A
-355
C2405H5
Q355-12
3929
Q355-10
3945
360
100
460
C1805H5
-390
3937
Q355-10
3925
Q355φ180X5
6874
X1805H7
-350
120
Q355-10
3932
120
-350
X1805H7
3908
3909
18
18
-415
X1805H7
Q355-10
3931
3939
Q355-8
220
200
-415
220
X1805H7
3939
Q355-8
163
7734
8574
3974
3924
Q355φ180X5
3139
3923
Q355φ180X5
10833
20
20
Q355-8
3938A
-425
C1805H5
Q355-10
3928
-410
3922
Q355φ140X4
4893
C1404H5
Q355-8
3946
300
250
3938A
Q355-8
5713
8574
8574
3906
3907
C3206H5
C3206H5

1-1

山东电力工程咨询院有限公司				浙江特高压交流环网工程线路 工程	施工图	设计阶段
批 准		校 核	马一丹	SZK31102A双回路直线塔 102.0-1.5m塔腿结构图(2/3) 105.0-4.5m塔腿结构图(2/3)	㊴	
审 核	高锡鹏	设计/勘测				
比 例		日 期	2026年 08月	图 号 37-SA36901S-T0121-088	版本	