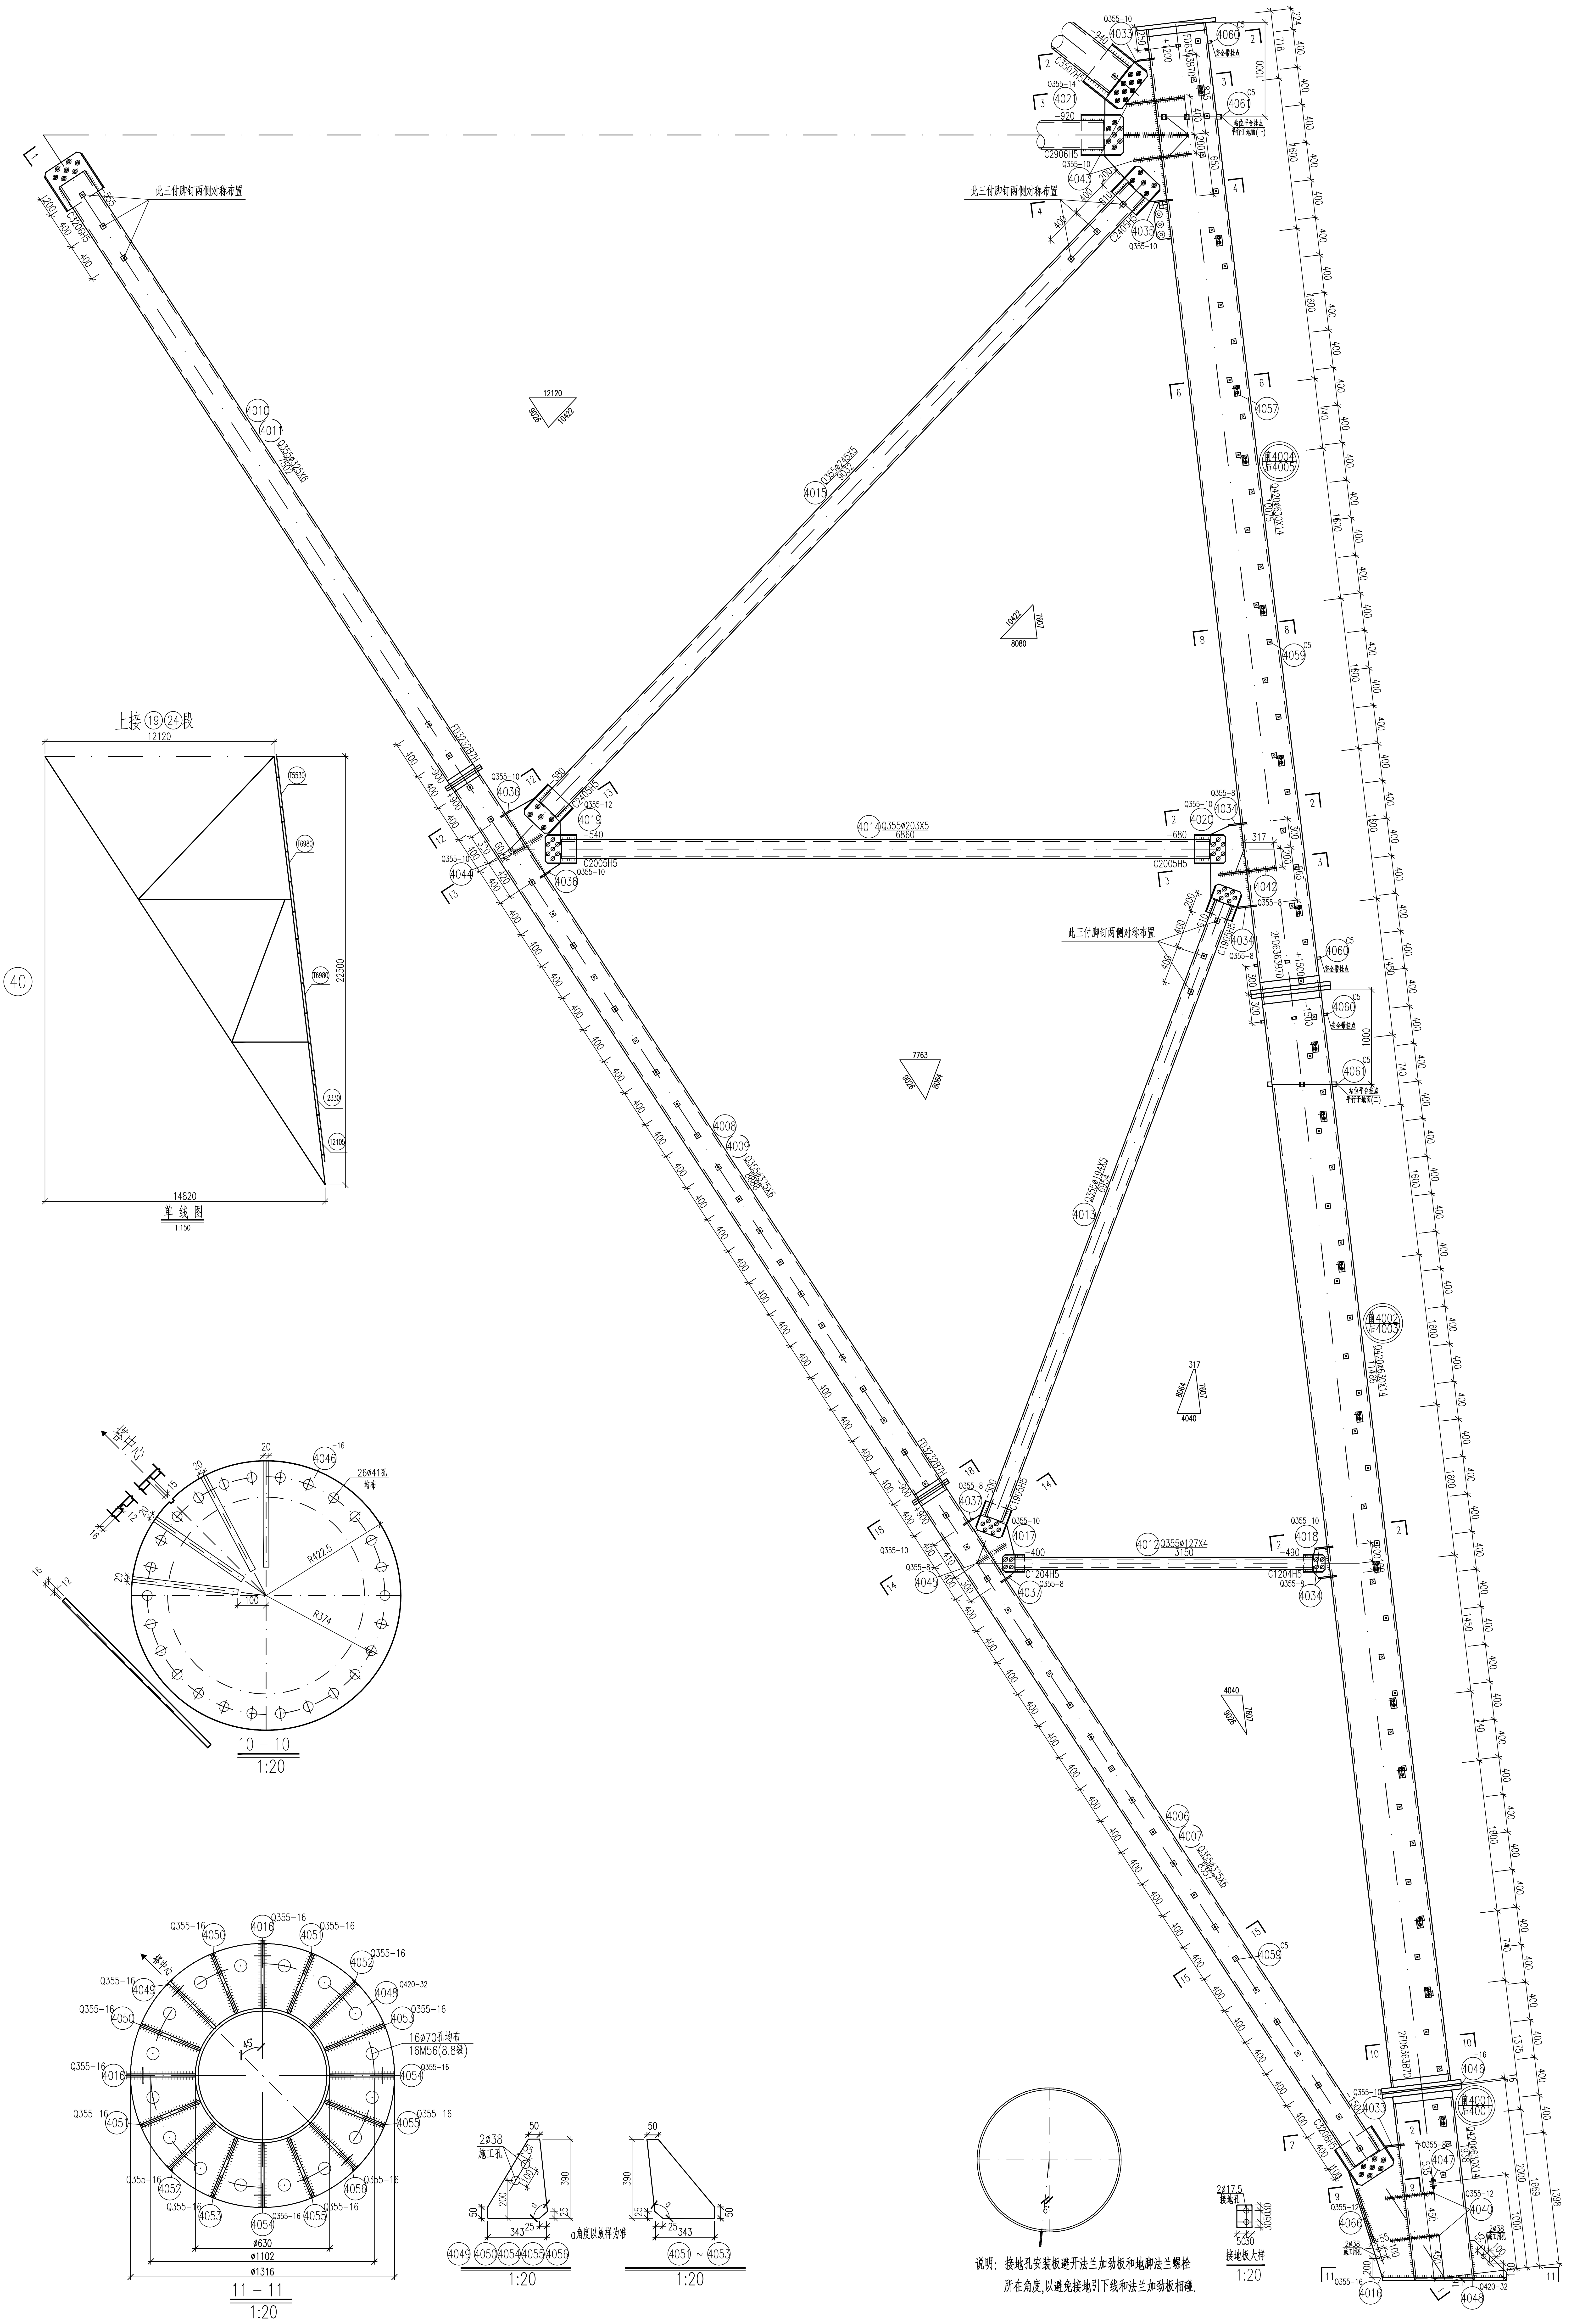

说明：接地孔安装板避开法兰加劲板和地脚法兰螺栓
所在角度,以避免接地引下线和法兰加劲板相碰.

山东电力工程咨询院有限公司

浙江特高压交流环网工程线路　工程　施工图　设计阶段

批　准	雷强	校　核	马一丹	SZK31102A双回路直线塔 102.0-0.0m塔腿结构图(1/3) 105.0-3.0m塔腿结构图(1/3)	㊵	
审　核	高锡鹏					
		设计/勘测	潘胜尧			
比　例		日　期	2026年 08月	图　号	37-SA36901S-T0121-090	版本

电气	赵庆周	2026.08
专业	会签	日期