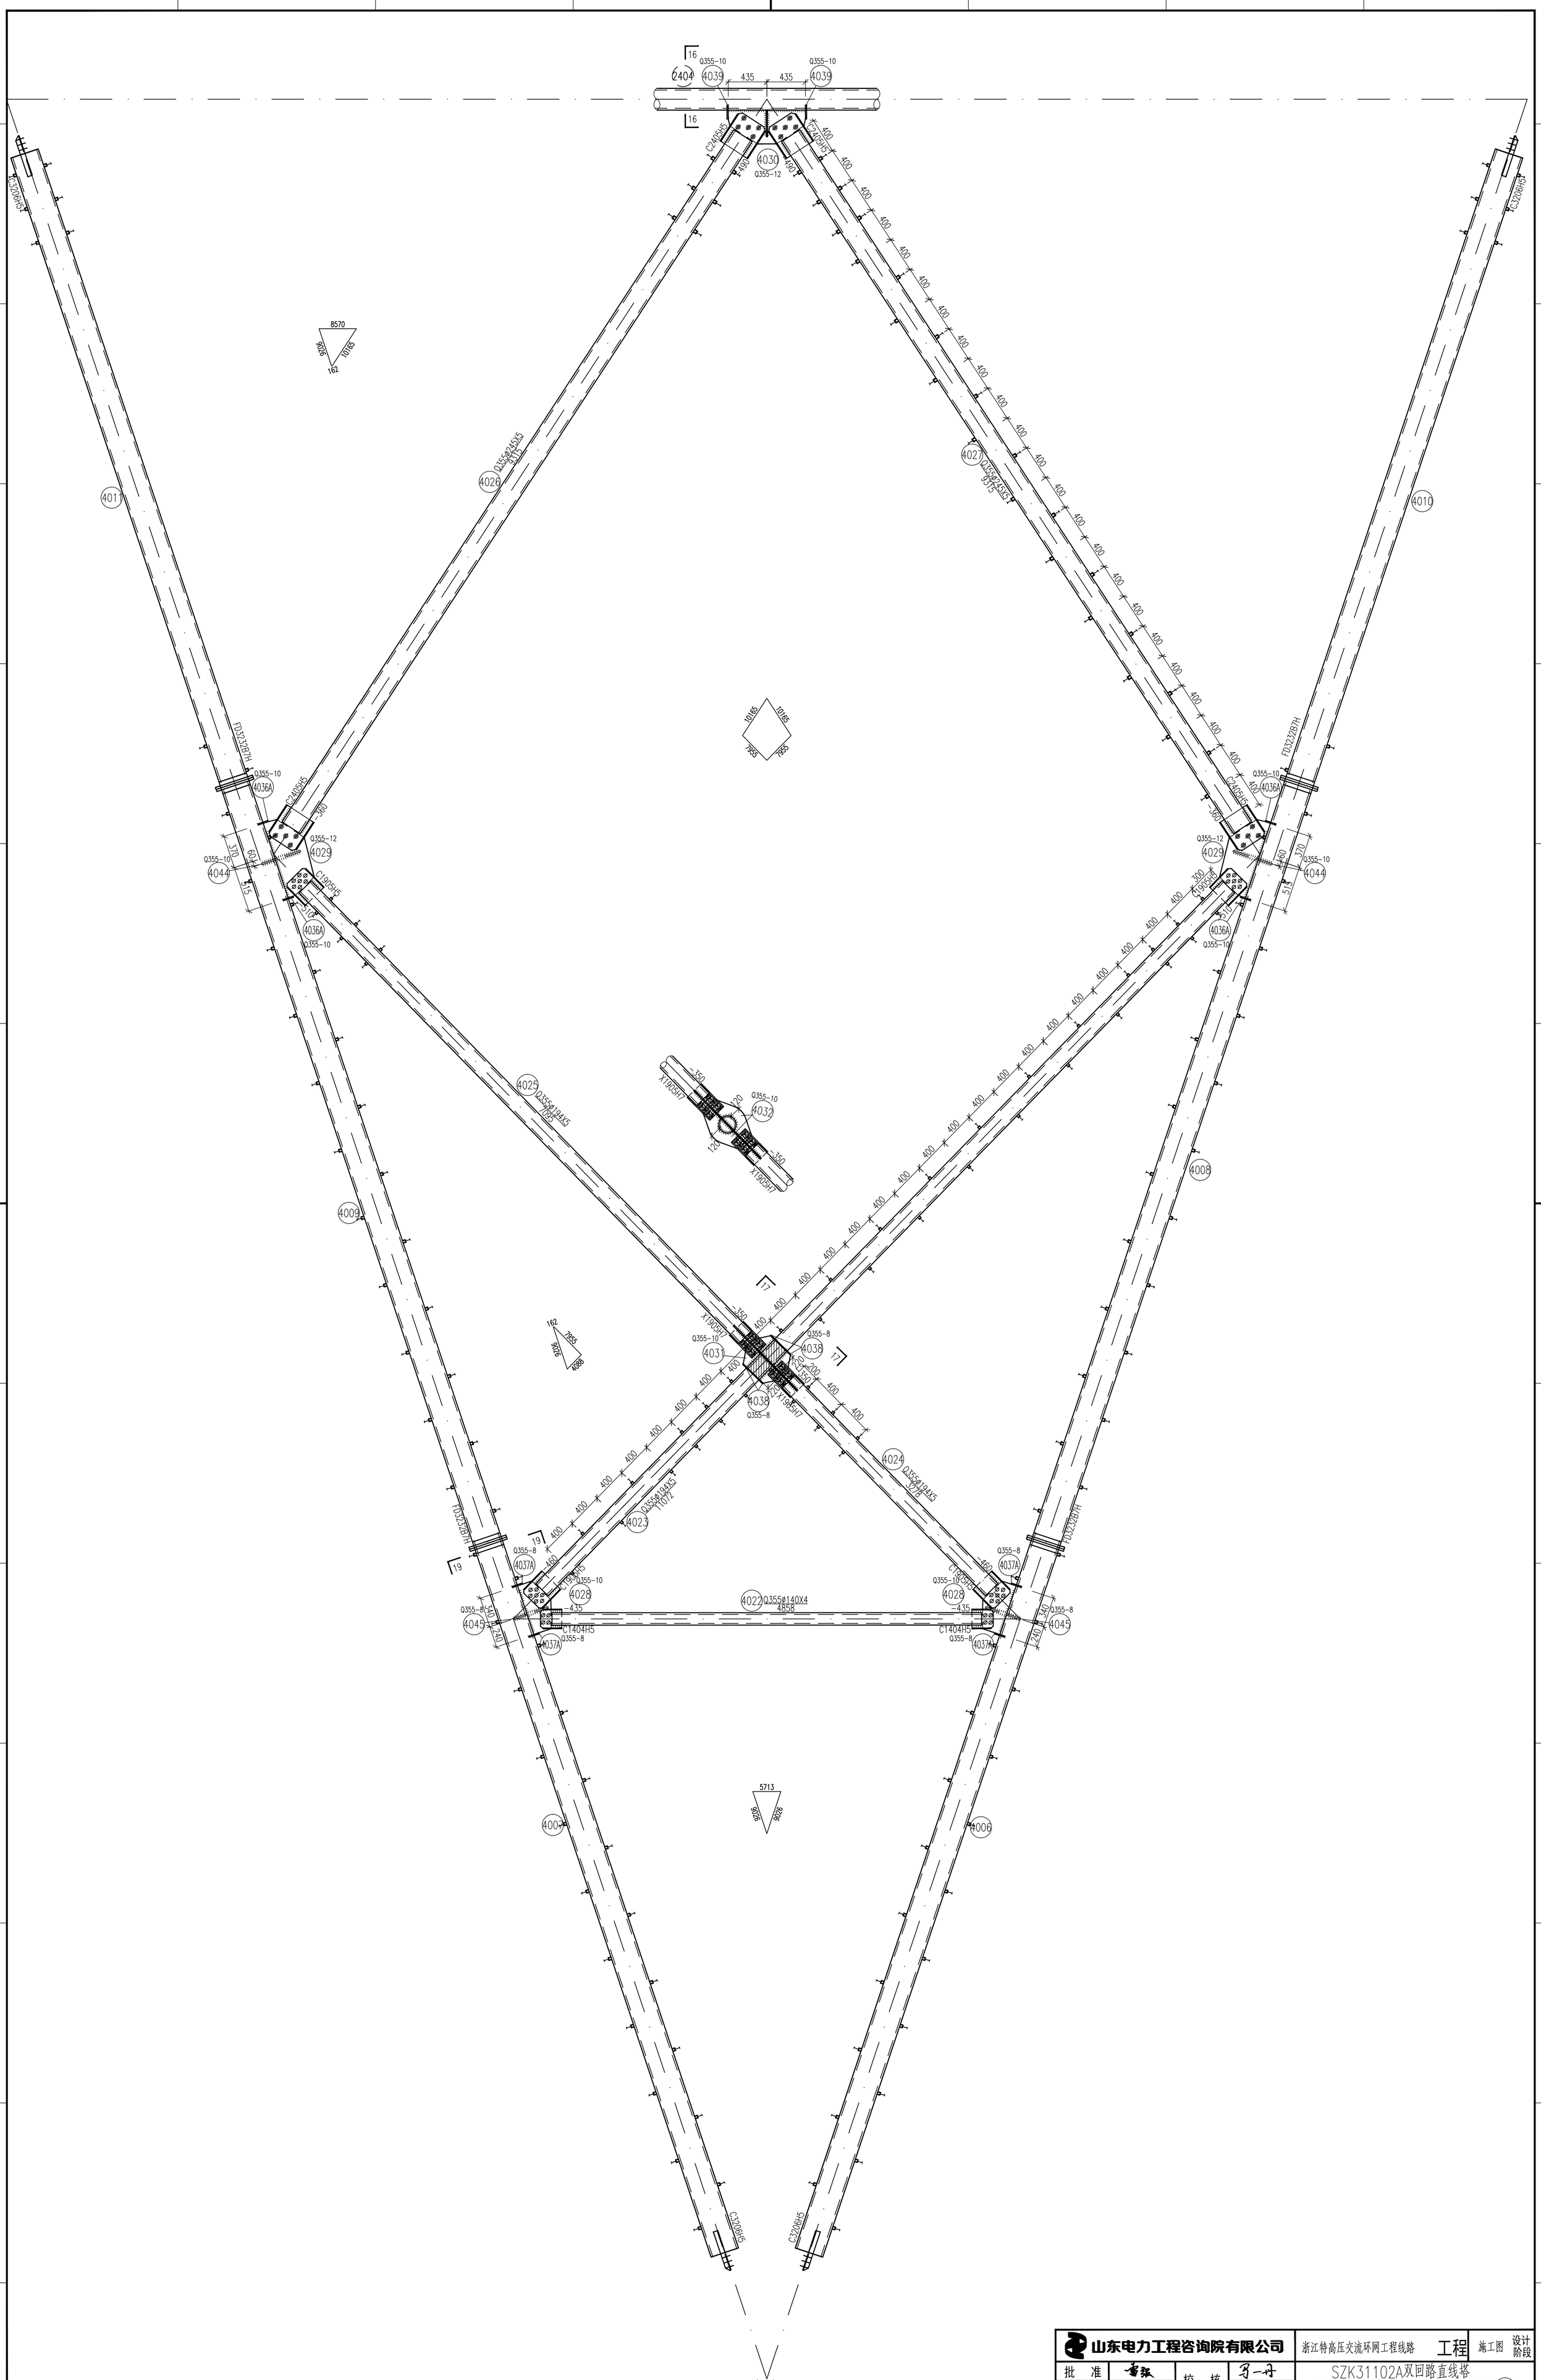



| | | | | | |
|---|---|---|---|---|---|
| 山东电力工程咨询院有限公司 | | | | 浙江特高压交流环网工程线路 工程 | 施工图 设计阶段 |
| 批 准 | 雷强 | 校 核 | 习一丹 | SZK31102A双回路直线塔<br>102.0-0.0m塔腿结构图(2/3)<br>105.0-3.0m塔腿结构图(2/3) | 40 |
| 审 核 | 高锡鹏 | | | | |
| | | 设计/勘测 | 潘世光 | | |
| 比 例 | | 日 期 | 2026年 08月 | 图 号 37-SA36901S-T0121-091 | 版本 |