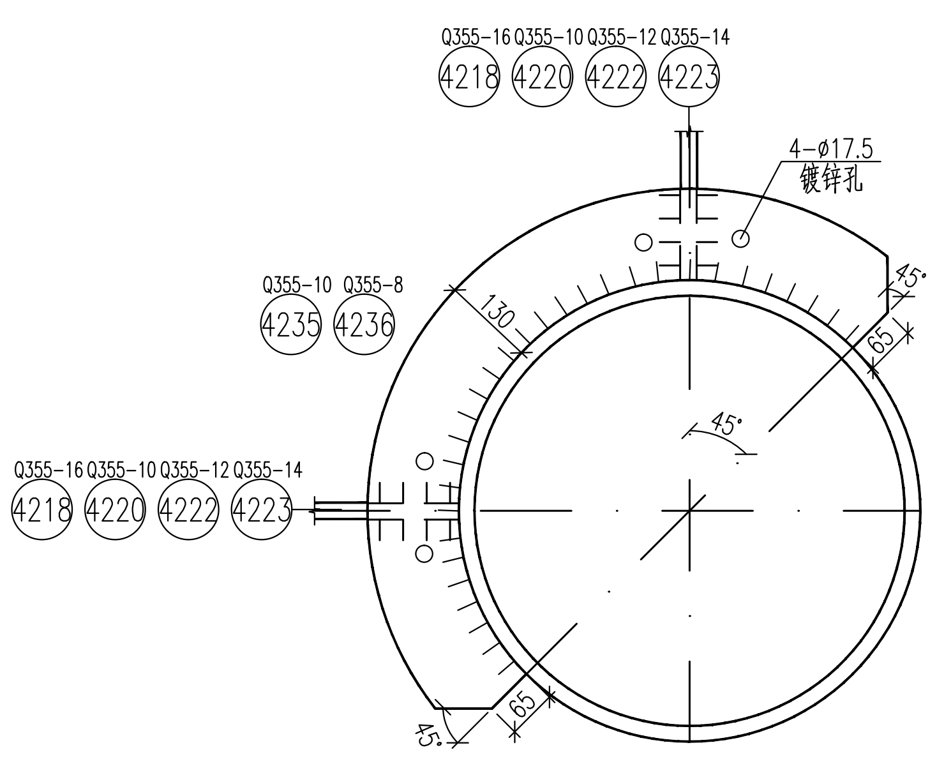

2－2
1:20

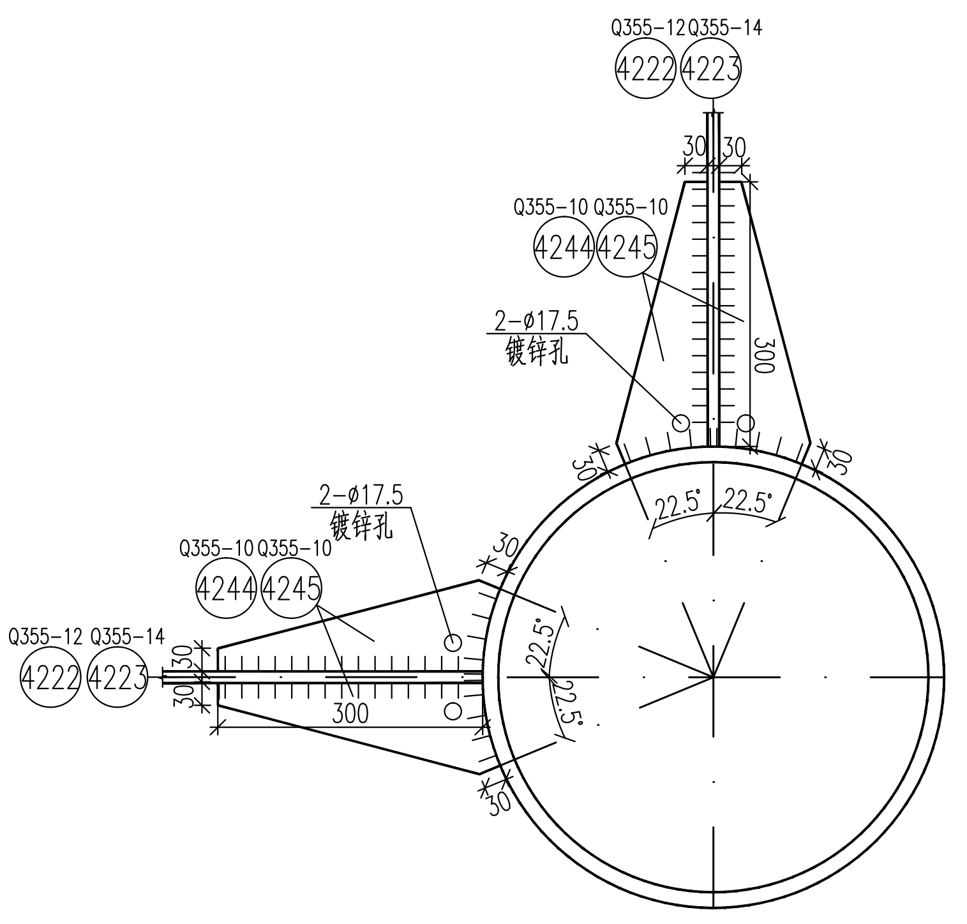

3－3
1:20

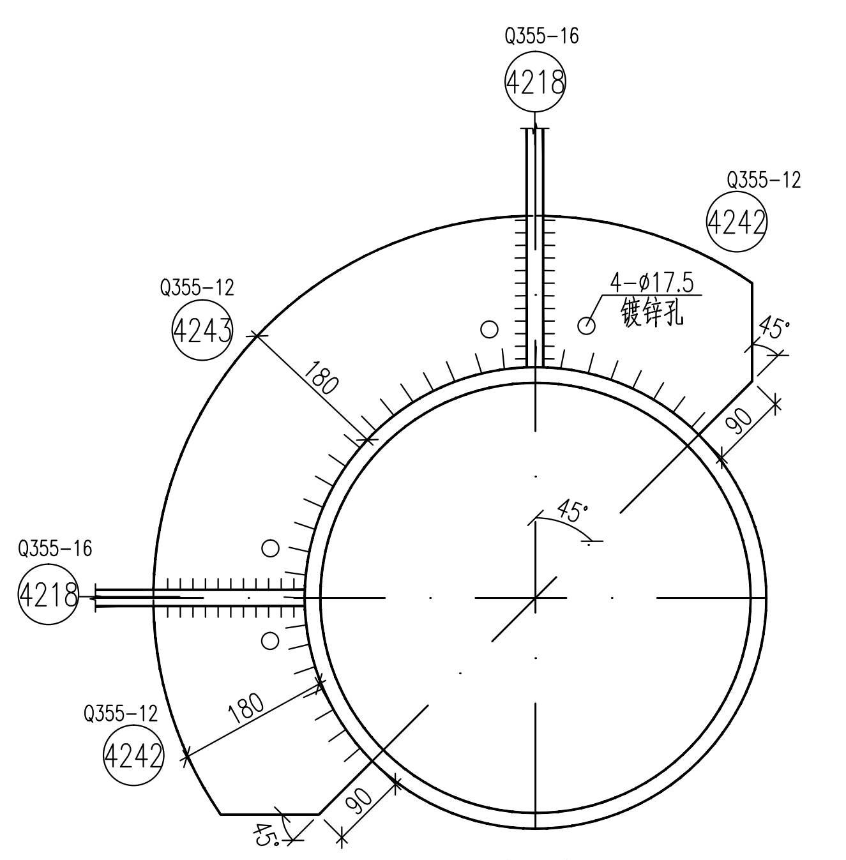

9－9
1:20

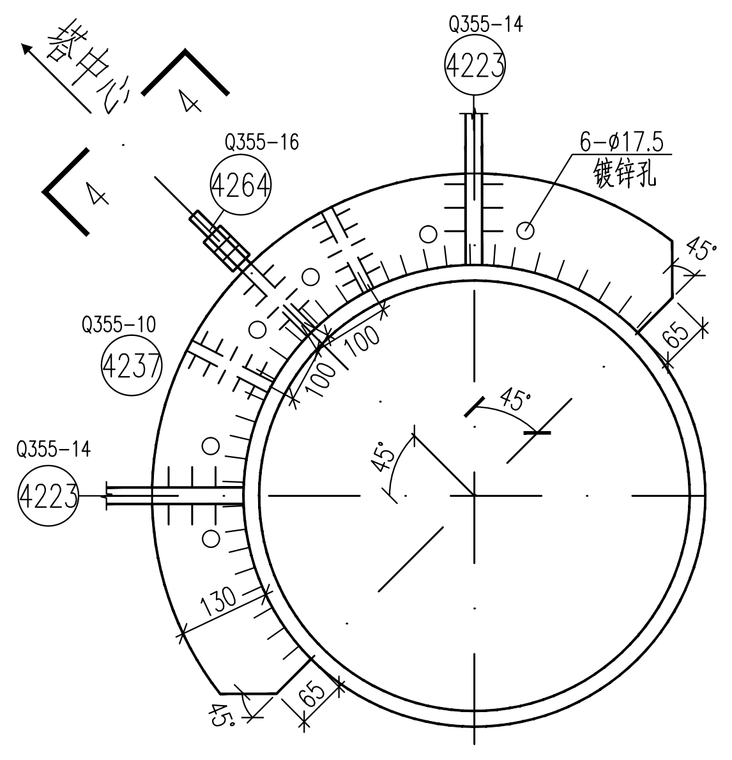

4－4
1:20

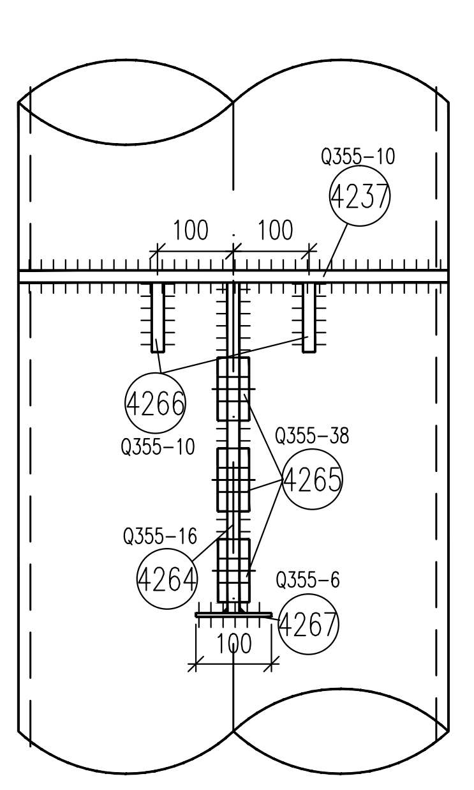

5－5
1:20

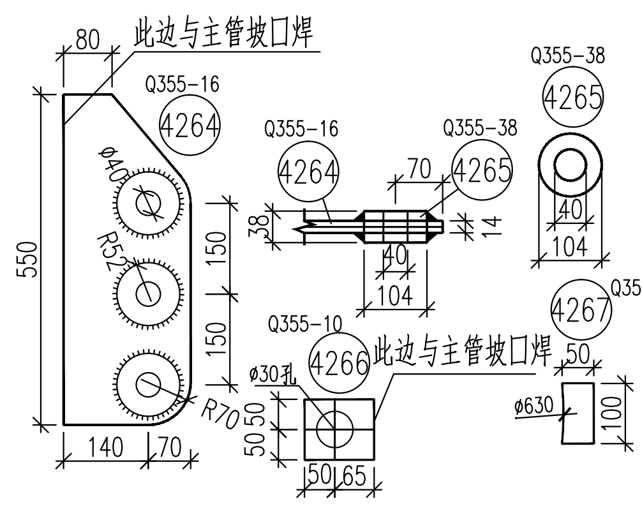

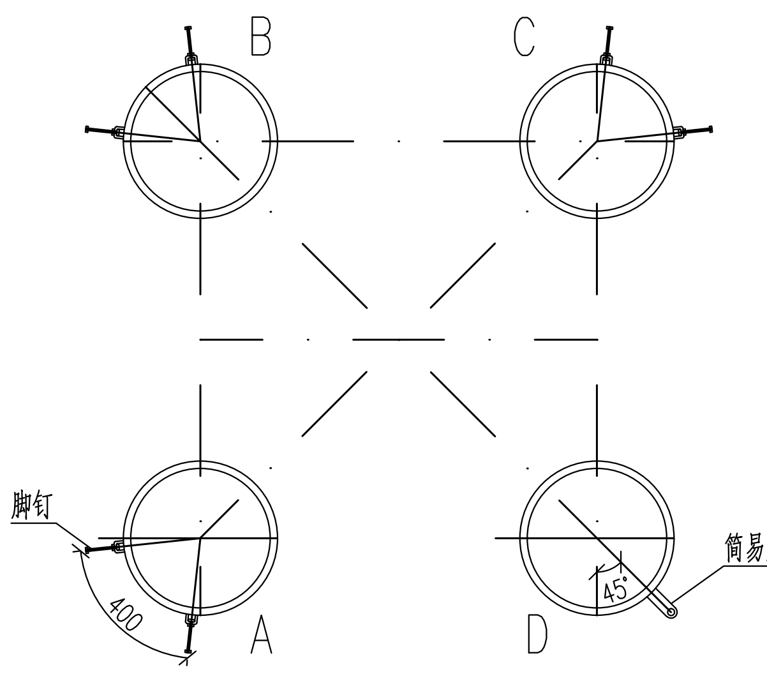

爬梯脚钉示意图

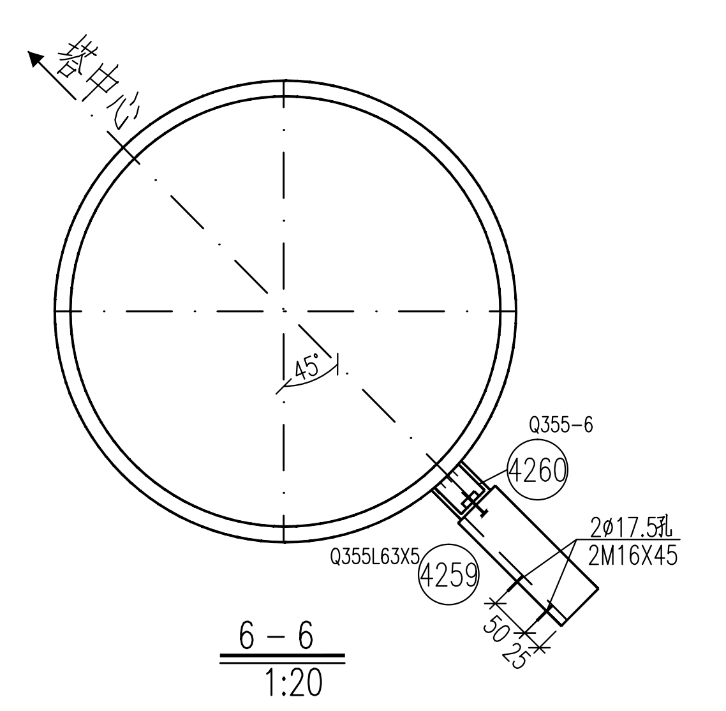

6－6
1:20

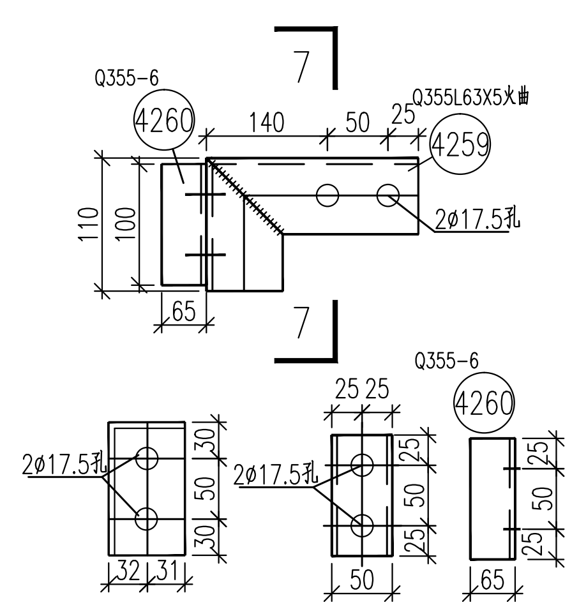

7－7
1:5

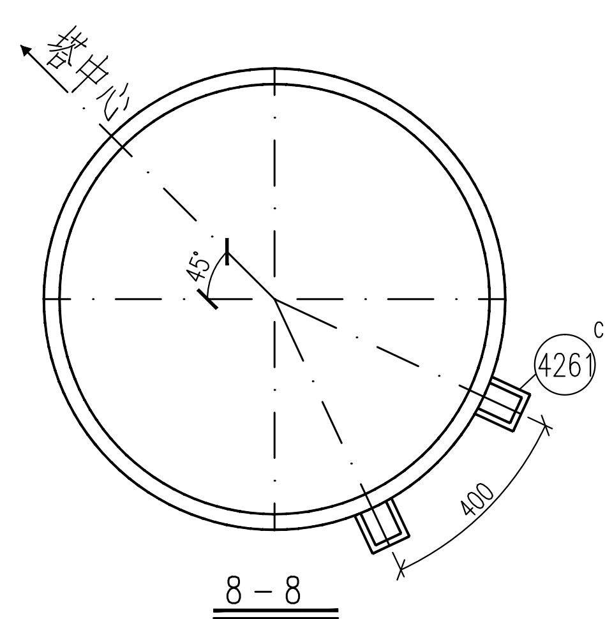

8－8
1:20

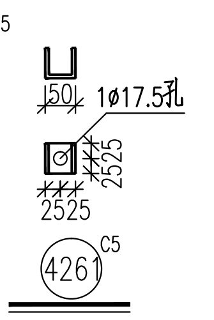

1:20

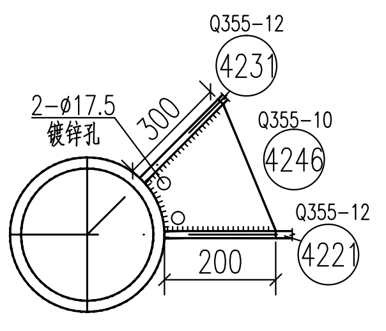

13－13
1:20

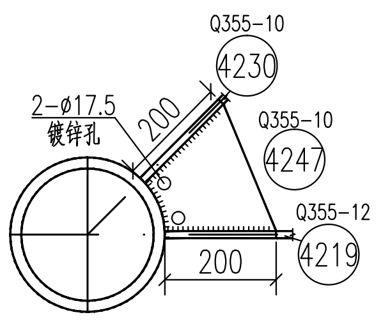

14－14
1:20

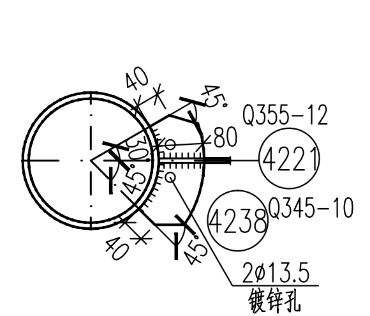

12－12
1:10

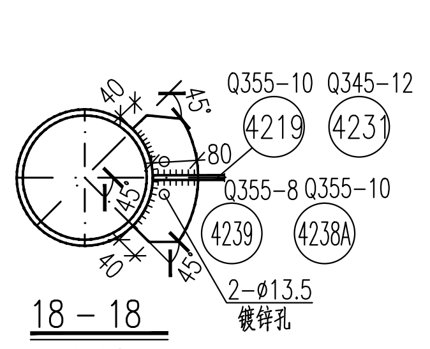

18－18
1:10

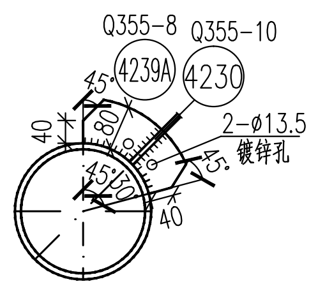

19－19
1:10

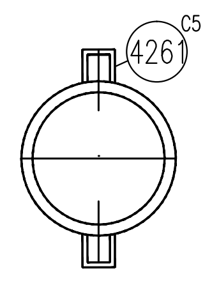

15－15
1:20

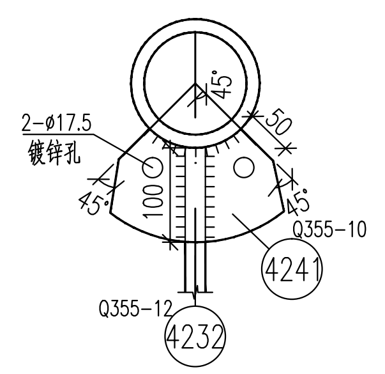

16－16
1:20

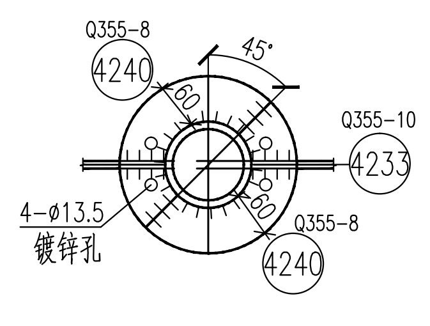

17－17
1:20

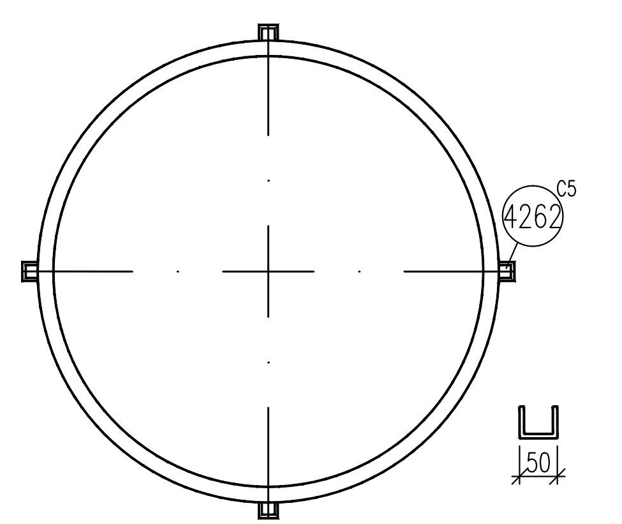

安全带挂点示意
扶手设置示意

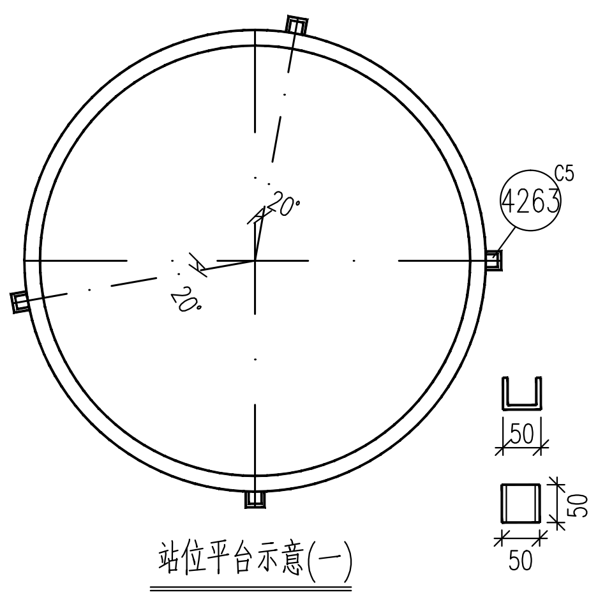

站位平台示意(一)

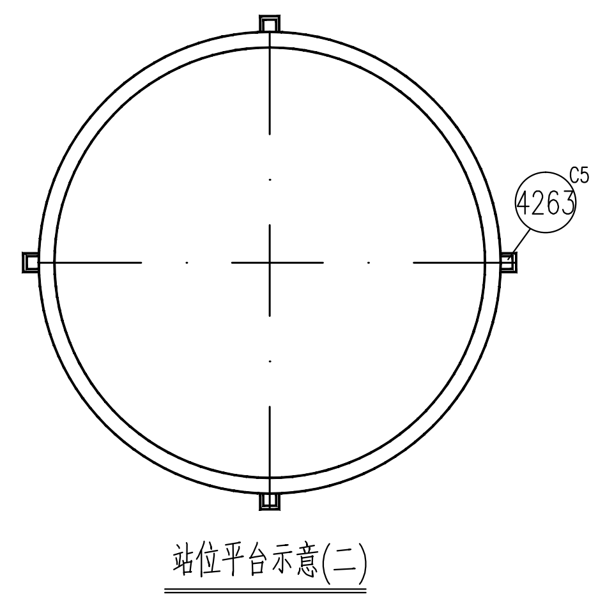

站位平台示意(二)

构 件 明 细 表

编号	规格	长度 (mm)	数量	重量(kg) 一件	重量(kg) 小计	备注
4201	Q420ø630X14	1938	1	412.18	412.2	一端切弧 带脚钉
4202	Q420ø630X14	7374	1	1568.31	1568.3	装爬梯
4203	Q420ø630X14	7374	0	1568.31	0.0	带脚钉
4204	Q420ø630X14	8390	1	1784.39	1784.4	装爬梯
4205	Q420ø630X14	8390	0	1784.39	0.0	带脚钉
4206	Q420ø630X14	8590	1	1826.93	1826.9	装爬梯
4207	Q420ø630X14	8590	0	1826.93	0.0	带脚钉
4208	Q355ø325X6	9096	1	429.35	429.4	带脚钉
4209	Q355ø325X6	9096	1	429.35	429.4	带脚钉
4210	Q355ø325X6	9807	1	462.91	462.9	带脚钉
4211	Q355ø325X6	9807	1	462.91	462.9	带脚钉
4212	Q355ø325X6	8446	1	398.67	398.7	带脚钉
4213	Q355ø325X6	8446	1	398.67	398.7	带脚钉
4214	Q355ø159X5	3070	2	58.30	116.6	
4215	Q355ø245X5	7623	2	225.59	451.2	带脚钉
4216	Q355ø203X5	6840	2	167.00	334.0	
4217	Q355ø273X5	9742	2	321.94	643.9	带脚钉
4218	Q355-16X625	1837	2	144.20	288.4	
4219	Q355-12X438	941	2	38.83	77.7	
4220	Q355-10X193	418	2	6.33	12.7	
4221	Q355-12X412	831	2	32.25	64.5	
4222	Q355-12X527	1128	2	56.00	112.0	
4223	Q355-14X655	1716	2	123.53	247.1	
4224	Q355ø140X4	4853	1	65.11	65.1	
4225	Q355ø194X5	11750	1	273.84	273.8	带脚钉
4226	Q355ø194X5	3507	1	81.73	81.7	带脚钉
4227	Q355ø194X5	7543	1	175.79	175.8	带脚钉
4228	Q355ø273X5	10088	1	333.37	333.4	带脚钉
4229	Q355ø273X5	10088	1	333.37	333.4	带脚钉
4230	Q355-10X336	655	2	17.28	34.6	
4231	Q355-12X382	1056	2	38.00	76.0	
4232	Q355-12X474	990	1	44.20	44.2	
4233	Q355-10X570	484	1	21.66	21.7	
4234	Q355-10X570	231	2	10.34	20.7	
4235	Q355-10X130	1313	4	13.40	53.6	
4236	Q355-8X130	1313	2	10.72	21.4	
4237	Q355-10X130	1313	1	13.40	13.4	
4238	Q355-10X65	224	4	1.14	4.6	
4238A	Q355-10X65	224	4	1.14	4.6	
4239	Q355-10X65	224	4	1.14	4.6	
4239A	Q355-10X65	224	4	1.14	4.6	
4240	Q355-8X60	439	4	1.65	6.6	
4241	Q355-10X100	298	2	2.34	4.7	
4242	Q355-12X180	306	4	5.19	20.8	
4243	Q355-12X180	613	2	10.39	20.8	
4244	Q355-10X300	201	4	4.73	18.9	
4245	Q355-10X300	201	8	4.73	37.8	
4246	Q355-10X200	330	2	5.18	10.4	
4247	Q355-10X200	220	2	3.45	6.9	
4248	-16X845	845	1	70.43	70.4	遮水板
4249	Q345-8X80	110	1	0.55	0.6	
4250	Q420-32X1316	1316	1	263.37	263.4	
4251	Q355-16X343	390	1	16.80	16.8	
4252	Q355-16X343	390	2	16.80	33.6	
4253	Q355-16X343	390	2	16.80	33.6	
4254	Q355-16X343	390	2	16.80	33.6	
4255	Q355-16X343	390	2	16.80	33.6	
4256	Q355-16X343	390	2	16.80	33.6	
4257	Q355-16X343	390	2	16.80	33.6	
4258	Q355-16X343	390	1	16.80	16.8	
4259	Q355L63X5	325	19	1.57	29.8	火曲（用于主材装爬梯）
4260	Q355-6X100	180	19	0.85	16.2	火曲（用于主材装爬梯）
4261	C5	50	215	0.27	58.1	槽钢（用于主材装爬梯）
4261	C5	50	279	0.27	75.3	槽钢（用于主材带脚钉）
4262	C5	25	24	0.14	3.4	槽钢
4263	C5	50	12	0.27	3.2	槽钢
4264	Q355-14X210	550	1	12.69	12.7	
4265	Q355-38X104	104	3	3.23	9.7	
4266	Q355-10X100	115	2	0.90	1.8	
4267	Q355-6X50	100	1	0.24	0.2	
4268	Q355-12X80	820	2	6.18	12.4	
	C1404H5		2	4.80	9.60	
	C1905H5		4	8.80	35.20	
	C2705H5		8	18.10	144.80	
	C1505H5		4	6.75	27.00	
	C2405H5		4	17.27	69.08	
	C2005H5		4	9.74	38.96	
	C3206H5		4	31.43	125.72	
	X1905H7		2	17.90	35.80	
	FD3232B7H		8	16.80	134.4	
	FD6363B7D		7	103.00	721.00	
	T3605	–	1	19.00	190.00	主材安装爬梯
	T3930	–	1	20.70	20.70	主材安装爬梯
	T5530	–	1	28.80	28.80	主材安装爬梯
	T6980	–	2	36.20	72.40	主材安装爬梯
合计		14245.9 kg(用于主材带脚钉)				
合计		14586.6 kg(用于主材装爬梯)				

螺栓、脚钉、垫圈明细表

名称	级别	规格	符号	数量	重量(kg)	备注
螺栓	6.8级	M16X45	⊘	76	12.8	用于主材装爬梯
		M16X65	⊗	32	6.4	
		M20X65	∅	84	29.6	
	8.8级	M24X75	⊘	116	68.8	
		M20X100	○	88	43.6	法兰螺栓
		M39X175	○	78	276.9	法兰螺栓
		M39X190	○	26	96.0	法兰螺栓
脚钉	6.8级	M16X185	⊖	215	89.1	用于主材装爬梯
		M16X185		279	115.7	用于主材带脚钉
垫圈	Q235		规格X个数			
合计			637.0 kg (用于主材带脚钉)			
合计			623.2 kg (用于主材装爬梯)			

说明：1.材料表为一个塔腿的重量。
2.本段塔腿为铁塔D腿，安装爬梯，当为A、B、C腿时需焊接脚钉连接槽钢。

山东电力工程咨询院有限公司				浙江特高压交流环网工程线路 工程	施工图 设计阶段
批准	雷强	校核	马一丹	SZK31102A双回路直线塔 105.0-0.0m塔腿结构图(3/3)	㊷
审核	高锡鹏				
		设计/勘测	潘旺光		
比例		日期	2026年 08月	图号 37-SA36901S-T0121-098	版本