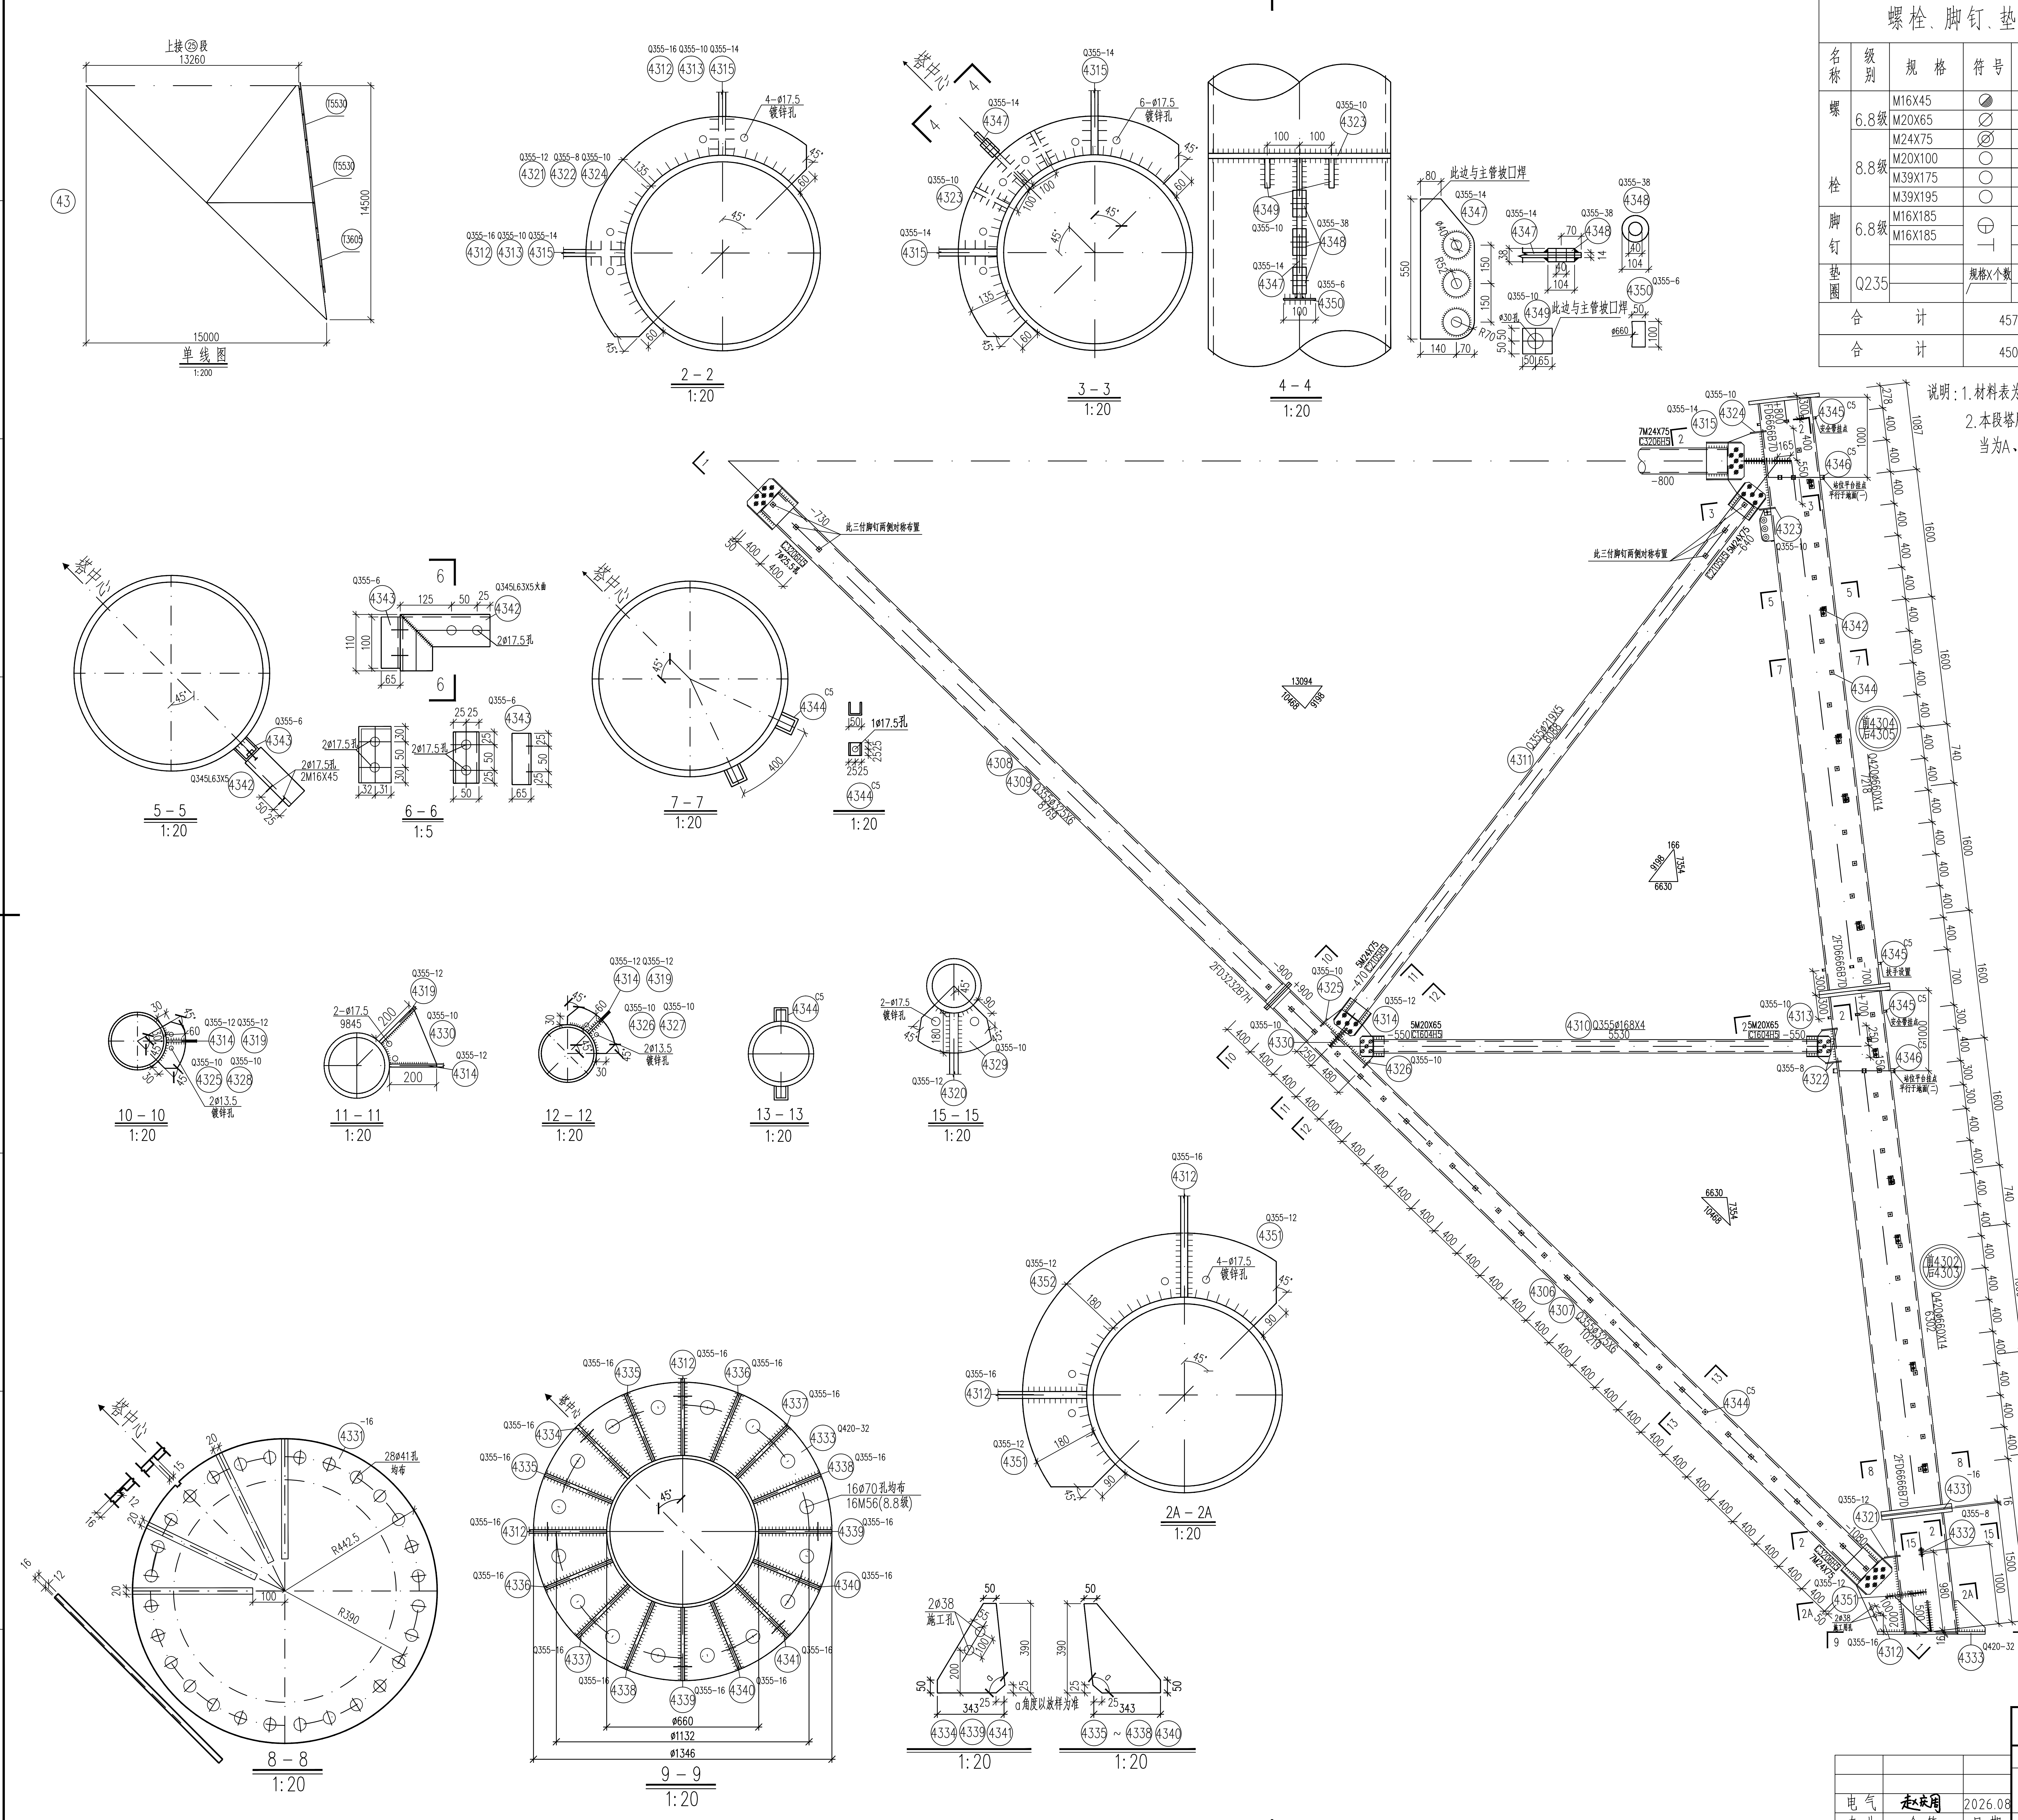

螺栓、脚钉、垫圈 明细表

名称	级别	规格	符号	数量	重量(kg)	备注
螺栓	6.8级	M16X45	◍	40	6.7	用于主材装爬梯
		M20X65	⊘	20	7.1	
	8.8级	M24X75	⊘	78	46.2	
		M20X100	○	44	21.8	法兰螺栓
		M39X175	○	56	198.9	法兰螺栓
		M39X195	○	28	104.7	法兰螺栓
脚钉	6.8级	M16X185	⊖	156	64.7	用于主材装爬梯
		M16X185		190	78.8	用于主材带脚钉
垫圈	Q235		规格X个数			
合计		457.5 kg (用于主材带脚钉)				
合计		450.1 kg (用于主材装爬梯)				

说明：1.材料表为一个塔腿的重量。

2.本段塔腿为铁塔D腿，安装爬梯，当为A、B、C腿时需焊接脚钉连接槽钢。

构 件 明 细 表

编号	规格	长度(mm)	数量	重量(kg) 一件	重量(kg) 小计	备注
4301	Q420ø660X14	1437	1	320.51	320.5	一端切弧 带脚钉
4302	Q420ø660X14	6302	1	1405.59	1405.6	装爬梯
4303	Q420ø660X14	6302	0	1405.59	0.0	带脚钉
4304	Q420ø660X14	7218	1	1609.89	1609.9	装爬梯
4305	Q420ø660X14	7218	0	1609.89	0.0	带脚钉
4306	Q355ø325X6	10219	1	482.36	482.4	带脚钉
4307	Q355ø325X6	10219	1	482.36	482.4	带脚钉
4308	Q355ø325X6	8769	1	413.92	413.9	带脚钉
4309	Q355ø325X6	8769	1	413.92	413.9	带脚钉
4310	Q355ø168X4	5530	2	89.46	178.9	
4311	Q355ø219X5	8088	2	213.42	426.8	带脚钉
4312	Q355－16X576	999	2	72.27	144.5	
4313	Q355－10X242	440	2	8.36	16.7	
4314	Q355－12X344	803	2	26.02	52.0	
4315	Q355－14X532	1045	2	49.90	99.8	
4316	Q355ø245X5	8376	1	247.88	247.9	
4317	Q355ø245X5	9420	1	278.77	278.8	带脚钉
4318	Q355ø245X5	9420	1	278.77	278.8	带脚钉
4319	Q355－12X399	952	2	35.78	71.6	
4320	Q355－12X398	935	1	35.05	35.0	
4321	Q355－12X135	1374	1	17.47	17.5	
4322	Q355－8X135	1374	2	11.65	23.3	
4323	Q355－10X135	1374	1	14.56	14.6	
4324	Q355－10X135	1374	1	14.56	14.6	
4325	Q355－10X70	285	2	1.57	3.1	
4326	Q355－10X70	341	2	1.87	3.7	
4327	Q355－10X70	341	2	1.87	3.7	
4328	Q355－10X70	285	2	1.57	3.1	
4329	Q355－10X180	392	2	5.54	11.1	
4330	Q355－10X200	205	2	3.22	6.4	
4331	－16X885	885	1	77.26	77.3	遮水板
4332	Q345－8X80	110	1	0.55	0.6	接地孔用
4333	Q420－32X1346	1346	1	271.50	271.5	
4334	Q355－16X343	390	1	16.80	16.8	
4335	Q355－16X343	390	2	16.80	33.6	
4336	Q355－16X343	390	2	16.80	33.6	
4337	Q355－16X343	390	2	16.80	33.6	
4338	Q355－16X343	390	2	16.80	33.6	
4339	Q355－16X343	390	2	16.80	33.6	
4340	Q355－16X343	390	2	16.80	33.6	
4341	Q355－16X343	390	1	16.80	16.8	
4342	Q345L63X5	310	10	1.49	14.9	火曲 (用于主材装爬梯)
4343	Q355－6X100	180	10	0.85	8.5	火曲 (用于主材装爬梯)
4344	C5	50	156	0.27	42.1	槽钢 (用于主材装爬梯)
4344	C5	50	190	0.27	51.3	槽钢 (用于主材带脚钉)
4345	C5	25	16	0.14	2.2	槽钢
4346	C5	50	8	0.27	2.2	槽钢
4347	Q355－14X210	550	1	12.69	12.7	
4348	Q355－38X104	104	3	3.23	9.7	
4349	Q355－10X100	115	2	0.90	1.8	
4350	Q355－6X50	100	1	0.24	0.2	
4351	Q355－12X180	330	2	5.60	11.2	
4352	Q355－12X180	660	1	11.19	11.2	
	C1604H5		4	7.12	28.5	
	C2105H5		4	14.54	58.2	
	C2405H5		6	17.27	103.6	
	C3206H5		4	31.43	125.7	
	FD3232B7H		4	16.80	67.2	
	FD6666B7D		5	116.50	582.5	
	T3605	–	1	19.00	19.0	主材安装爬梯
	T5530	–	2	28.80	57.6	主材安装爬梯
合计		8713.3 kg (用于主材带脚钉)				
合计		8804.1 kg (用于主材装爬梯)				

山东电力工程咨询院有限公司

			批准	雷强	校核	马一丹	浙江特高压交流环网工程线路 工程
			审核	高锡鹏			施工图 设计阶段
电气	赵庆周	2026.08			设计/勘测	潘胜光	SZK31102A双回路直线塔 108.0－4.5m塔腿结构图(1/2) ㊸
专业	会签	日期	比例	1:40	日期	2026年 08月	图号 37-SA36901S-T0121-099 版本