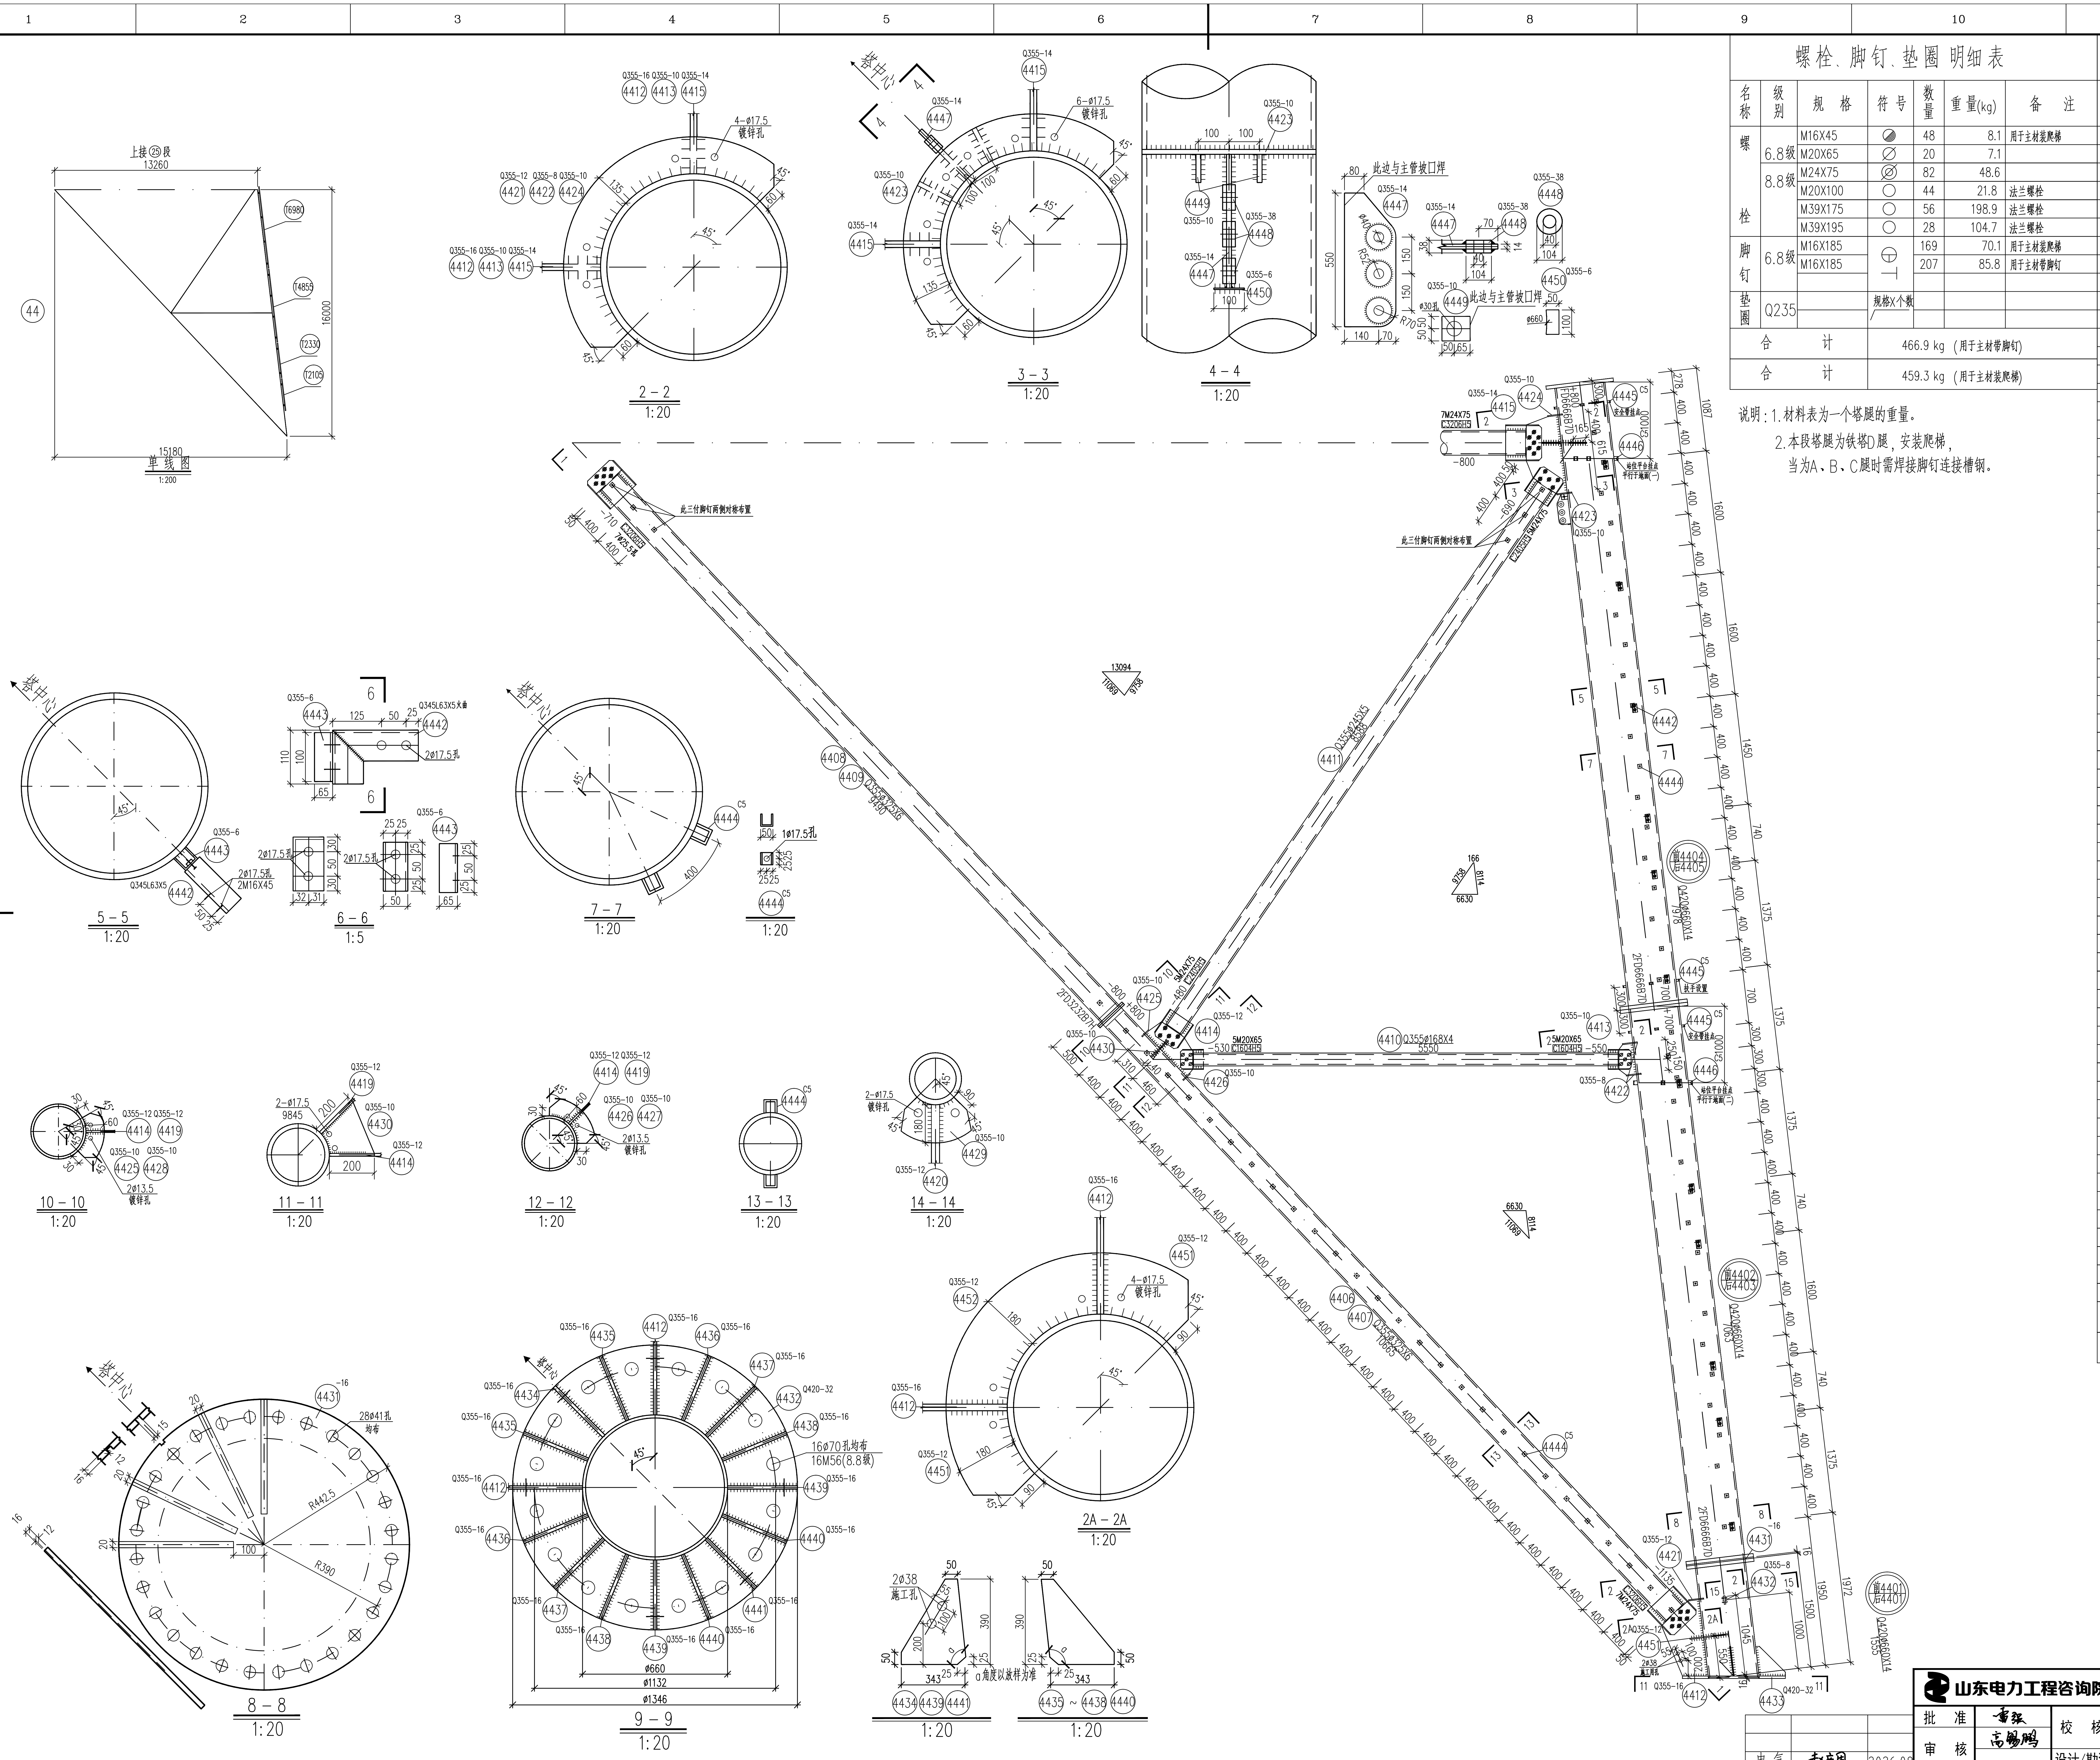

螺栓、脚钉、垫圈 明细表

名称	级别	规格	符号	数量	重量(kg)	备注
螺栓	6.8级	M16X45	◍	48	8.1	用于主材装爬梯
		M20X65	⊘	20	7.1	
	8.8级	M24X75	⊘	82	48.6	
		M20X100	○	44	21.8	法兰螺栓
		M39X175	○	56	198.9	法兰螺栓
		M39X195	○	28	104.7	法兰螺栓
脚钉	6.8级	M16X185		169	70.1	用于主材装爬梯
		M16X185		207	85.8	用于主材带脚钉
垫圈	Q235		规格X个数			
合计			466.9 kg (用于主材带脚钉)			
合计			459.3 kg (用于主材装爬梯)			

说明：1.材料表为一个塔腿的重量。

2.本段塔腿为铁塔D腿，安装爬梯，当为A、B、C腿时需焊接脚钉连接槽钢。

构 件 明 细 表

编号	规格	长度(mm)	数量	重量(kg) 一件	重量(kg) 小计	备注
4401	Q420ø660X14	1555	1	346.83	346.8	一端切弧 带脚钉
4402	Q420ø660X14	7063	1	1575.32	1575.3	装爬梯
4403	Q420ø660X14	7063	0	1575.32	0.0	带脚钉
4404	Q420ø660X14	7978	1	1779.40	1779.4	装爬梯
4405	Q420ø660X14	7978	0	1779.40	0.0	带脚钉
4406	Q355ø325X6	10665	1	503.41	503.4	带脚钉
4407	Q355ø325X6	10665	1	503.41	503.4	带脚钉
4408	Q355ø325X6	9490	1	447.95	448.0	带脚钉
4409	Q355ø325X6	9490	1	447.95	448.0	带脚钉
4410	Q355ø168X4	5550	2	89.79	179.6	
4411	Q355ø245X5	8588	2	254.15	508.3	带脚钉
4412	Q355－16X578	1071	2	77.75	155.5	
4413	Q355－10X242	440	2	8.36	16.7	
4414	Q355－12X359	847	2	28.64	57.3	
4415	Q355－14X532	1117	2	54.10	108.2	
4416	Q355ø245X5	8396	1	248.47	248.5	
4417	Q355ø273X5	10002	1	330.53	330.5	带脚钉
4418	Q355ø273X5	10002	1	330.53	330.5	带脚钉
4419	Q355－12X396	979	2	36.52	73.0	
4420	Q355－12X428	946	1	38.14	38.1	
4421	Q355－12X135	1374	1	17.47	17.5	
4422	Q355－8X135	1374	2	11.65	23.3	
4423	Q355－10X135	1374	1	14.56	14.6	
4424	Q355－10X135	1374	1	14.56	14.6	
4425	Q355－10X70	285	2	1.57	3.1	
4426	Q355－10X70	341	2	1.87	3.7	
4427	Q355－10X70	341	2	1.87	3.7	
4428	Q355－10X70	285	2	1.57	3.1	
4429	Q355－10X180	392	2	5.54	11.1	
4430	Q355－10X200	205	2	3.22	6.4	
4431	－16X885	885	1	77.26	77.3	遮水板
4432	Q345－8X80	110	1	0.55	0.6	接地孔用
4433	Q420－32X1346	1346	1	271.50	271.5	
4434	Q355－16X343	390	1	16.80	16.8	
4435	Q355－16X343	390	2	16.80	33.6	
4436	Q355－16X343	390	2	16.80	33.6	
4437	Q355－16X343	390	2	16.80	33.6	
4438	Q355－16X343	390	2	16.80	33.6	
4439	Q355－16X343	390	2	16.80	33.6	
4440	Q355－16X343	390	2	16.80	33.6	
4441	Q355－16X343	390	1	16.80	16.8	
4442	Q345L63X5	310	12	1.49	17.9	火曲（用于主材装爬梯）
4443	Q355－6X100	180	12	0.85	10.2	火曲（用于主材装爬梯）
4444	C5	50	169	0.27	45.6	槽钢（用于主材装爬梯）
4444	C5	50	207	0.27	55.9	槽钢（用于主材带脚钉）
4445	C5	25	20	0.14	2.8	槽钢
4446	C5	50	12	0.27	3.2	槽钢
4447	Q355－14X210	550	1	12.69	12.7	
4448	Q355－38X104	104	3	3.23	9.7	
4449	Q355－10X100	115	2	0.90	1.8	
4450	Q355－6X50	100	1	0.24	0.2	
4451	Q355－12X180	330	2	5.60	11.2	
4452	Q355－12X180	660	1	11.19	11.2	
	C1604H5		4	6.41	25.6	
	C2405H5		6	17.27	103.6	
	C2705H5		4	18.10	72.4	
	C3206H5		4	31.43	125.7	
	FD3232B7H		4	16.80	67.2	
	FD6666B7D		5	116.50	582.5	
	T2105	－	1	11.50	11.5	主材安装爬梯
	T2330	－	1	12.40	12.4	主材安装爬梯
	T4855	－	1	25.00	25.0	主材安装爬梯
	T6980	－	1	36.20	36.2	主材安装爬梯
合计		9421.9 kg (用于主材带脚钉)				
合计		9524.8 kg (用于主材装爬梯)				

			山东电力工程咨询院有限公司				浙江特高压交流环网工程线路 工程	施工图 设计阶段
			批准	雷强	校核	马一丹	SZK31102A双回路直线塔 108.0－3.0m塔腿结构图(1/2)	44
电气	赵庆周	2026.08	审核	高锡鹏	设计/勘测	潘旭光		
专业	会签	日期	比例	1:40	日期	2026年 08月	图号 37－SA36901S－T0121－101	版本