



爬梯脚钉示意图

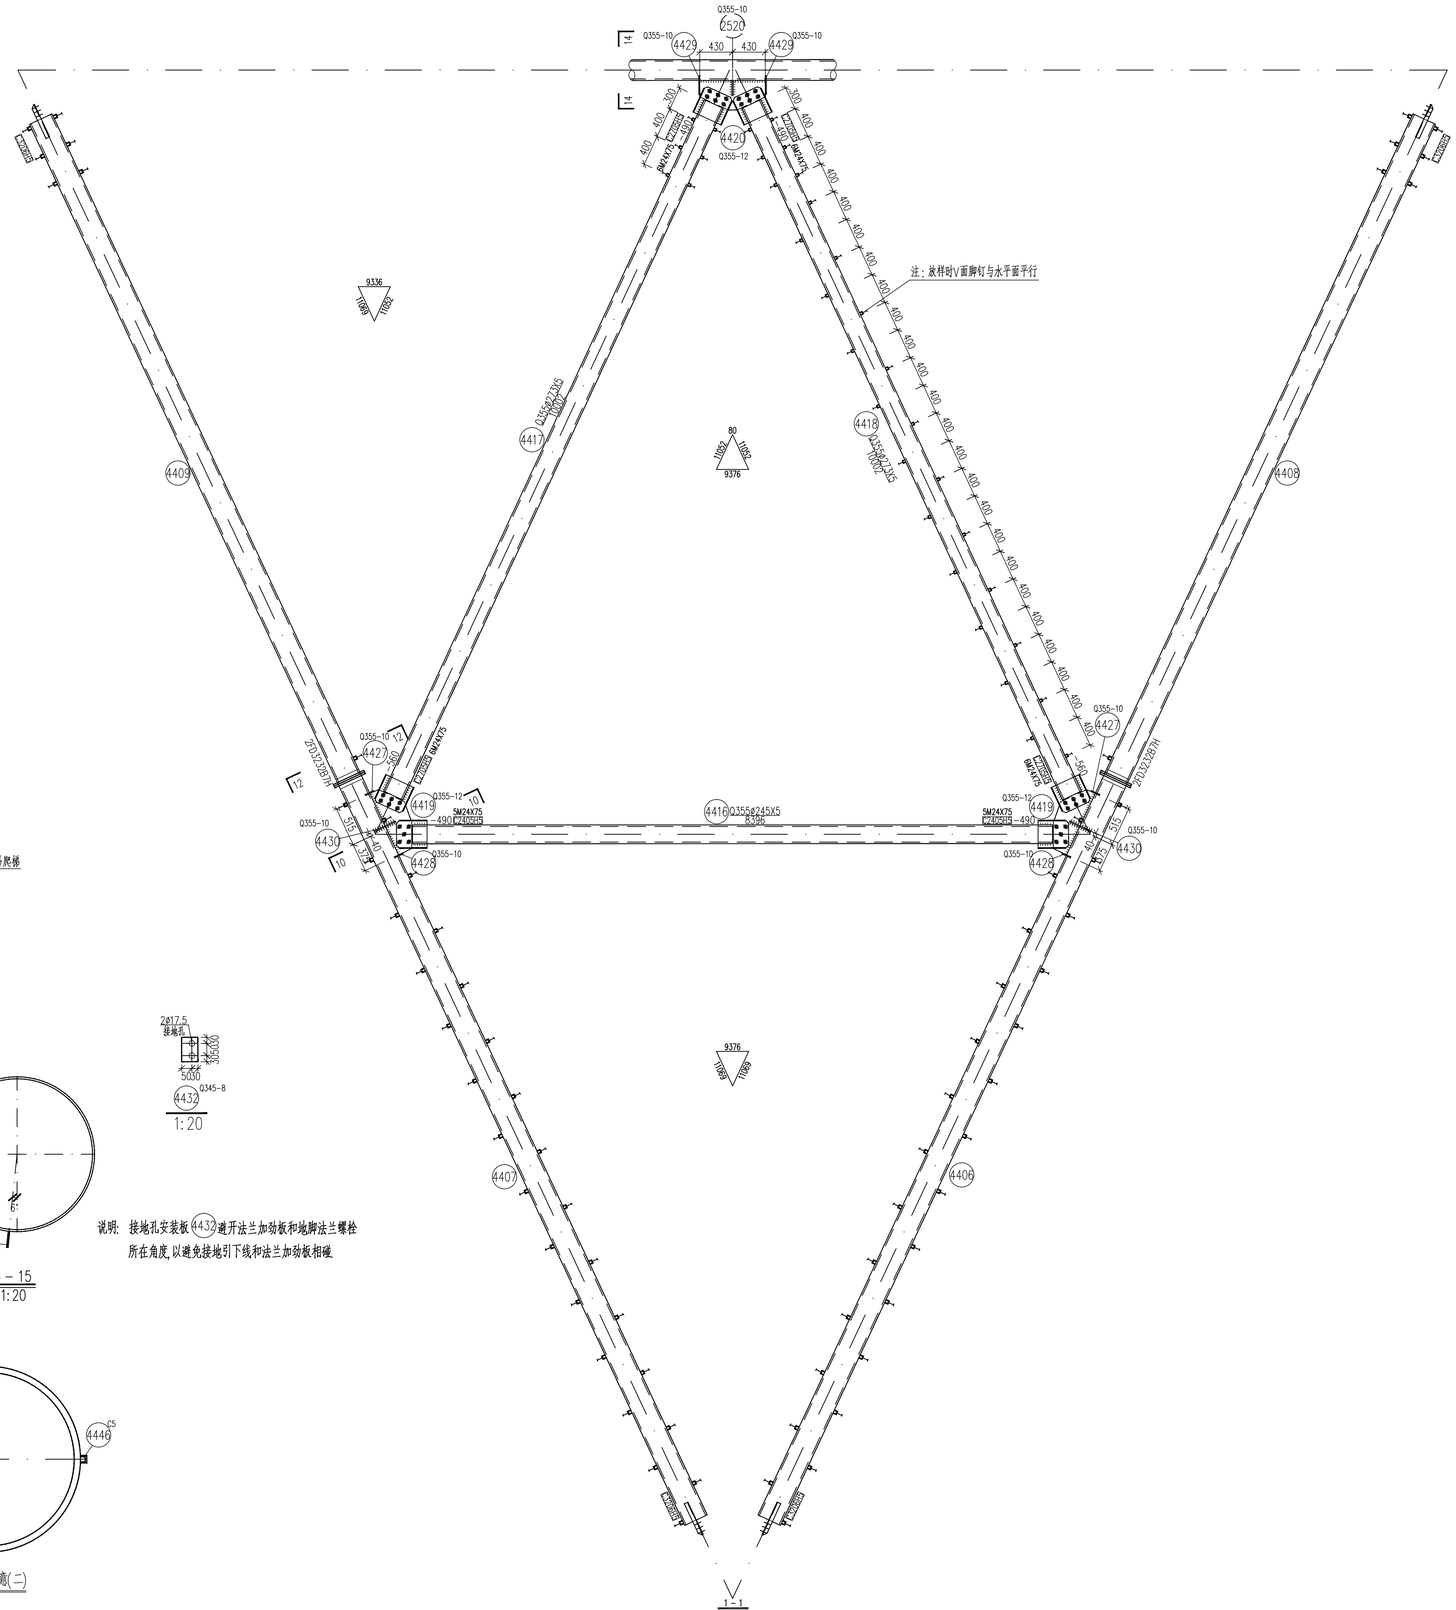


1:20

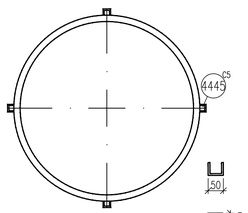

安全带挂点示意


扶手设置示意

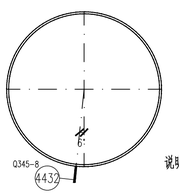


15 - 15

1:20

说明：接地孔安装板(4432)避开法兰加劲板和地脚法兰螺栓所在角度，以避免接地引下线和法兰加劲板相碰

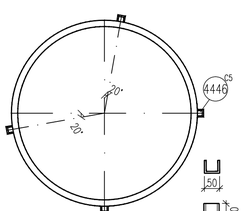

站位平台示意(一)

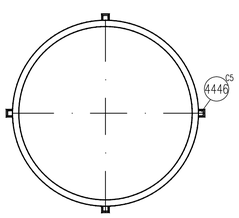

站位平台示意(二)

山东电力工程咨询院有限公司				浙江特高压交流环网工程线路 工程	施工图 设计阶段
批 准		校 核		SZK31102A双回路直线塔 108.0-3.0m塔腿结构图(2/2) (44)	
审 核		设计/勘测			
比 例	1:40	日 期	2026年 08月	图 号 37-SA36901S-T0121-102	版本