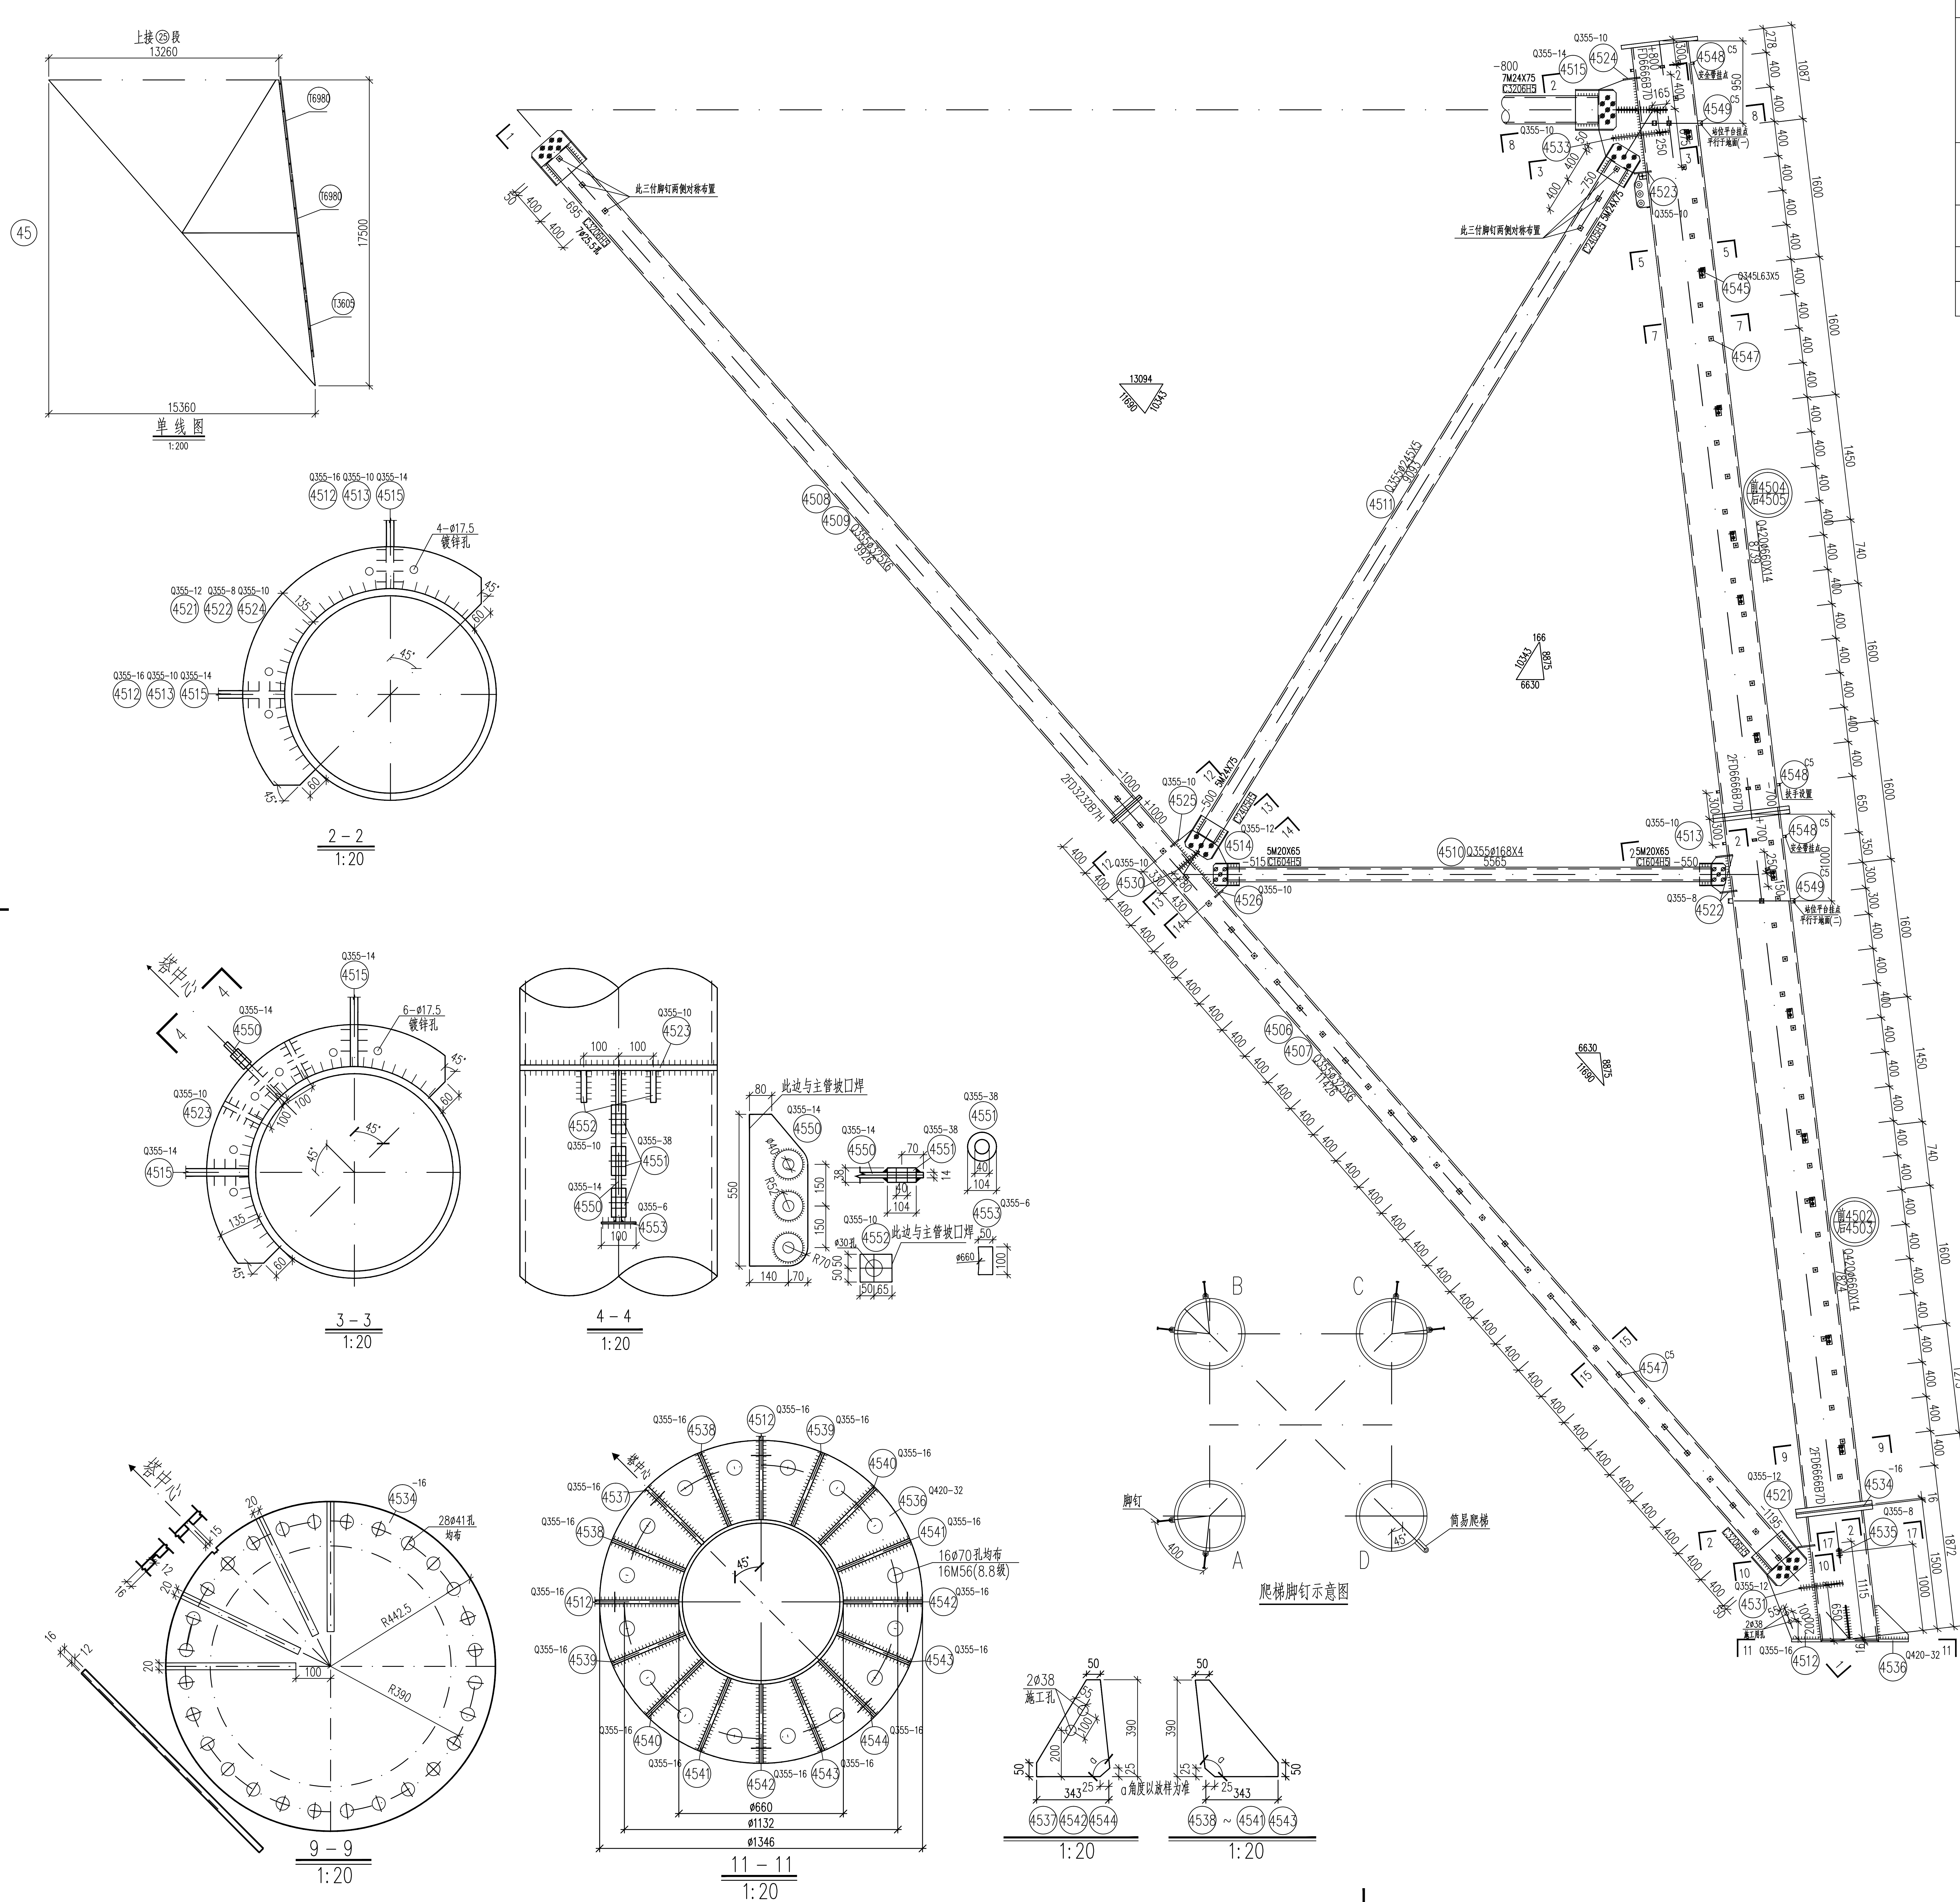

单线图
1:200

2－2
1:20

3－3
1:20

4－4
1:20

9－9
1:20

11－11
1:20

爬梯脚钉示意图

4537 4542 4544
1:20

4538 ~ 4541 4543
1:20

螺栓、脚钉、垫圈 明细表

名称	级别	规格	符号	数量	重量(kg)	备注
螺栓	6.8级	M16X45	◎	48	8.1	用于主材装爬梯
		M20X65	⌀	20	7.1	
	8.8级	M24X75	⊘	82	48.6	
		M20X100	○	44	21.8	法兰螺栓
		M39X175	○	56	198.9	法兰螺栓
		M39X195	○	28	104.7	法兰螺栓
脚钉	6.8级	M16X185	⊖	179	74.2	用于主材装爬梯
		M16X185		221	91.6	用于主材带脚钉
垫圈	Q235		规格X个数			
合计			472.7 kg (用于主材带脚钉)			
合计			463.4 kg (用于主材装爬梯)			

说明：1.材料表为一个塔腿的重量。

2.本段塔腿为铁塔D腿，安装爬梯，

当为A、B、C腿时需焊接脚钉连接槽钢。

构 件 明 细 表

编号	规格	长度 (mm)	数量	重量 (kg) 一件	重量 (kg) 小计	备注
4501	Q420ø660X14	1437	1	320.51	320.5	一端切弧 带脚钉
4502	Q420ø660X14	7824	1	1745.05	1745.0	装爬梯
4503	Q420ø660X14	7824	0	1745.05	0.0	带脚钉
4504	Q420ø660X14	8739	1	1949.13	1949.1	装爬梯
4505	Q420ø660X14	8739	0	1949.13	0.0	带脚钉
4506	Q355ø325X6	11426	1	539.33	539.3	带脚钉
4507	Q355ø325X6	11426	1	539.33	539.3	带脚钉
4508	Q355ø325X6	9926	1	468.53	468.5	带脚钉
4509	Q355ø325X6	9926	1	468.53	468.5	带脚钉
4510	Q355ø168X4	5565	2	90.03	180.1	
4511	Q355ø245X5	9093	2	269.10	538.2	带脚钉
4512	Q355-16X582	1147	2	83.84	167.7	
4513	Q355-10X242	440	2	8.36	16.7	
4514	Q355-12X391	836	2	30.79	61.6	
4515	Q355-14X532	1183	2	69.17	138.3	
4516	Q355ø245X5	8396	1	248.47	248.5	
4517	Q355ø273X5	10554	1	348.77	348.8	带脚钉
4518	Q355ø273X5	10554	1	348.77	348.8	带脚钉
4519	Q355-12X416	1007	2	39.46	78.9	
4520	Q355-12X462	968	1	42.13	42.1	
4521	Q355-12X135	1374	1	17.47	17.5	
4522	Q355-8X135	1374	2	11.65	23.3	
4523	Q355-10X135	1374	1	14.56	14.6	
4524	Q355-10X135	1374	1	14.56	14.6	
4525	Q355-10X70	285	2	1.57	3.1	
4526	Q355-10X70	341	2	1.87	3.7	
4527	Q355-10X70	341	2	1.87	3.7	
4528	Q355-10X70	285	2	1.57	3.1	
4529	Q355-10X200	408	2	6.41	12.8	
4530	Q355-10X200	205	2	3.22	6.4	
4531	Q355-12X180	330	2	5.60	11.2	
4532	Q355-12X180	660	1	11.19	11.2	
4533	Q355-10X284	495	4	11.04	44.2	
4534	-16X885	885	1	77.26	77.3	遮水板
4535	Q345-8X80	110	1	0.55	0.6	接地孔用
4536	Q420-32X1346	1346	1	271.50	271.5	
4537	Q355-16X343	390	1	16.80	16.8	
4538	Q355-16X343	390	2	16.80	33.6	
4539	Q355-16X343	390	2	16.80	33.6	
4540	Q355-16X343	390	2	16.80	33.6	
4541	Q355-16X343	390	2	16.80	33.6	
4542	Q355-16X343	390	2	16.80	33.6	
4543	Q355-16X343	390	2	16.80	33.6	
4544	Q355-16X343	390	1	16.80	16.8	
4545	Q345L63X5	310	12	1.49	17.9	火曲 (用于主材装爬梯)
4546	Q355-6X100	180	12	0.85	10.2	火曲 (用于主材装爬梯)
4547	C5	50	179	0.27	48.3	槽钢 (用于主材装爬梯)
4547	C5	50	221	0.27	59.7	槽钢 (用于主材带脚钉)
4548	C5	25	20	0.14	2.8	槽钢
4549	C5	50	12	0.27	3.2	槽钢
4550	Q355-14X210	550	1	12.69	12.7	
4551	Q355-38X104	104	3	3.23	9.7	
4552	Q355-10X100	115	2	0.90	1.8	
4553	Q355-6X50	100	1	0.24	0.2	
	C1604H5		4	7.12	28.5	
	C2405H5		6	17.27	103.6	
	C2705H5		4	18.10	72.4	
	C3206H5		4	31.43	125.7	
	FD3232B7H		4	16.80	67.2	
	FD6666B7D		5	116.50	582.5	
	T3605	–	1	19.00	19.0	主材安装爬梯
	T6980	–	2	36.20	36.2	主材安装爬梯
合计		10023.9 kg (用于主材带脚钉)				
合计		10095.8 kg (用于主材装爬梯)				

			山东电力工程咨询院有限公司			浙江特高压交流环网工程线路 工程	施工图	设计阶段
			批准	雷强	校核	马一丹	SZK31102A双回路直线塔 108.0-1.5m腿部结构图(1/2) 111.0-4.5m腿部结构图(1/2)	45
			审核	高锡鹏				
电气	赵庆周	2026.08			设计/勘测	潘旭光		
专业	会签	日期	比例	1:40	日期	2026年 08月	图号 37-SA36901S-T0121-103	版本