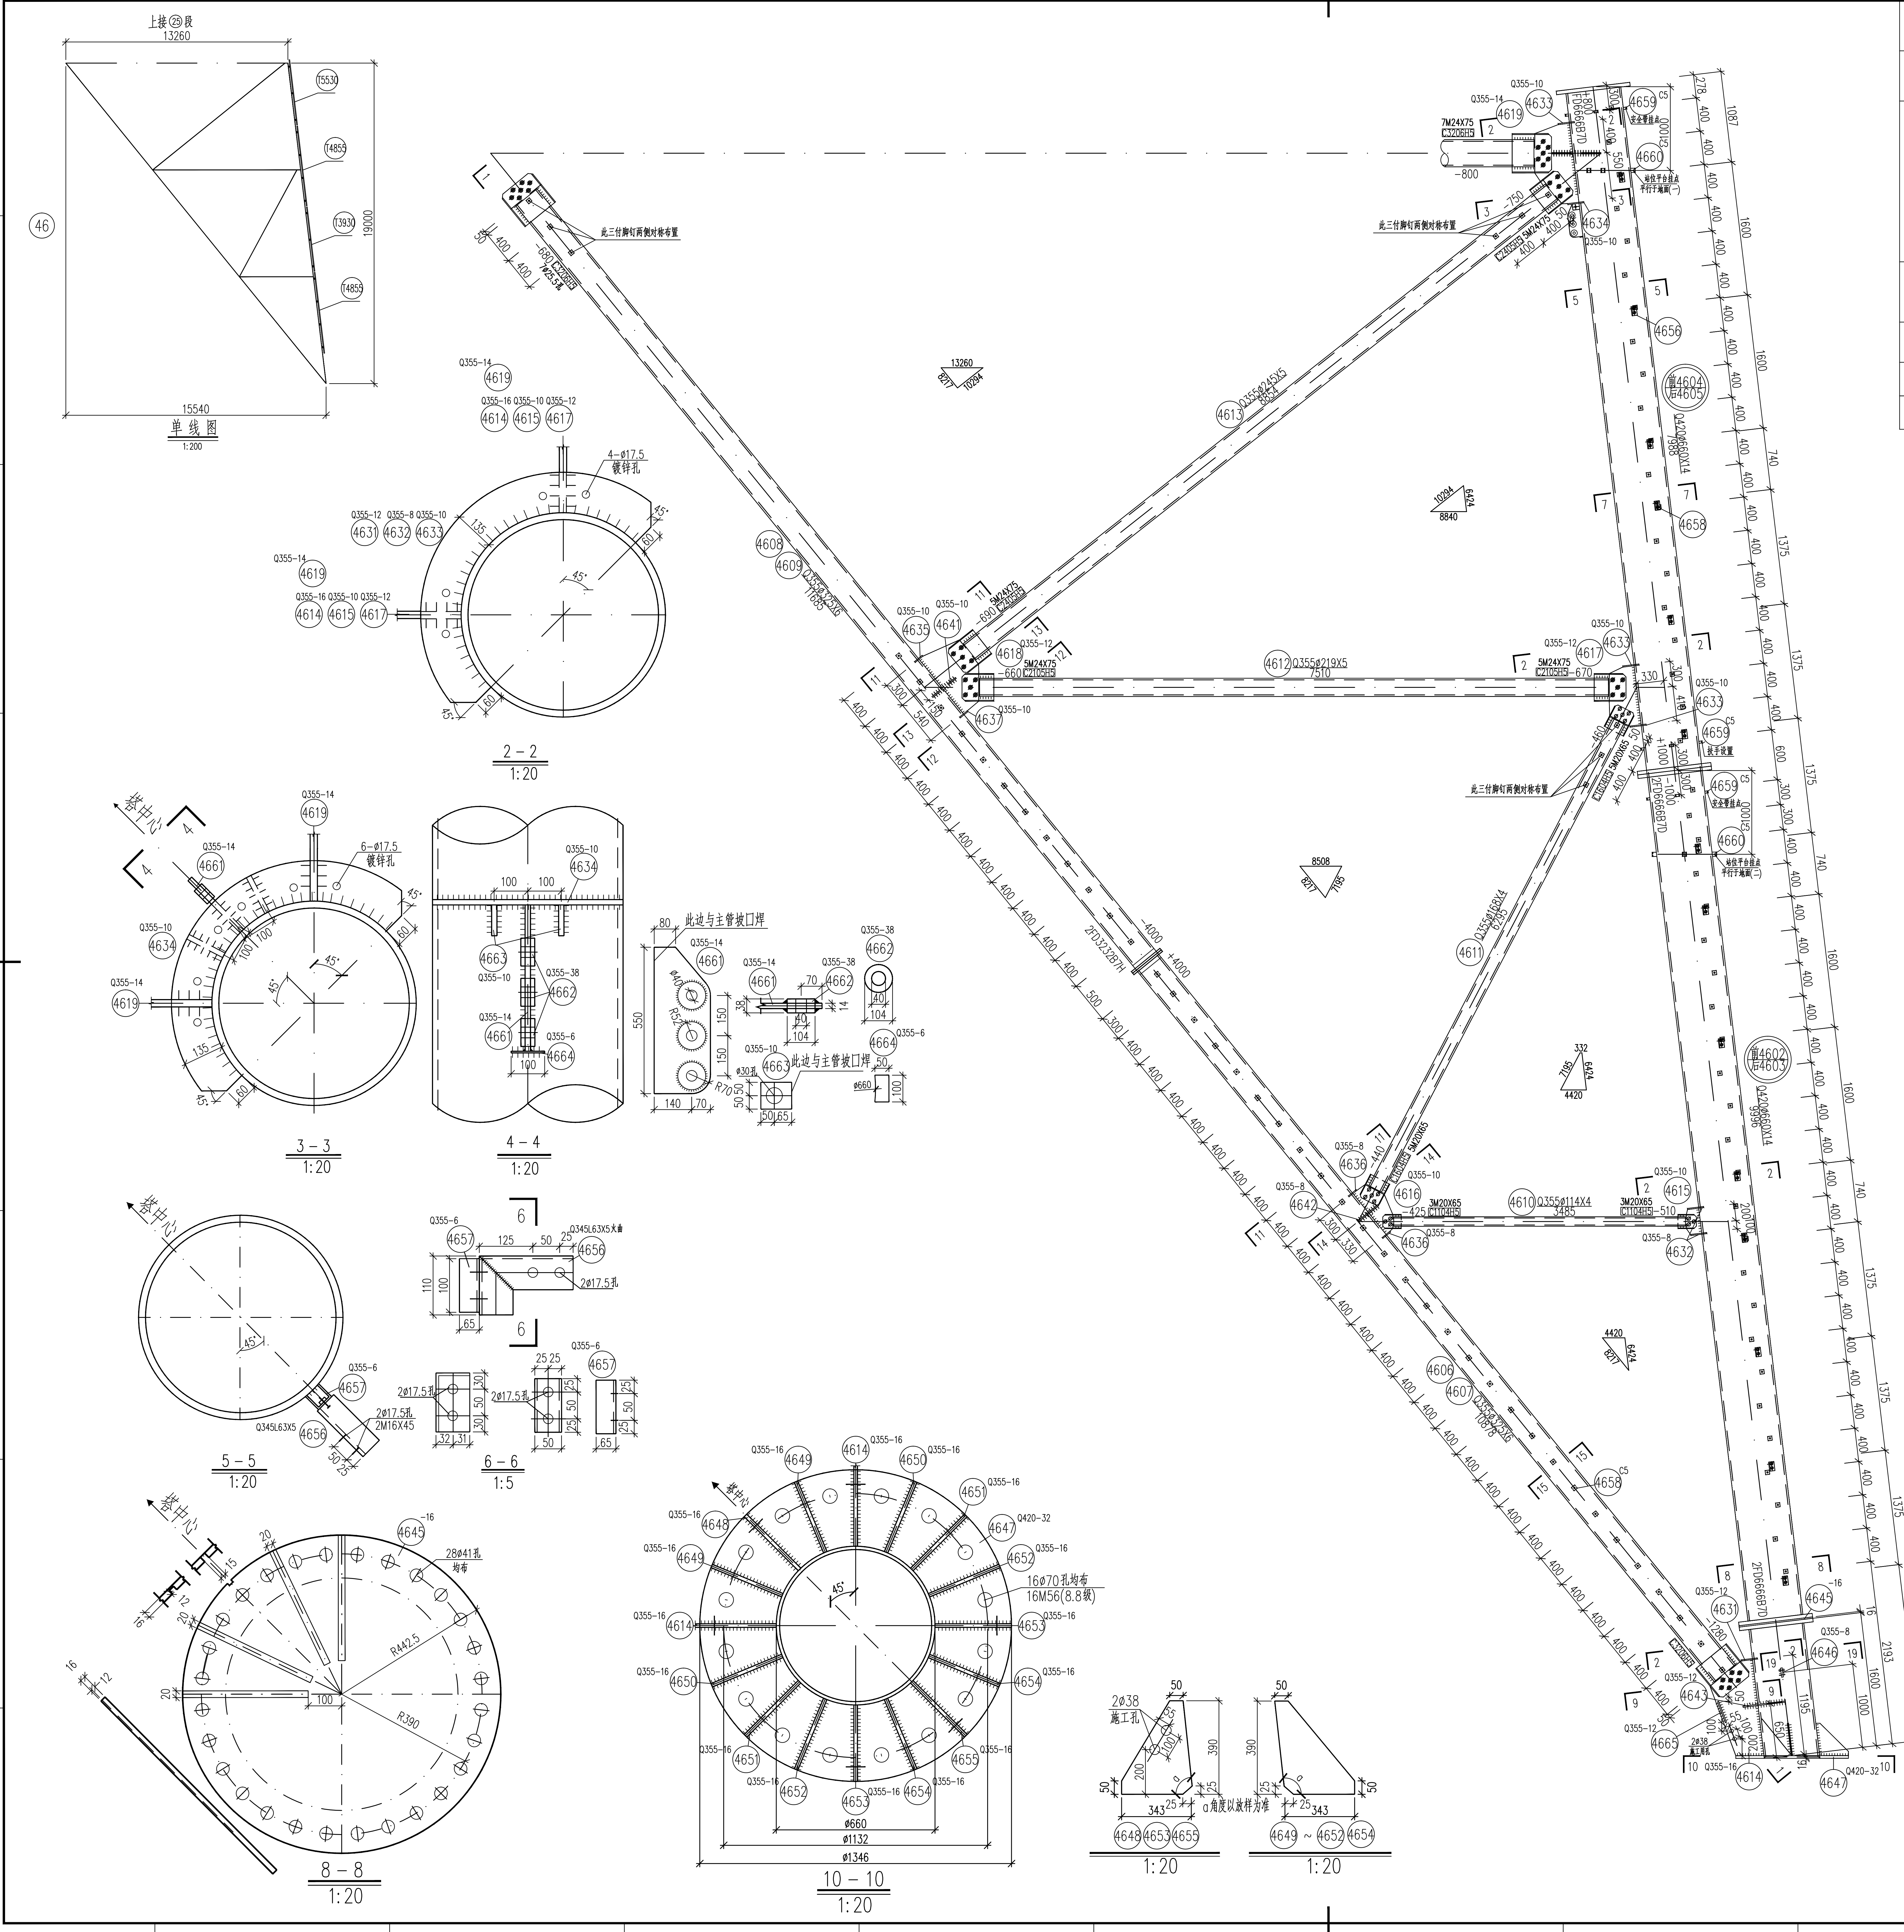

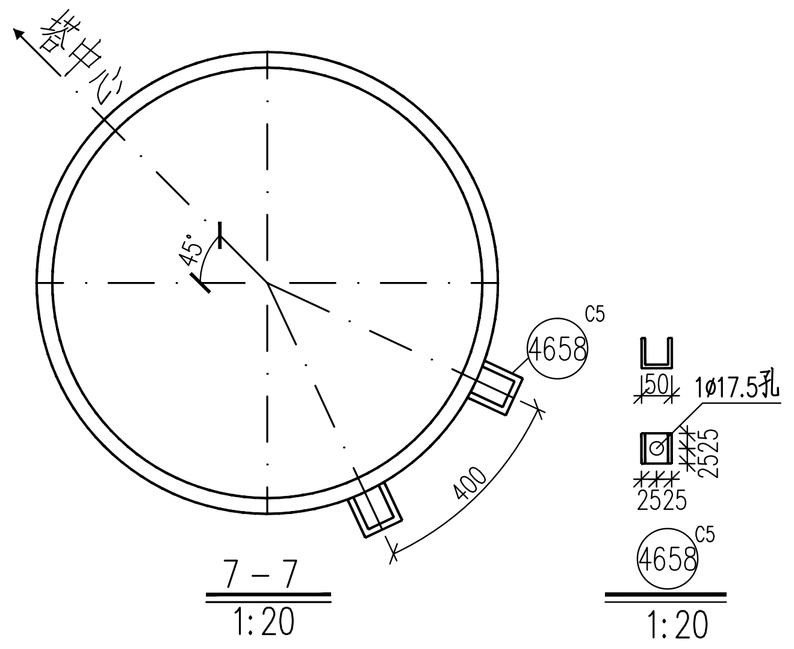

螺栓、脚钉、垫圈 明细表

名称	级别	规格	符号	数量	重量(kg)	备注
螺栓	6.8级	M16X45	◎	56	9.4	用于主材装爬梯
		M16X65	⊗	48	9.6	
		M20X65	∅	66	23.3	
	8.8级	M24X75	⦰	88	52.2	
		M20X100	○	44	21.8	法兰螺栓
		M39X175	○	56	198.9	法兰螺栓
		M39X195	○	28	104.7	法兰螺栓
脚钉	6.8级	M16X185	⊖	258	107.0	用于主材装爬梯
		M16X185	⊣	303	125.6	用于主材带脚钉
垫圈	Q235		规格X个数			
合计			536.1 kg (用于主材带脚钉)			
合计			526.9 kg (用于主材装爬梯)			

说明：1.材料表为一个塔腿的重量。

2.本段塔腿为铁塔D腿，安装爬梯，当为A、B、C腿时需焊接脚钉连接槽钢。

构 件 明 细 表

编号	规格	长度 (mm)	数量	重量(kg) 一件	重量(kg) 小计	备注
4601	Q420ø660X14	1537	1	342.81	342.8	一端切弧 带脚钉
4602	Q420ø660X14	9996	1	2229.49	2229.5	装爬梯
4603	Q420ø660X14	9996	0	2229.49	0.0	带脚钉
4604	Q420ø660X14	7988	1	1781.63	1781.6	装爬梯
4605	Q420ø660X14	7988	0	1781.63	0.0	带脚钉
4606	Q355ø325X6	10878	1	513.46	513.5	带脚钉
4607	Q355ø325X6	10878	1	513.46	513.5	带脚钉
4608	Q355ø325X6	11685	1	551.56	551.6	带脚钉
4609	Q355ø325X6	11685	1	551.56	551.6	带脚钉
4610	Q355ø114X4	3485	2	37.82	75.6	
4611	Q355ø168X4	6295	2	101.84	203.7	带脚钉
4612	Q355ø219X5	7510	2	198.17	396.3	
4613	Q355ø245X5	8854	2	262.02	524.0	
4614	Q355-16X592	1235	2	91.83	183.7	
4615	Q355-10X213	330	2	5.52	11.0	
4616	Q355-10X318	726	2	18.12	36.2	
4617	Q355-12X391	781	2	28.77	57.5	
4618	Q355-12X570	924	2	49.61	99.2	
4619	Q355-14X522	1045	2	59.95	119.9	
4620	Q355ø159X4	5321	1	81.36	81.4	
4621	Q355ø180X5	3158	1	68.15	68.2	带脚钉
4622	Q355ø180X5	7075	1	152.67	152.7	带脚钉
4623	Q355ø180X5	11082	1	239.14	239.1	带脚钉
4624	Q355ø219X5	8852	1	233.58	233.6	带脚钉
4625	Q355ø219X5	8852	1	233.58	233.6	带脚钉
4626	Q355-10X322	726	2	18.35	36.7	
4627	Q355-10X610	440	1	21.07	21.1	
4628	Q355-10X610	223	2	10.68	21.4	
4629	Q355-12X377	814	2	28.91	57.8	
4630	Q355-12X412	1001	1	38.85	38.8	
4631	Q355-12X135	1374	1	17.47	17.5	
4632	Q355-8X135	1374	2	11.65	23.3	
4633	Q355-10X135	1374	3	14.56	43.7	
4634	Q355-10X135	1374	1	14.56	14.6	
4635	Q355-10X70	512	2	2.81	5.6	
4636	Q355-8X70	512	4	2.25	9.0	
4637	Q355-10X70	341	2	1.87	3.7	
4638	Q355-10X70	285	2	1.57	3.1	
4639	Q355-8X60	415	4	1.56	6.2	
4640	Q355-10X150	365	2	4.30	8.6	
4641	Q355-10X200	205	2	3.22	6.4	
4642	Q355-8X200	205	2	2.57	5.1	
4643	Q355-12X180	330	2	5.60	11.2	
4644	Q355-12X180	660	1	11.19	11.2	
4645	-16X885	885	1	77.26	77.3	遮水板
4646	Q345-8X80	110	1	0.55	0.6	接地孔用
4647	Q420-32X1346	1346	1	271.50	271.5	
4648	Q355-16X343	390	1	16.80	16.8	
4649	Q355-16X343	390	2	16.80	33.6	
4650	Q355-16X343	390	2	16.80	33.6	
4651	Q355-16X343	390	2	16.80	33.6	
4652	Q355-16X343	390	2	16.80	33.6	
4653	Q355-16X343	390	2	16.80	33.6	
4654	Q355-16X343	390	2	16.80	33.6	
4655	Q355-16X343	390	1	16.80	16.8	
4656	Q345L63X5	310	14	1.49	20.9	火曲(用于主材装爬梯)
4657	Q355-6X100	180	14	0.85	11.9	火曲(用于主材装爬梯)
4658	C5	50	258	0.27	69.7	槽钢(用于主材装爬梯)
4658	C5	50	303	0.27	81.8	槽钢(用于主材带脚钉)
4659	C5	25	12	0.14	1.7	槽钢
4660	C5	50	8	0.27	2.2	槽钢
4661	Q355-14X210	550	1	12.69	12.7	
4662	Q355-38X104	104	3	3.23	9.7	
4663	Q355-10X100	115	2	0.90	1.8	
4664	Q355-6X50	100	1	0.24	0.2	
4665	Q355-12X80	270	2	2.03	4.1	
	C1104H5		4	3.44	13.8	
	C1504H5		2	6.52	13.0	
	C1604H5		4	7.12	28.5	
	C1805H5		4	7.12	28.5	
	X1805H7		2	21.60	43.2	
	C2105H5		8	14.54	116.3	
	C2405H5		4	17.27	69.1	
	C3206H5		4	31.43	125.7	
	FD3232B7H		4	16.80	67.2	
	FD6666B7D		5	116.50	582.5	
	T3930	–	1	20.70	20.7	主材安装爬梯
	T4855	–	2	25.00	50.0	主材安装爬梯
	T5530	–	1	28.80	28.8	主材安装爬梯
合计	11331.4 kg (用于主材带脚钉)					
合计	11451.6 kg (用于主材装爬梯)					

山东电力工程咨询院有限公司				浙江特高压交流环网工程线路 工程		施工图	设计阶段
批准	雷强	校核	马一丹	SZK31102A双回路直线塔 108.0-0.0m腿部结构图(1/2) 111.0-3.0m腿部结构图(1/2)		46	
审核	高锡鹏	设计/勘测	潘胜先				
比例	1:40	日期	2026年 08月	图号	37-SA36901S-T0121-105	版本	

电气	赵庆周	2026.08
专业	会签	日期