




11 – 11
1:20

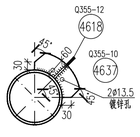


12 – 12
1:20

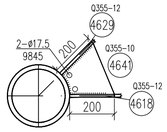


13 – 13
1:20

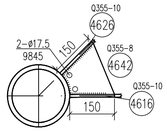


14 – 14
1:20

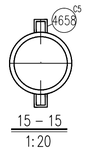


15 – 15
1:20

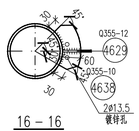


16 – 16
1:20

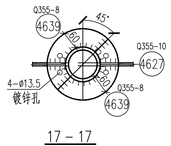

17 – 17
1:20

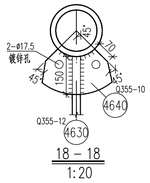


18 – 18
1:20

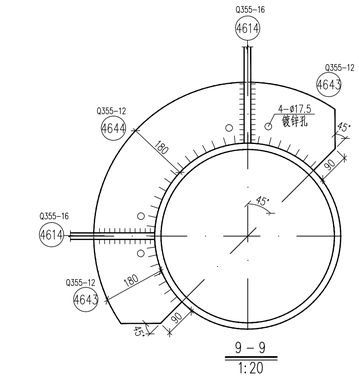


9 – 9
1:20

1:20

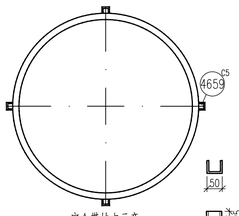


安全带挂点示意
扶手设置示意

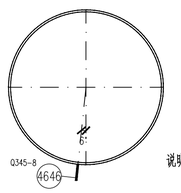


19 – 19
1:20


说明：接地孔安装板 4646 避开法兰加劲板和地脚法兰螺栓所在角度，以避免接地引下线和法兰加劲板相碰。

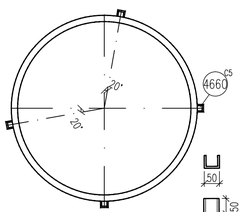


站位平台示意(一)

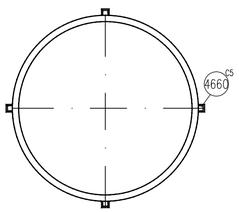

站位平台示意(二)

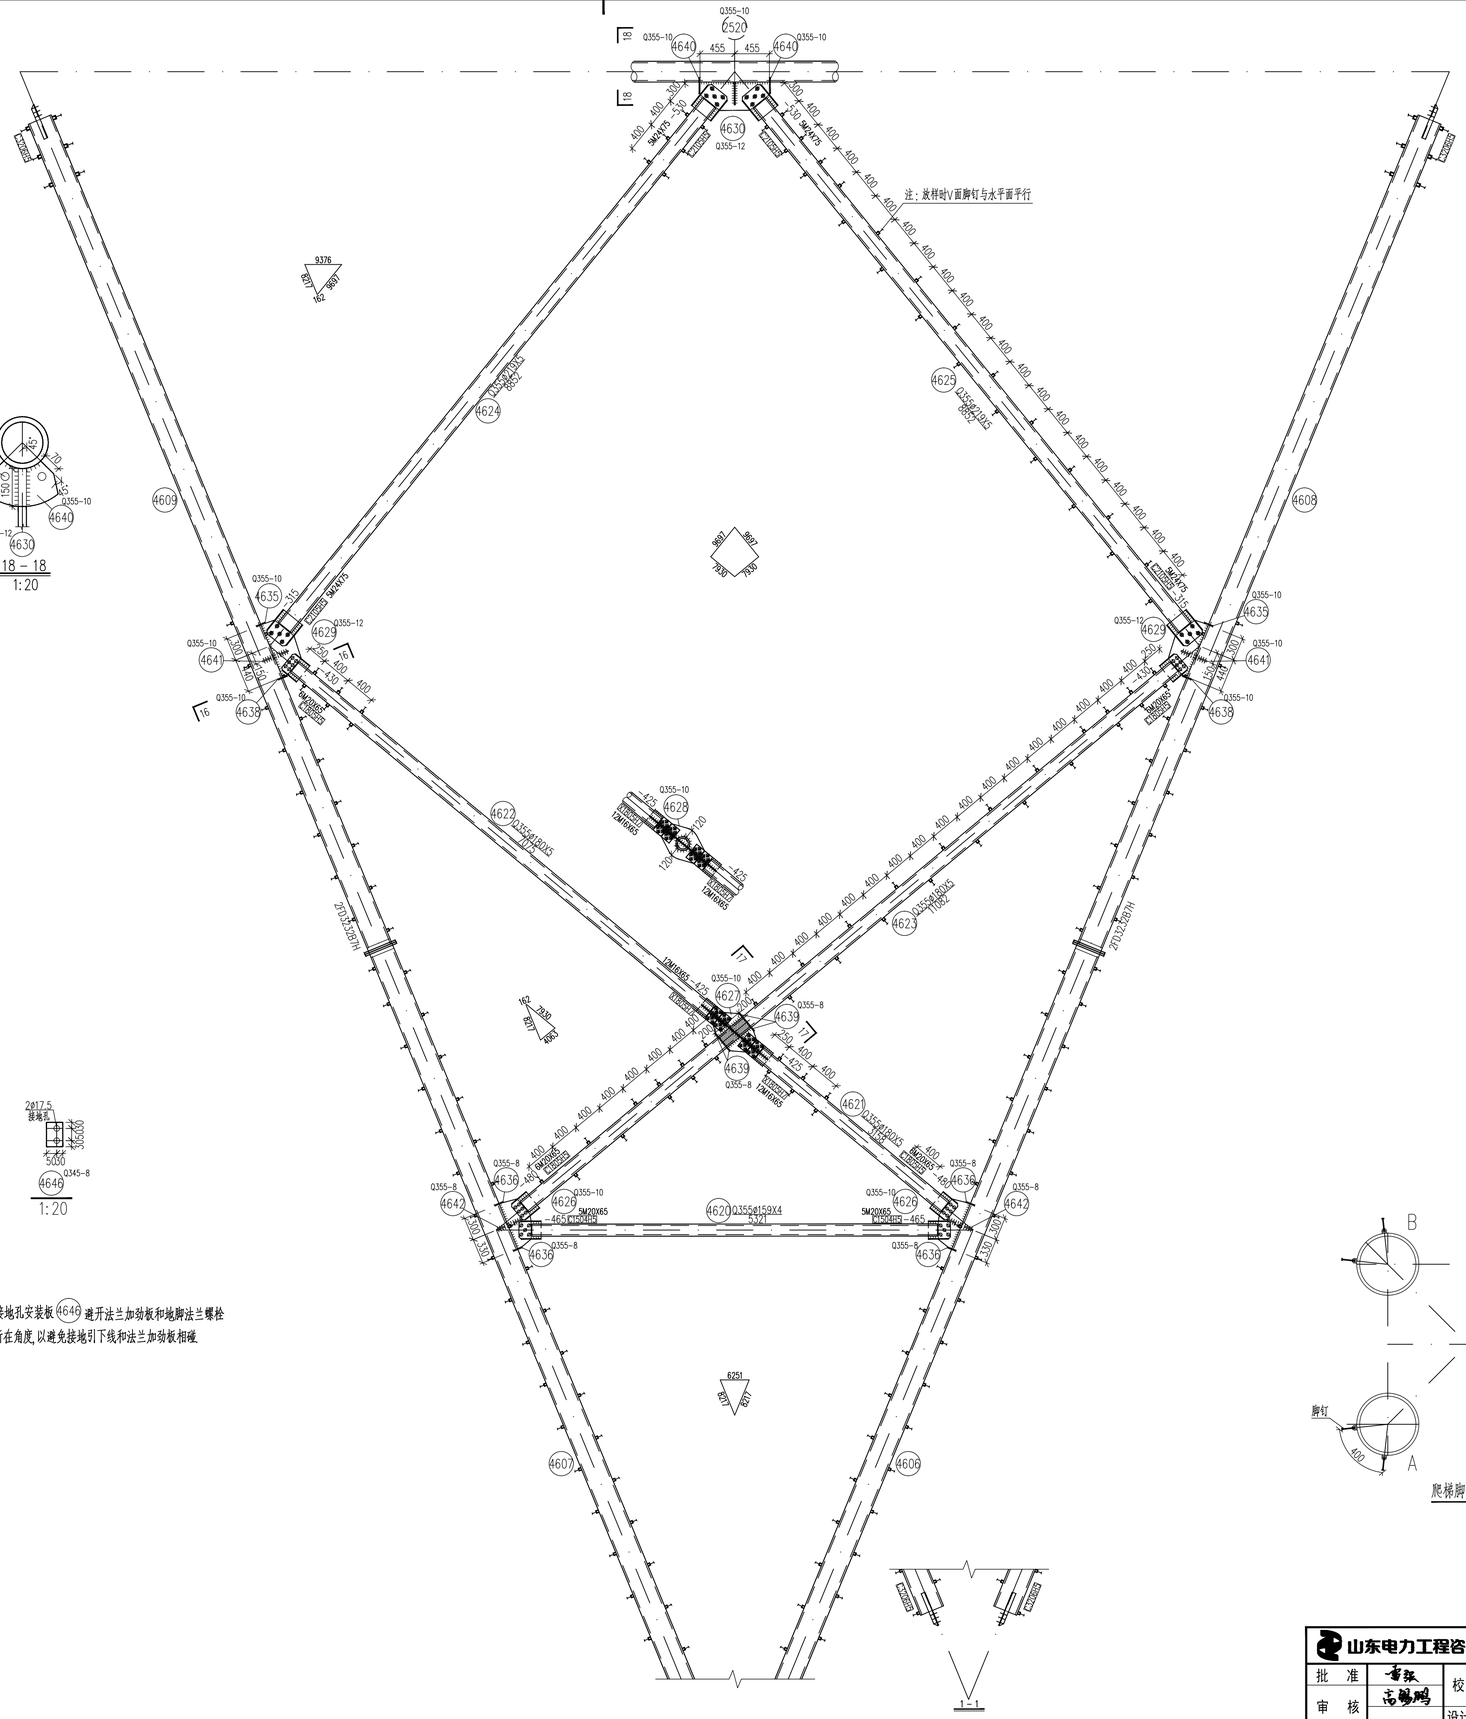

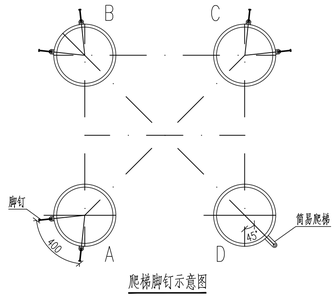

爬梯脚钉示意图

山东电力工程咨询院有限公司				浙江特高压交流环网工程线路 工程	施工图 设计阶段
批 准		校 核		SZK31102A双回路直线塔	
审 核		设计/勘测		108.0-0.0m腿部结构图(2/2) 111.0-3.0m腿部结构图(2/2)	46
比 例	1:40	日 期	2026年 08月	图 号 37-SA36901S-T0121-106	版本