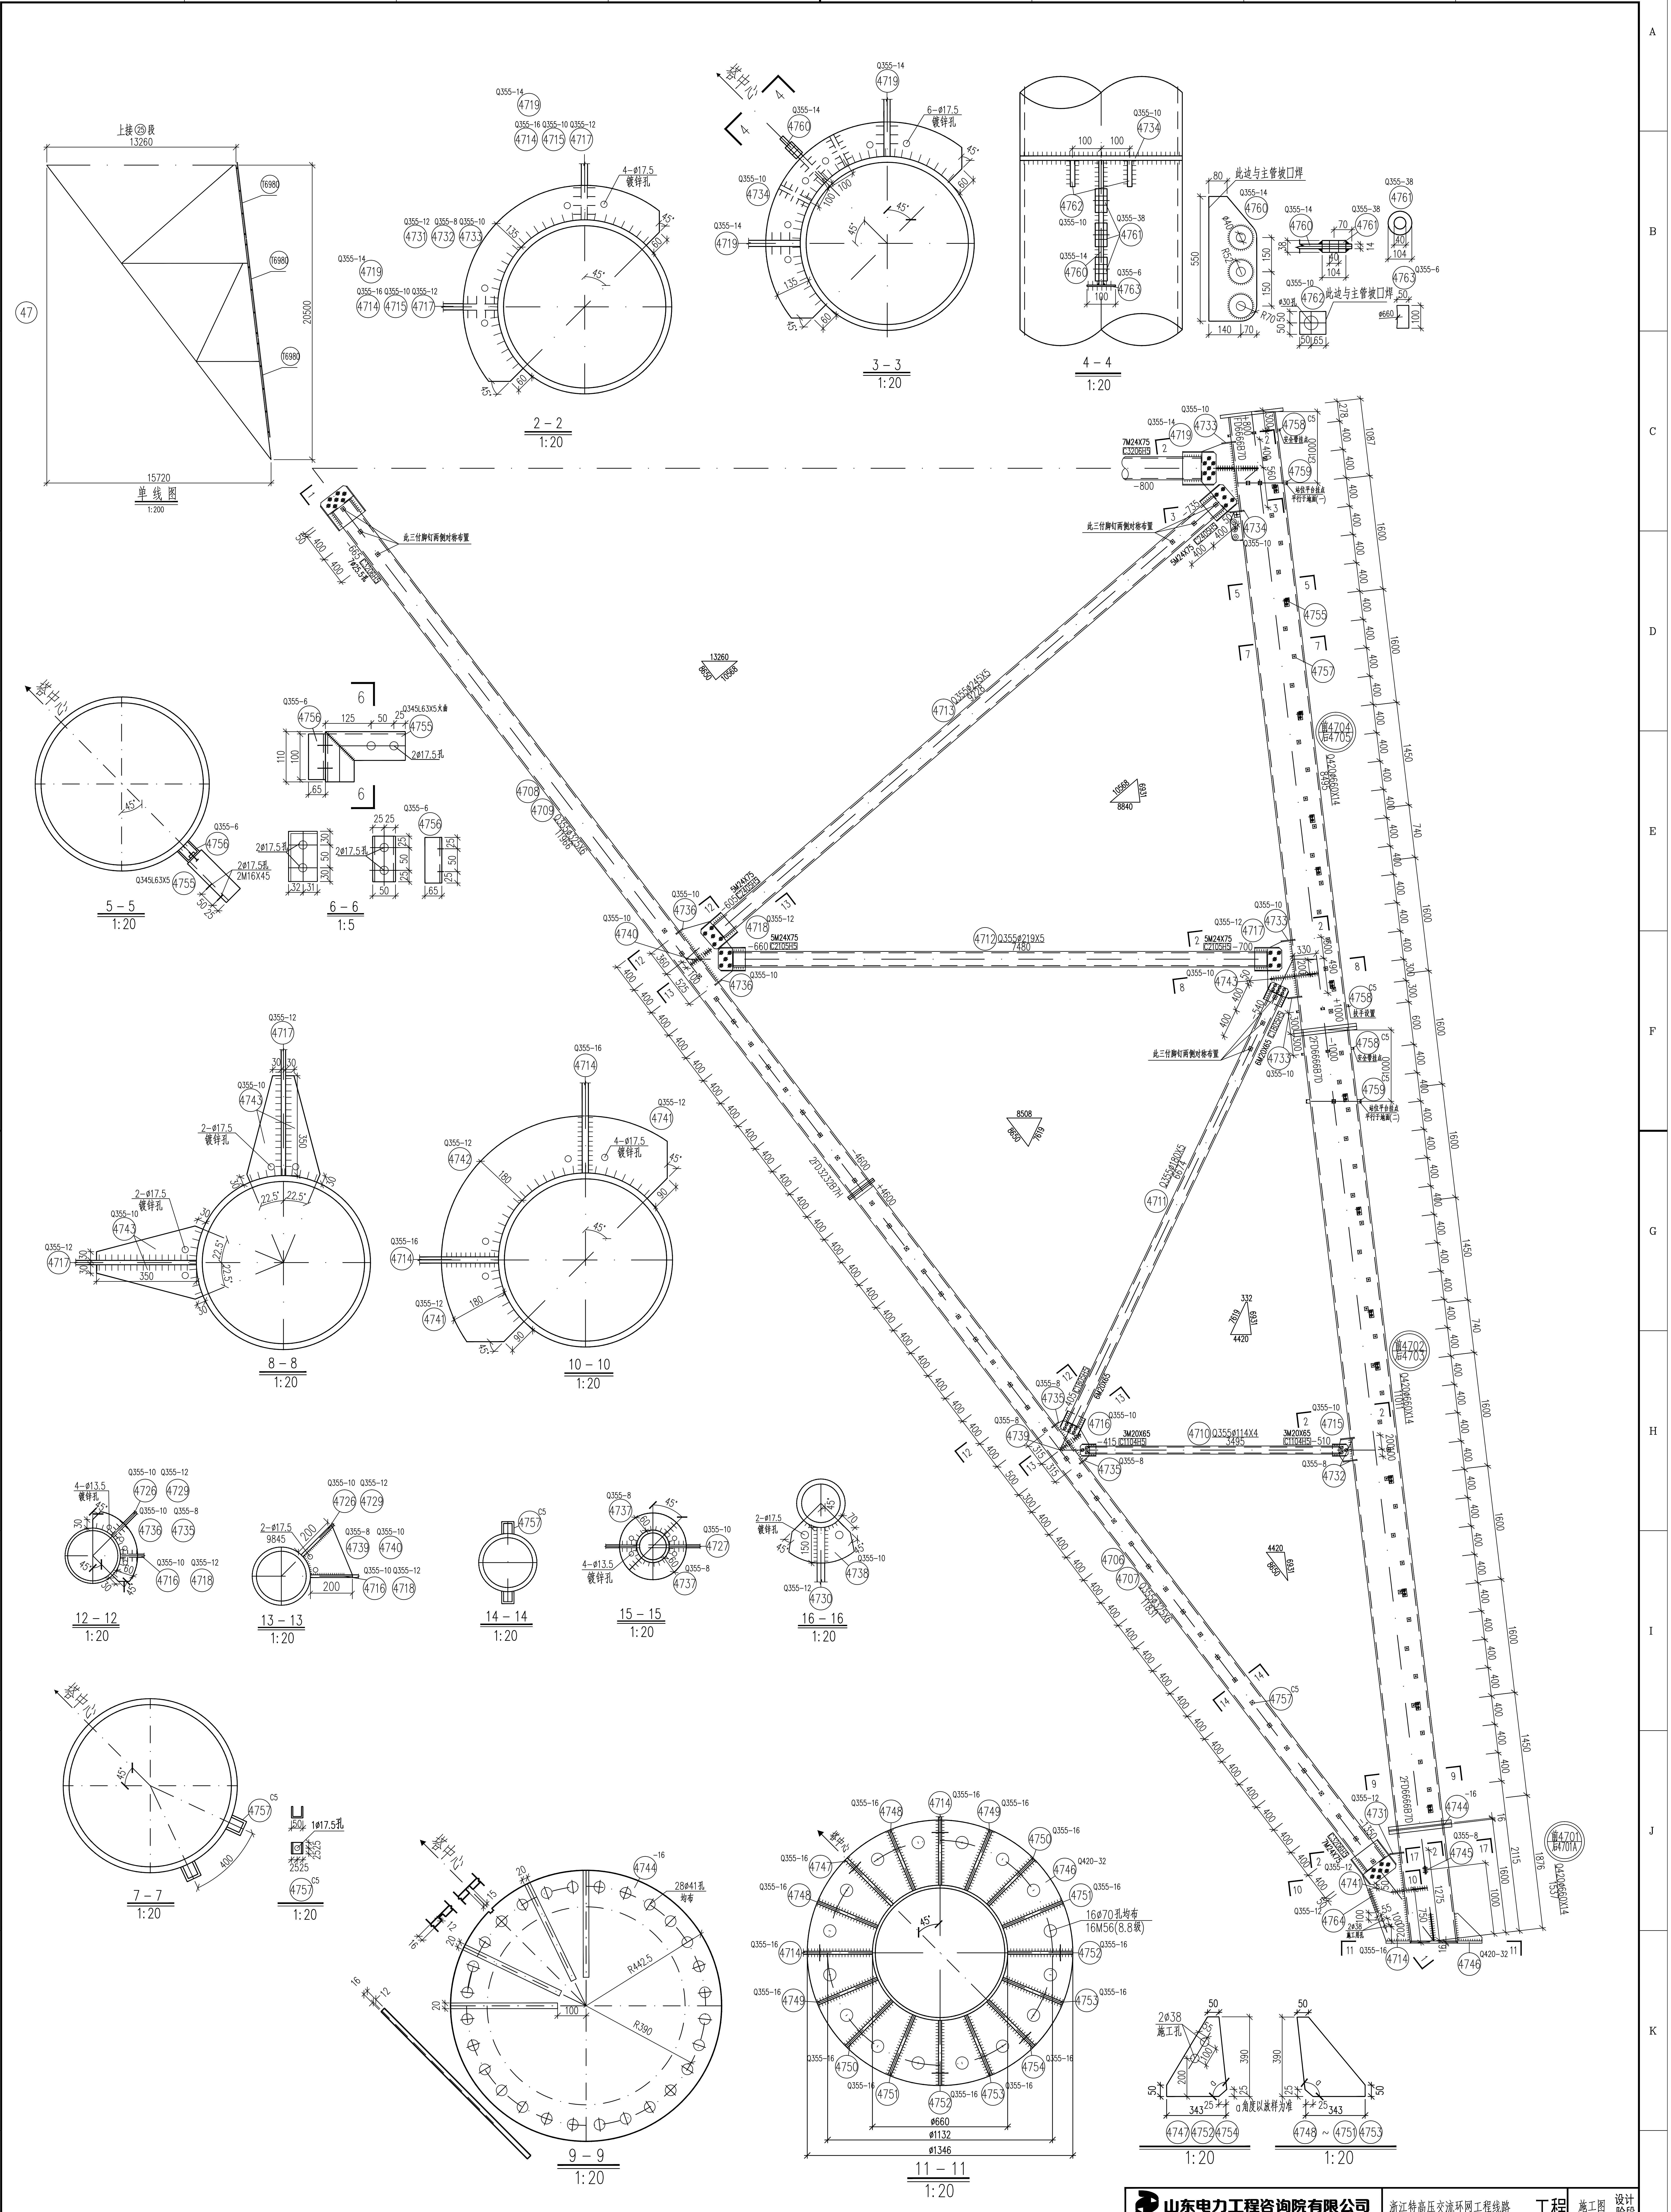

山东电力工程咨询院有限公司				浙江特高压交流环网工程线路 工程	施工图	设计阶段
批 准	雷强	校 核	马一丹	SZK31102A双回路直线塔 111.0-1.5m腿部结构图(1/2) 114.0-4.5m腿部结构图(1/2)	47	
审 核	高锡鹏					
		设计/勘测	潘旭光			
比 例	1:40	日 期	2026年 08月	图 号	37-SA36901S-T0121-107	版本

电 气	赵庆周	2026.08
专 业	会 签	日 期