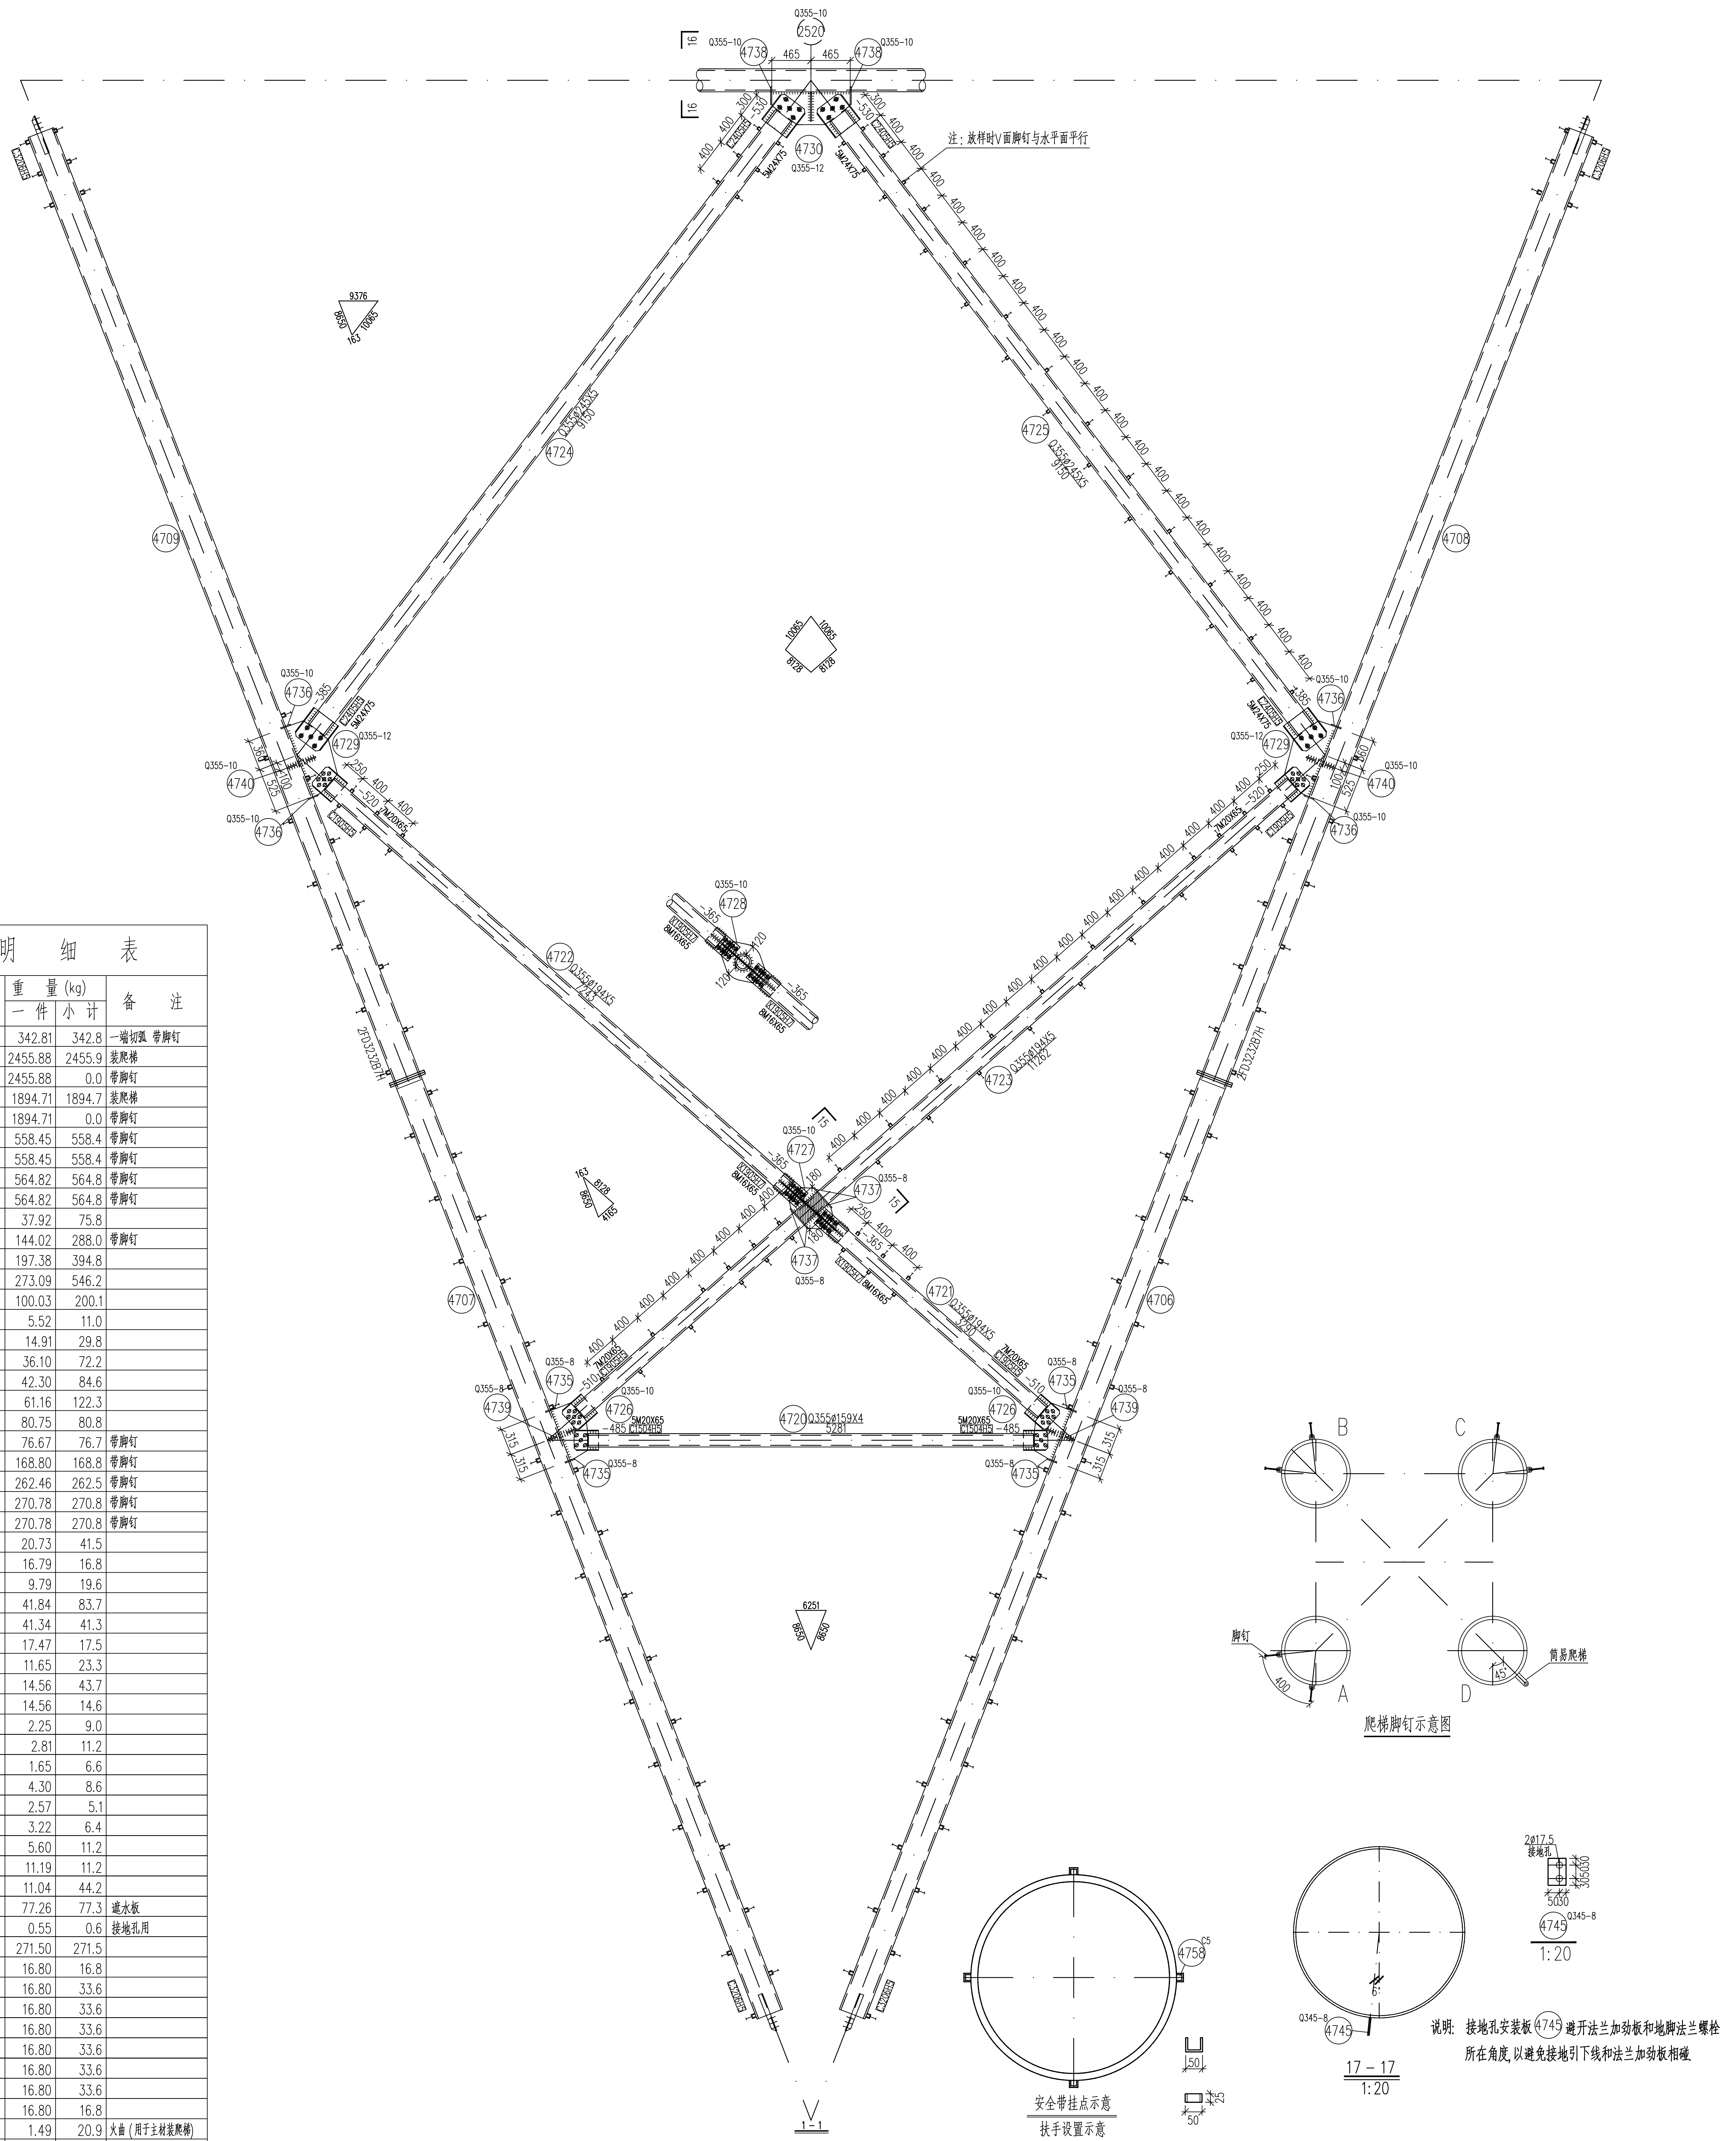
Q355-10
2520
4738
465
465
16
300
530
400
C2405H5
5M24X75
4730
Q355-12
注：放样时V面脚钉与水平面平行
4701
4702
4706
4707
4708
4709
4720
Q355ø159X4
5281
4721
4722
4723
4724
4725
Q355ø245X5
9150
Q355ø194X5
11262
4726
4727
4728
4729
4735
4736
4737
4739
4740
Q355-8
5M20X65
C1504H5
2FD3232B7H
1-1
B
C
A
D
脚钉
400
简易爬梯
45°
4758
C5
50
25
2ø17.5
接地孔
5030
305030
4745
Q345-8
6
1:20

爬梯脚钉示意图

安全带挂点示意

扶手设置示意

17 - 17
1:20

说明：接地孔安装板④745避开法兰加劲板和地脚法兰螺栓所在角度，以避免接地引下线和法兰加劲板相碰.

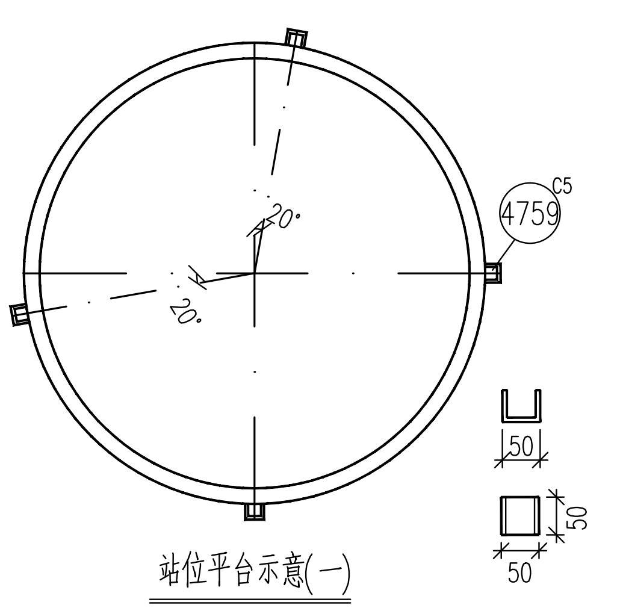
4759
C5
20°
20°
50

站位平台示意(一)

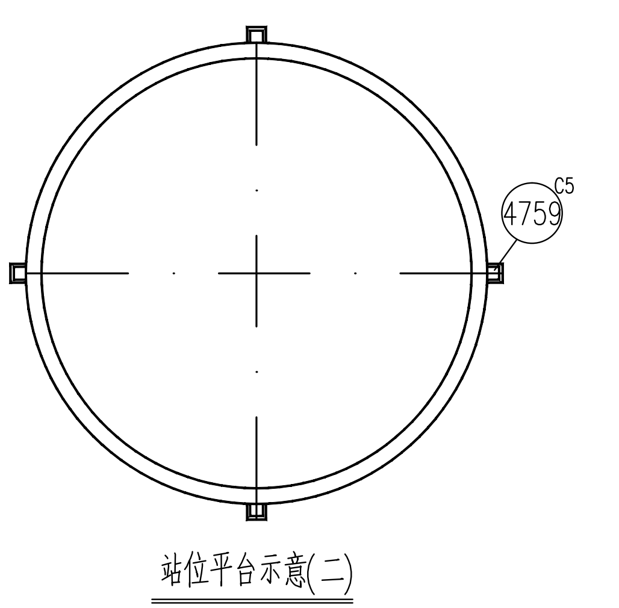

站位平台示意(二)

构 件 明 细 表

编号	规 格	长 度 (mm)	数量	重 量 (kg) 一 件	重 量 (kg) 小 计	备 注
4701	Q420ø660X14	1537	1	342.81	342.8	一端切弧 带脚钉
4702	Q420ø660X14	11011	1	2455.88	2455.9	装爬梯
4703	Q420ø660X14	11011	0	2455.88	0.0	带脚钉
4704	Q420ø660X14	8495	1	1894.71	1894.7	装爬梯
4705	Q420ø660X14	8495	0	1894.71	0.0	带脚钉
4706	Q355ø325X6	11831	1	558.45	558.4	带脚钉
4707	Q355ø325X6	11831	1	558.45	558.4	带脚钉
4708	Q355ø325X6	11966	1	564.82	564.8	带脚钉
4709	Q355ø325X6	11966	1	564.82	564.8	带脚钉
4710	Q355ø114X4	3495	2	37.92	75.8	
4711	Q355ø180X5	6674	2	144.02	288.0	带脚钉
4712	Q355ø219X5	7480	2	197.38	394.8	
4713	Q355ø245X5	9228	2	273.09	546.2	
4714	Q355-16X602	1323	2	100.03	200.1	
4715	Q355-10X213	330	2	5.52	11.0	
4716	Q355-10X274	693	2	14.91	29.8	
4717	Q355-12X441	869	2	36.10	72.2	
4718	Q355-12X461	974	2	42.30	84.6	
4719	Q355-14X527	1056	2	61.16	122.3	
4720	Q355ø159X4	5281	1	80.75	80.8	
4721	Q355ø194X5	3290	1	76.67	76.7	带脚钉
4722	Q355ø194X5	7243	1	168.80	168.8	带脚钉
4723	Q355ø194X5	11262	1	262.46	262.5	带脚钉
4724	Q355ø245X5	9150	1	270.78	270.8	带脚钉
4725	Q355ø245X5	9150	1	270.78	270.8	带脚钉
4726	Q355-10X381	693	2	20.73	41.5	
4727	Q355-10X540	396	1	16.79	16.8	
4728	Q355-10X540	231	2	9.79	19.6	
4729	Q355-12X456	974	2	41.84	83.7	
4730	Q355-12X429	1023	1	41.34	41.3	
4731	Q355-12X135	1374	1	17.47	17.5	
4732	Q355-8X135	1374	2	11.65	23.3	
4733	Q355-10X135	1374	3	14.56	43.7	
4734	Q355-10X135	1374	1	14.56	14.6	
4735	Q355-8X70	512	4	2.25	9.0	
4736	Q355-10X70	512	4	2.81	11.2	
4737	Q355-8X60	439	4	1.65	6.6	
4738	Q355-10X150	365	2	4.30	8.6	
4739	Q355-8X200	205	2	2.57	5.1	
4740	Q355-10X200	205	2	3.22	6.4	
4741	Q355-12X180	330	2	5.60	11.2	
4742	Q355-12X180	660	1	11.19	11.2	
4743	Q355-10X284	495	4	11.04	44.2	
4744	-16X885	885	1	77.26	77.3	遮水板
4745	Q345-8X80	110	1	0.55	0.6	接地孔用
4746	Q420-32X1346	1346	1	271.50	271.5	
4747	Q355-16X343	390	1	16.80	16.8	
4748	Q355-16X343	390	2	16.80	33.6	
4749	Q355-16X343	390	2	16.80	33.6	
4750	Q355-16X343	390	2	16.80	33.6	
4751	Q355-16X343	390	2	16.80	33.6	
4752	Q355-16X343	390	2	16.80	33.6	
4753	Q355-16X343	390	2	16.80	33.6	
4754	Q355-16X343	390	1	16.80	16.8	
4755	Q345L63X5	310	14	1.49	20.9	火曲 (用于主材装爬梯)
4756	Q355-6X100	180	14	0.85	11.9	火曲 (用于主材装爬梯)
4757	C5	50	267	0.27	72.1	槽钢 (用于主材装爬梯)
4757	C5	50	316	0.27	85.3	槽钢 (用于主材带脚钉)
4758	C5	25	12	0.14	1.7	槽钢
4759	C5	50	8	0.27	2.2	槽钢
4760	Q355-14X210	550	1	12.69	12.7	
4761	Q355-38X104	104	3	3.23	9.7	
4762	Q355-10X100	115	2	0.90	1.8	
4763	Q355-6X50	100	1	0.24	0.2	
4764	Q355-12X80	360	1	2.71	2.7	
	C1104H5		4	3.44	13.8	
	C1504H5		2	6.52	13.0	
	C1805H5		4	7.12	28.5	
	C1905H5		4	8.80	35.2	
	X1905H7		2	17.90	35.8	
	C2105H5		4	14.54	58.2	
	C2405H5		8	17.27	138.2	
	C3206H5		4	31.43	125.7	
	FD3232B7H		4	16.80	67.2	
	FD6666B7D		5	116.50	582.5	
	T6980	-	3	36.20	108.6	主材安装爬梯
合 计	12109.5 kg (用于主材带脚钉)					
合 计	12237.7 kg (用于主材装爬梯)					

说明：1.材料表为一个塔腿的重量。

2.本段塔腿为铁塔D腿，安装爬梯，当为A、B、C腿时需焊接脚钉连接槽钢。

螺栓、脚钉、垫圈 明细表

名称	级别	规 格	符 号	数量	重量(kg)	备 注
螺栓	6.8级	M16X45	◎	56	9.4	用于主材装爬梯
		M16X65	⊗	32	6.4	
		M20X65	∅	74	26.1	
	8.8级	M24X75	⊘	88	52.2	
		M20X100	○	44	21.8	法兰螺栓
		M39X175	○	56	198.9	法兰螺栓
		M39X195	○	28	104.7	法兰螺栓
脚钉	6.8级	M16X185	⊖ ⊣	267	110.7	用于主材装爬梯
		M16X185		316	131.0	用于主材带脚钉
垫圈	Q235		规格X个数			
合 计			541.1 kg (用于主材带脚钉)			
合 计			530.2 kg (用于主材装爬梯)			

山东电力工程咨询院有限公司		浙江特高压交流环网工程线路 工程	施工图	设计阶段
批 准	雷强	校 核	马一丹	SZK31102A双回路直线塔 111.0-1.5m腿部结构图(2/2) 114.0-4.5m腿部结构图(2/2)
审 核	高锡鹏			㊼
		设计/勘测	潘旺光	
比 例	1:40	日 期	2026年 08月	图 号 37-SA36901S-T0121-108 版本