

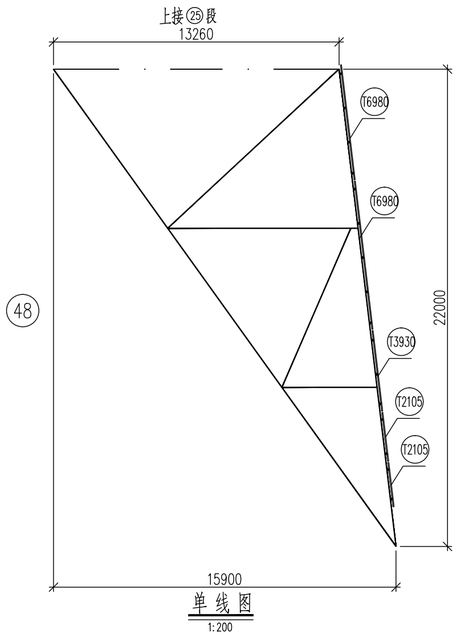




单线图
1:200

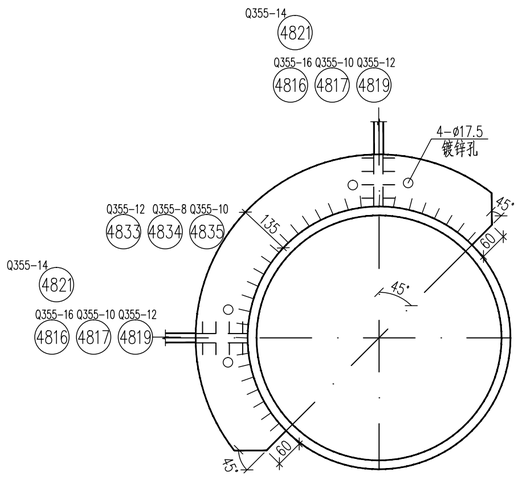



2 – 2
1:20

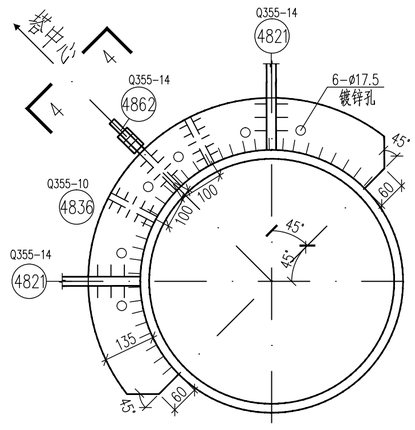



3 – 3
1:20

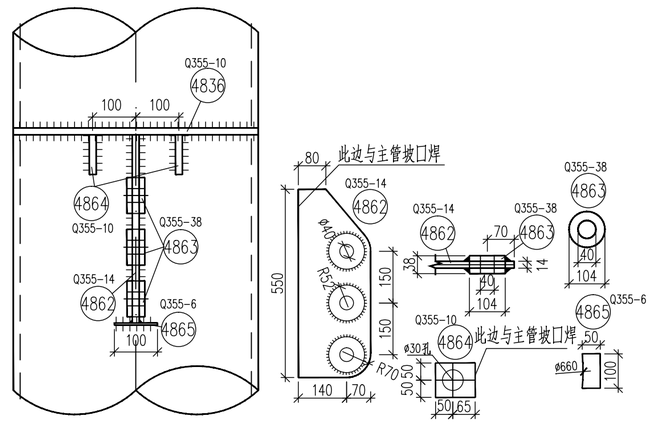




4 – 4
1:20

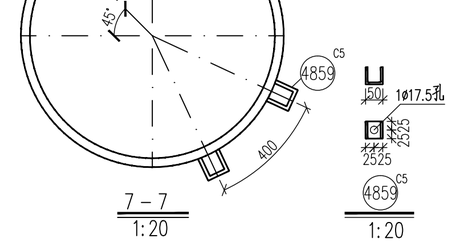


1:20

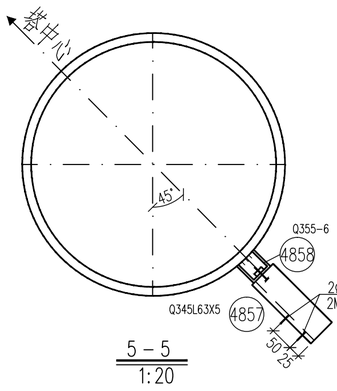

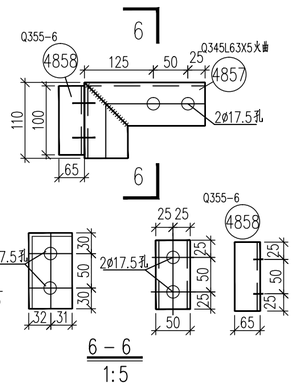


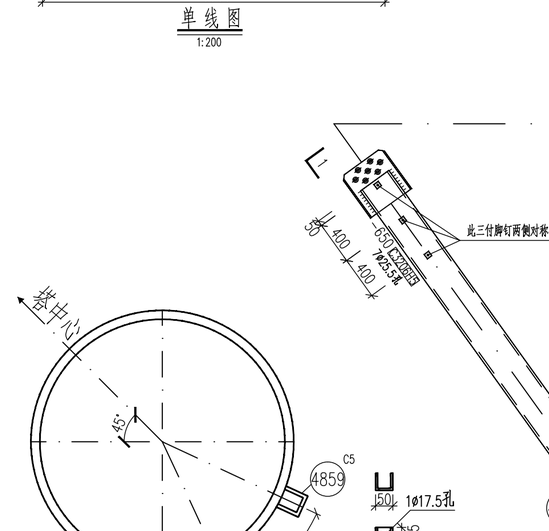




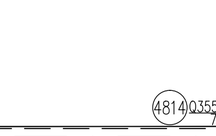


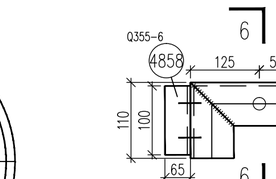



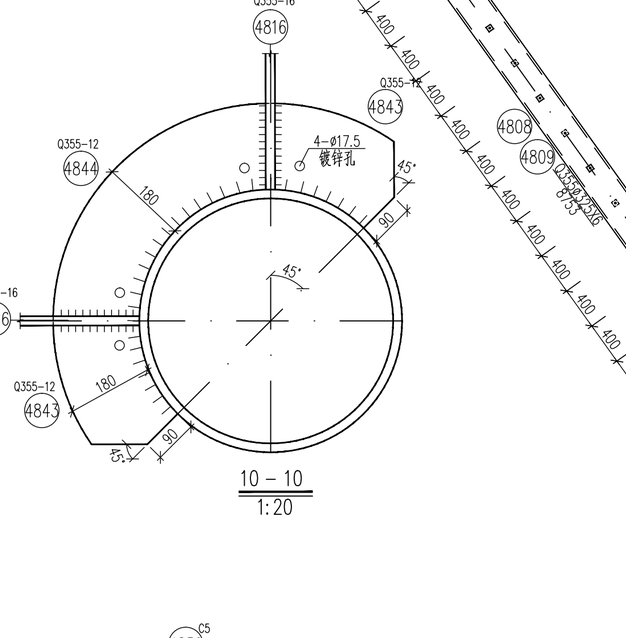








1:20

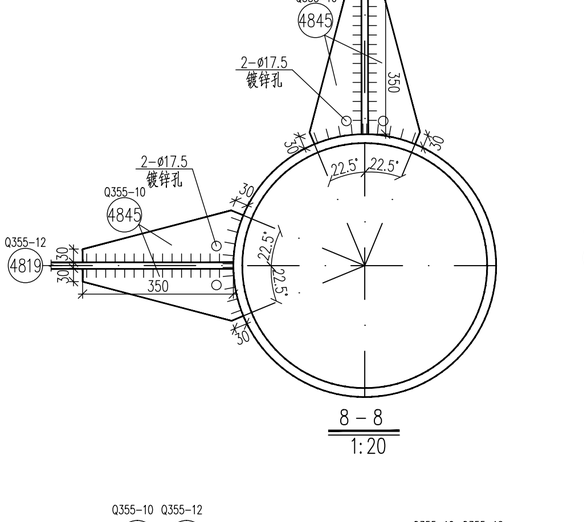1:20

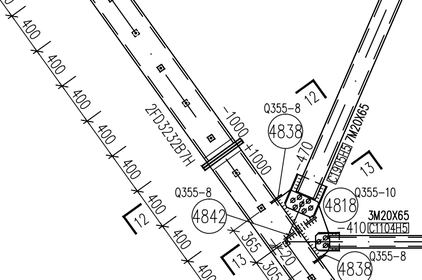


| | | | | | | | |
|---|---|---|---|---|---|---|---|
| 山东电力工程咨询院有限公司 | | | | | | 浙江特高压交流环网工程线路 | 工程 | 施工图 | 设计阶段 |
| 批准 | 雷张 | 校核 | 刘一丹 | | | SZK31102A双回路直线塔 | | | |
| 审核 | 高鹏鹏 | | | | | 111.0-0.0m腿部结构图(1/2) | 48 | | |
| | | | | | | 114.0-3.0m腿部结构图(1/2) | | | |
| 电气 | 赵安周 | 2026.08 | 设计/勘测 | 潘祖光 | | | | | |
| 专业 | 会签 | 日期 | 比例 | 1:40 | 日期 | 2026年08月 | 图号 | 37-SA36901S-T0121-109 | 版本 |