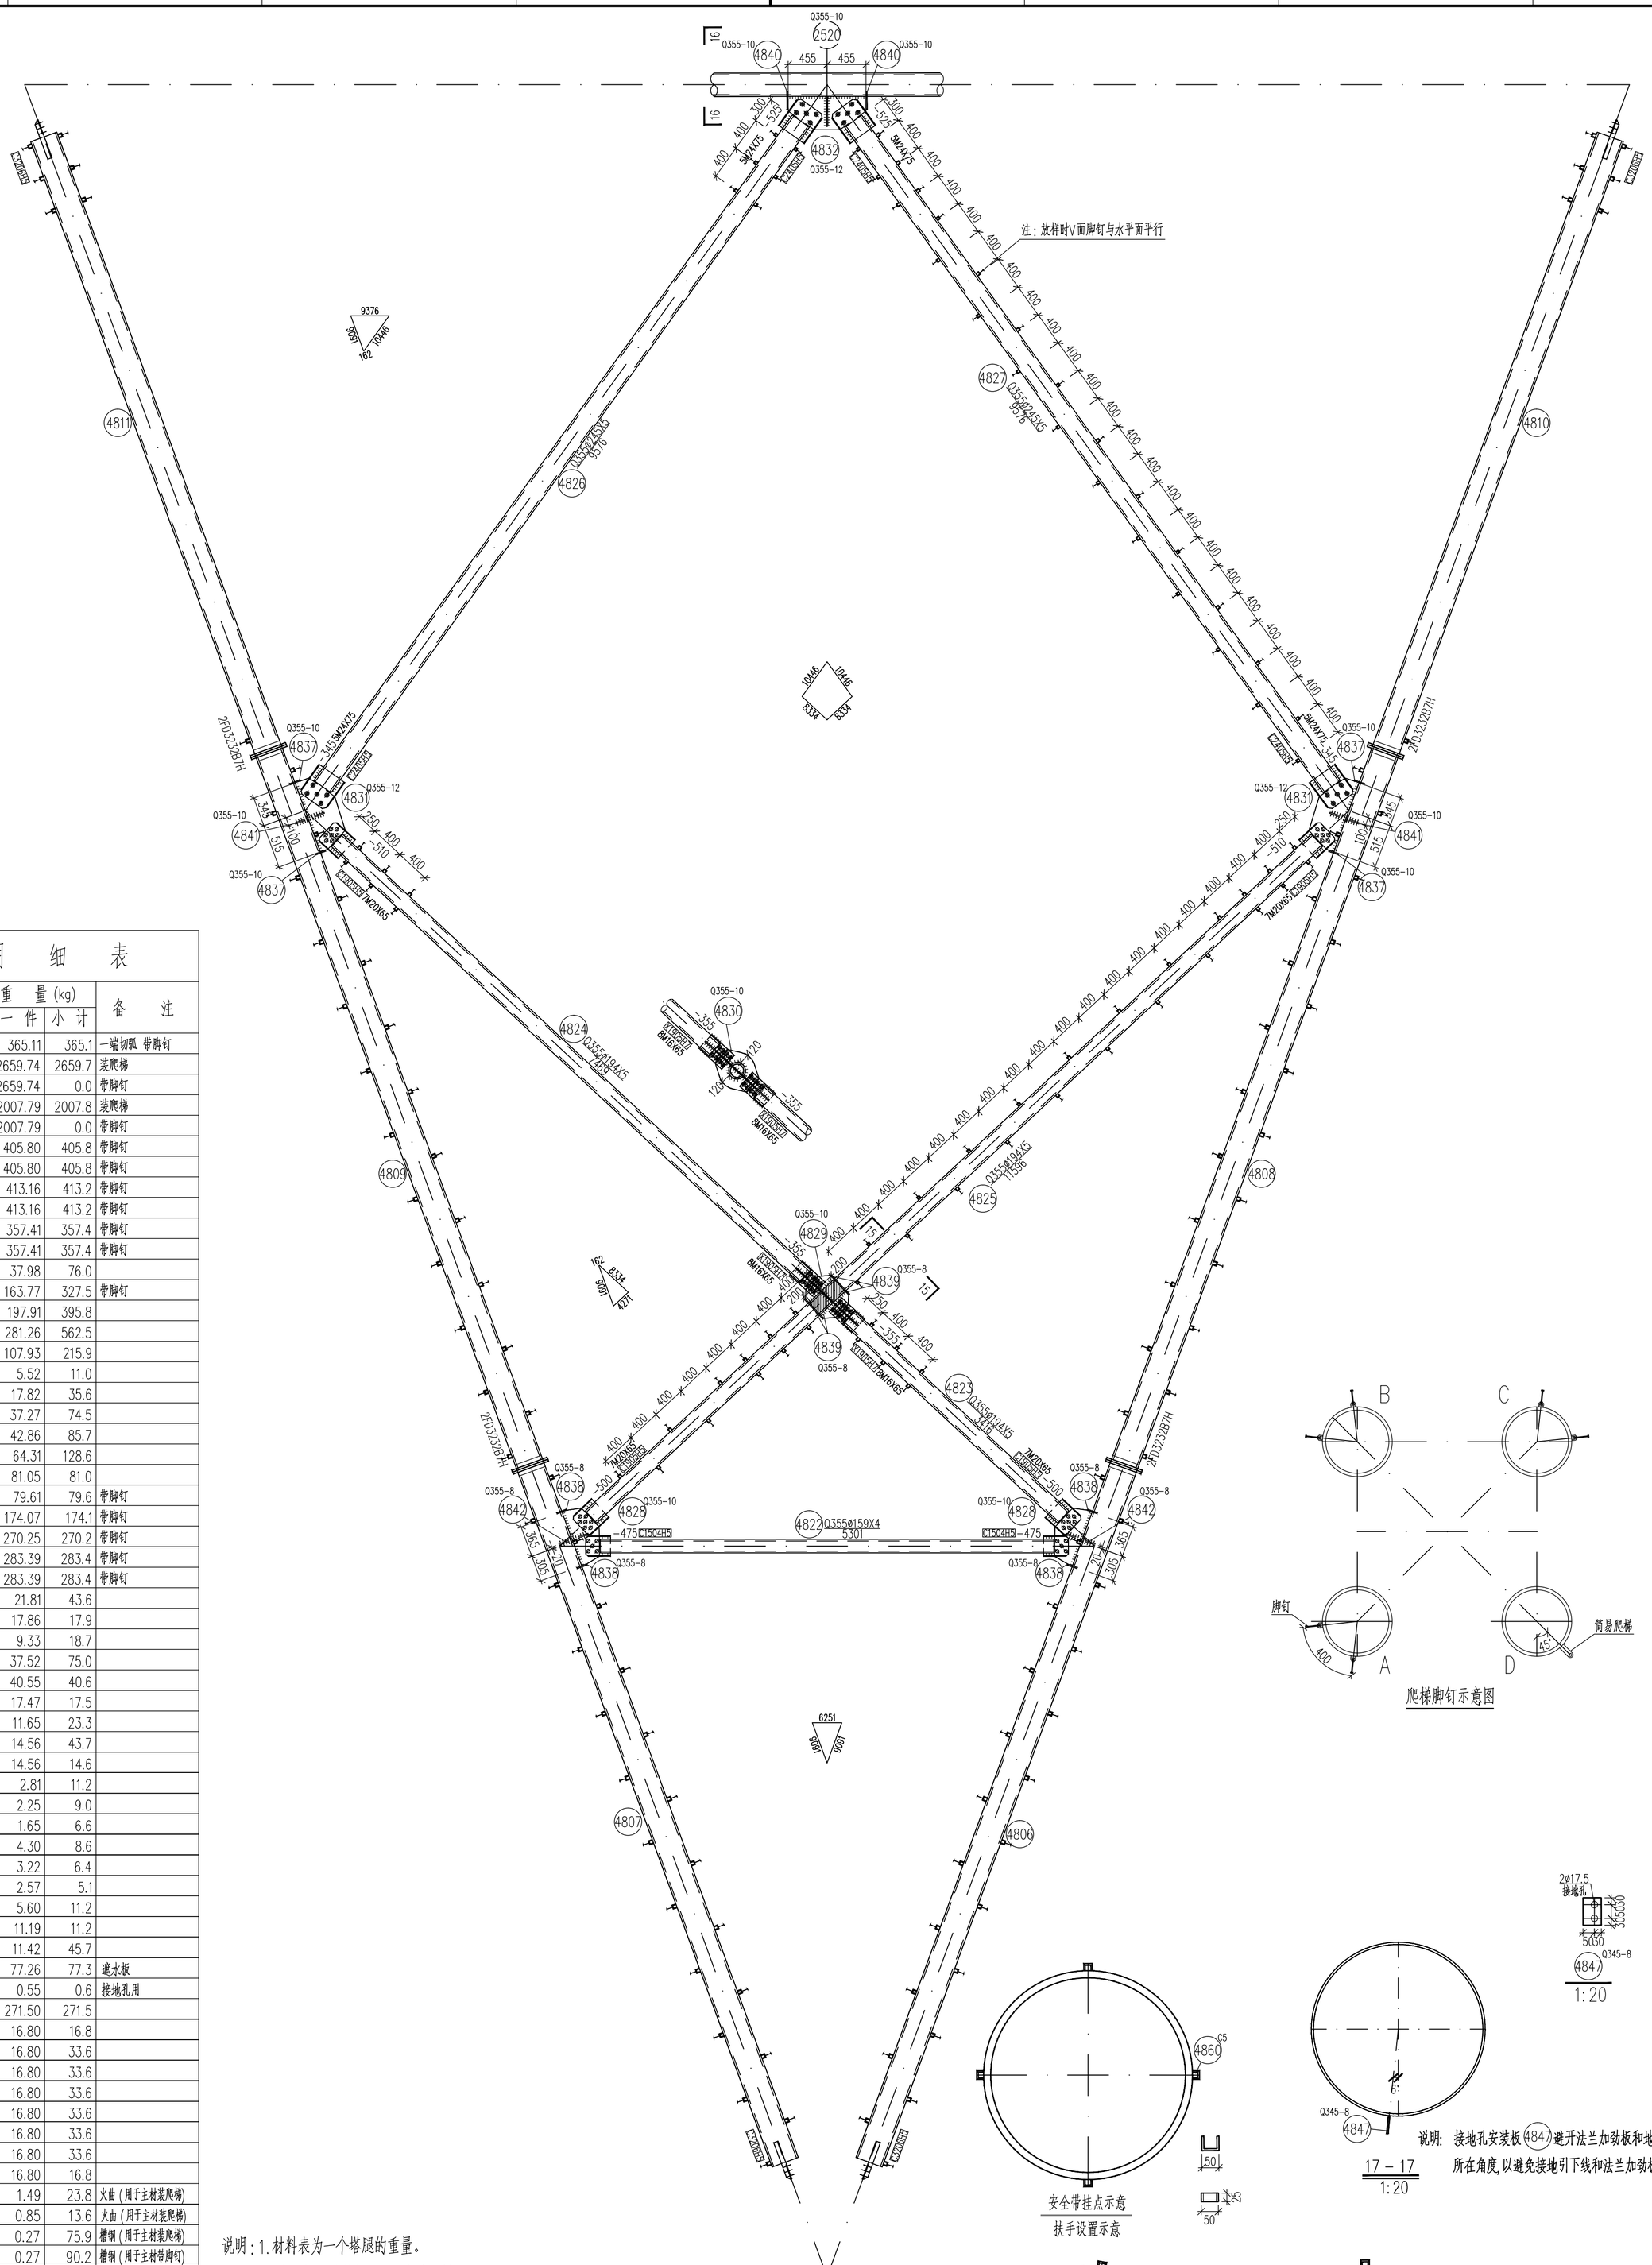


构件明细表						
编号	规格	长度(mm)	数量	重量(kg) 一件	重量(kg) 小计	备注
4801	Q420ø660X14	1637	1	365.11	365.1	一端切弧 带脚钉
4802	Q420ø660X14	11925	1	2659.74	2659.7	装爬梯
4803	Q420ø660X14	11925	0	2659.74	0.0	带脚钉
4804	Q420ø660X14	9002	1	2007.79	2007.8	装爬梯
4805	Q420ø660X14	9002	0	2007.79	0.0	带脚钉
4806	Q355ø325X6	8597	1	405.80	405.8	带脚钉
4807	Q355ø325X6	8597	1	405.80	405.8	带脚钉
4808	Q355ø325X6	8753	1	413.16	413.2	带脚钉
4809	Q355ø325X6	8753	1	413.16	413.2	带脚钉
4810	Q355ø325X6	7572	1	357.41	357.4	带脚钉
4811	Q355ø325X6	7572	1	357.41	357.4	带脚钉
4812	Q355ø114X4	3500	2	37.98	76.0	
4813	Q355ø194X5	7027	2	163.77	327.5	带脚钉
4814	Q355ø219X5	7500	2	197.91	395.8	
4815	Q355ø245X5	9504	2	281.26	562.5	
4816	Q355-16X609	1411	2	107.93	215.9	
4817	Q355-10X213	330	2	5.52	11.0	
4818	Q355-10X308	737	2	17.82	35.6	
4819	Q355-12X444	891	2	37.27	74.5	
4820	Q355-12X481	946	2	42.86	85.7	
4821	Q355-14X532	1100	2	64.31	128.6	
4822	Q355ø159X4	5301	1	81.05	81.0	
4823	Q355ø194X5	3416	1	79.61	79.6	带脚钉
4824	Q355ø194X5	7469	1	174.07	174.1	带脚钉
4825	Q355ø194X5	11596	1	270.25	270.2	带脚钉
4826	Q355ø245X5	9576	1	283.39	283.4	带脚钉
4827	Q355ø245X5	9576	1	283.39	283.4	带脚钉
4828	Q355-10X377	737	2	21.81	43.6	
4829	Q355-10X440	517	1	17.86	17.9	
4830	Q355-10X230	517	2	9.33	18.7	
4831	Q355-12X421	946	2	37.52	75.0	
4832	Q355-12X430	1001	1	40.55	40.6	
4833	Q355-12X135	1374	1	17.47	17.5	
4834	Q355-8X135	1374	2	11.65	23.3	
4835	Q355-10X135	1374	3	14.56	43.7	
4836	Q355-10X135	1374	1	14.56	14.6	
4837	Q355-10X70	512	4	2.81	11.2	
4838	Q355-8X70	512	4	2.25	9.0	
4839	Q355-8X60	439	4	1.65	6.6	
4840	Q355-10X150	365	2	4.30	8.6	
4841	Q355-10X200	205	2	3.22	6.4	
4842	Q355-8X200	205	2	2.57	5.1	
4843	Q355-12X180	330	2	5.60	11.2	
4844	Q355-12X180	660	1	11.19	11.2	
4845	Q355-10X294	495	4	11.42	45.7	
4846	-16X885	885	1	77.26	77.3	遮水板
4847	Q345-8X80	110	1	0.55	0.6	接地孔用
4848	Q420-32X1346	1346	1	271.50	271.5	
4849	Q355-16X343	390	1	16.80	16.8	
4850	Q355-16X343	390	2	16.80	33.6	
4851	Q355-16X343	390	2	16.80	33.6	
4852	Q355-16X343	390	2	16.80	33.6	
4853	Q355-16X343	390	2	16.80	33.6	
4854	Q355-16X343	390	2	16.80	33.6	
4855	Q355-16X343	390	2	16.80	33.6	
4856	Q355-16X343	390	1	16.80	16.8	
4857	Q345L63X5	310	16	1.49	23.8	火曲(用于主材装爬梯)
4858	Q355-6X100	180	16	0.85	13.6	火曲(用于主材装爬梯)
4859	C5	50	281	0.27	75.9	槽钢(用于主材装爬梯)
4859	C5	50	334	0.27	90.2	槽钢(用于主材带脚钉)
4860	C5	25	12	0.14	1.7	槽钢
4861	C5	50	8	0.27	2.2	槽钢
4862	Q355-14X210	550	1	12.69	12.7	
4863	Q355-38X104	104	3	3.23	9.7	
4864	Q355-10X100	115	2	0.90	1.8	
4865	Q355-6X50	100	1	0.24	0.2	
4866	Q355-12X80	450	2	3.39	6.8	
	C1104H5		4	3.44	13.8	
	C1504H5		2	6.52	13.0	
	C1905H5		8	11.34	90.7	
	X1905H7		2	17.90	71.6	
	C2105H5		4	14.54	58.2	
	C2405H5		8	17.27	138.2	
	C3206H5		4	31.43	125.7	
	FD3232B7H		8	16.80	134.4	
	FD6666B7D		5	116.50	582.5	
	T2105	–	2	11.50	23.0	主材安装爬梯
	T3930	–	1	20.70	20.7	主材安装爬梯
	T6980	–	2	36.20	72.4	主材安装爬梯
合计		12818.1 kg (用于主材带脚钉)				
合计		12957.3 kg (用于主材装爬梯)				

说明：1.材料表为一个塔腿的重量。

2.本段塔腿为铁塔D腿，安装爬梯，当为A、B、C腿时需焊接脚钉连接槽钢。

螺栓、脚钉、垫圈明细表						
名称	级别	规格	符号	数量	重量(kg)	备注
螺栓	6.8级	M16X45		64	10.8	用于主材装爬梯
		M16X65		32	6.4	
		M20X65		78	27.5	
	8.8级	M24X75		88	52.2	
		M20X100		88	43.6	法兰螺栓
		M39X175		56	198.9	法兰螺栓
		M39X195		28	104.7	法兰螺栓
脚钉	6.8级	M16X185	规格X个数	281	116.5	用于主材装爬梯
		M16X185		334	138.5	用于主材带脚钉
垫圈	Q235					
合计		571.8 kg (用于主材带脚钉)				
合计		560.6 kg (用于主材装爬梯)				

爬梯脚钉示意图

安全带挂点示意

扶手设置示意

站位平台示意(一)

站位平台示意(二)

说明：接地孔安装板(4847)避开法兰加劲板和地脚法兰螺栓所在角度，以避免接地引下线和法兰加劲板相碰

17 – 17
1:20

山东电力工程咨询院有限公司				浙江特高压交流环网工程线路 工程	施工图 设计阶段
批准	雷强	校核	习一丹	SZK31102A双回路直线塔 111.0-0.0m腿部结构图(2/2) 114.0-3.0m腿部结构图(2/2)	48
审核	高锡鹏	设计/勘测	潘胜龙		
比例	1:40	日期	2026年08月	图号 37-SA36901S-T0121-110	版本