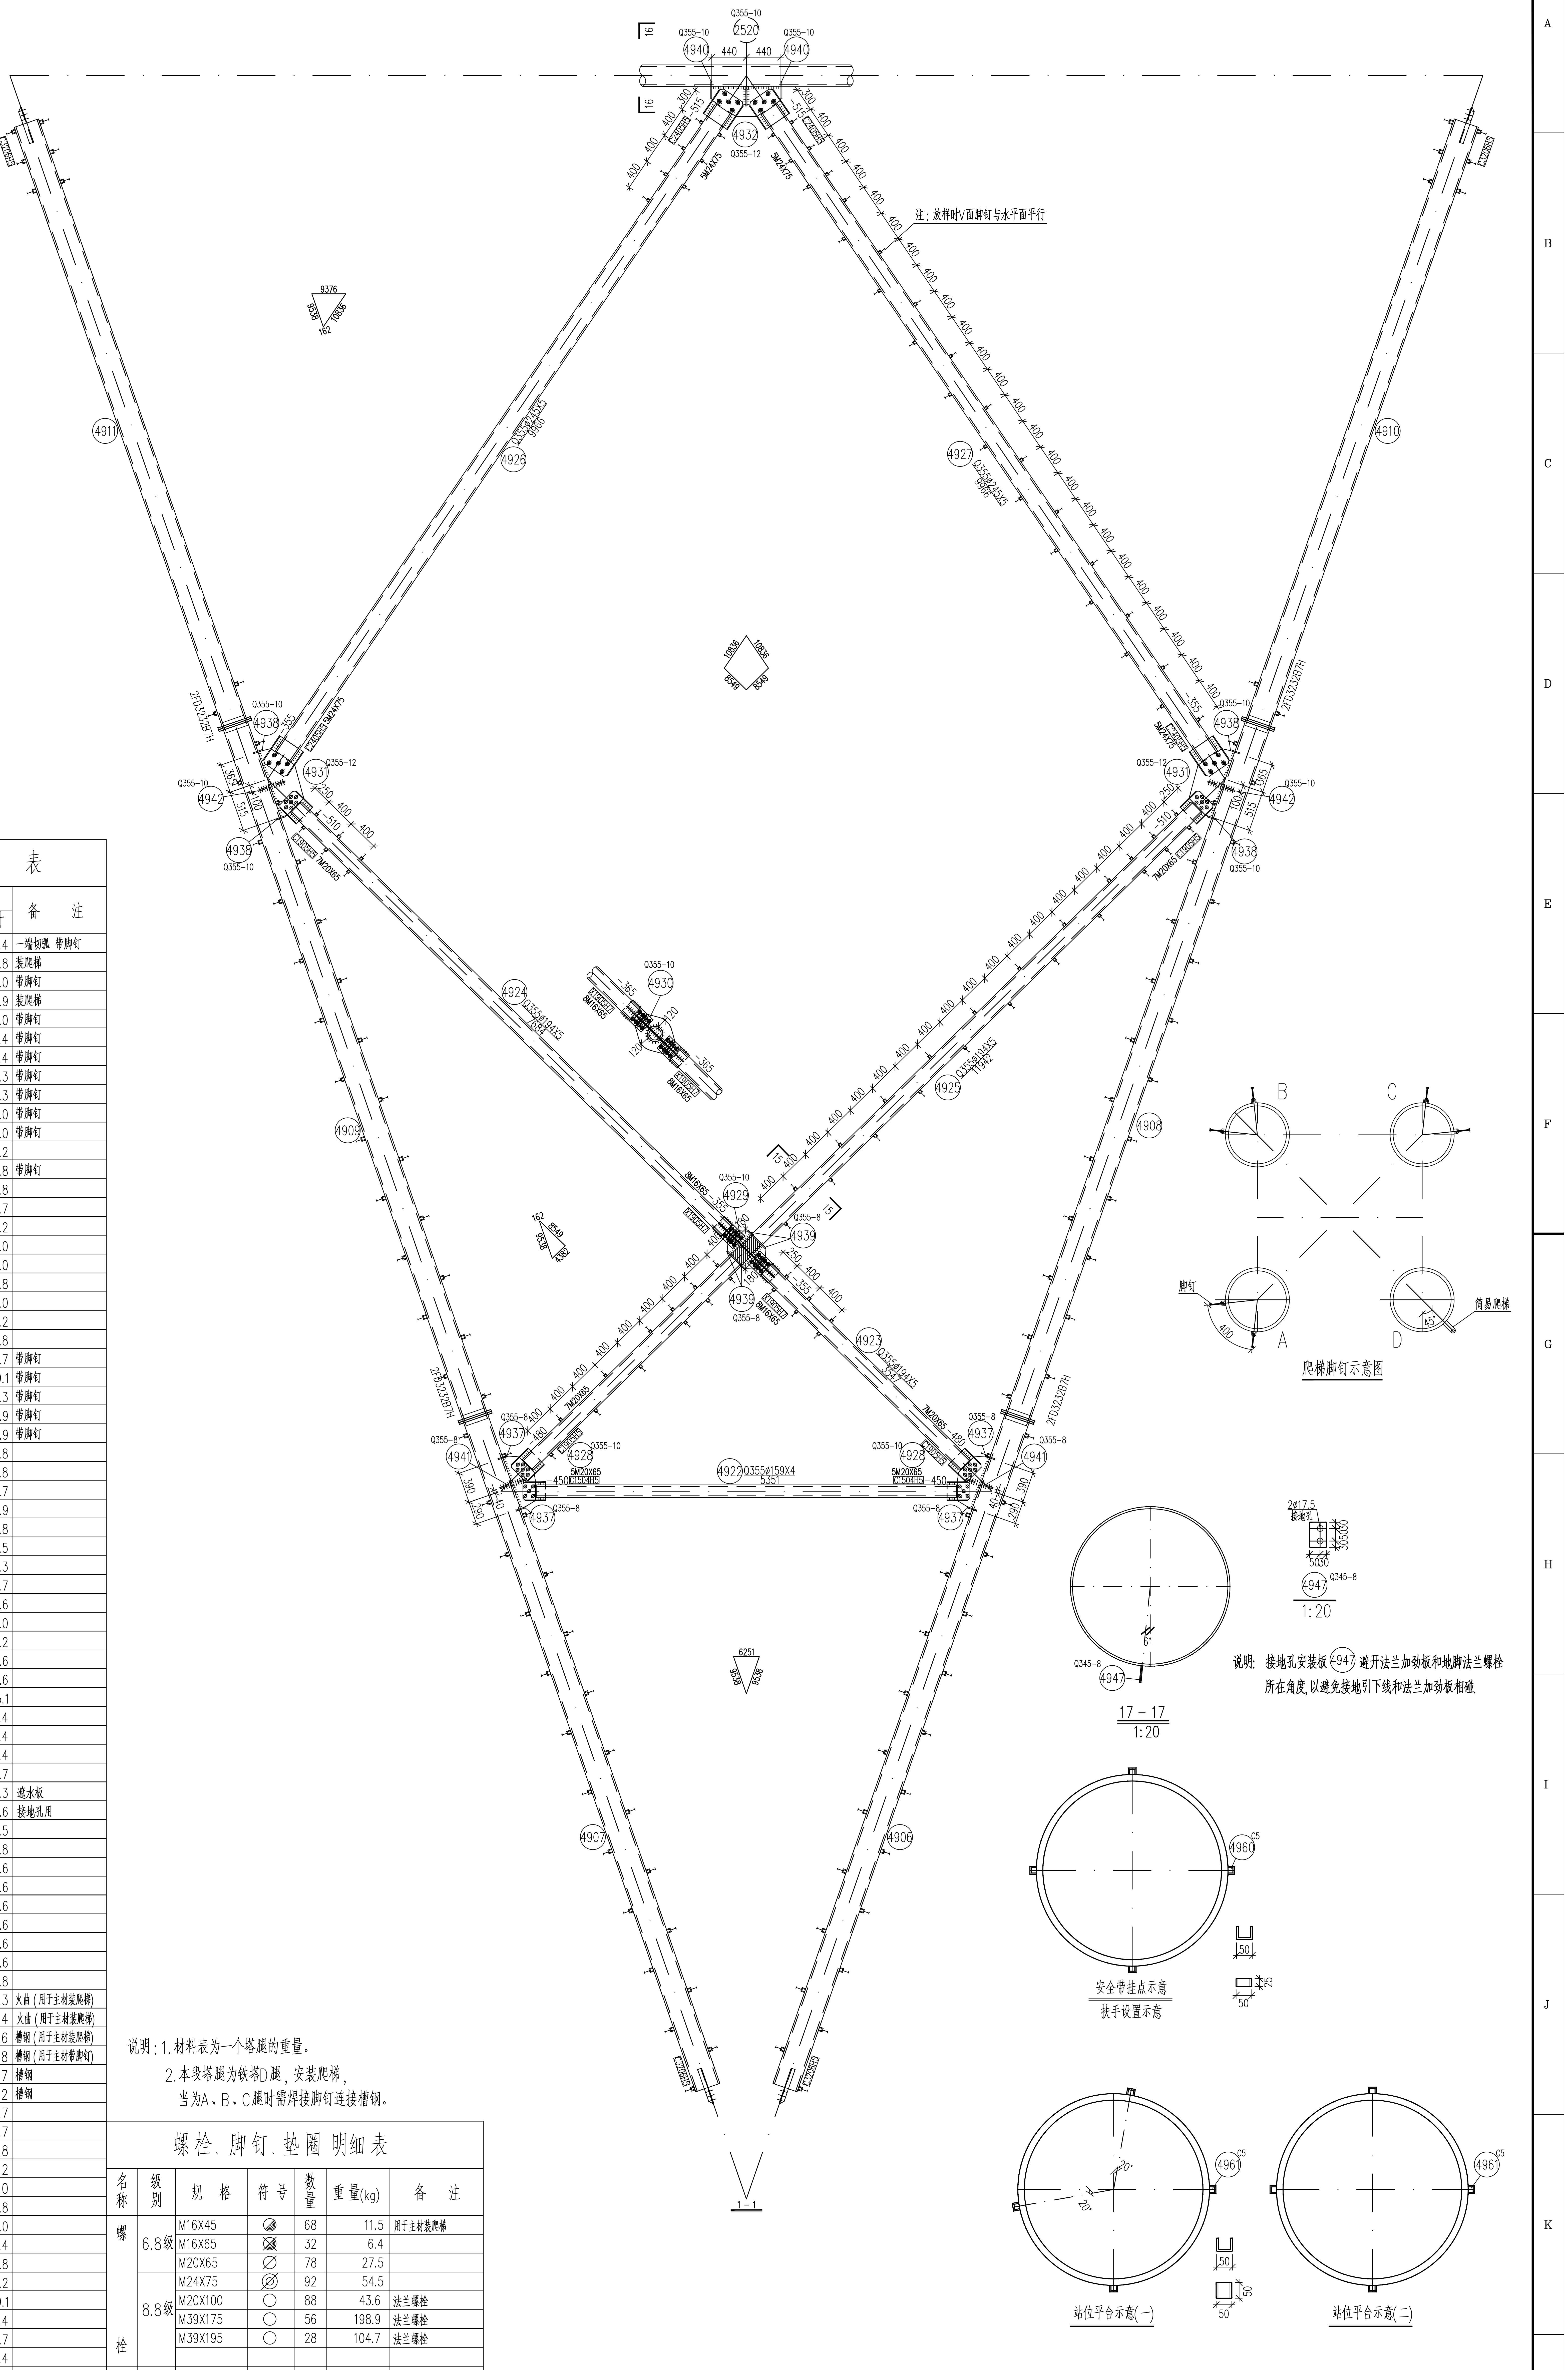

爬梯脚钉示意图

4947 Q345-8
1:20

17－17
1:20

说明：接地孔安装板④⑨④⑦避开法兰加劲板和地脚法兰螺栓所在角度，以避免接地引下线和法兰加劲板相碰。

安全带挂点示意

扶手设置示意

站位平台示意(一)

站位平台示意(二)

构　件　明　细　表

编号	规　格	长　度(mm)	数量	重　量(kg) 一　件	小　计	备　注
4901	Q420ø660X14	1737	1	387.42	387.4	一端切弧 带脚钉
4902	Q420ø660X14	11840	1	2640.78	2640.8	装爬梯
4903	Q420ø660X14	11840	0	2640.78	0.0	带脚钉
4904	Q420ø660X14	10509	1	2343.91	2343.9	装爬梯
4905	Q420ø660X14	10509	0	2343.91	0.0	带脚钉
4906	Q355ø325X6	8969	1	423.36	423.4	带脚钉
4907	Q355ø325X6	8969	1	423.36	423.4	带脚钉
4908	Q355ø325X6	9200	1	434.26	434.3	带脚钉
4909	Q355ø325X6	9200	1	434.26	434.3	带脚钉
4910	Q355ø325X6	8029	1	378.99	379.0	带脚钉
4911	Q355ø325X6	8029	1	378.99	379.0	带脚钉
4912	Q355ø114X4	3510	2	38.09	76.2	
4913	Q355ø194X5	7419	2	172.90	345.8	带脚钉
4914	Q355ø219X5	7500	2	197.91	395.8	
4915	Q355ø273X5	9815	2	324.35	648.7	
4916	Q355-16X614	1499	2	115.60	231.2	
4917	Q355-10X213	330	2	5.52	11.0	
4918	Q355-10X332	748	2	19.49	39.0	
4919	Q355-12X444	930	2	38.90	77.8	
4920	Q355-12X477	968	2	43.50	87.0	
4921	Q355-14X532	1139	2	66.59	133.2	
4922	Q355ø159X4	5351	1	81.82	81.8	
4923	Q355ø194X5	3547	1	82.66	82.7	带脚钉
4924	Q355ø194X5	7684	1	179.08	179.1	带脚钉
4925	Q355ø194X5	11942	1	278.31	278.3	带脚钉
4926	Q355ø245X5	9966	1	294.93	294.9	带脚钉
4927	Q355ø245X5	9966	1	294.93	294.9	带脚钉
4928	Q355-10X347	748	2	20.38	40.8	
4929	Q355-10X390	517	1	15.83	15.8	
4930	Q355-10X230	517	2	9.33	18.7	
4931	Q355-12X427	968	2	38.94	77.9	
4932	Q355-12X425	968	1	38.75	38.8	
4933	Q355-12X135	1374	1	17.47	17.5	
4934	Q355-8X135	1374	2	11.65	23.3	
4935	Q355-10X135	1374	3	14.56	43.7	
4936	Q355-10X135	1374	1	14.56	14.6	
4937	Q355-8X70	512	4	2.25	9.0	
4938	Q355-10X70	512	4	2.81	11.2	
4939	Q355-8X60	439	4	1.65	6.6	
4940	Q355-10X150	365	2	4.30	8.6	
4941	Q355-8X200	205	2	2.57	5.1	
4942	Q355-10X200	205	2	3.22	6.4	
4943	Q355-12X180	330	4	5.60	22.4	
4944	Q355-12X180	660	2	11.19	22.4	
4945	Q355-10X294	495	4	11.42	45.7	
4946	-16X885	885	1	77.26	77.3	遮水板
4947	Q345-8X80	110	1	0.55	0.6	接地孔用
4948	Q420-32X1346	1346	1	271.50	271.5	
4949	Q355-16X343	390	1	16.80	16.8	
4950	Q355-16X343	390	2	16.80	33.6	
4951	Q355-16X343	390	2	16.80	33.6	
4952	Q355-16X343	390	2	16.80	33.6	
4953	Q355-16X343	390	2	16.80	33.6	
4954	Q355-16X343	390	2	16.80	33.6	
4955	Q355-16X343	390	2	16.80	33.6	
4956	Q355-16X343	390	1	16.80	16.8	
4957	Q345L63X5	310	17	1.49	25.3	火曲（用于主材装爬梯）
4958	Q355-6X100	180	17	0.85	14.4	火曲（用于主材装爬梯）
4959	C5	50	295	0.27	79.6	槽钢（用于主材装爬梯）
4959	C5	50	351	0.27	94.8	槽钢（用于主材带脚钉）
4960	C5	25	12	0.14	1.7	槽钢
4961	C5	50	8	0.27	2.2	槽钢
4962	Q355-14X210	550	1	12.69	12.7	
4963	Q355-38X104	104	3	3.23	9.7	
4964	Q355-10X100	115	2	0.90	1.8	
4965	Q355-6X50	100	1	0.24	0.2	
4966	Q355-12X50	535	2	2.52	5.0	
	C1104H5		4	3.44	13.8	
	C1504H5		2	6.52	13.0	
	C1905H5		8	8.80	70.4	
	X1905H7		2	17.9	35.8	
	C2105H5		4	14.54	58.2	
	C2405H5		4	17.27	69.1	
	C2705H5		4	18.10	72.4	
	C3206H5		4	31.43	125.7	
	FD3232B7H		8	16.80	134.4	
	FD6666B7D		5	116.50	582.5	
	T2105		1	11.50	11.5	主材安装爬梯
	T3605	-	1	19.00	19.0	主材安装爬梯
	T3930	-	1	20.70	20.7	主材安装爬梯
	T6980	-	2	36.20	72.4	主材安装爬梯
合　计		13419.4 kg（用于主材带脚钉）				
合　计		13567.5 kg（用于主材装爬梯）				

说明：1.材料表为一个塔腿的重量。
2.本段塔腿为铁塔D腿，安装爬梯，
当为A、B、C腿时需焊接脚钉连接槽钢。

螺栓、脚钉、垫圈明细表

名称	级别	规　格	符　号	数量	重量(kg)	备　注
螺栓	6.8级	M16X45	◎	68	11.5	用于主材装爬梯
		M16X65	⊗	32	6.4	
		M20X65	∅	78	27.5	
	8.8级	M24X75	∅	92	54.5	
		M20X100	○	88	43.6	法兰螺栓
		M39X175	○	56	198.9	法兰螺栓
		M39X195	○	28	104.7	法兰螺栓
脚钉	6.8级	M16X185	⊖	295	122.3	用于主材装爬梯
		M16X185		351	145.5	用于主材带脚钉
垫圈	Q235		规格X个数			
合　计		581.1 kg（用于主材带脚钉）				
合　计		569.4 kg（用于主材装爬梯）				

山东电力工程咨询院有限公司

浙江特高压交流环网工程线路 工程				施工图	设计阶段
批　准	雷强	校　核	马一丹	SZK31102A双回路直线塔 114.0-1.5m腿部结构图(2/2) 117.0-4.5m腿部结构图(2/2)	49
审　核	高锡鹏				
		设计/勘测	潘胜光		
比　例	1:40	日　期	2026年 08月	图　号 37-SA36901S-T0121-112	版本