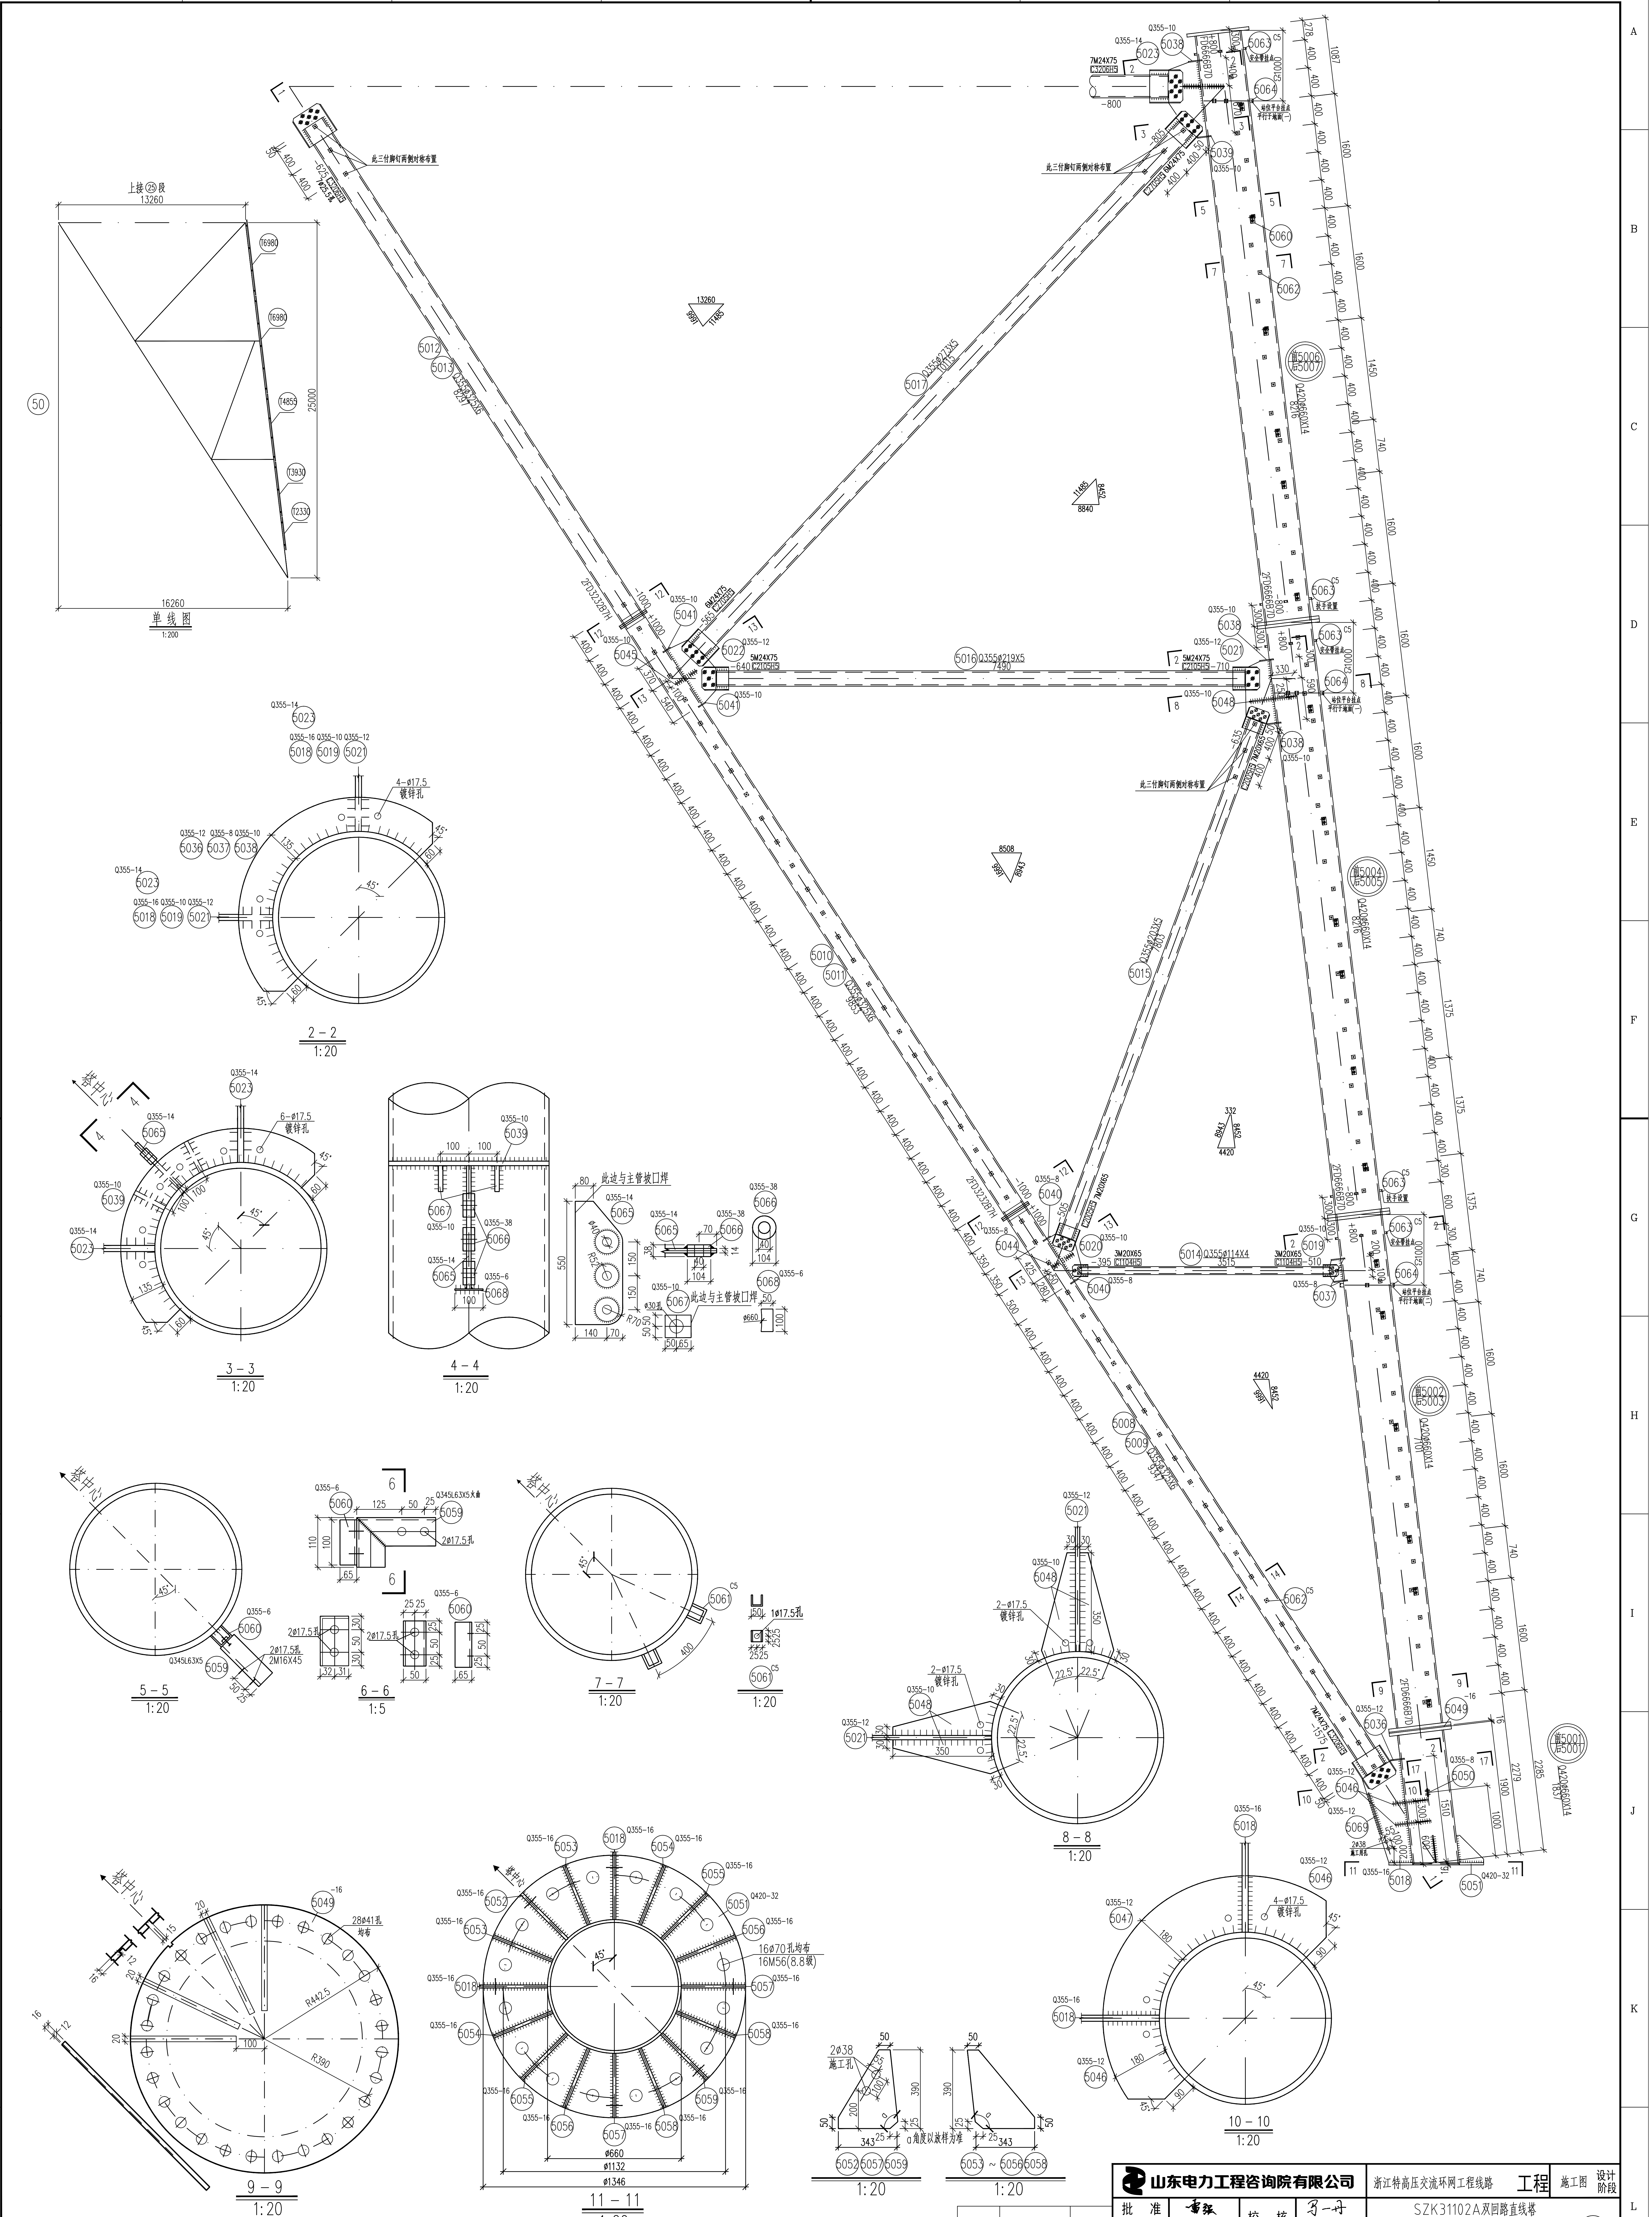

山东电力工程咨询院有限公司

浙江特高压交流环网工程线路 工程

施工图 设计阶段

批　准	雷强	校　核	马一丹
审　核	高锡鹏		
		设计/勘测	潘胜光
比　例	1:40	日　期	2026年 08月

SZK31102A双回路直线塔

114.0-0.0m腿部结构图(1/2)

117.0-3.0m腿部结构图(1/2)

(50)

图　号 37-SA36901S-T0121-113 版本

专业	会签	日期
电气	赵庆周	2026.08