构 件 明 细 表


编号	规 格	长度(mm)	数量	重量(kg) 一件	重量(kg) 小计	备 注
5001	Q420ø660X14	1837	1	409.72	409.7	一端切弧 带脚钉
5002	Q420ø660X14	7101	1	1583.80	1583.8	装爬梯
5003	Q420ø660X14	7101	0	1583.80	0.0	带脚钉
5004	Q420ø660X14	8216	1	1832.49	1832.5	装爬梯
5005	Q420ø660X14	8216	0	1832.49	0.0	带脚钉
5006	Q420ø660X14	8216	1	1832.49	1832.5	装爬梯
5007	Q420ø660X14	8216	0	1832.49	0.0	带脚钉
5008	Q355ø325X6	9347	1	441.20	441.2	带脚钉
5009	Q355ø325X6	9347	1	441.20	441.2	带脚钉
5010	Q355ø325X6	9853	1	465.08	465.1	带脚钉
5011	Q355ø325X6	9853	1	465.08	465.1	带脚钉
5012	Q355ø325X6	8297	1	391.64	391.6	带脚钉
5013	Q355ø325X6	8297	1	391.64	391.6	带脚钉
5014	Q355ø114X4	3515	2	38.14	76.3	
5015	Q355ø203X5	7803	2	190.51	381.0	带脚钉
5016	Q355ø219X5	7490	2	197.64	395.3	
5017	Q355ø273X5	10115	2	334.26	668.5	
5018	Q355-16X619	1583	2	123.07	246.1	
5019	Q355-10X213	330	2	5.52	11.0	
5020	Q355-10X342	776	2	20.83	41.7	
5021	Q355-12X462	979	2	42.61	85.2	
5022	Q355-12X482	1001	2	45.45	90.9	
5023	Q355-14X440	737	2	35.64	71.3	
5024	Q355ø159X4	5361	1	81.97	82.0	
5025	Q355ø203X5	3587	1	87.58	87.6	带脚钉
5026	Q355ø203X5	7822	1	190.97	191.0	带脚钉
5027	Q355ø203X5	4947	1	120.78	120.8	带脚钉
5028	Q355ø203X5	7182	1	175.35	175.4	带脚钉
5029	Q355ø273X5	10416	1	344.21	344.2	带脚钉
5030	Q355ø273X5	10416	1	344.21	344.2	带脚钉
5031	Q355-10X354	776	2	21.56	43.1	
5032	Q355-10X440	594	1	20.52	20.5	
5033	Q355-10X265	594	2	12.36	24.7	
5034	Q355-12X426	1023	2	41.05	82.1	
5035	Q355-12X410	935	1	36.11	36.1	
5036	Q355-12X135	1374	1	17.47	17.5	
5037	Q355-8X135	1374	2	11.65	23.3	
5038	Q355-10X135	1374	3	14.56	43.7	
5039	Q355-10X135	1374	1	14.56	14.6	
5040	Q355-8X70	512	2	2.25	4.5	
5041	Q355-10X70	512	2	2.81	5.6	
5042	Q355-8X60	454	4	1.71	6.8	
5043	Q355-10X120	340	2	3.20	6.4	
5044	Q355-8X200	205	2	2.57	5.1	
5045	Q355-10X200	205	2	3.22	6.4	
5046	Q355-12X180	330	4	5.60	22.4	
5047	Q355-12X180	660	2	11.19	22.4	
5048	Q355-10X294	495	4	11.42	45.7	
5049	-16X885	885	1	77.26	77.3	遮水板
5050	Q345-8X80	110	1	0.55	0.6	接地孔用
5051	Q420-32X1346	1346	1	271.50	271.5	
5052	Q355-16X343	390	1	16.80	16.8	
5053	Q355-16X343	390	2	16.80	33.6	
5054	Q355-16X343	390	2	16.80	33.6	
5055	Q355-16X343	390	2	16.80	33.6	
5056	Q355-16X343	390	2	16.80	33.6	
5057	Q355-16X343	390	2	16.80	33.6	
5058	Q355-16X343	390	2	16.80	33.6	
5059	Q355-16X343	390	1	16.80	16.8	
5060	Q345L63X5	310	18	1.49	26.8	火曲(用于主材装爬梯)
5061	Q355-6X100	180	18	0.85	15.3	火曲(用于主材装爬梯)
5062	C5	50	305	0.27	82.4	槽钢(用于主材装爬梯)
5062	C5	50	365	0.27	98.6	槽钢(用于主材带脚钉)
5063	C5	25	20	0.14	2.8	槽钢
5064	C5	50	12	0.27	3.2	槽钢
5065	Q355-14X210	550	1	12.69	12.7	
5066	Q355-38X104	104	3	3.23	9.7	
5067	Q355-10X100	115	2	0.90	1.8	
5068	Q355-6X50	100	1	0.24	0.2	
5069	Q355-12X80	620	2	4.67	9.3	
	C1104H5		4	3.44	13.8	
	C1504H5		2	6.52	13.0	
	X2005H7		2	24.4	48.8	
	C2005H5		8	9.74	77.9	
	C2105H5		4	14.54	58.2	
	C2705H5		8	18.10	144.8	
	C3206H5		4	31.43	125.7	
	FD2020B7H		2	8.60	17.2	
	FD3232B7H		8	16.80	134.4	
	FD6666B7D		7	116.50	815.5	
	T2330		1	12.40	12.4	主材安装爬梯
	T3930	-	1	20.70	20.7	主材安装爬梯
	T4855	-	1	25.00	25.0	主材安装爬梯
	T6980	-	2	36.20	72.4	主材安装爬梯
合 计		14269.9 kg(用于主材带脚钉)				
合 计		14426.3 kg(用于主材装爬梯)				

说明:1.材料表为一个塔腿的重量。

2.本段塔腿为铁塔D腿,安装爬梯,
当为A、B、C腿时需焊接脚钉连接槽钢。

螺栓、脚钉、垫圈明细表

名称	级别	规 格	符号	数量	重量(kg)	备 注
螺栓	6.8级	M16X45		72	12.1	用于主材装爬梯
		M16X65		48	9.6	
		M20X65		78	27.5	
	8.8级	M24X75		96	56.9	
		M20X90		12	5.7	法兰螺栓
		M20X100		88	43.6	法兰螺栓
		M39X175		84	298.3	法兰螺栓
		M39X195		28	104.7	法兰螺栓
脚钉	6.8级	M16X185		305	126.5	用于主材装爬梯
		M16X185		365	151.3	用于主材带脚钉
垫圈	Q235		规格X个数			
合 计				697.6 kg (用于主材带脚钉)		
合 计				684.9 kg (用于主材装爬梯)		

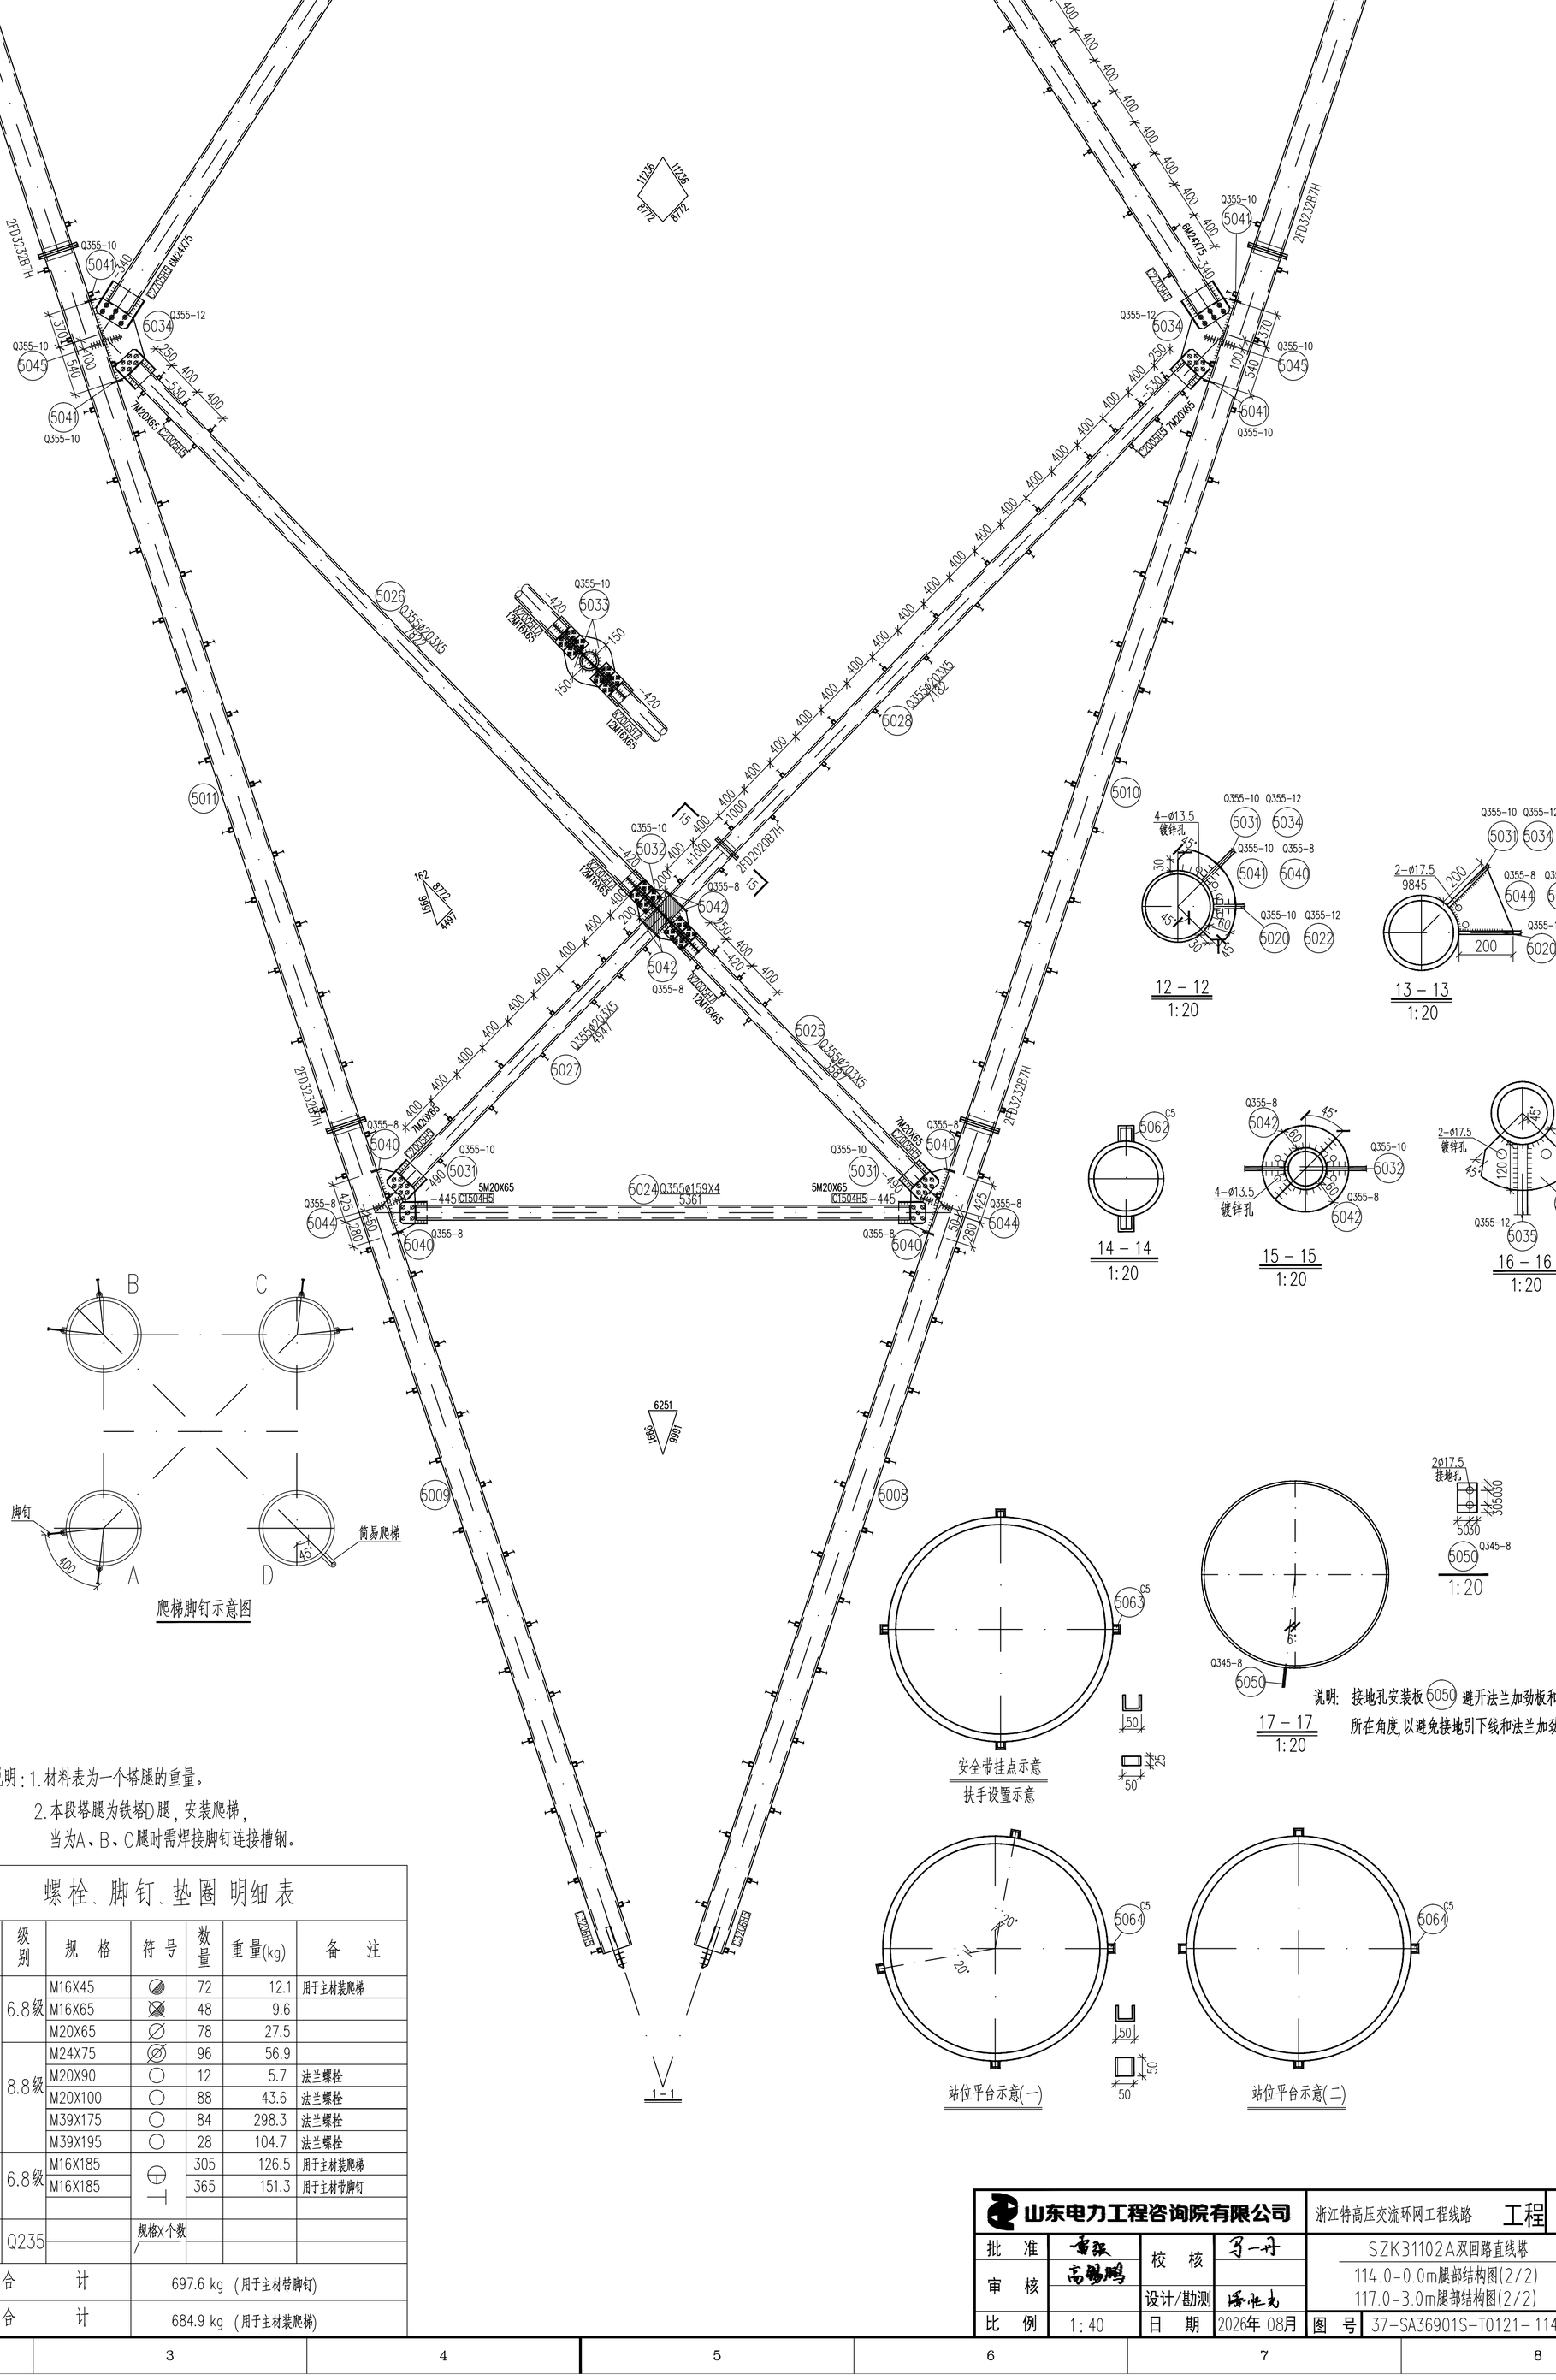

爬梯脚钉示意图

安全带挂点示意
扶手设置示意

站位平台示意(一)

站位平台示意(二)

12 – 12
1:20

13 – 13
1:20

14 – 14
1:20

15 – 15
1:20

16 – 16
1:20

17 – 17
1:20

说明: 接地孔安装板(5050)避开法兰加劲板和地脚法兰螺栓所在角度,以避免接地引下线和法兰加劲板相碰

山东电力工程咨询院有限公司				浙江特高压交流环网工程线路 工程	施工图 设计阶段
批 准	雷强	校 核	马一丹	SZK31102A双回路直线塔	
审 核	高锡鹏			114.0-0.0m腿部结构图(2/2)	50
		设计/勘测	陈龙龙	117.0-3.0m腿部结构图(2/2)	
比 例	1:40	日 期	2026年 08月	图 号 37-SA36901S-T0121-114	版本