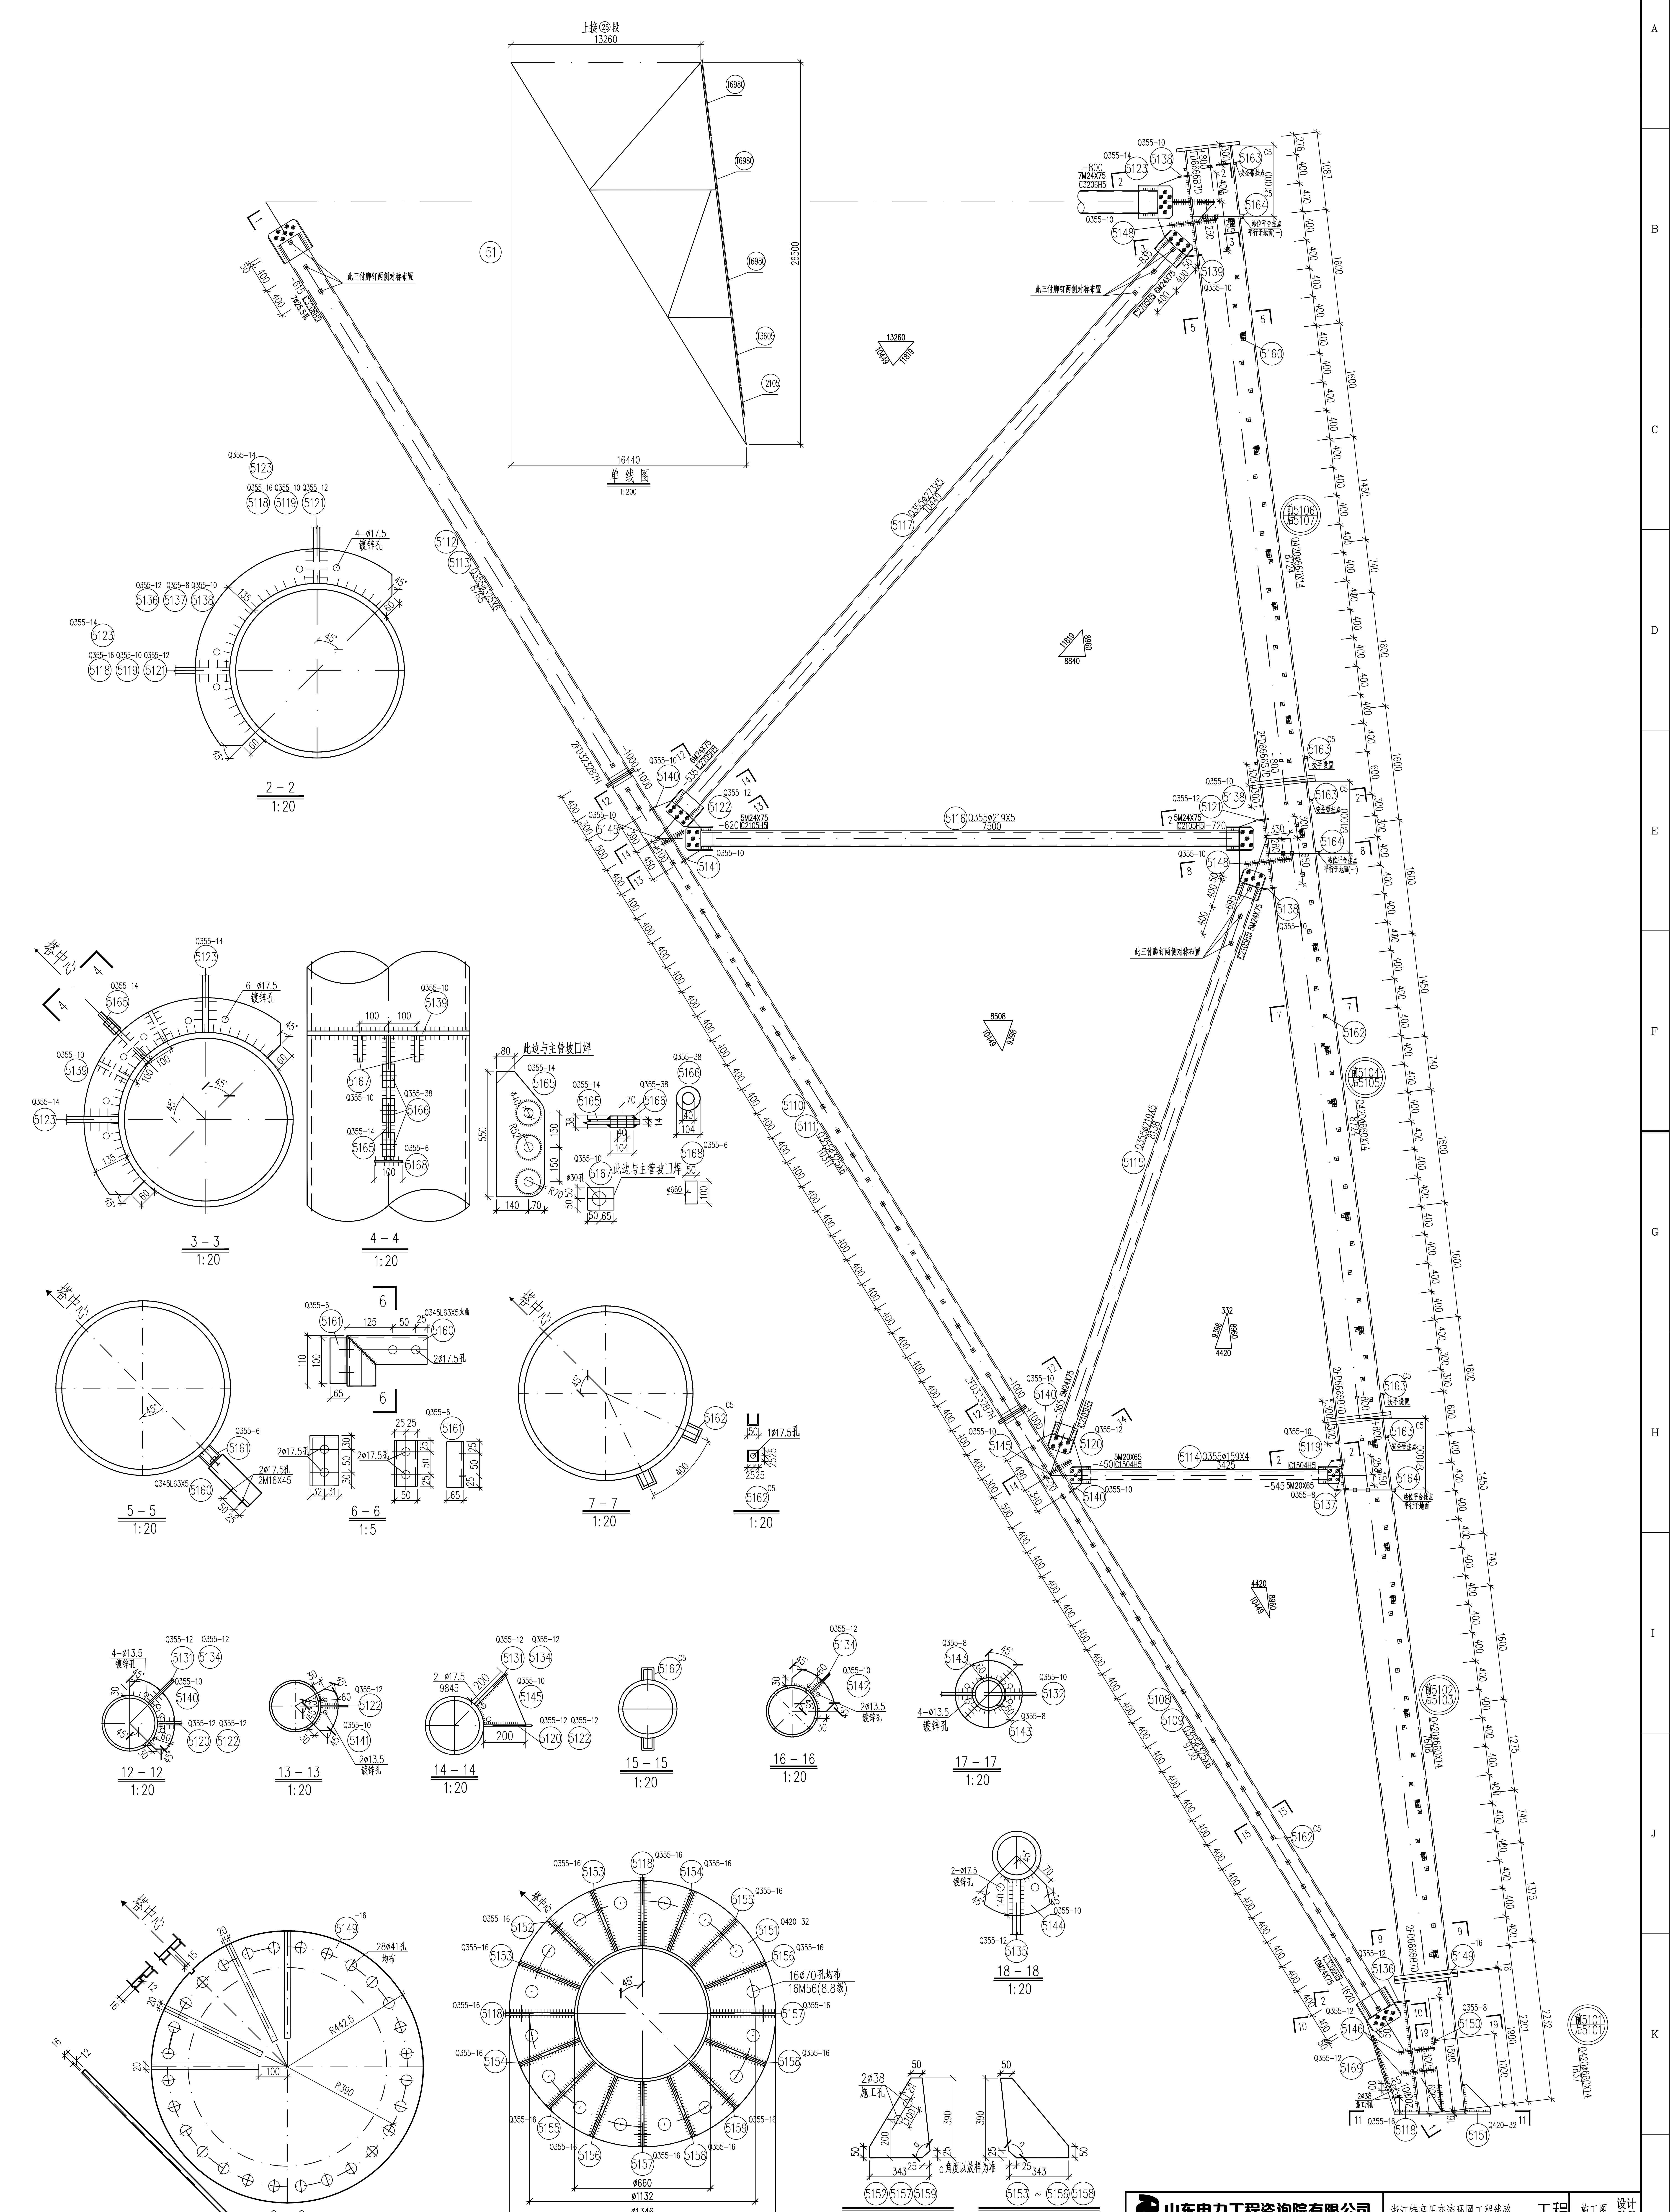

单线图 1:200

2－2 1:20

3－3 1:20

4－4 1:20

5－5 1:20

6－6 1:5

7－7 1:20

5162 1:20

12－12 1:20

13－13 1:20

14－14 1:20

15－15 1:20

16－16 1:20

17－17 1:20

18－18 1:20

9－9 1:20

11－11 1:20

5152 5157 5159 1:20

5153 ~ 5156 5158 1:20

山东电力工程咨询院有限公司				浙江特高压交流环网工程线路 工程	施工图	设计阶段
批准	雷强	校核	马一丹	SZK31102A双回路直线塔 117.0-1.5m塔腿结构图(1/2)		㊿
审核	高锡鹏					
		设计/勘测	潘胜光			
比例	1:40	日期	2026年 08月	图号	37-SA36901S-T0121-115	版本

电气	赵庆周	2026.08
专业	会签	日期