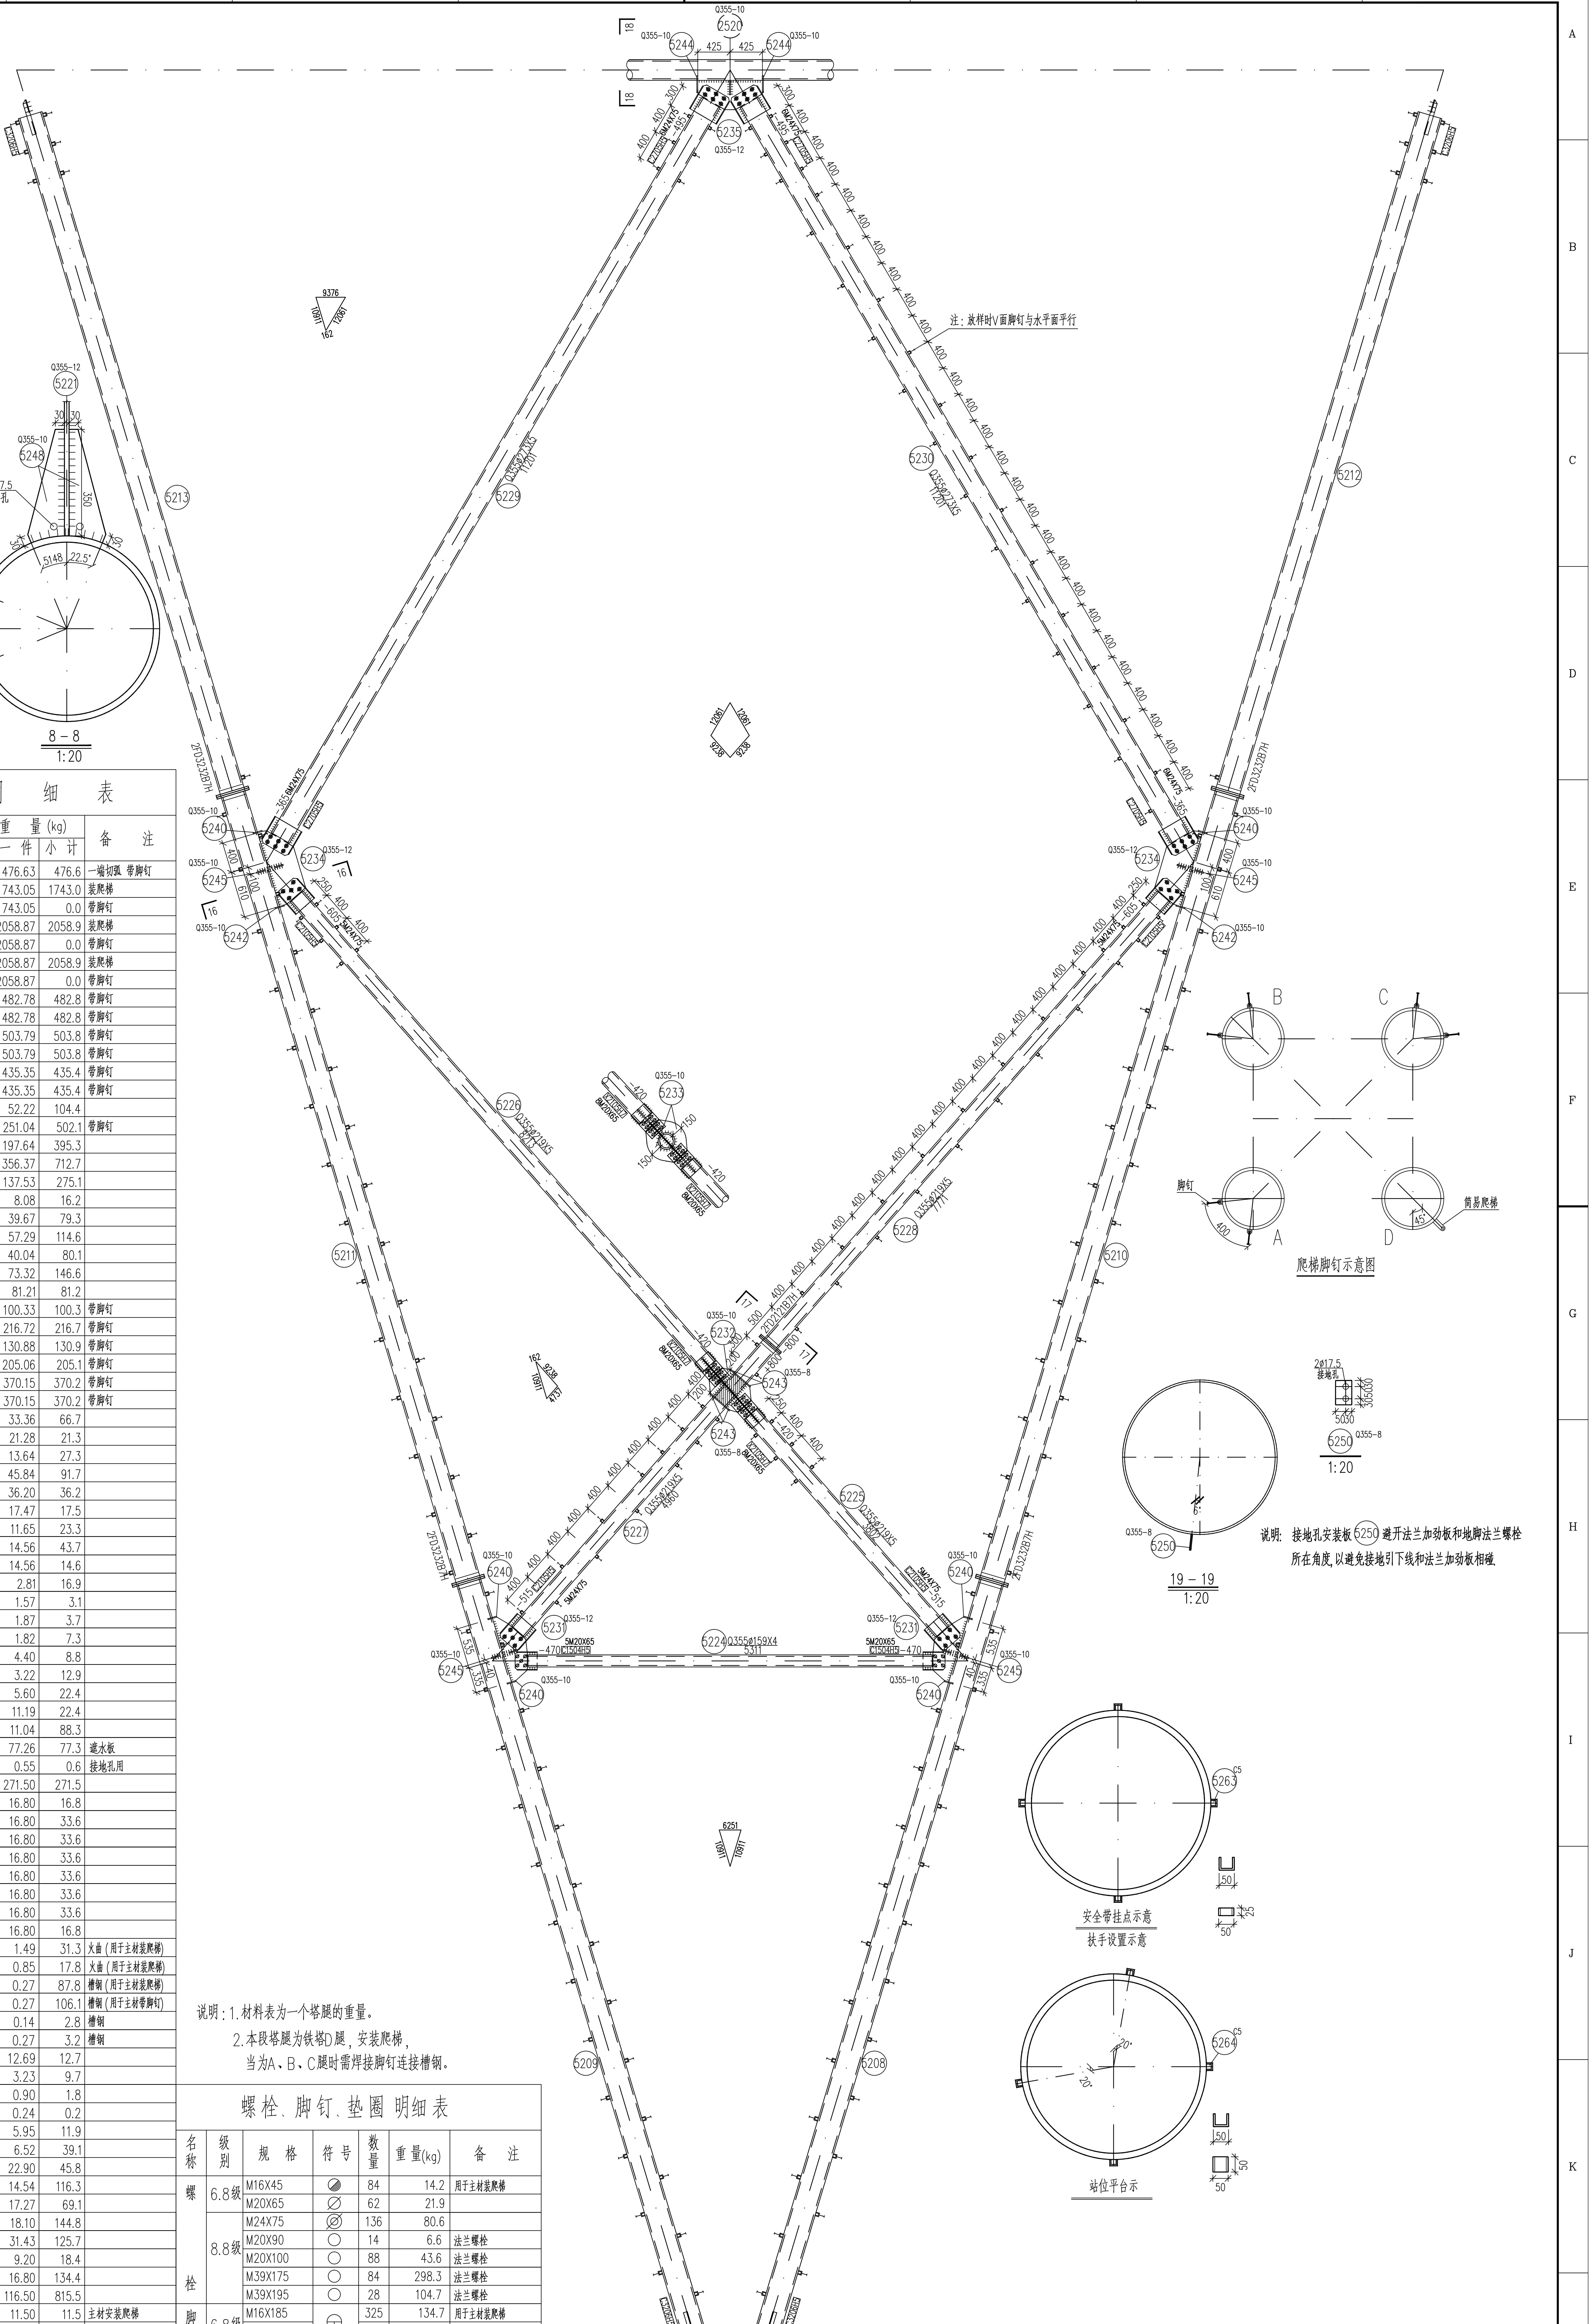

说明：接地孔安装板⑸250避开法兰加劲板和地脚法兰螺栓所在角度，以避免接地引下线和法兰加劲板相碰.

构 件 明 细 表

编号	规　格	长 度 (mm)	数量	重 量(kg) 一 件	重 量(kg) 小 计	备　注
5201	Q420ø660X14	2137	1	476.63	476.6	一端切弧 带脚钉
5202	Q420ø660X14	7815	1	1743.05	1743.0	装爬梯
5203	Q420ø660X14	7815	0	1743.05	0.0	带脚钉
5204	Q420ø660X14	9231	1	2058.87	2058.9	装爬梯
5205	Q420ø660X14	9231	0	2058.87	0.0	带脚钉
5206	Q420ø660X14	9231	1	2058.87	2058.9	装爬梯
5207	Q420ø660X14	9231	0	2058.87	0.0	带脚钉
5208	Q355ø325X6	10228	1	482.78	482.8	带脚钉
5209	Q355ø325X6	10228	1	482.78	482.8	带脚钉
5210	Q355ø325X6	10673	1	503.79	503.8	带脚钉
5211	Q355ø325X6	10673	1	503.79	503.8	带脚钉
5212	Q355ø325X6	9223	1	435.35	435.4	带脚钉
5213	Q355ø325X6	9223	1	435.35	435.4	带脚钉
5214	Q355ø159X4	3415	2	52.22	104.4	
5215	Q355ø245X5	8483	2	251.04	502.1	带脚钉
5216	Q355ø219X5	7490	2	197.64	395.3	
5217	Q355ø273X5	10784	2	356.37	712.7	
5218	Q355-16X625	1752	2	137.53	275.1	
5219	Q355-10X234	440	2	8.08	16.2	
5220	Q355-12X440	957	2	39.67	79.3	
5221	Q355-12X534	1139	2	57.29	114.6	
5222	Q355-12X457	930	2	40.04	80.1	
5223	Q355-14X532	1254	2	73.32	146.6	
5224	Q355ø159X4	5311	1	81.21	81.2	
5225	Q355ø219X5	3802	1	100.33	100.3	带脚钉
5226	Q355ø219X5	8213	1	216.72	216.7	带脚钉
5227	Q355ø219X5	4960	1	130.88	130.9	带脚钉
5228	Q355ø219X5	7771	1	205.06	205.1	带脚钉
5229	Q355ø273X5	11201	1	370.15	370.2	带脚钉
5230	Q355ø273X5	11201	1	370.15	370.2	带脚钉
5231	Q355-12X370	957	2	33.36	66.7	
5232	Q355-10X440	616	1	21.28	21.3	
5233	Q355-10X282	616	2	13.64	27.3	
5234	Q355-12X438	1111	2	45.84	91.7	
5235	Q355-12X411	935	1	36.20	36.2	
5236	Q355-12X135	1374	1	17.47	17.5	
5237	Q355-8X135	1374	2	11.65	23.3	
5238	Q355-10X135	1374	3	14.56	43.7	
5239	Q355-10X135	1374	1	14.56	14.6	
5240	Q355-10X70	512	6	2.81	16.9	
5241	Q355-10X70	285	2	1.57	3.1	
5242	Q355-10X70	341	2	1.87	3.7	
5243	Q355-8X60	482	4	1.82	7.3	
5244	Q355-10X150	374	2	4.40	8.8	
5245	Q355-10X200	205	4	3.22	12.9	
5246	Q355-12X180	330	4	5.60	22.4	
5247	Q355-12X180	660	2	11.19	22.4	
5248	Q355-10X284	495	8	11.04	88.3	
5249	-16X885	885	1	77.26	77.3	遮水板
5250	Q345-8X80	110	1	0.55	0.6	接地孔用
5251	Q420-32X1346	1346	1	271.50	271.5	
5252	Q355-16X343	390	1	16.80	16.8	
5253	Q355-16X343	390	2	16.80	33.6	
5254	Q355-16X343	390	2	16.80	33.6	
5255	Q355-16X343	390	2	16.80	33.6	
5256	Q355-16X343	390	2	16.80	33.6	
5257	Q355-16X343	390	2	16.80	33.6	
5258	Q355-16X343	390	2	16.80	33.6	
5259	Q355-16X343	390	1	16.80	16.8	
5260	Q345L63X5	310	21	1.49	31.3	火曲（用于主材装爬梯）
5261	Q355-6X100	180	21	0.85	17.8	火曲（用于主材装爬梯）
5262	C5	50	325	0.27	87.8	槽钢（用于主材装爬梯）
5262	C5	50	393	0.27	106.1	槽钢（用于主材带脚钉）
5263	C5	25	20	0.14	2.8	槽钢
5264	C5	50	12	0.27	3.2	槽钢
5265	Q355-14X210	550	1	12.69	12.7	
5266	Q355-38X104	104	3	3.23	9.7	
5267	Q355-10X100	115	2	0.90	1.8	
5268	Q355-6X50	100	1	0.24	0.2	
5269	Q345-12X80	790	2	5.95	11.9	
	C1504H5		6	6.52	39.1	
	X2105H7		2	22.90	45.8	
	C2105H5		8	14.54	116.3	
	C2405H5		4	17.27	69.1	
	C2705H5		8	18.10	144.8	
	C3206H5		4	31.43	125.7	
	FD2121B7H		2	9.20	18.4	
	FD3232B7H		8	16.80	134.4	
	FD6666B7D		7	116.50	815.5	
	T2105	-	1	11.50	11.5	主材安装爬梯
	T2330	-	1	12.40	12.4	主材安装爬梯
	T3930	-	3	20.70	62.1	主材安装爬梯
	T5530	-	1	28.80	28.8	主材安装爬梯
	T6980	-	1	36.20	36.2	主材安装爬梯
合　计		15852.6 kg（用于主材带脚钉）				
合　计		16034.4 kg（用于主材装爬梯）				

说明：1.材料表为一个塔腿的重量。

2.本段塔腿为铁塔D腿，安装爬梯，

当为A、B、C腿时需焊接脚钉连接槽钢。

螺栓、脚钉、垫圈明细表

名称	级别	规　格	符号	数量	重量(kg)	备　注
螺栓	6.8级	M16X45	◎	84	14.2	用于主材装爬梯
		M20X65	∅	62	21.9	
	8.8级	M24X75	∅	136	80.6	
		M20X90	○	14	6.6	法兰螺栓
		M20X100	○	88	43.6	法兰螺栓
		M39X175	○	84	298.3	法兰螺栓
		M39X195	○	28	104.7	法兰螺栓
脚钉	6.8级	M16X185	⊖	325	134.7	用于主材装爬梯
		M16X185		393	162.9	用于主材带脚钉
垫圈	Q235		规格X个数			
合　计			718.6 kg （用于主材带脚钉）			
合　计			704.6 kg （用于主材装爬梯）			

山东电力工程咨询院有限公司				浙江特高压交流环网工程线路　工程	施工图	设计阶段
批　准		校　核	马一丹	SZK31102A双回路直线塔 117.0-0.0m塔腿结构图(2/2)		(52)
审　核	高锡鹏					
		设计/勘测				
比　例	1:40	日　期	2026年 08月	图　号	37-SA36901S-T0121-118	版本