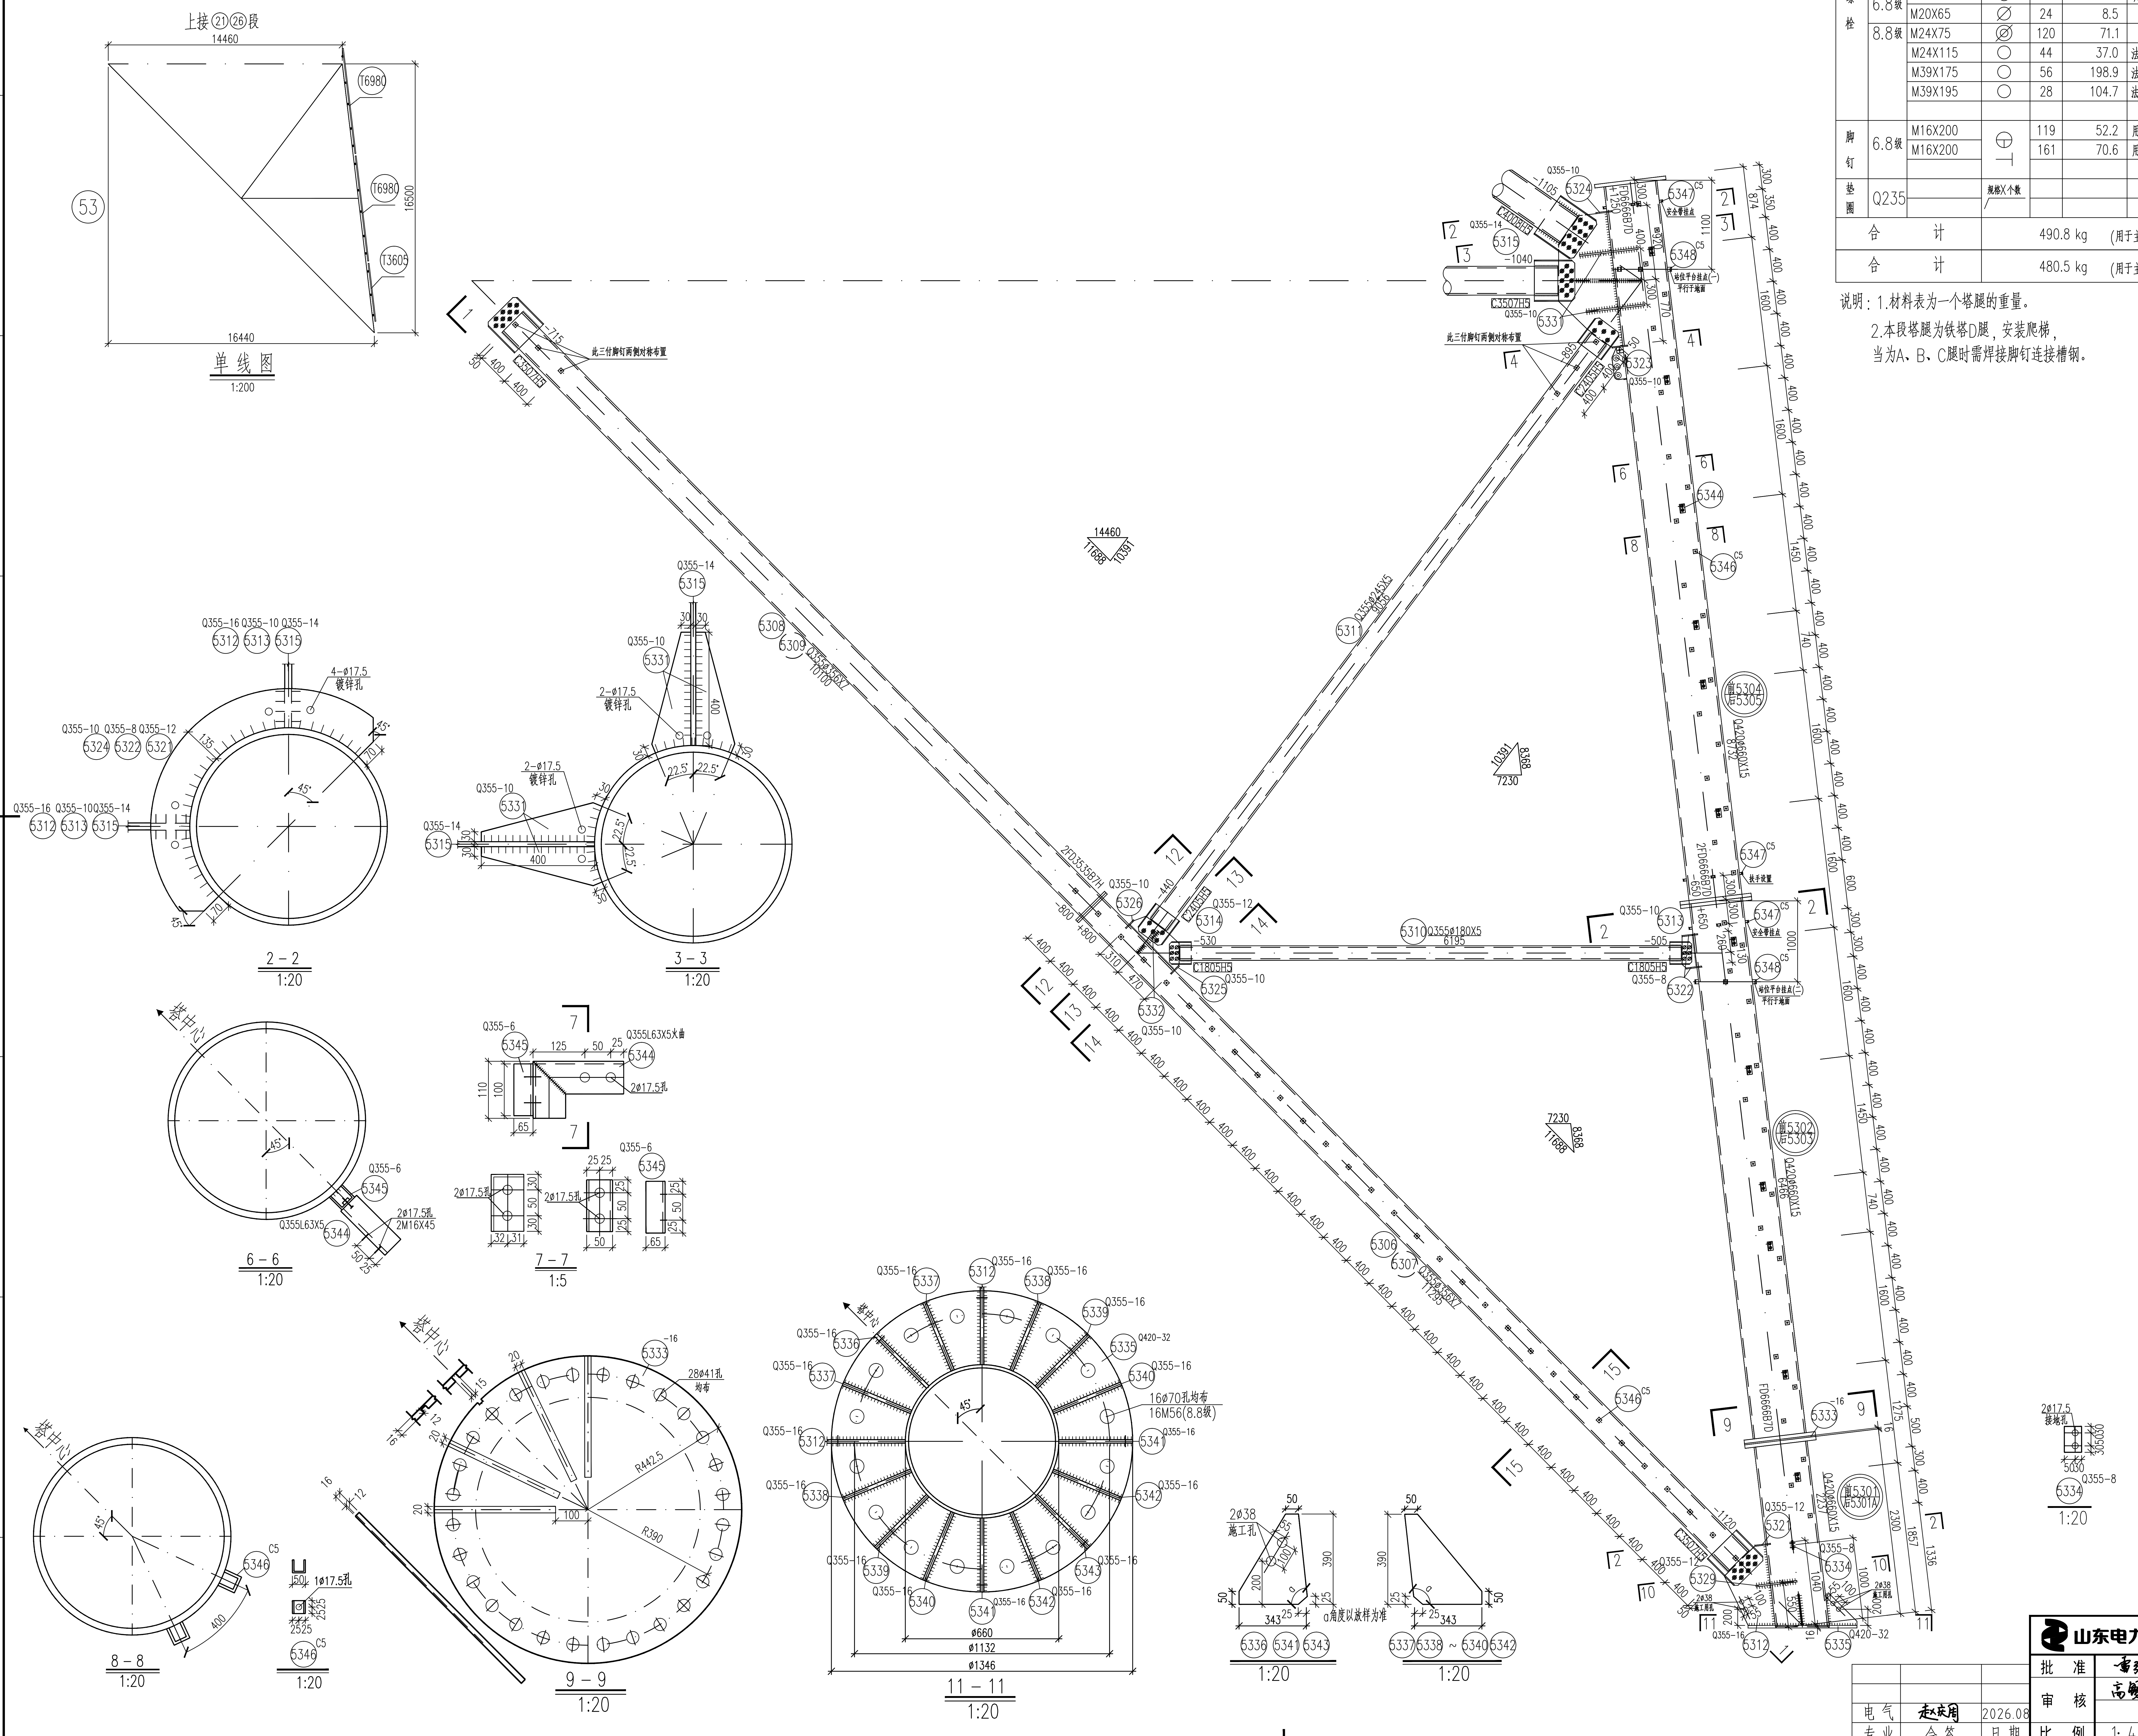

螺栓、脚钉、垫圈 明细表

名称	级别	规格	符号	数量	重量(kg)	备注
螺栓	6.8级	M16X45	◎	48	8.1	用于主材装爬梯
		M20X65	∅	24	8.5	
	8.8级	M24X75	∅	120	71.1	
		M24X115	○	44	37.0	法兰螺栓
		M39X175	○	56	198.9	法兰螺栓
		M39X195	○	28	104.7	法兰螺栓 无扣长97mm
脚钉	6.8级	M16X200	⊖	119	52.2	用于主材装爬梯
		M16X200		161	70.6	用于主材带脚钉
垫圈	Q235		规格X个数			
合计			490.8 kg (用于主材带脚钉)			
合计			480.5 kg (用于主材装爬梯)			

说明：1.材料表为一个塔腿的重量。

2.本段塔腿为铁塔D腿，安装爬梯，当为A、B、C腿时需焊接脚钉连接槽钢。

构 件 明 细 表

编号	规格	长度(mm)	数量	重量(kg) 一件	重量(kg) 小计	备注
5301	Q420ø660X15	2237	1	533.75	533.8	一端切弧 装爬梯
5301A	Q420ø660X15	2237	0	533.75	0.0	一端切弧 带脚钉
5302	Q420ø660X15	6466	1	1542.79	1542.8	装爬梯
5303	Q420ø660X15	6466	0	1542.79	0.0	带脚钉
5304	Q420ø660X15	8732	1	2083.46	2083.5	装爬梯
5305	Q420ø660X15	8732	0	2083.46	0.0	带脚钉
5306	Q355ø356X7	11295	1	680.50	680.5	带脚钉
5307	Q355ø356X7	11295	1	680.50	680.5	带脚钉
5308	Q355ø356X7	10100	1	608.51	608.5	带脚钉
5309	Q355ø356X7	10100	1	608.51	608.5	带脚钉
5310	Q355ø180X5	6195	2	133.68	267.4	
5311	Q355ø245X5	9056	2	268.00	536.0	带脚钉
5312	Q355-16X604	1144	2	86.79	173.6	
5313	Q355-10X199	429	2	6.70	13.4	
5314	Q355-12X301	858	2	24.33	48.7	
5315	Q355-14X793	1859	2	162.01	324.0	
5316	Q355ø273X5	9265	1	306.18	306.2	
5317	Q355ø273X5	10627	1	351.18	351.2	带脚钉
5318	Q355ø273X5	10627	1	351.18	351.2	带脚钉
5319	Q355-12X419	1078	2	42.55	85.1	
5320	Q355-12X378	990	1	35.25	35.2	
5321	Q355-12X135	1374	1	17.47	17.5	
5322	Q355-8X135	1374	2	11.65	23.3	
5323	Q355-10X135	1374	1	14.56	14.6	
5324	Q355-10X135	1374	1	14.56	14.6	
5325	Q355-10X80	565	2	3.55	7.1	
5326	Q355-10X80	314	2	1.97	3.9	
5327	Q355-10X80	376	2	2.36	4.7	
5328	Q355-10X150	388	2	4.57	9.1	
5329	Q355-12X180	330	2	5.60	11.2	
5330	Q355-12X180	660	1	11.19	11.2	
5331	Q355-10X150	509	8	5.99	47.9	
5332	Q355-10X200	241	2	3.78	7.6	
5333	-16X885	885	1	77.26	77.3	遮水板
5334	Q355-8X80	110	1	0.55	0.6	接地孔用
5335	Q420-32X1346	1346	1	272.50	272.5	
5336	Q355-16X343	390	1	16.80	16.8	
5337	Q355-16X343	390	2	16.80	33.6	
5338	Q355-16X343	390	2	16.80	33.6	
5339	Q355-16X343	390	2	16.80	33.6	
5340	Q355-16X343	390	2	16.80	33.6	
5341	Q355-16X343	390	2	16.80	33.6	
5342	Q355-16X343	390	2	16.80	33.6	
5343	Q355-16X343	390	1	16.80	16.8	
5344	Q355L63X5	310	12	1.49	17.9	火曲 (用于主材装爬梯)
5345	Q355-6X100	180	12	0.85	10.2	火曲 (用于主材装爬梯)
5346	C5	50	119	0.27	32.1	槽钢 (用于主材装爬梯)
5346	C5	50	161	0.27	43.5	槽钢 (用于主材带脚钉)
5347	C5	25	12	0.14	1.7	槽钢
5348	C5	50	8	0.27	2.2	槽钢
5349	Q355-14X210	550	1	12.69	12.7	
5350	Q355-38X104	104	3	3.23	9.7	
5351	Q355-10X100	115	2	0.90	1.8	
5352	Q355-6X50	100	1	0.24	0.2	
	C1805H5		4	7.12	28.5	
	C2405H5		4	17.27	69.1	
	C2705H5		6	18.10	108.6	
	C3507H5		4	36.27	145.1	
	FD3535B7H		4	22.10	88.4	
	FD6666B7D		5	116.50	582.5	
	T3605		1	19.00	19.0	(用于主材装爬梯)
	T6980		2	36.20	72.4	(用于主材装爬梯)
合计		11082.4 kg(用于主材带脚钉)				
合计		11190.5 kg(用于主材装爬梯)				

			山东电力工程咨询院有限公司				浙江特高压交流环网工程线路 工程	施工图 设计阶段
			批准		校核	马一丹	SZK31102A双回路直线塔 120.0-4.5m呼高腿部结构图（1/2）	53
			审核	高锡鹏				
电气	赵庆周	2026.08			设计/勘测			
专业	会签	日期	比例	1: 40	日期	2026年 08月	图号 37-SA36901S-T0121-119	版本