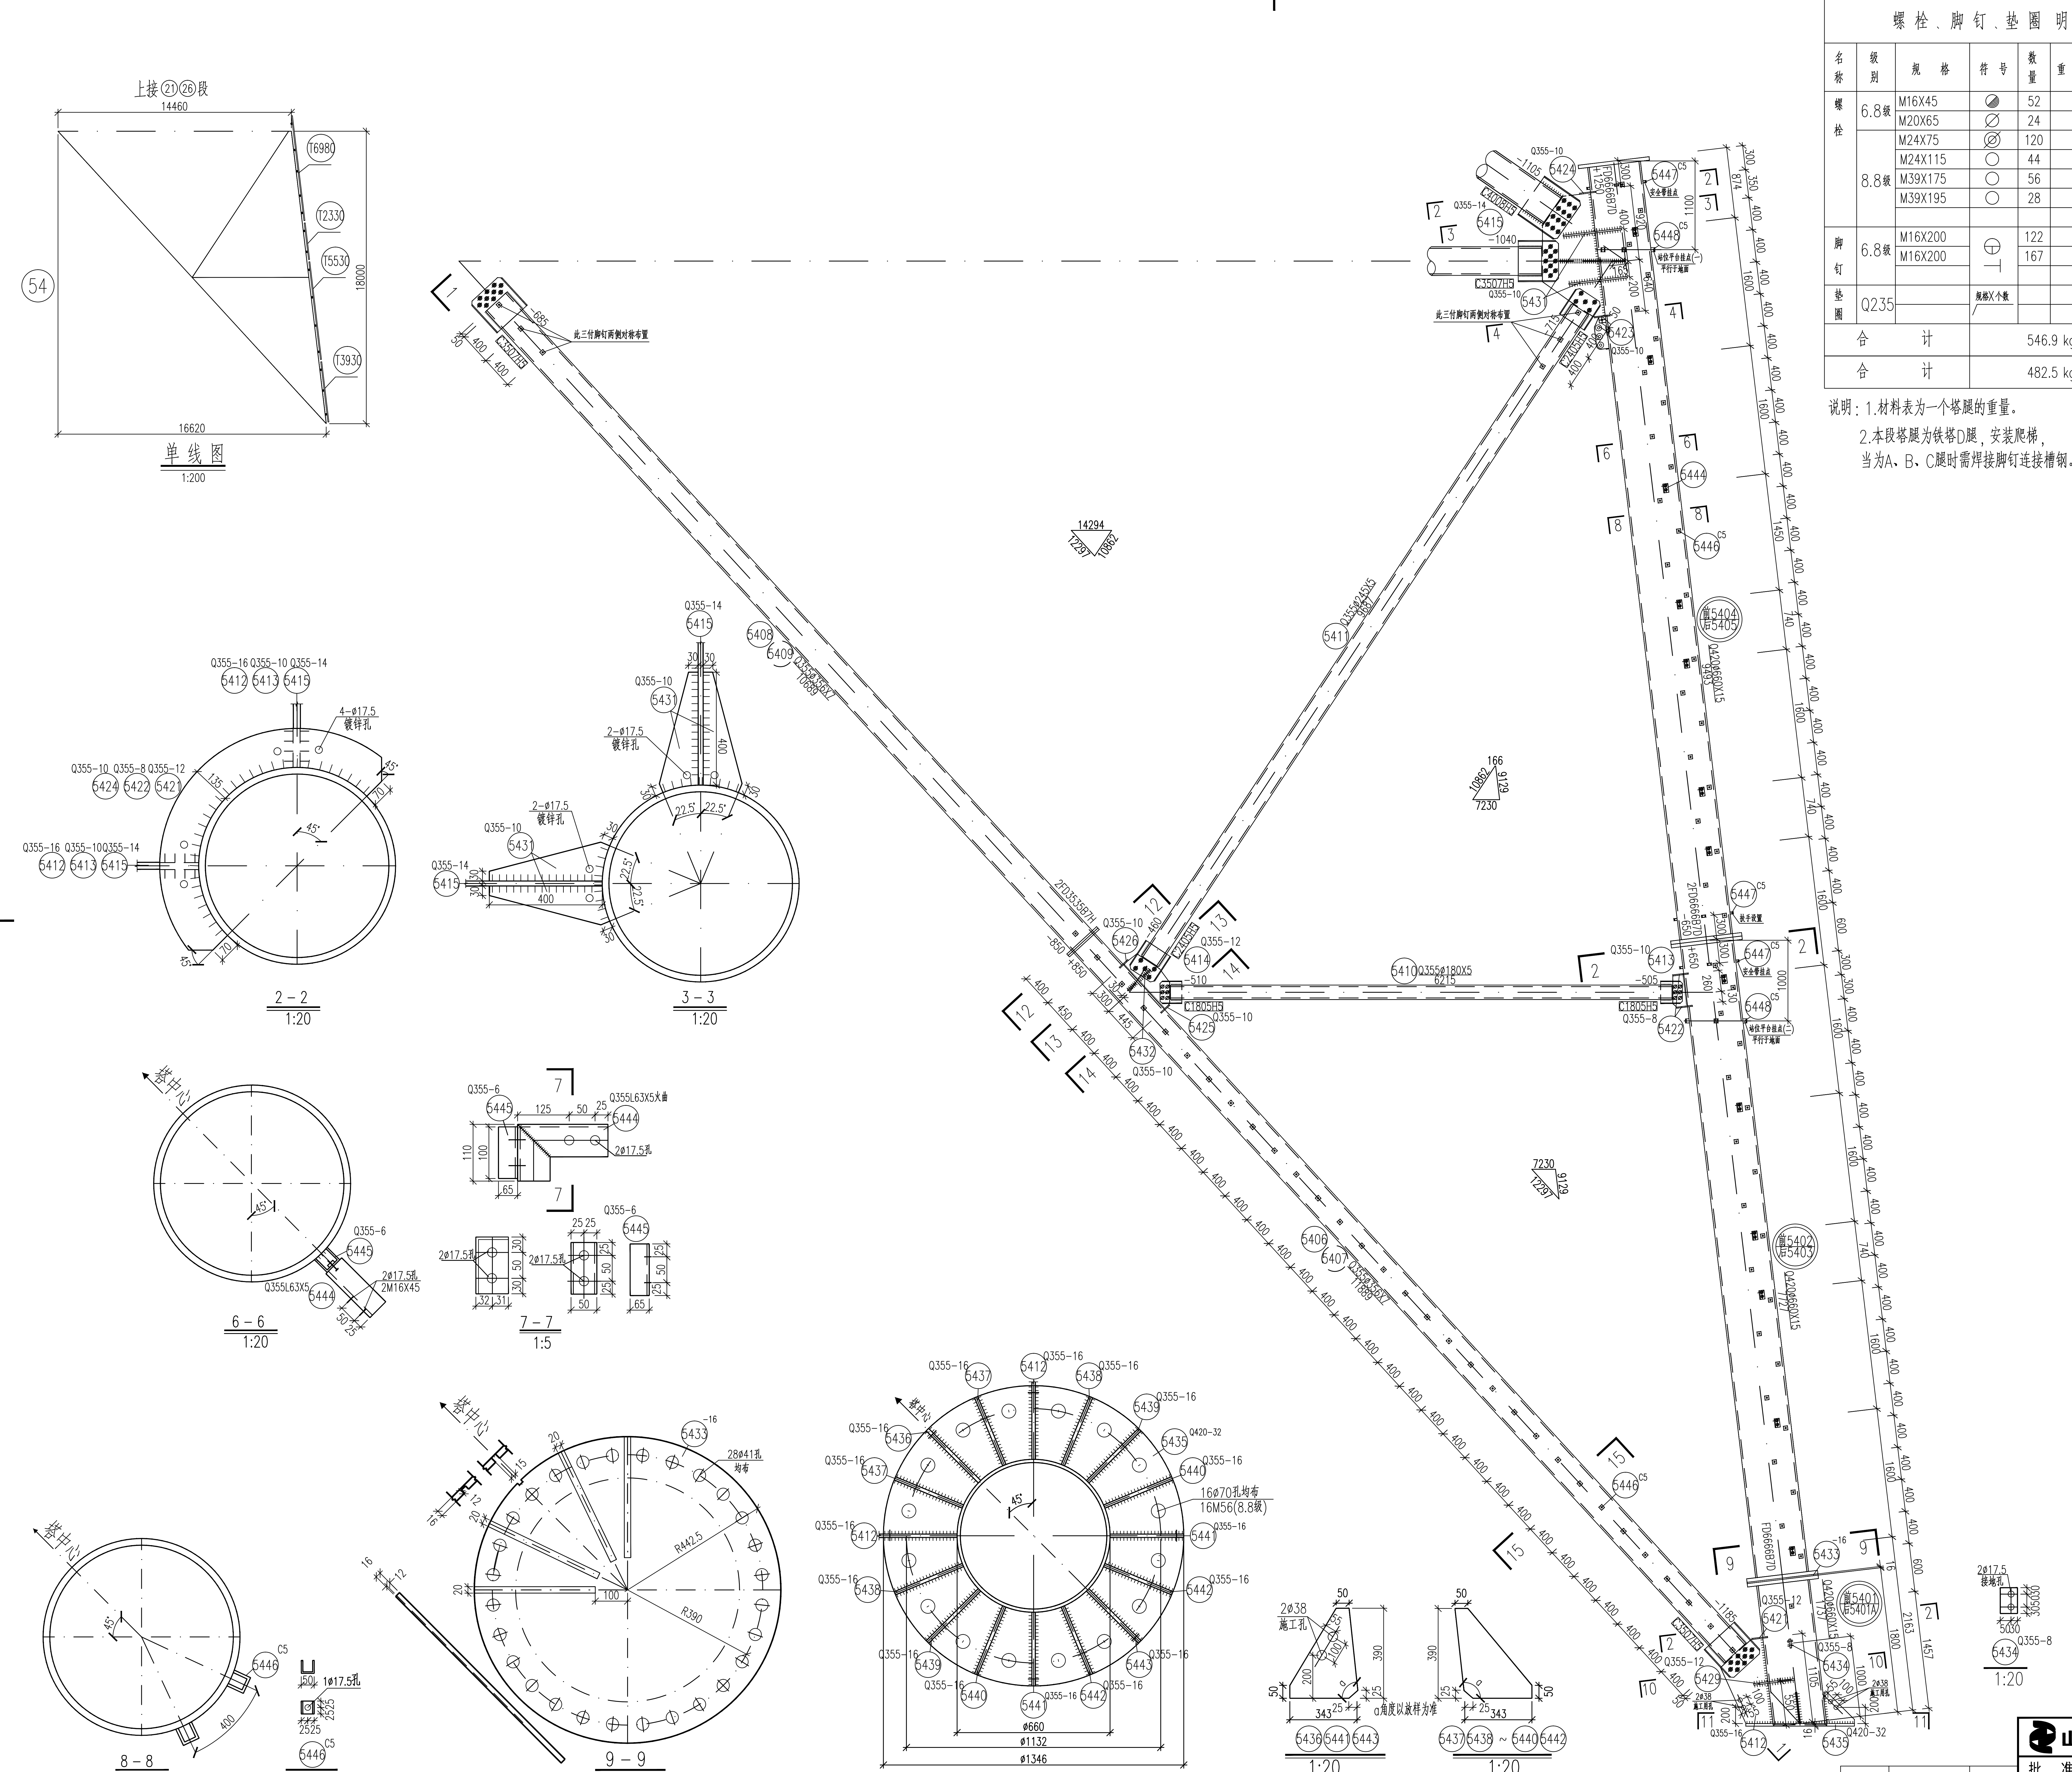

螺栓、脚钉、垫圈 明细表

名称	级别	规格	符号	数量	重量(kg)	备注
螺栓	6.8级	M16X45	◎	52	8.8	用于主材装爬梯
		M20X65	∅	24	8.5	
	8.8级	M24X75	∅	120	71.1	
		M24X115	○	44	37.0	法兰螺栓
		M39X175	○	56	198.9	法兰螺栓
		M39X195	○	28	104.7	法兰螺栓 无扣长97mm
脚钉	6.8级	M16X200	⊖	122	53.5	用于主材装爬梯
		M16X200		167	73.2	用于主材带脚钉
垫圈	Q235		规格X个数			
合计		546.9 kg (用于主材带脚钉)				
合计		482.5 kg (用于主材装爬梯)				

说明：1.材料表为一个塔腿的重量。

2.本段塔腿为铁塔D腿，安装爬梯，当为A、B、C腿时需焊接脚钉连接槽钢。

构 件 明 细 表

编号	规格	长度(mm)	数量	重量(kg) 一件	重量(kg) 小计	备注
5401	Q420ø660X15	1737	1	414.45	414.4	一端切弧
5401A	Q420ø660X15	1737	0	414.45	0.0	一端切弧 带脚钉
5402	Q420ø660X15	7727	1	1843.66	1843.7	装爬梯
5403	Q420ø660X15	7727	0	1843.66	0.0	带脚钉
5404	Q420ø660X15	9493	1	2265.03	2265.0	装爬梯
5405	Q420ø660X15	9493	0	2265.03	0.0	带脚钉
5406	Q355ø356X7	11889	1	716.29	716.3	带脚钉
5407	Q355ø356X7	11889	1	716.29	716.3	带脚钉
5408	Q355ø356X7	10689	1	643.99	644.0	带脚钉
5409	Q355ø356X7	10689	1	643.99	644.0	带脚钉
5410	Q355ø180X5	6215	2	134.11	268.2	
5411	Q355ø245X5	9687	2	286.68	573.4	带脚钉
5412	Q355-16X624	1216	2	95.30	190.6	
5413	Q355-10X199	429	2	6.70	13.4	
5414	Q355-12X335	820	2	25.88	51.8	
5415	Q355-14X793	1716	2	149.55	299.1	
5416	Q355ø273X5	9285	1	306.84	306.8	
5417	Q355ø273X5	11207	1	370.35	370.4	带脚钉
5418	Q355ø273X5	11207	1	370.35	370.4	带脚钉
5419	Q355-12X425	1078	2	43.16	86.3	
5420	Q355-12X378	990	1	35.25	35.2	
5421	Q355-12X135	1374	1	17.47	17.5	
5422	Q355-8X135	1374	2	11.65	23.3	
5423	Q355-10X135	1374	1	14.56	14.6	
5424	Q355-10X135	1374	1	14.56	14.6	
5425	Q355-10X80	565	2	3.55	7.1	
5426	Q355-10X80	314	2	1.97	3.9	
5427	Q355-10X80	376	2	2.36	4.7	
5428	Q355-10X160	396	2	4.97	9.9	
5429	Q355-12X180	330	2	5.60	11.2	
5430	Q355-12X180	660	1	11.19	11.2	
5431	Q355-10X150	509	8	5.99	47.9	
5432	Q355-10X200	241	2	3.78	7.6	
5433	-16X885	885	1	77.26	77.3	遮水板
5434	Q355-8X80	110	1	0.55	0.6	接地孔用
5435	Q420-32X1346	1346	1	272.50	272.5	
5436	Q355-16X343	390	1	16.80	16.8	
5437	Q355-16X343	390	2	16.80	33.6	
5438	Q355-16X343	390	2	16.80	33.6	
5439	Q355-16X343	390	2	16.80	33.6	
5440	Q355-16X343	390	2	16.80	33.6	
5441	Q355-16X343	390	2	16.80	33.6	
5442	Q355-16X343	390	2	16.80	33.6	
5443	Q355-16X343	390	1	16.80	16.8	
5444	Q355L63X5	310	13	1.49	19.4	火曲 (用于主材装爬梯)
5445	Q355-6X100	180	13	0.85	11.0	火曲 (用于主材装爬梯)
5446	C5	50	122	0.27	32.9	槽钢 (用于主材装爬梯)
5446	C5	50	167	0.27	45.1	槽钢 (用于主材带脚钉)
5447	C5	25	12	0.14	1.7	槽钢
5448	C5	50	8	0.27	2.2	槽钢
5449	Q355-14X210	550	1	12.69	12.7	
5450	Q355-38X104	104	3	3.23	9.7	
5451	Q355-10X100	115	2	0.90	1.8	
5452	Q355-6X50	100	1	0.24	0.2	
	C1805H5		4	7.12	28.5	
	C2405H5		4	17.27	69.1	
	C2705H5		6	18.10	108.6	
	C3507H5		4	36.27	145.1	
	FD3535B7H		4	22.10	88.4	
	FD6666B7D		5	116.50	582.5	
	T2330		1	12.40	12.4	(用于主材装爬梯)
	T3930		1	20.70	20.7	(用于主材装爬梯)
	T5530		1	28.80	28.8	(用于主材装爬梯)
	T6980		1	36.20	36.2	(用于主材装爬梯)
合计		11664.0 kg(用于主材带脚钉)				
合计		11780.3 kg(用于主材装爬梯)				

			山东电力工程咨询院有限公司			浙江特高压交流环网工程线路 工程	施工图 设计阶段
			批准	雷强	校核	马一丹	SZK31102A双回路直线塔 120.0-3.0m呼高腿部结构图（1/2） ㊹
			审核	高锡鹏			
电气	赵庆周	2026.08			设计/勘测		
专业	会签	日期	比例	1: 40	日期	2026年 08月	图号 37-SA36901S-T0121- 121 版本