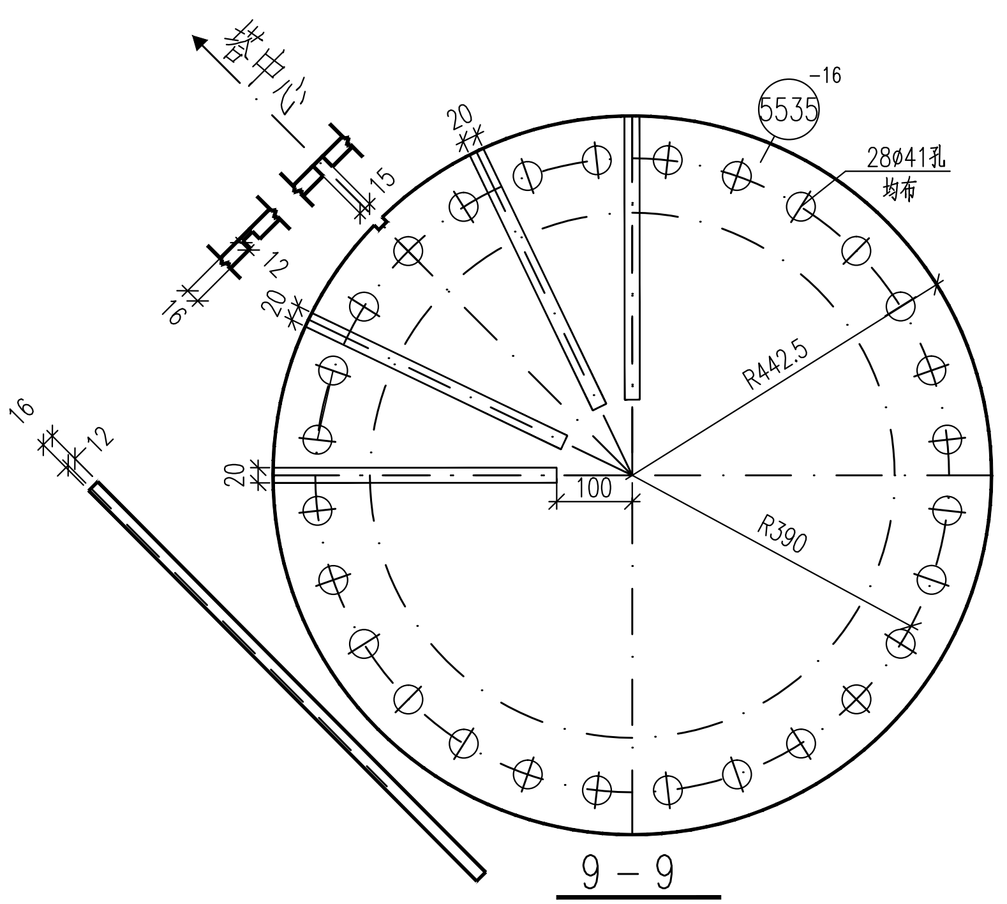
塔中心
5535
-16
28ø41孔
均布
R442.5
R390
100
20
15
12
16

9－9
1:20

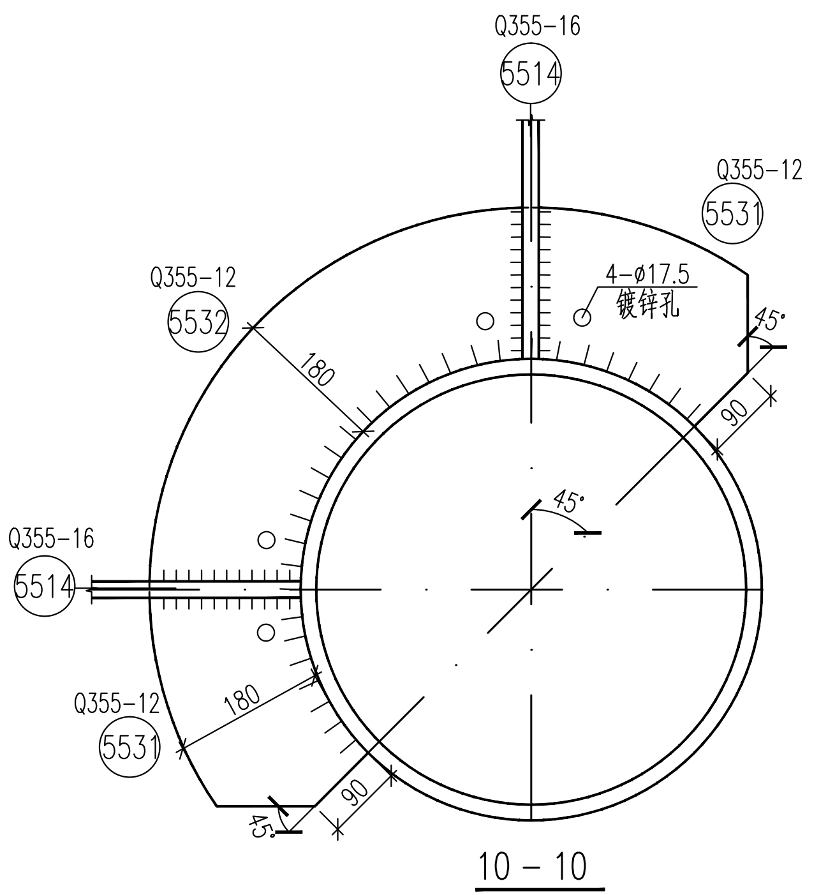
Q355-16
5514
Q355-12
5531
4-ø17.5
镀锌孔
Q355-12
5532
Q355-16
5514
Q355-12
5531
180
90
45°

10－10
1:20

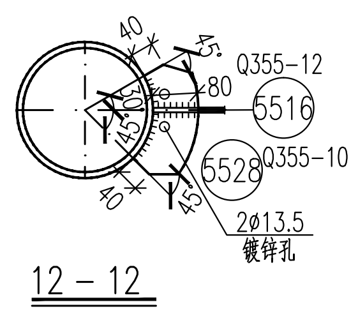
Q355-12
5516
Q355-10
5529
2ø13.5
镀锌孔
80
40

12－12
1:10

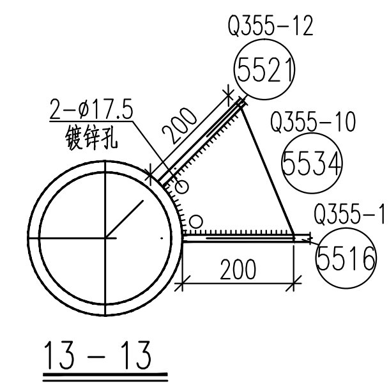
Q355-12
5521
2-ø17.5
镀锌孔
Q355-10
5534
Q355-12
5516
200

13－13
1:10

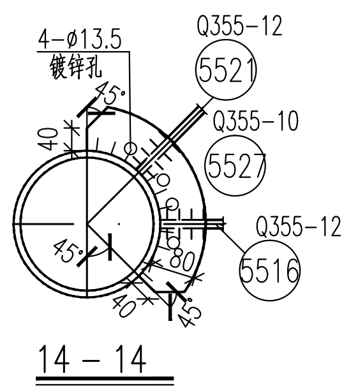
4-ø13.5
镀锌孔
Q355-12
5521
Q355-10
5527
Q355-12
5516

14－14
1:10

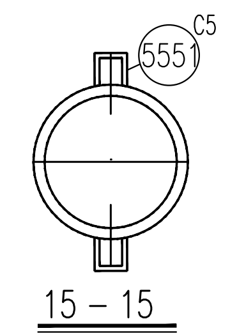

15－15
1:10

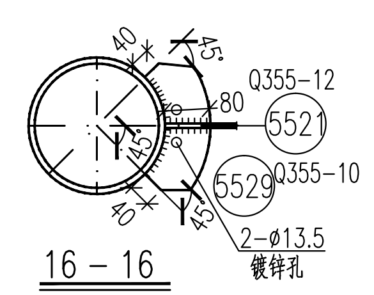
Q355-12
5521
Q355-10
5529
2-ø13.5
镀锌孔
80
40

16－16
1:10

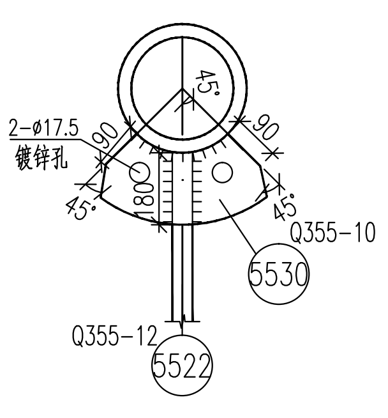
2-ø17.5
镀锌孔
Q355-10
5530
Q355-12
5522
45°

17－17
1:10

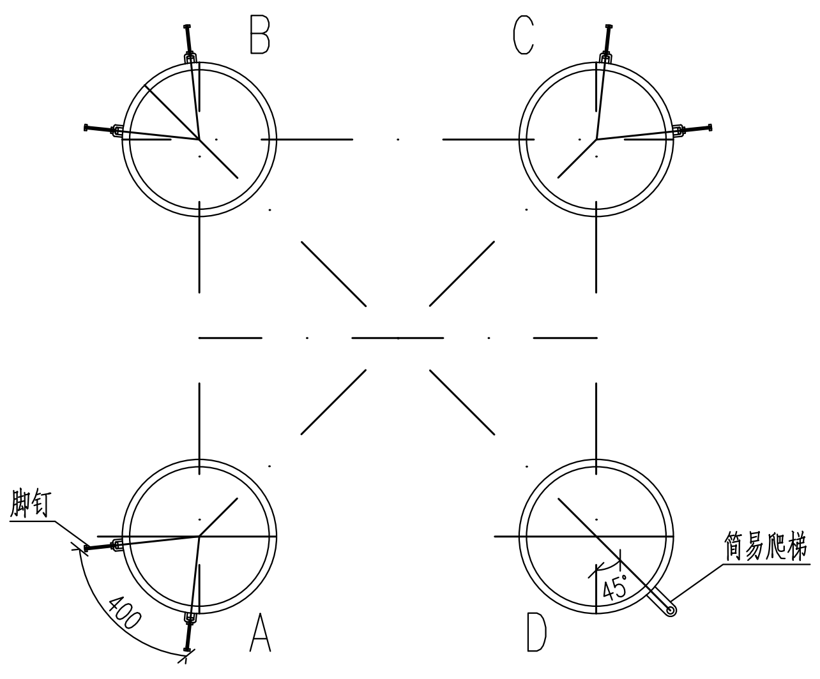
B
C
A
D
脚钉
简易爬梯
400
45°

爬梯脚钉示意图

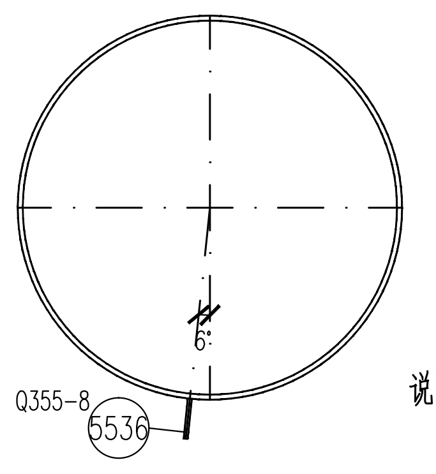
6°
Q355-8
5536

接地孔位置示意图
1:20

说明：接地孔安装板⑤⑤③⑥避开法兰加劲板和地脚法兰螺栓所在角度，以避免接地引下线和法兰加劲板相碰.

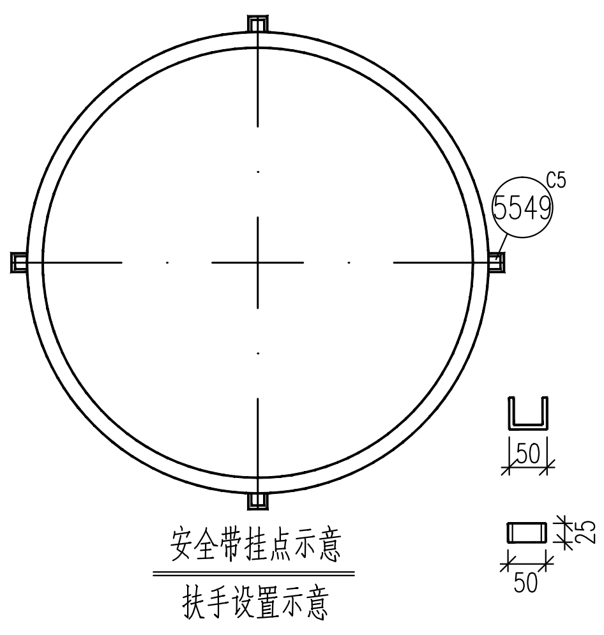
5549
C5
50
15

安全带挂点示意
扶手设置示意

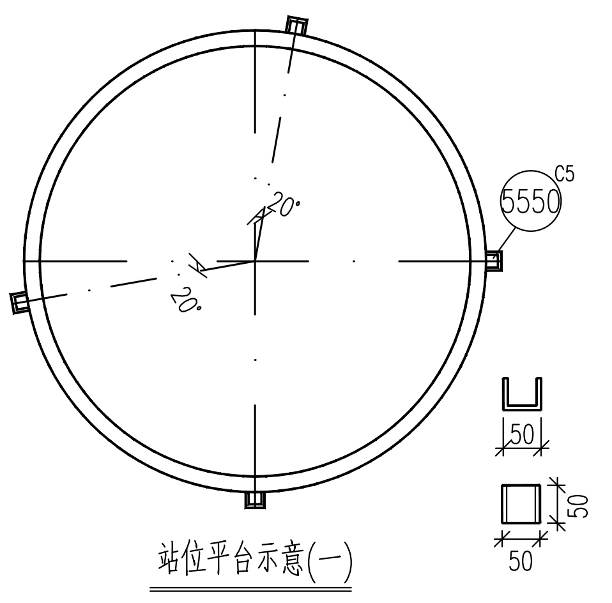
5550
C5
20°
50

站位平台示意(一)

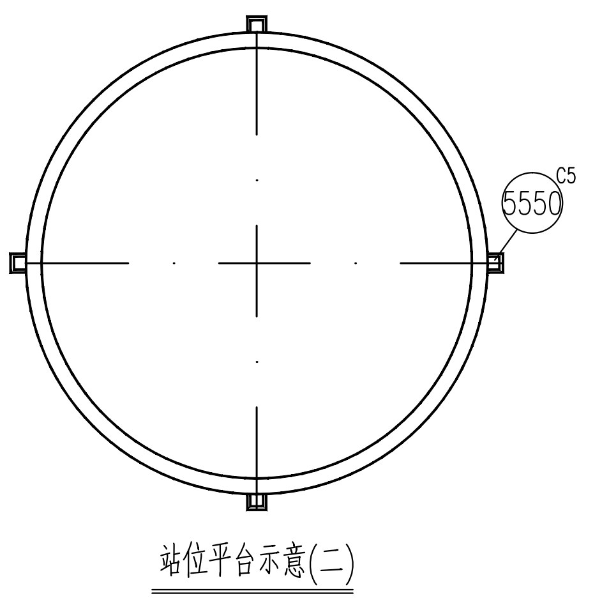

站位平台示意(二)

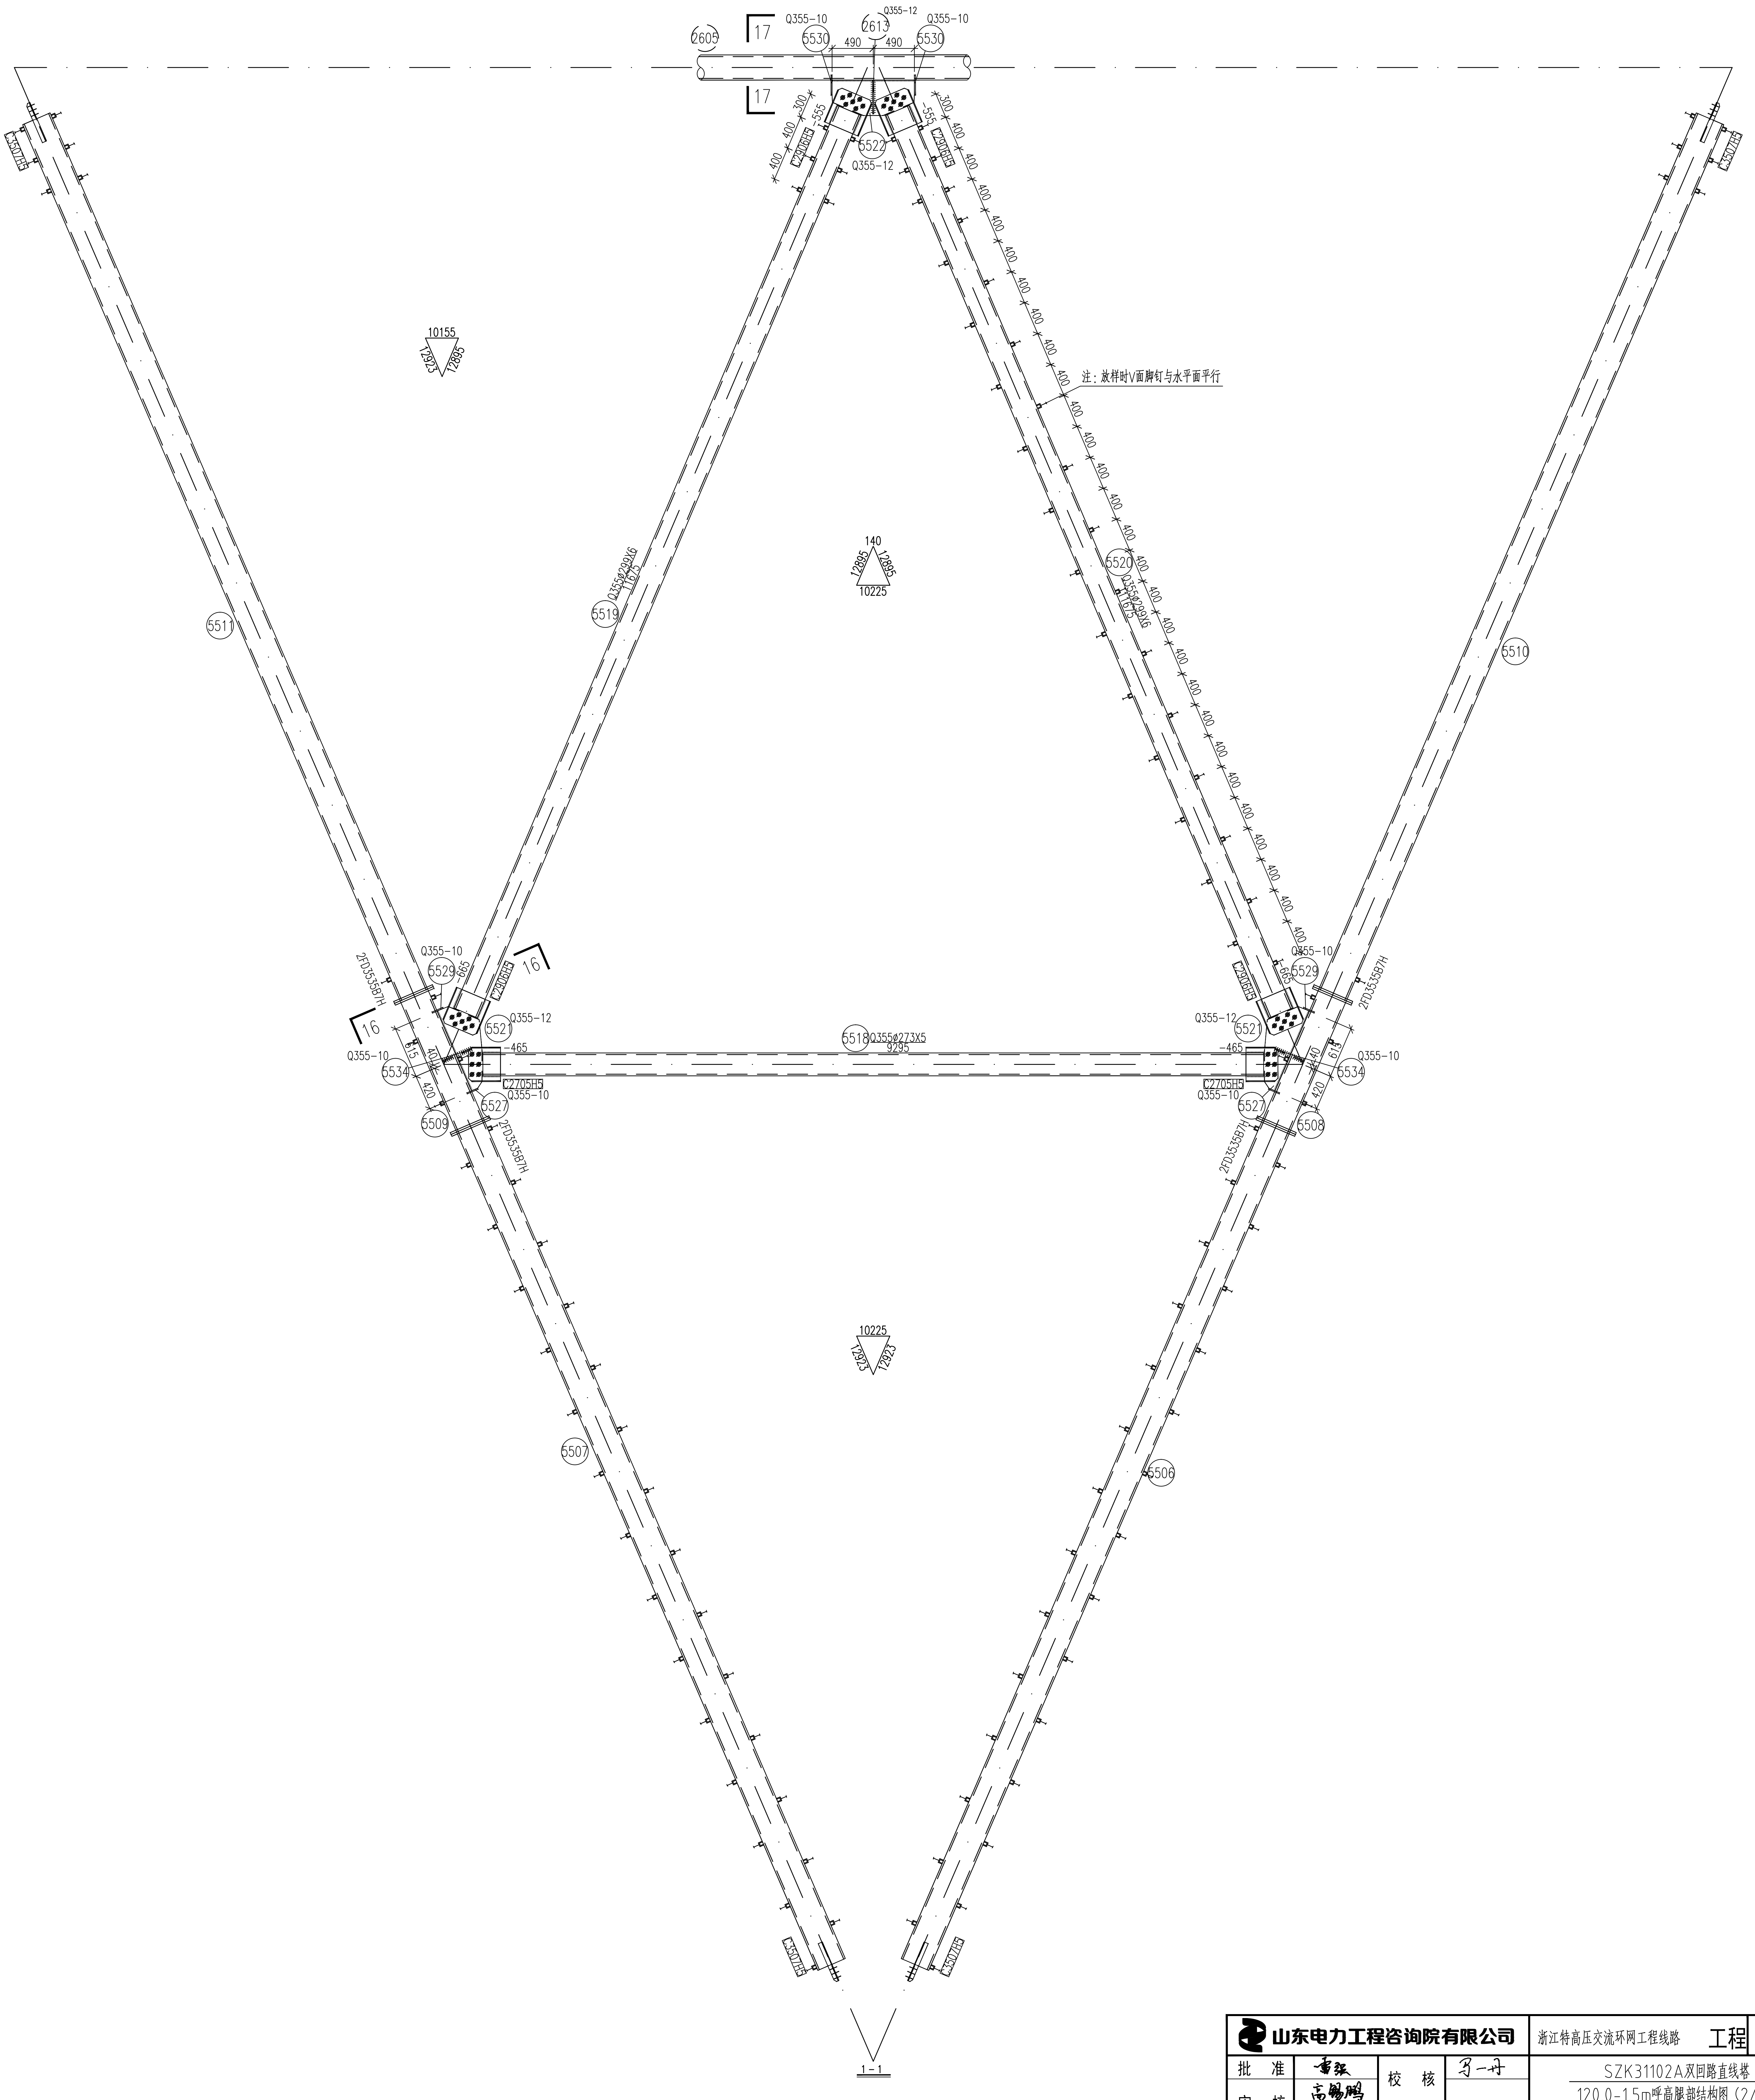
2605
17
Q355-10
5530
2613
Q355-12
490
490
5522
Q355-12
10155
12923
12895
5519
5520
5510
5511
140
10225
注：放样时V面脚钉与水平面平行
Q355-10
5529
Q355-12
5521
Q355-10
5534
5527
5509
5518
Q355ø273X5
9285
C2705H5
5508
16
10225
12923
5507
5506

1－1

山东电力工程咨询院有限公司				浙江特高压交流环网工程线路 工程	施工图 设计阶段
批 准	雷强	校 核	马一丹	SZK31102A双回路直线塔 120.0-1.5m呼高腿部结构图（2/2） 123.0-4.5m呼高腿部结构图（2/2）	(55)
审 核	高锡鹏	设计/勘测	潘旺光		
比 例	1：40	日 期	2026年 08月	图 号 37-SA36901S-T0121-124	版本