

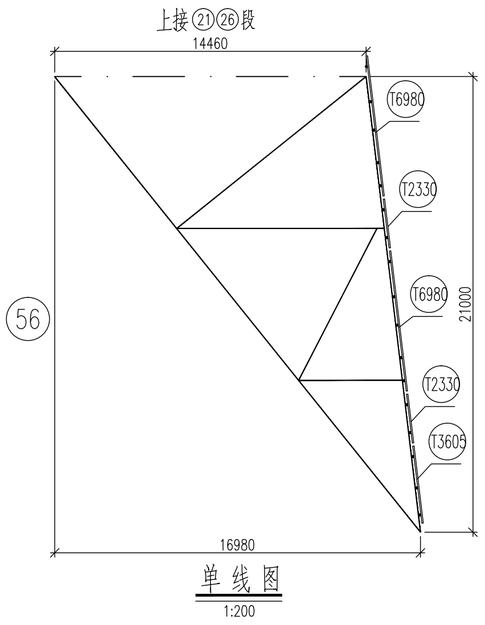




单线图
1:200

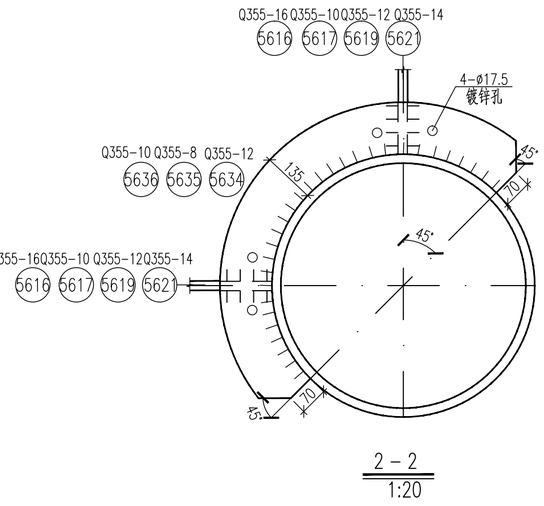



2 - 2
1:20

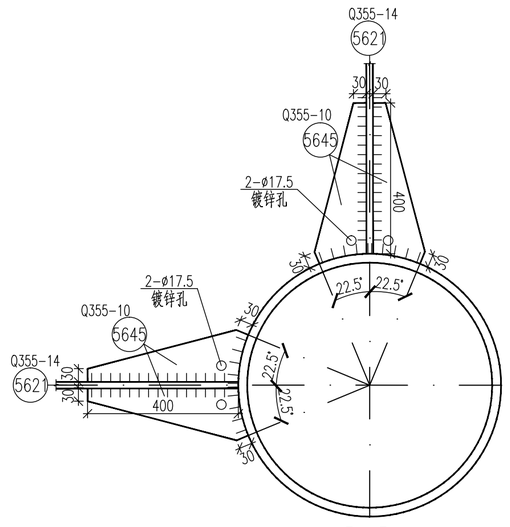



3 - 3
1:20

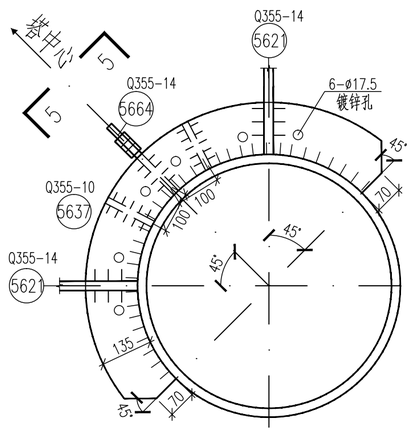


4 - 4
1:20

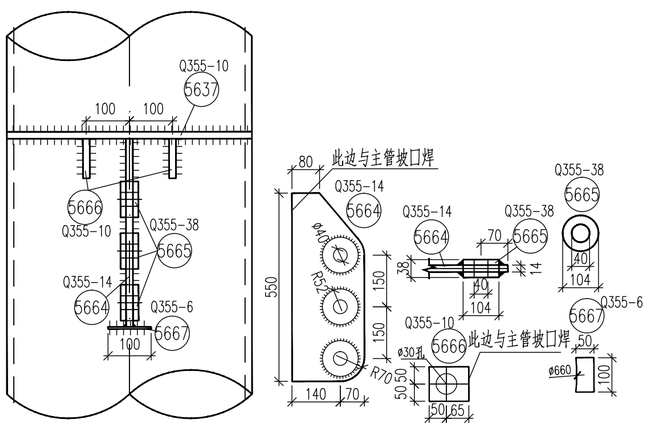



5 - 5
1:20

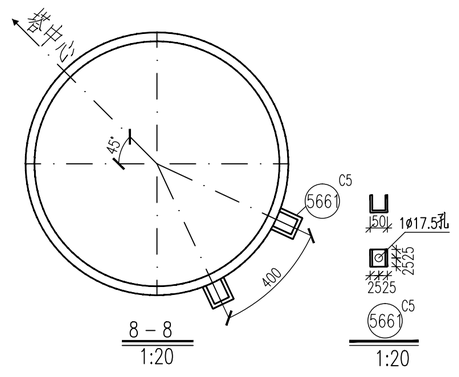


8 - 8
1:20

1:20

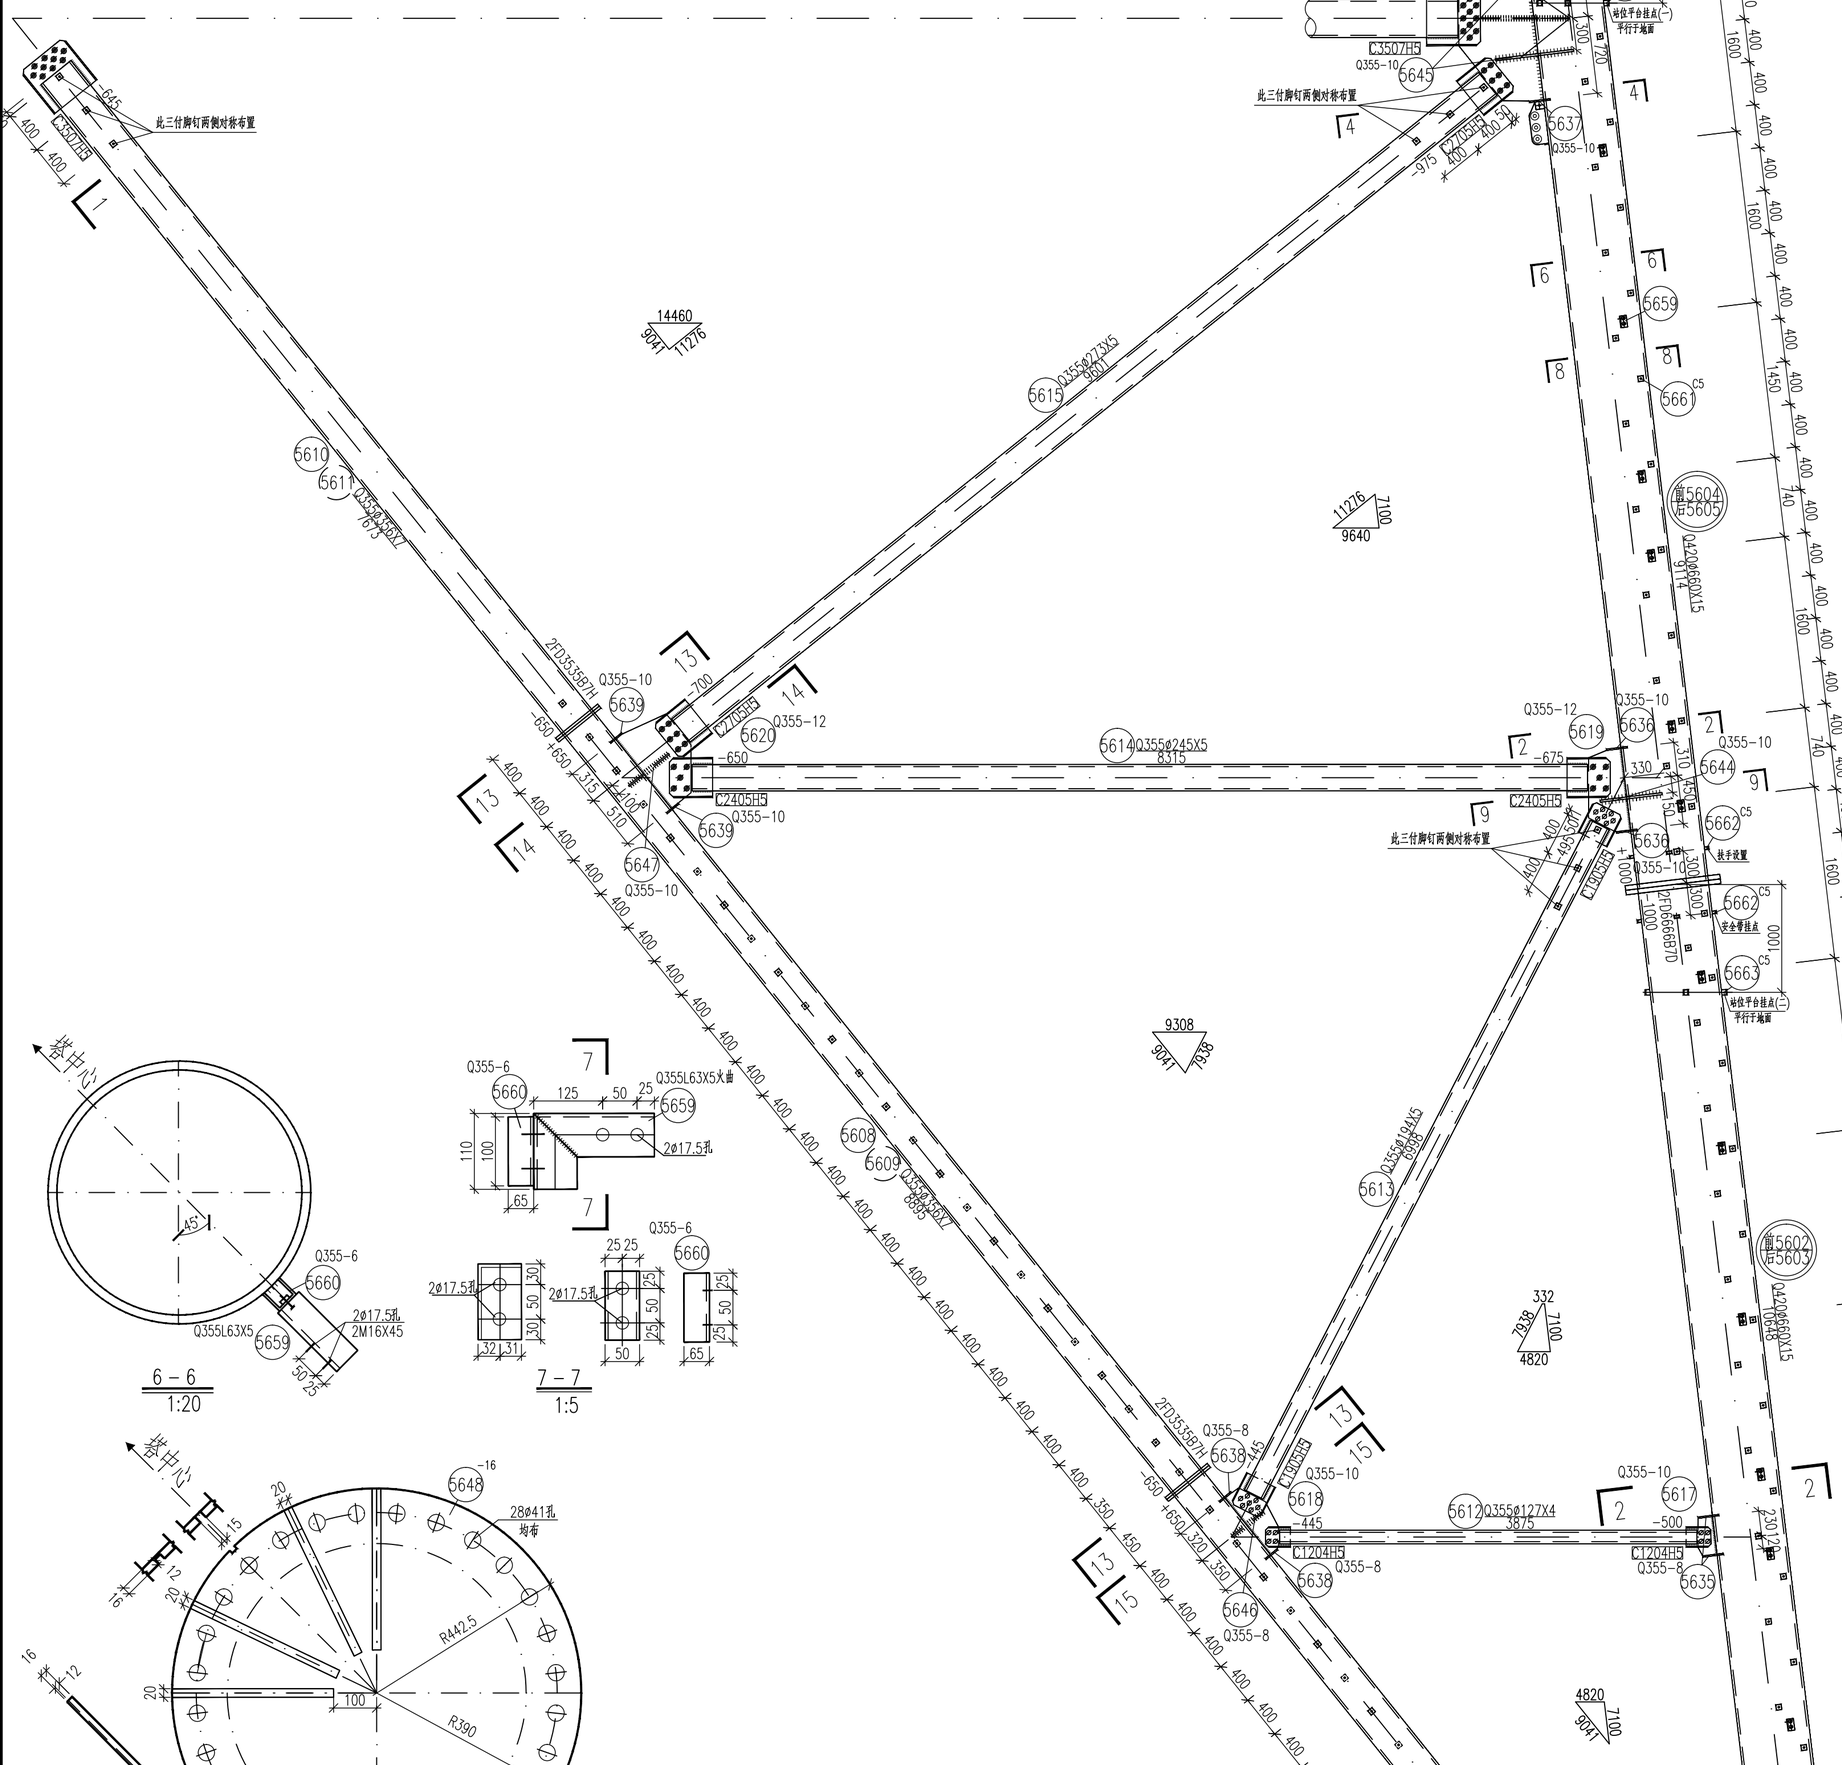







6 - 6
1:20




7 - 7
1:5

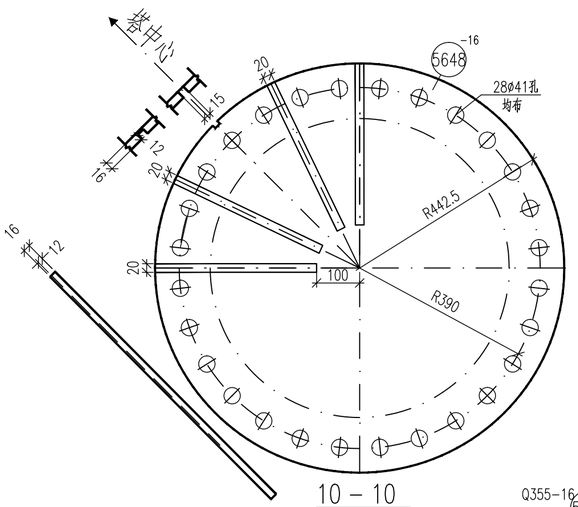


10 - 10
1:20

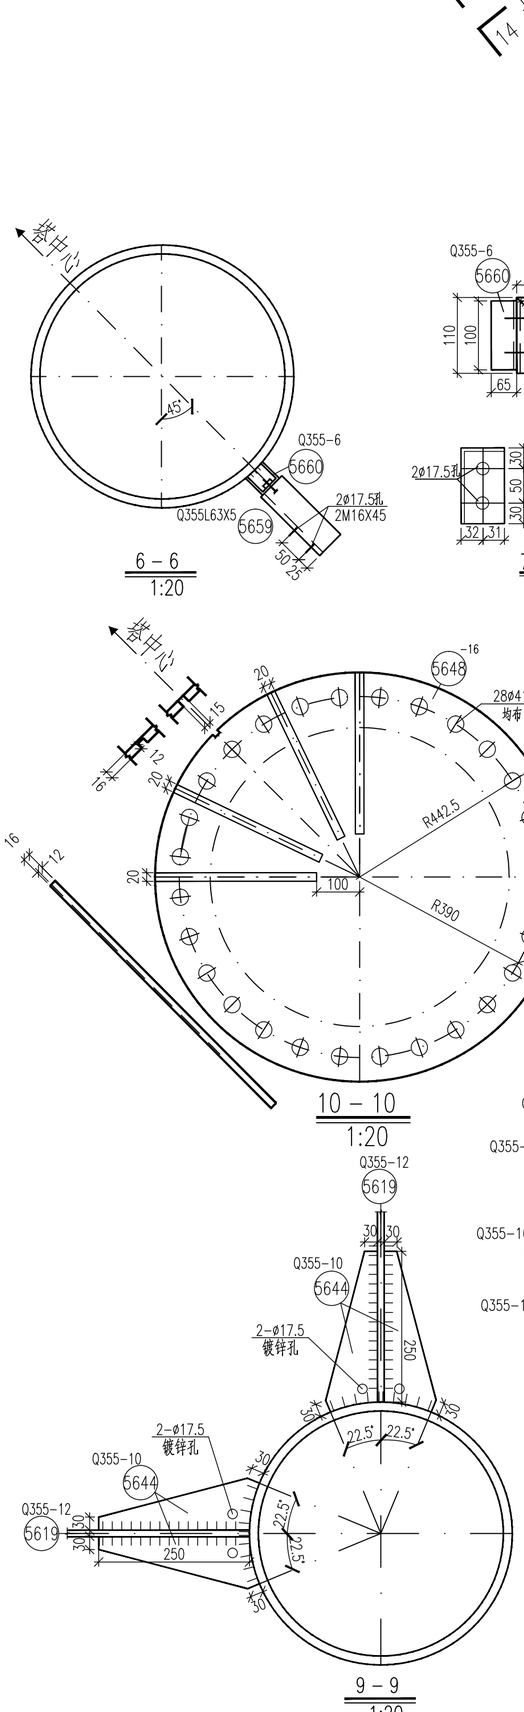


9 - 9
1:20




12 - 12
1:20




1:20

1:20

## 构件明细表

| 编号 | 规格 | 长度(mm) | 数量 | 重量(kg) 一件 | 重量(kg) 小计 | 备注 |
|---|---|---|---|---|---|---|
| 5601 | Q420ø660X15 | 2237 | 1 | 533.75 | 533.8 | 一端切弧 装爬梯 |
| 5601A | Q420ø660X15 | 2237 | 0 | 533.75 | 0.0 | 一端切弧 带脚钉 |
| 5602 | Q420ø660X15 | 10648 | 1 | 2540.61 | 2540.6 | 装爬梯 |
| 5603 | Q420ø660X15 | 10648 | 0 | 2540.61 | 0.0 | 带脚钉 |
| 5604 | Q420ø660X15 | 9114 | 1 | 2174.60 | 2174.6 | 装爬梯 |
| 5605 | Q420ø660X15 | 9114 | 0 | 2174.60 | 0.0 | 带脚钉 |
| 5606 | Q355ø356X7 | 8303 | 1 | 500.24 | 500.2 | 带脚钉 |
| 5607 | Q355ø356X7 | 8303 | 1 | 500.24 | 500.2 | 带脚钉 |
| 5608 | Q355ø356X7 | 8895 | 1 | 535.91 | 535.9 | 带脚钉 |
| 5609 | Q355ø356X7 | 8895 | 1 | 535.91 | 535.9 | 带脚钉 |
| 5610 | Q355ø356X7 | 7673 | 1 | 462.28 | 462.3 | 带脚钉 |
| 5611 | Q355ø356X7 | 7673 | 1 | 462.28 | 462.3 | 带脚钉 |
| 5612 | Q355ø127X4 | 3875 | 2 | 47.02 | 94.0 | |
| 5613 | Q355ø194X5 | 6998 | 2 | 163.09 | 326.2 | 带脚钉 |
| 5614 | Q355ø245X5 | 8315 | 2 | 246.07 | 492.1 | |
| 5615 | Q355ø273X5 | 9601 | 2 | 317.28 | 634.6 | 带脚钉 |
| 5616 | Q355-16X628 | 1370 | 2 | 108.06 | 216.1 | |
| 5617 | Q355-10X188 | 385 | 2 | 5.68 | 11.4 | |
| 5618 | Q355-10X316 | 737 | 2 | 18.28 | 36.6 | |
| 5619 | Q355-12X416 | 836 | 2 | 32.76 | 65.5 | |
| 5620 | Q355-12X563 | 908 | 2 | 48.16 | 96.3 | |
| 5621 | Q355-14X793 | 1804 | 2 | 157.22 | 314.4 | |
| 5622 | Q355ø168X4 | 5847 | 1 | 94.59 | 94.6 | |
| 5623 | Q355ø203X5 | 4344 | 1 | 106.06 | 106.1 | 带脚钉 |
| 5624 | Q355ø203X5 | 7623 | 1 | 186.11 | 186.1 | 带脚钉 |
| 5625 | Q355ø203X5 | 3474 | 1 | 84.82 | 84.8 | 带脚钉 |
| 5626 | Q355ø203X5 | 7753 | 1 | 189.29 | 189.3 | 带脚钉 |
| 5627 | Q355ø245X5 | 9772 | 1 | 289.19 | 289.2 | 带脚钉 |
| 5628 | Q355ø245X5 | 9772 | 1 | 289.19 | 289.2 | 带脚钉 |
| 5629 | Q355-10X403 | 737 | 2 | 23.32 | 46.6 | |
| 5630 | Q355-10X610 | 484 | 1 | 23.18 | 23.2 | |
| 5631 | Q355-10X242 | 616 | 2 | 11.70 | 23.4 | |
| 5632 | Q355-12X407 | 908 | 2 | 34.81 | 69.6 | |
| 5633 | Q355-12X408 | 1078 | 1 | 41.43 | 41.4 | |
| 5634 | Q355-12X135 | 1374 | 1 | 17.47 | 17.5 | |
| 5635 | Q355-8X135 | 1374 | 4 | 11.65 | 46.6 | |
| 5636 | Q355-10X135 | 1374 | 1 | 14.56 | 14.6 | |
| 5637 | Q355-10X135 | 1374 | 1 | 14.56 | 14.6 | |
| 5638 | Q355-8X80 | 565 | 4 | 2.84 | 11.4 | |
| 5639 | Q355-10X80 | 565 | 4 | 3.55 | 14.2 | |
| 5640 | Q355-8X60 | 454 | 4 | 1.71 | 6.8 | |
| 5641 | Q355-10X120 | 362 | 2 | 3.41 | 6.8 | |
| 5642 | Q355-12X180 | 330 | 2 | 5.60 | 11.2 | |
| 5643 | Q355-12X180 | 660 | 1 | 11.19 | 11.2 | |
| 5644 | Q355-10X150 | 344 | 4 | 4.05 | 16.2 | |
| 5645 | Q355-10X150 | 509 | 8 | 5.99 | 47.9 | |
| 5646 | Q355-8X200 | 241 | 2 | 3.03 | 6.1 | |
| 5647 | Q355-10X300 | 284 | 2 | 6.69 | 13.4 | |
| 5648 | -16X885 | 885 | 1 | 77.26 | 77.3 | 遮水板 |
| 5649 | Q355-8X80 | 110 | 1 | 0.55 | 0.6 | 接地孔用 |
| 5650 | Q420-32X1346 | 1346 | 1 | 272.50 | 272.5 | |
| 5651 | Q355-16X343 | 390 | 1 | 16.80 | 16.8 | |
| 5652 | Q355-16X343 | 390 | 2 | 16.80 | 33.6 | |
| 5653 | Q355-16X343 | 390 | 2 | 16.80 | 33.6 | |
| 5654 | Q355-16X343 | 390 | 2 | 16.80 | 33.6 | |
| 5655 | Q355-16X343 | 390 | 2 | 16.80 | 33.6 | |
| 5656 | Q355-16X343 | 390 | 2 | 16.80 | 33.6 | |
| 5657 | Q355-16X343 | 390 | 2 | 16.80 | 33.6 | |
| 5658 | Q355-16X343 | 390 | 1 | 16.80 | 16.8 | |
| 5659 | Q355L63X5 | 310 | 16 | 1.49 | 23.8 | 火曲 (用于主材装爬梯) |
| 5660 | Q355-6X100 | 180 | 16 | 0.85 | 13.6 | 火曲 (用于主材装爬梯) |
| 5661 | C5 | 50 | 208 | 0.27 | 56.2 | 槽钢 (用于主材装爬梯) |
| 5661 | C5 | 50 | 260 | 0.27 | 70.2 | 槽钢 (用于主材带脚钉) |
| 5662 | C5 | 25 | 12 | 0.14 | 1.7 | 槽钢 |
| 5663 | C5 | 50 | 8 | 0.27 | 2.2 | 槽钢 |
| 5664 | Q355-14X210 | 550 | 1 | 12.69 | 12.7 | |
| 5665 | Q355-38X104 | 104 | 3 | 3.23 | 9.7 | |
| 5666 | Q355-10X100 | 115 | 2 | 0.90 | 1.8 | |
| 5667 | Q355-6X50 | 100 | 1 | 0.24 | 0.2 | |
| 5668 | Q355-12X100 | 301 | 2 | 2.84 | 5.7 | |
| | C1204H5 | | 4 | 4.19 | 16.8 | |
| | C1604H5 | | 2 | 7.12 | 14.2 | |
| | C1905H5 | | 4 | 8.80 | 35.2 | |
| | C2005H5 | | 4 | 9.74 | 39.0 | |
| | C2405H5 | | 8 | 17.27 | 138.2 | |
| | C2705H5 | | 4 | 18.10 | 72.4 | |
| | X2005H7 | | 2 | 24.40 | 48.8 | |
| | C3507H5 | | 4 | 36.27 | 145.1 | |
| | FD2020B7H | | 2 | 8.60 | 17.2 | |
| | FD3535B7H | | 8 | 22.10 | 176.8 | |
| | FD6666B7D | | 5 | 116.50 | 582.5 | |
| | T2330 | | 2 | 12.40 | 24.8 | (用于主材装爬梯) |
| | T3605 | | 1 | 19.00 | 19.0 | (用于主材装爬梯) |
| | T6980 | | 2 | 36.20 | 72.4 | (用于主材装爬梯) |
| | | | | | | |
| | | | | | | |
| 合计 | | | | 14191.0 kg(用于主材带脚钉) | | |
| 合计 | | | | 14330.6 kg(用于主材装爬梯) | | |

## 螺栓、脚钉、垫圈明细表

| 名称 | 级别 | 规格 | 符号 | 数量 | 重量(kg) | 备注 |
|---|---|---|---|---|---|---|
| 螺栓 | 6.8级 | M16X45 | ◪ | 64 | 10.8 | 用于主材装爬梯 |
| | | M16X60 | ⊗ | 48 | 9.6 | |
| | | M20X65 | ∅ | 82 | 28.9 | |
| | 8.8级 | M24X75 | ⊘ | 128 | 75.9 | |
| | | M20X90 | ○ | 12 | 5.7 | 法兰螺栓 |
| | | M24X115 | ○ | 88 | 73.9 | 法兰螺栓 |
| | | M39X175 | ○ | 56 | 198.9 | 法兰螺栓 |
| | | M39X195 | ○ | 28 | 104.7 | 法兰螺栓 无扣长97mm |
| 脚钉 | 6.8级 | M16X200 | ⊕ | 208 | 91.2 | 用于主材装爬梯 |
| | | M16X200 | ⊕ | 260 | 114.0 | 用于主材带脚钉 |
| | | | | | | |
| 垫圈 | Q235 | | 规格X个数 | | | |
| 合计 | | | | 611.6 kg | | (用于主材带脚钉) |
| 合计 | | | | 599.6 kg | | (用于主材装爬梯) |

说明：1.材料表为一个塔腿的重量。

2.本段塔腿为铁塔D腿，安装爬梯，
当为A、B、C腿时需焊接脚钉连接槽钢。

| | | | | | | | |
|---|---|---|---|---|---|---|---|
| 山东电力工程咨询院有限公司 | | | | | 浙江特高压交流环网工程线路 | 工程 | 施工图 设计阶段 |
| 批准 | 雷振 | 校核 | 马一丹 | | SZK31102A双回路直线塔 | | 56 |
| 审核 | 高鹏鹏 | | | | 120.0-0.0m呼高腿部结构图(1/2) | | |
| | | 设计/勘测 | 潘胜龙 | | 123.0-3.0m呼高腿部结构图(1/2) | | |
| 电气 | 赵文周 | 2026.08 | | | | | |
| 专业 | 会签 | 日期 | 比例 | 1:40 | 日期 | 2026年08月 | 图号 37-SA36901S-T0121-125 | 版本 |