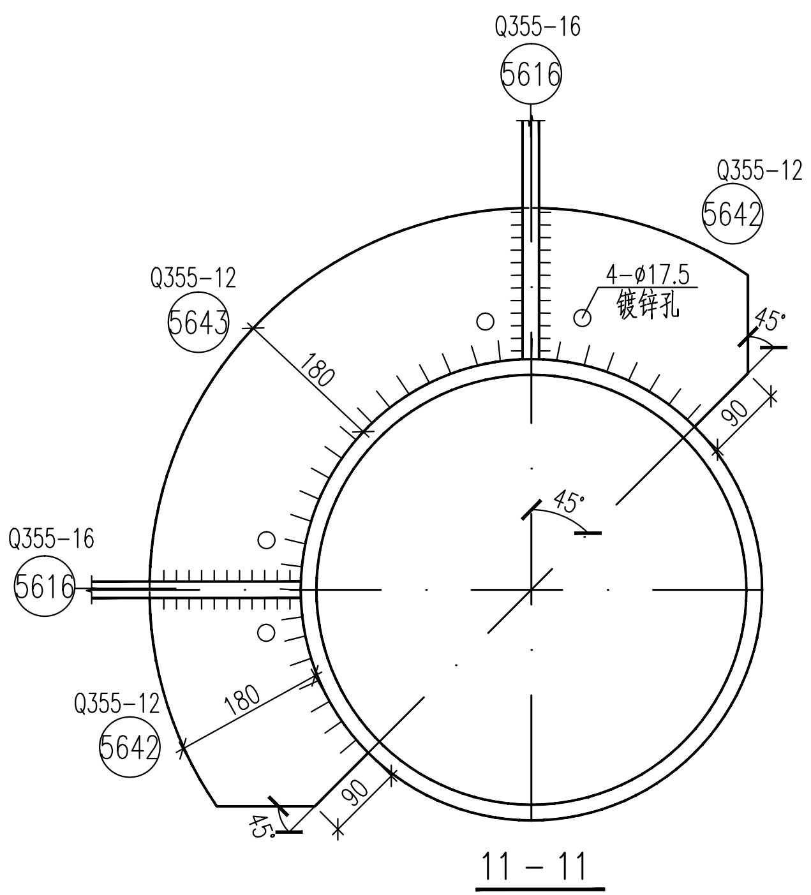
Q355-16
5616
Q355-12
5642
Q355-12
5643
4-ø17.5
镀锌孔
180
90
45°
Q355-16
5616
Q355-12
5642
180
90
45

11－11
1:20

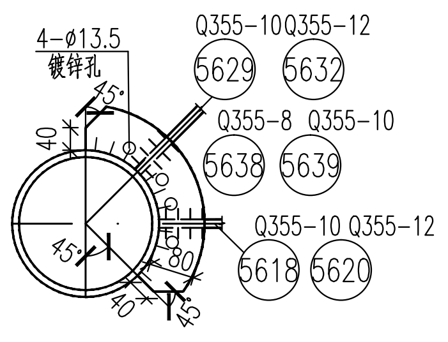
4-ø13.5
镀锌孔
Q355-10
5629
Q355-12
5632
Q355-8
5638
Q355-10
5639
Q355-10
5618
Q355-12
5620
40
45

13－13
1:20

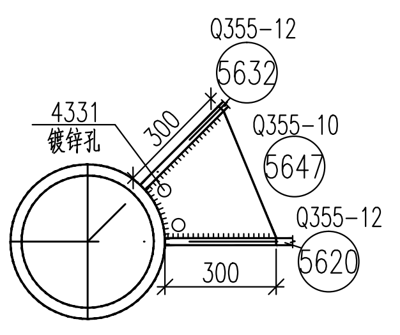
4ø13.5
镀锌孔
Q355-12
5632
Q355-10
5647
Q355-12
5620
300
300

14－14
1:10

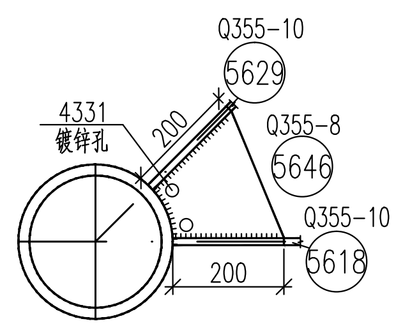
4ø13.5
镀锌孔
Q355-10
5629
Q355-8
5646
Q355-10
5618
200
200

15－15
1:10

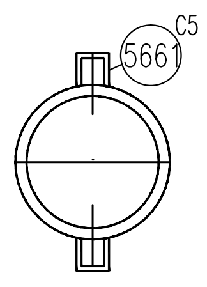

16－16
1:10

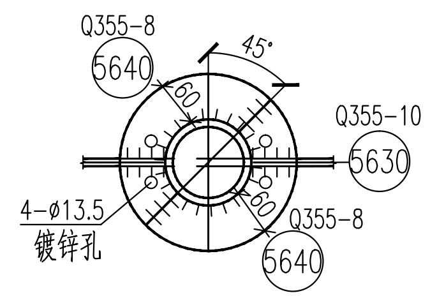
Q355-8
5640
45°
Q355-10
5630
4-ø13.5
镀锌孔
Q355-8
5640

17－17
1:10

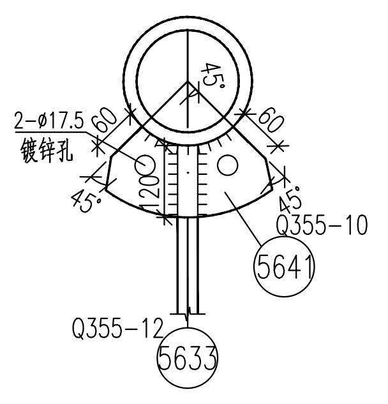
2-ø17.5
镀锌孔
45
Q355-10
5641
Q355-12
5633

18－18
1:10

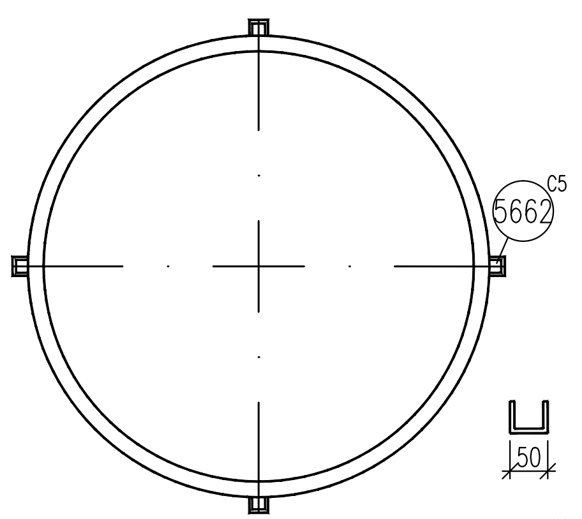
C5
5662
50
50
25

安全带挂点示意
扶手设置示意

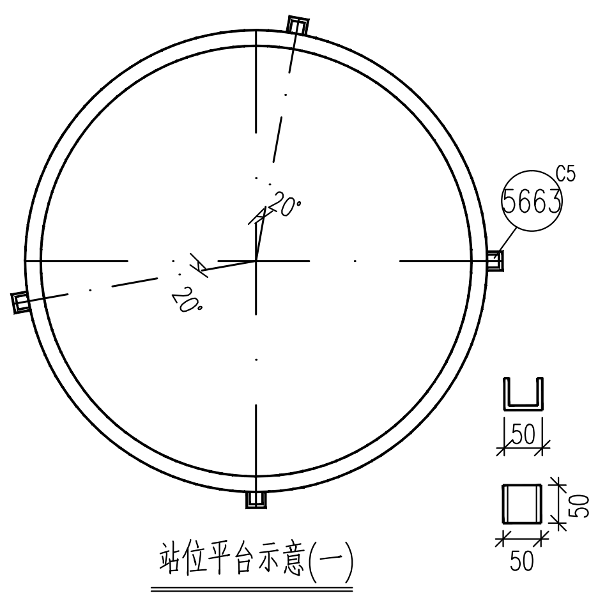
C5
5663
20
20
50
50
50

站位平台示意(一)

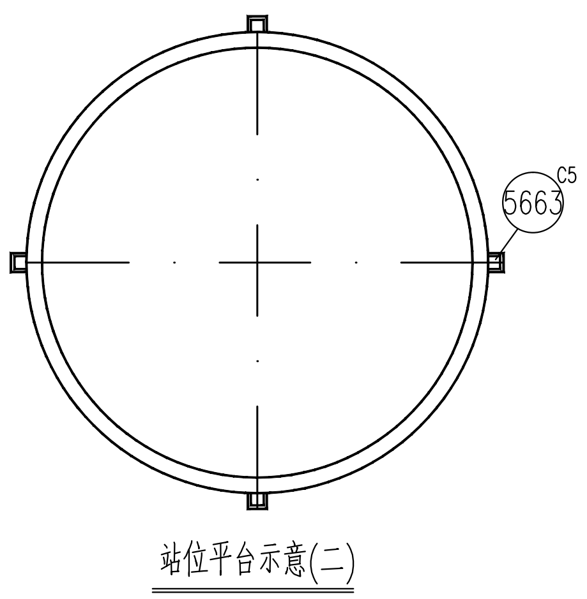

站位平台示意(二)

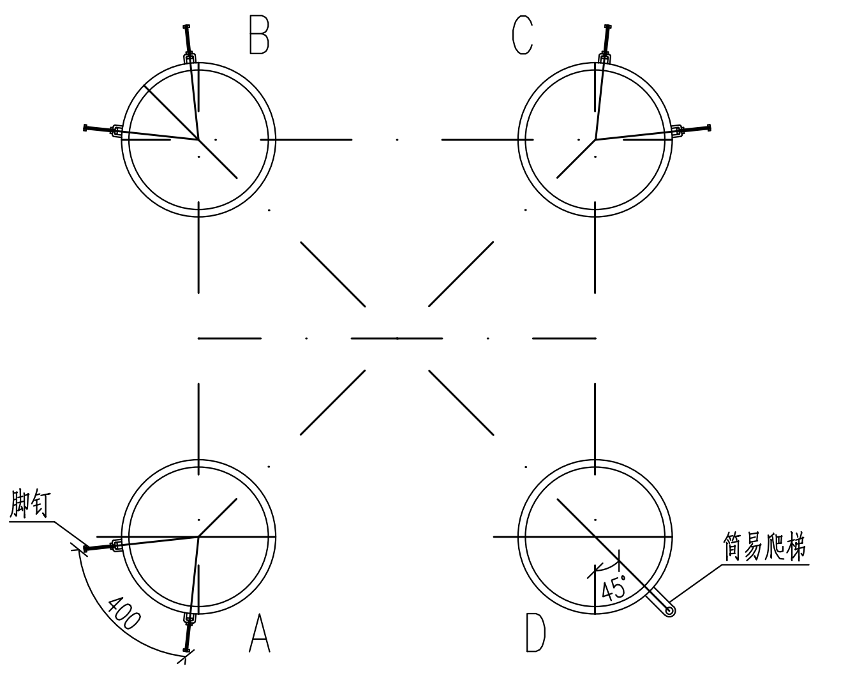
B
C
A
D
脚钉
400
攀爬爬梯
45°

爬梯脚钉示意图

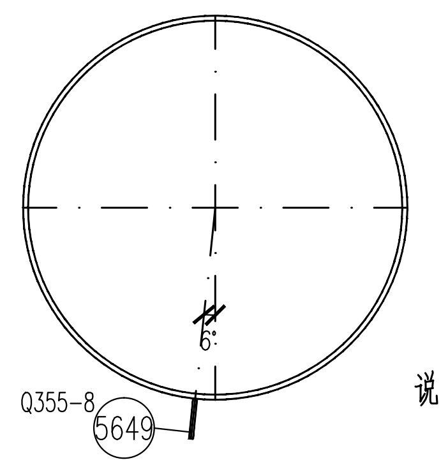
6°
Q355-8
5649

接地孔位置示意图
1:20

说明：接地孔安装板⑤⑥④⑨避开法兰加劲板和地脚法兰螺栓所在角度，以避免接地引下线和法兰加劲板相碰。

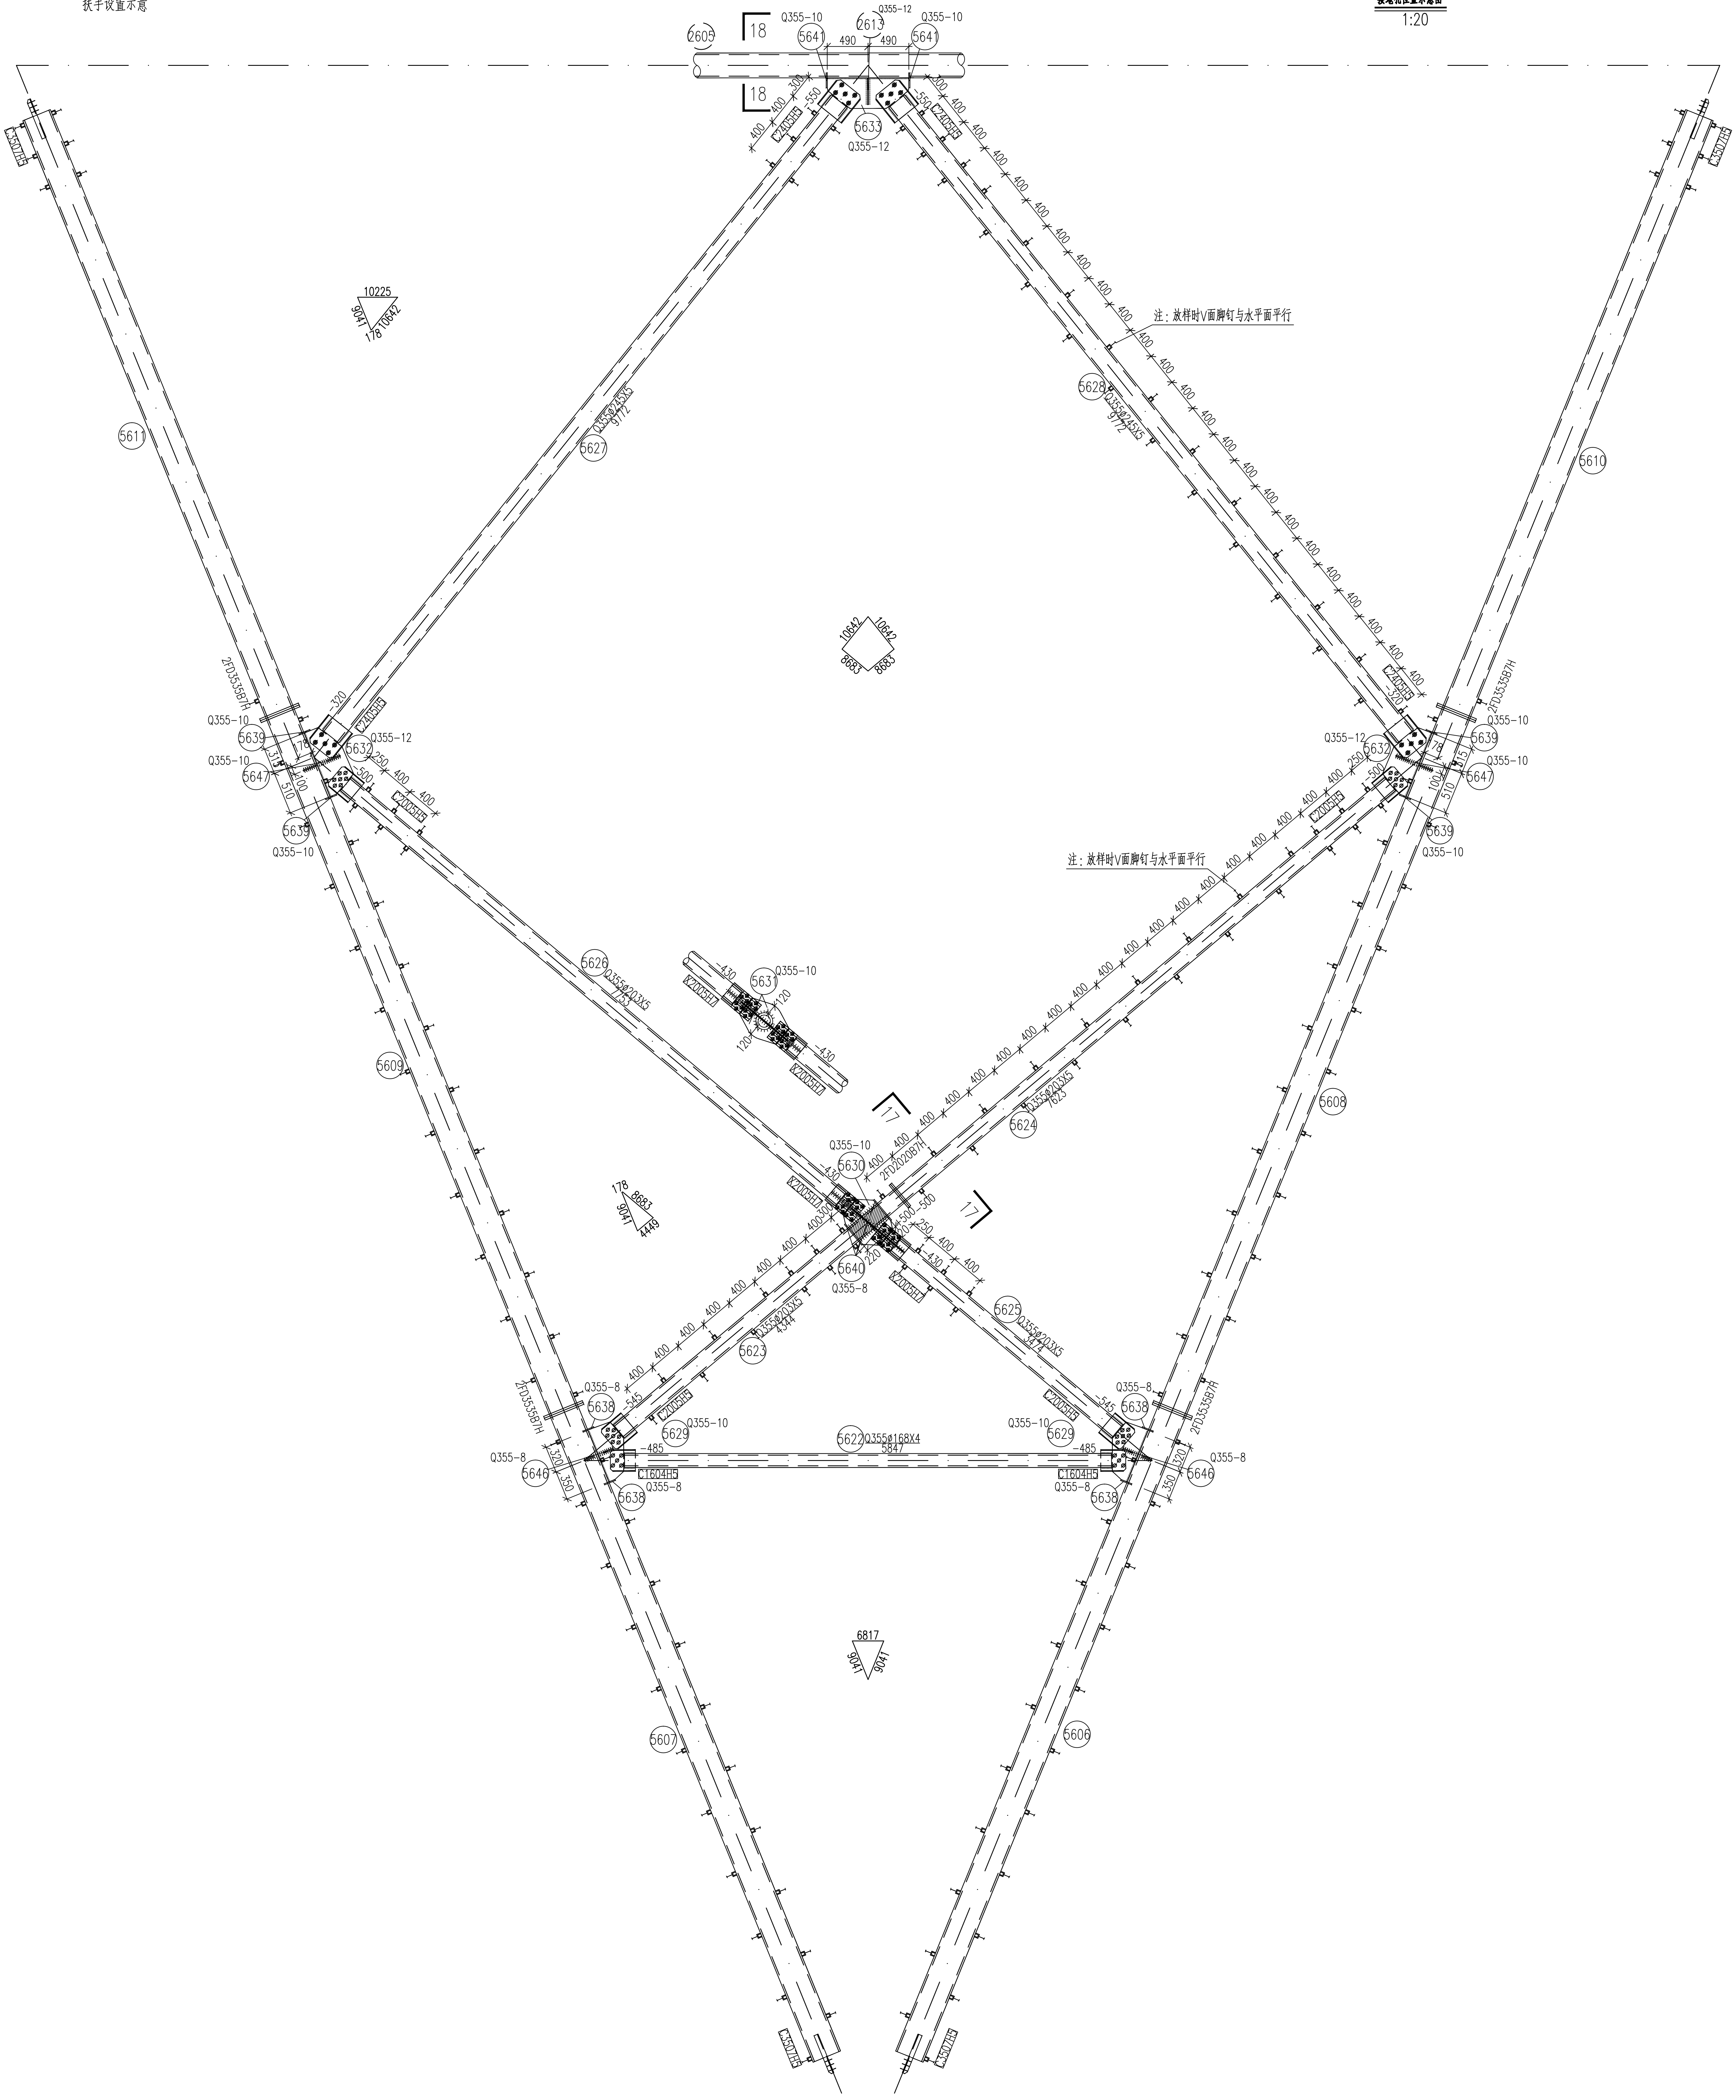
2609
18
18
Q355-10
5641
Q355-12
2613
Q355-10
5641
490
490
5633
Q355-12
10225
10642
5611
5627
5628
5610
10642
10642
8683
8683
Q355-10
5639
Q355-12
5632
Q355-10
5647
5639
Q355-10
Q355-12
5632
Q355-10
5639
Q355-10
5647
5639
Q355-10
5626
5631
Q355-10
5609
5608
17
17
Q355-10
5630
5640
Q355-8
5624
5623
5625
Q355-8
5638
Q355-10
5629
5622 Q355ø168X4
5847
Q355-10
5629
Q355-8
5638
Q355-8
5646
5638
Q355-8
Q355-8
5646
5638
Q355-8
C1604H5
C1604H5
6817
5607
5606
400

注：放样时V面脚钉与水平面平行

注：放样时V面脚钉与水平面平行

1－1

| | | | | | | |
|---|---|---|---|---|---|---|
| 山东电力工程咨询院有限公司 | | | | 浙江特高压交流环网工程线路 工程 | 施工图 | 设计阶段 |
| 批　准 | 雷强 | 校　核 | 马一丹 | SZK31102A双回路直线塔<br>120.0-0.0m呼高腿部结构图（2/2）<br>123.0-3.0m呼高腿部结构图（2/2） | ㊻ | |
| 审　核 | 高锡鹏 | | | | | |
| | | 设计/勘测 | 潘旭光 | | | |
| 比　例 | 1：40 | 日　期 | 2026年 08月 | 图　号 | 37-SA36901S-T0121-126 | 版本 |