


上接㉑㉖段

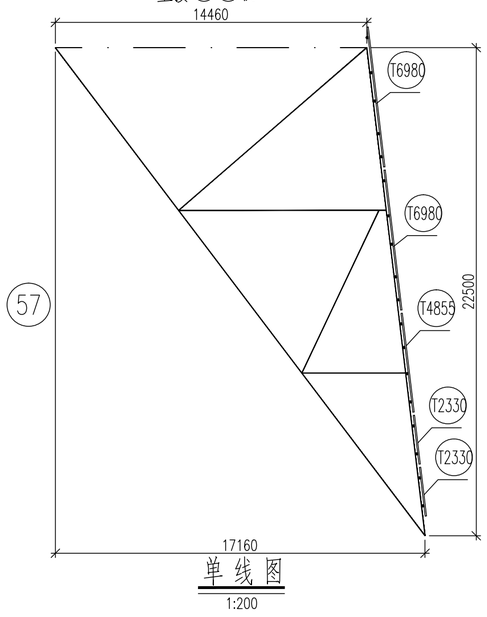


单线图
1:200

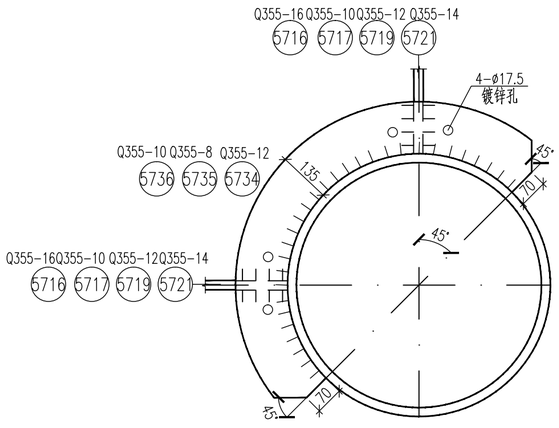


2 - 2
1:20

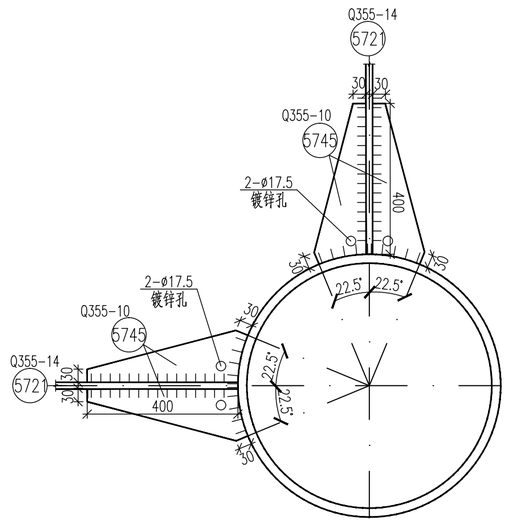

3 - 3
1:20

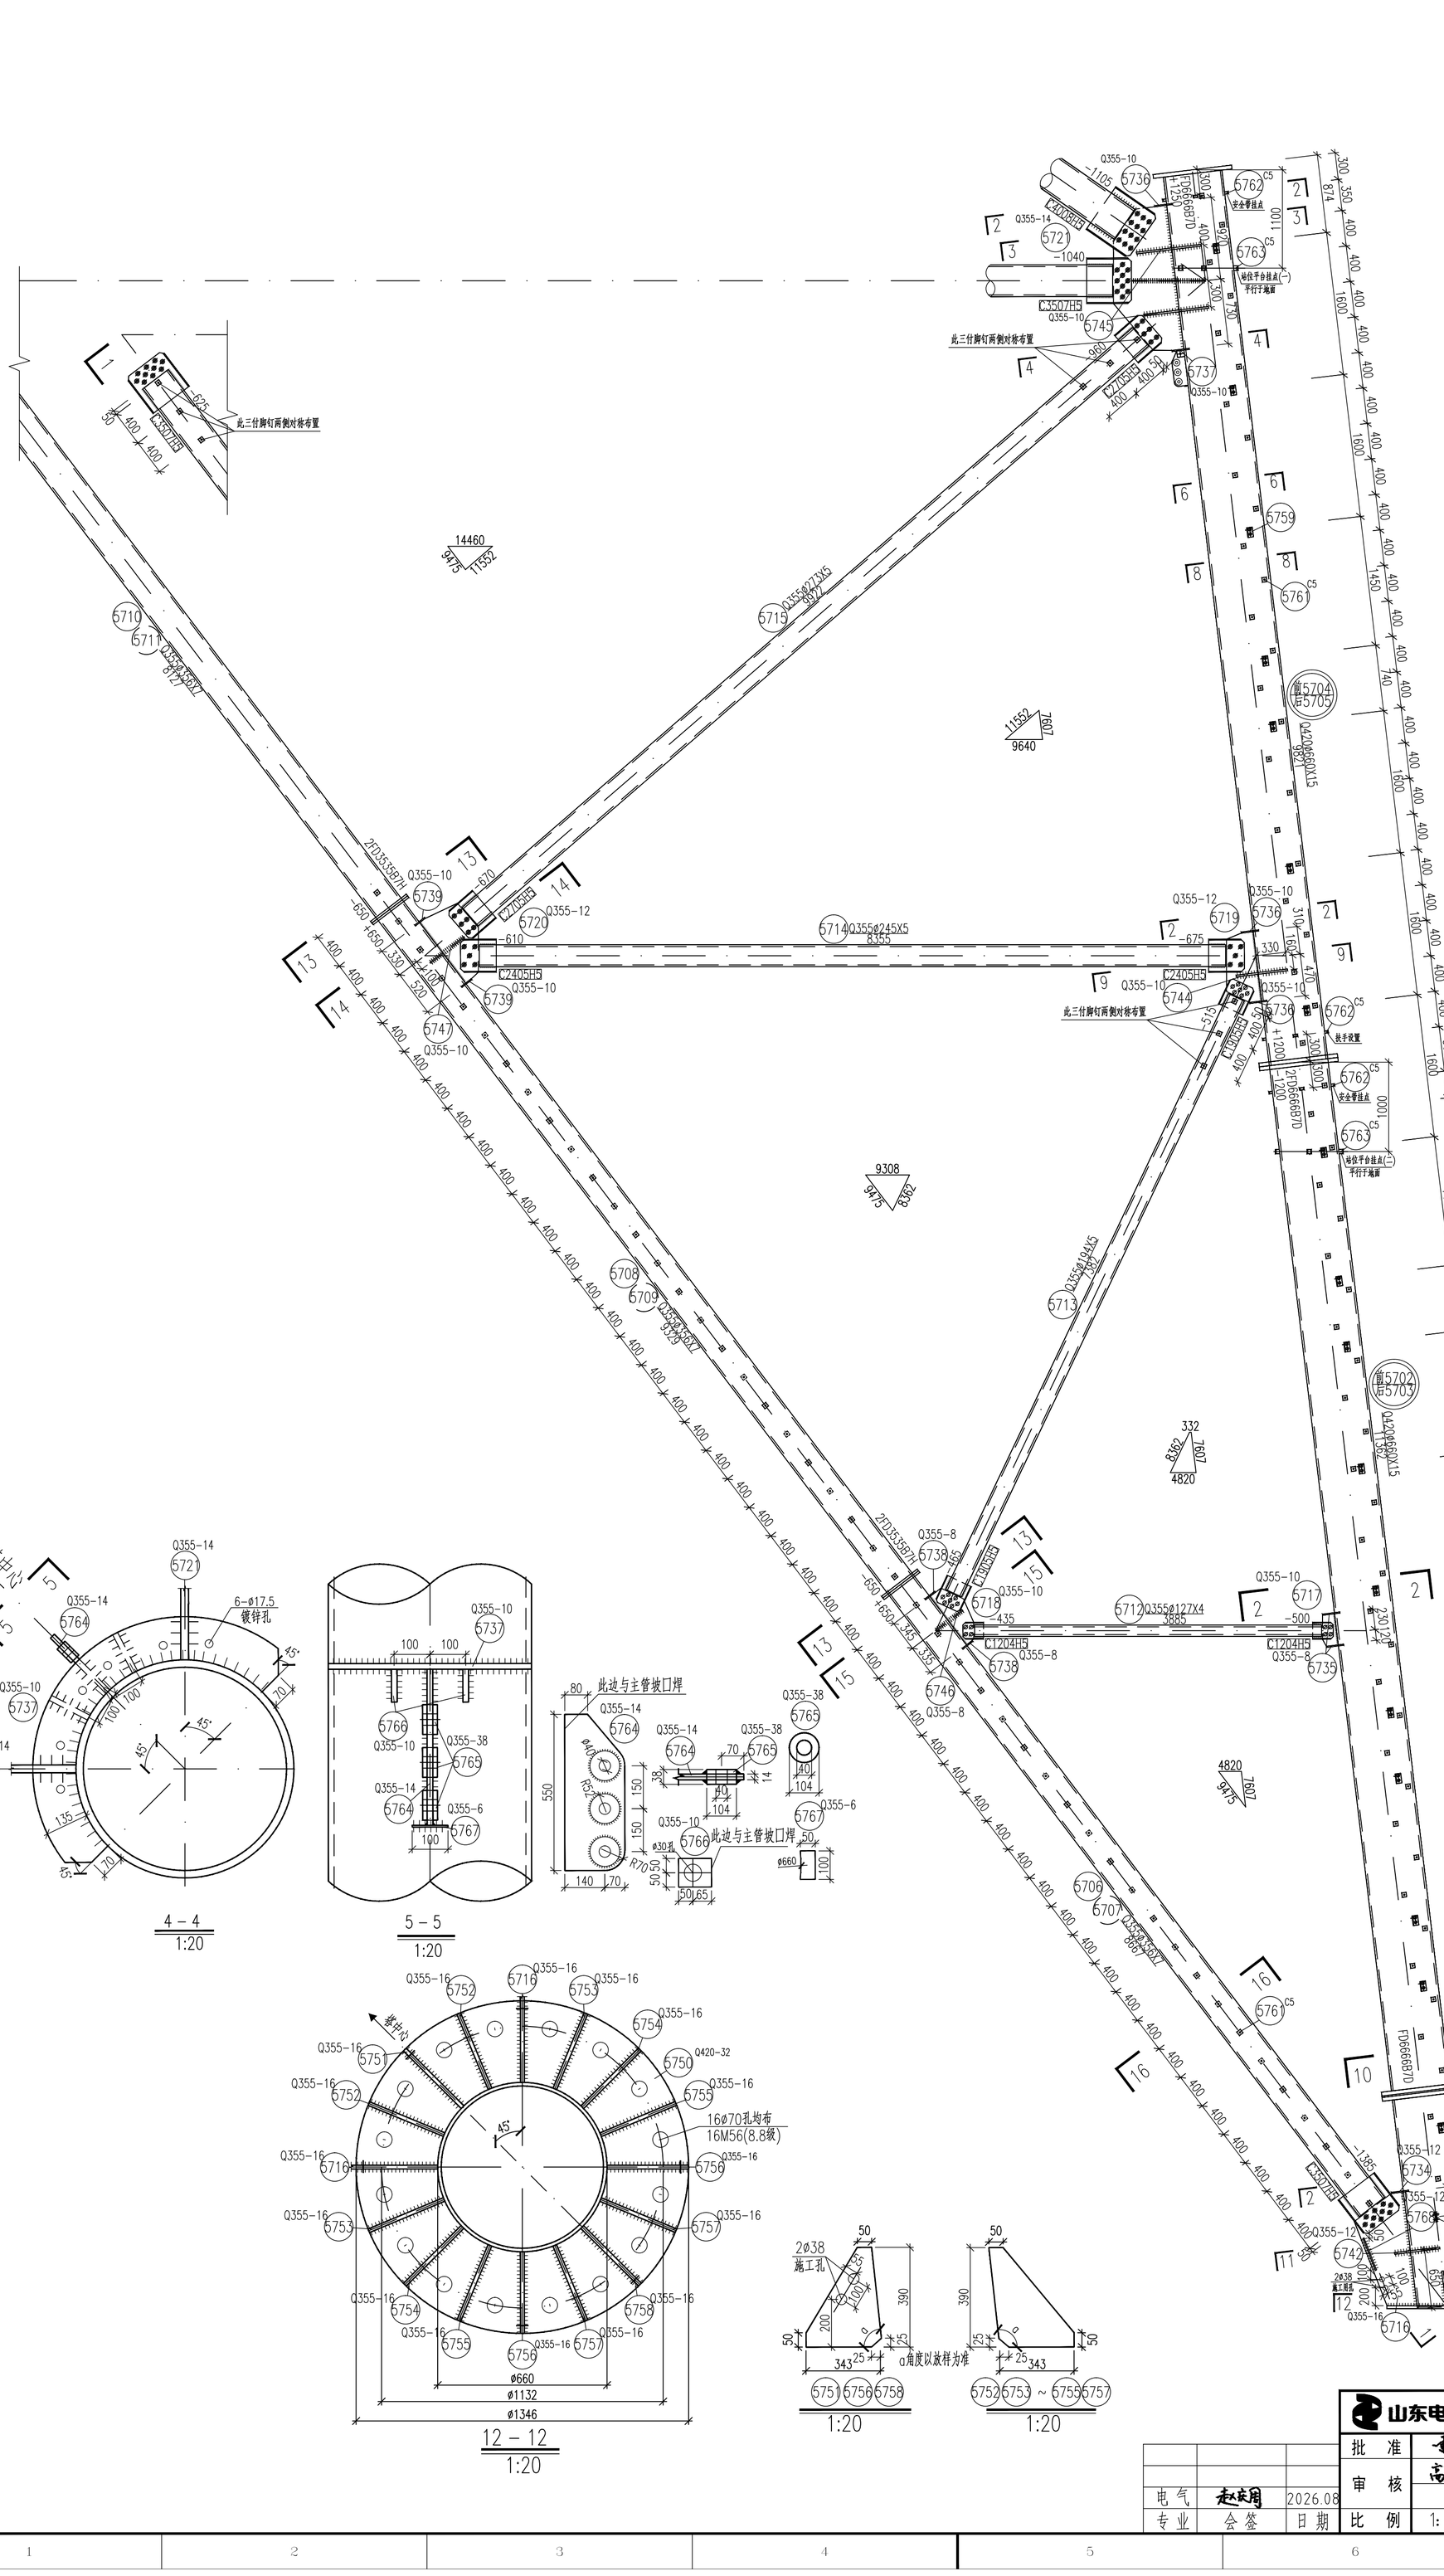

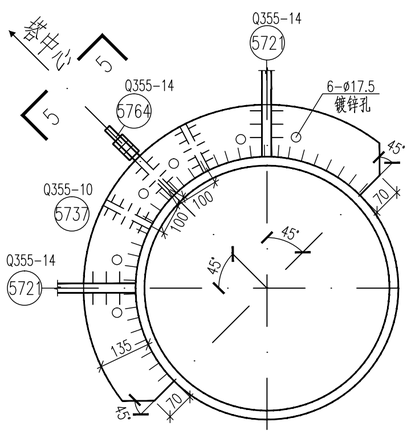


4 - 4
1:20

5 - 5
1:20

12 - 12
1:20

1:20

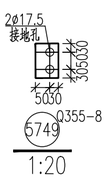

1:20

构件明细表

编号	规格	长度(mm)	数量	重量(kg) 一件	重量(kg) 小计	备注
5701	Q420ø660X15	2337	1	557.61	557.6	一端切弧 装爬梯
5701A	Q420ø660X15	2337	0	557.61	0.0	一端切弧 带脚钉
5702	Q420ø660X15	11362	1	2710.97	2711.0	装爬梯
5703	Q420ø660X15	11362	0	2710.97	0.0	带脚钉
5704	Q420ø660X15	9821	1	2343.29	2343.3	装爬梯
5705	Q420ø660X15	9821	0	2343.29	0.0	带脚钉
5706	Q355ø356X7	8667	1	522.17	522.2	带脚钉
5707	Q355ø356X7	8667	1	522.17	522.2	带脚钉
5708	Q355ø356X7	9329	1	562.05	562.0	带脚钉
5709	Q355ø356X7	9329	1	562.05	562.0	带脚钉
5710	Q355ø356X7	8127	1	489.64	489.6	带脚钉
5711	Q355ø356X7	8127	1	489.64	489.6	带脚钉
5712	Q355ø127X4	3885	2	47.14	94.3	
5713	Q355ø194X5	7382	2	172.04	344.1	带脚钉
5714	Q355ø245X5	8355	2	247.26	494.5	
5715	Q355ø273X5	9922	2	327.89	655.8	带脚钉
5716	Q355-16X646	1452	2	117.81	235.6	
5717	Q355-10X188	385	2	5.68	11.4	
5718	Q355-10X329	748	2	19.32	38.6	
5719	Q355-12X418	858	2	33.78	67.6	
5720	Q355-12X542	935	2	47.74	95.5	
5721	Q355-14X793	1815	2	158.18	316.4	
5722	Q355ø168X4	5887	1	95.24	95.2	
5723	Q355ø203X5	4462	1	108.94	108.9	带脚钉
5724	Q355ø203X5	7812	1	190.73	190.7	带脚钉
5725	Q355ø203X5	3597	1	87.82	87.8	带脚钉
5726	Q355ø203X5	7947	1	194.03	194.0	带脚钉
5727	Q355ø273X5	10187	1	336.64	336.6	带脚钉
5728	Q355ø273X5	10187	1	336.64	336.6	带脚钉
5729	Q355-10X375	748	2	22.02	44.0	
5730	Q355-10X610	484	1	23.18	23.2	
5731	Q355-10X242	605	2	11.49	23.0	
5732	Q355-12X409	935	2	36.02	72.0	
5733	Q355-12X399	1056	1	39.69	39.7	
5734	Q355-12X135	1374	1	17.47	17.5	
5735	Q355-8X135	1374	4	11.65	46.6	
5736	Q355-10X135	1374	1	14.56	14.6	
5737	Q355-10X135	1374	1	14.56	14.6	
5738	Q355-8X80	565	4	2.84	11.4	
5739	Q355-10X80	565	4	3.55	14.2	
5740	Q355-8X60	454	4	1.71	6.8	
5741	Q355-10X120	362	2	3.41	6.8	
5742	Q355-12X180	330	2	5.60	11.2	
5743	Q355-12X180	660	1	11.19	11.2	
5744	Q355-10X150	344	4	4.05	16.2	
5745	Q355-10X150	509	8	5.99	47.9	
5746	Q355-8X200	241	2	3.03	6.1	
5747	Q355-10X300	284	2	6.69	13.4	
5748	-16X885	885	1	77.26	77.3	遮水板
5749	Q355-8X80	110	1	0.55	0.6	接地孔用
5750	Q420-32X1346	1346	1	272.50	272.5	
5751	Q355-16X343	390	1	16.80	16.8	
5752	Q355-16X343	390	2	16.80	33.6	
5753	Q355-16X343	390	2	16.80	33.6	
5754	Q355-16X343	390	2	16.80	33.6	
5755	Q355-16X343	390	2	16.80	33.6	
5756	Q355-16X343	390	2	16.80	33.6	
5757	Q355-16X343	390	2	16.80	33.6	
5758	Q355-16X343	390	1	16.80	16.8	
5759	Q355L63X5	310	17	1.49	25.3	火曲 (用于主材装爬梯)
5760	Q355-6X100	180	17	0.85	14.4	火曲 (用于主材装爬梯)
5761	C5	50	216	0.27	58.3	槽钢 (用于主材装爬梯)
5761	C5	50	273	0.27	73.7	槽钢 (用于主材带脚钉)
5762	C5	25	12	0.14	1.7	槽钢
5763	C5	50	8	0.27	2.2	槽钢
5764	Q355-14X210	550	1	12.69	12.7	
5765	Q355-38X104	104	3	3.23	9.7	
5766	Q355-10X100	115	2	0.90	1.8	
5767	Q355-6X50	100	1	0.24	0.2	
5768	Q355-12X100	384	2	3.62	7.2	
	C1204H5		4	4.19	16.8	
	C1604H5		2	7.12	14.2	
	C1905H5		4	8.80	35.2	
	C2005H5		4	9.74	39.0	
	C2405H5		4	17.27	69.1	
	C2705H5		8	18.10	144.8	
	X2005H7		2	24.40	48.8	
	C3507H5		4	36.27	145.1	
	FD2020B7H		2	8.60	17.2	
	FD3535B7H		8	22.10	176.8	
	FD6666B7D		5	116.50	582.5	
	T2330		2	12.40	24.8	(用于主材装爬梯)
	T4855		1	25.00	25.0	(用于主材装爬梯)
	T6980		2	36.20	72.4	(用于主材装爬梯)
合计					14887.8 kg	(用于主材带脚钉)
合计					15034.3 kg	(用于主材装爬梯)

螺栓、脚钉、垫圈明细表

名称	级别	规格	符号	数量	重量(kg)	备注
螺栓	6.8级	M16X45	⊘	68	11.5	用于主材装爬梯
		M16X60	⊗	48	9.6	
		M20X65	∅	82	28.9	
	8.8级	M24X75	⊘	132	78.2	
		M20X90	○	12	5.7	法兰螺栓
		M24X115	○	88	73.9	法兰螺栓
		M39X175	○	56	198.9	法兰螺栓
		M39X195	○	28	104.7	法兰螺栓 无扣长97mm
脚钉	6.8级	M16X200	⊕	216	94.7	用于主材装爬梯
		M16X200	⊕	273	119.7	用于主材带脚钉
垫圈	Q235		规格X个数			
合计				619.6 kg		(用于主材带脚钉)
合计				606.1 kg		(用于主材装爬梯)

说明：1.材料表为一个塔腿的重量。

2.本段塔腿为铁塔D腿，安装爬梯，
当为A、B、C腿时需焊接脚钉连接槽钢。

山东电力工程咨询院有限公司			浙江特高压交流环网工程线路	工程	施工图	设计阶段	
批准	雷强	校核	习一斗	SZK31102A双回路直线塔			57
审核	高鹏鹏			123.0-1.5m呼高腰部结构图(1/2)			
电气	赵庆周	2026.08	设计/勘测	126.0-4.5m呼高腰部结构图(1/2)			
专业	会签	日期	比例	1:40	日期	2026年08月	图号 37-SA36901S-T0121-127 版本