

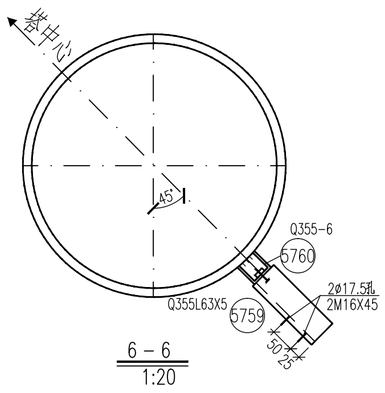



6 – 6
1:20

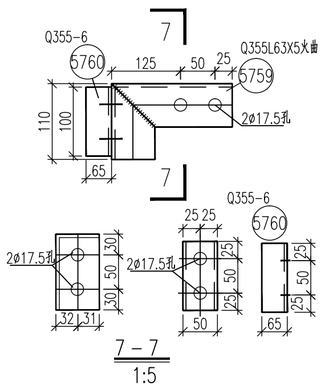


7 – 7
1:5

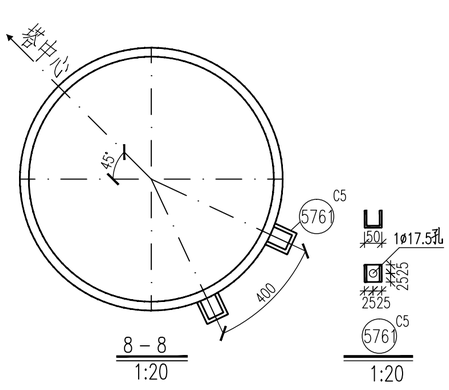


8 – 8
1:20

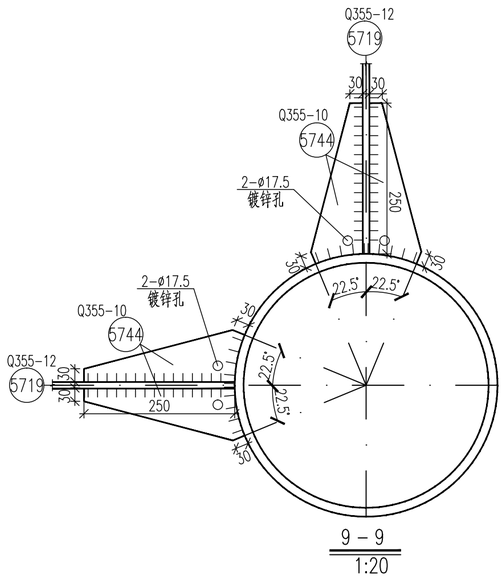

9 – 9
1:20

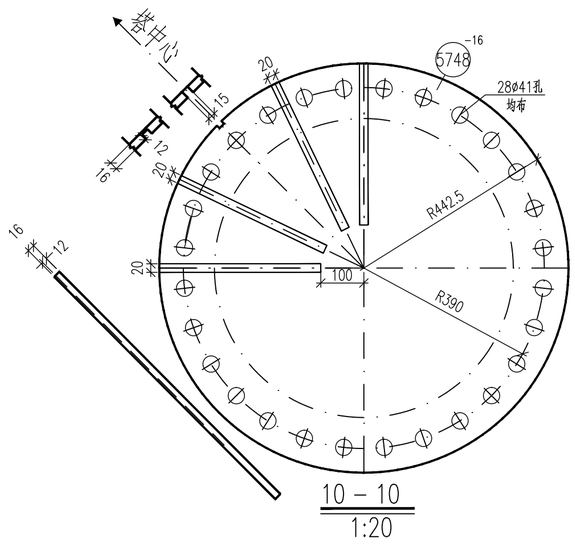

10 – 10
1:20

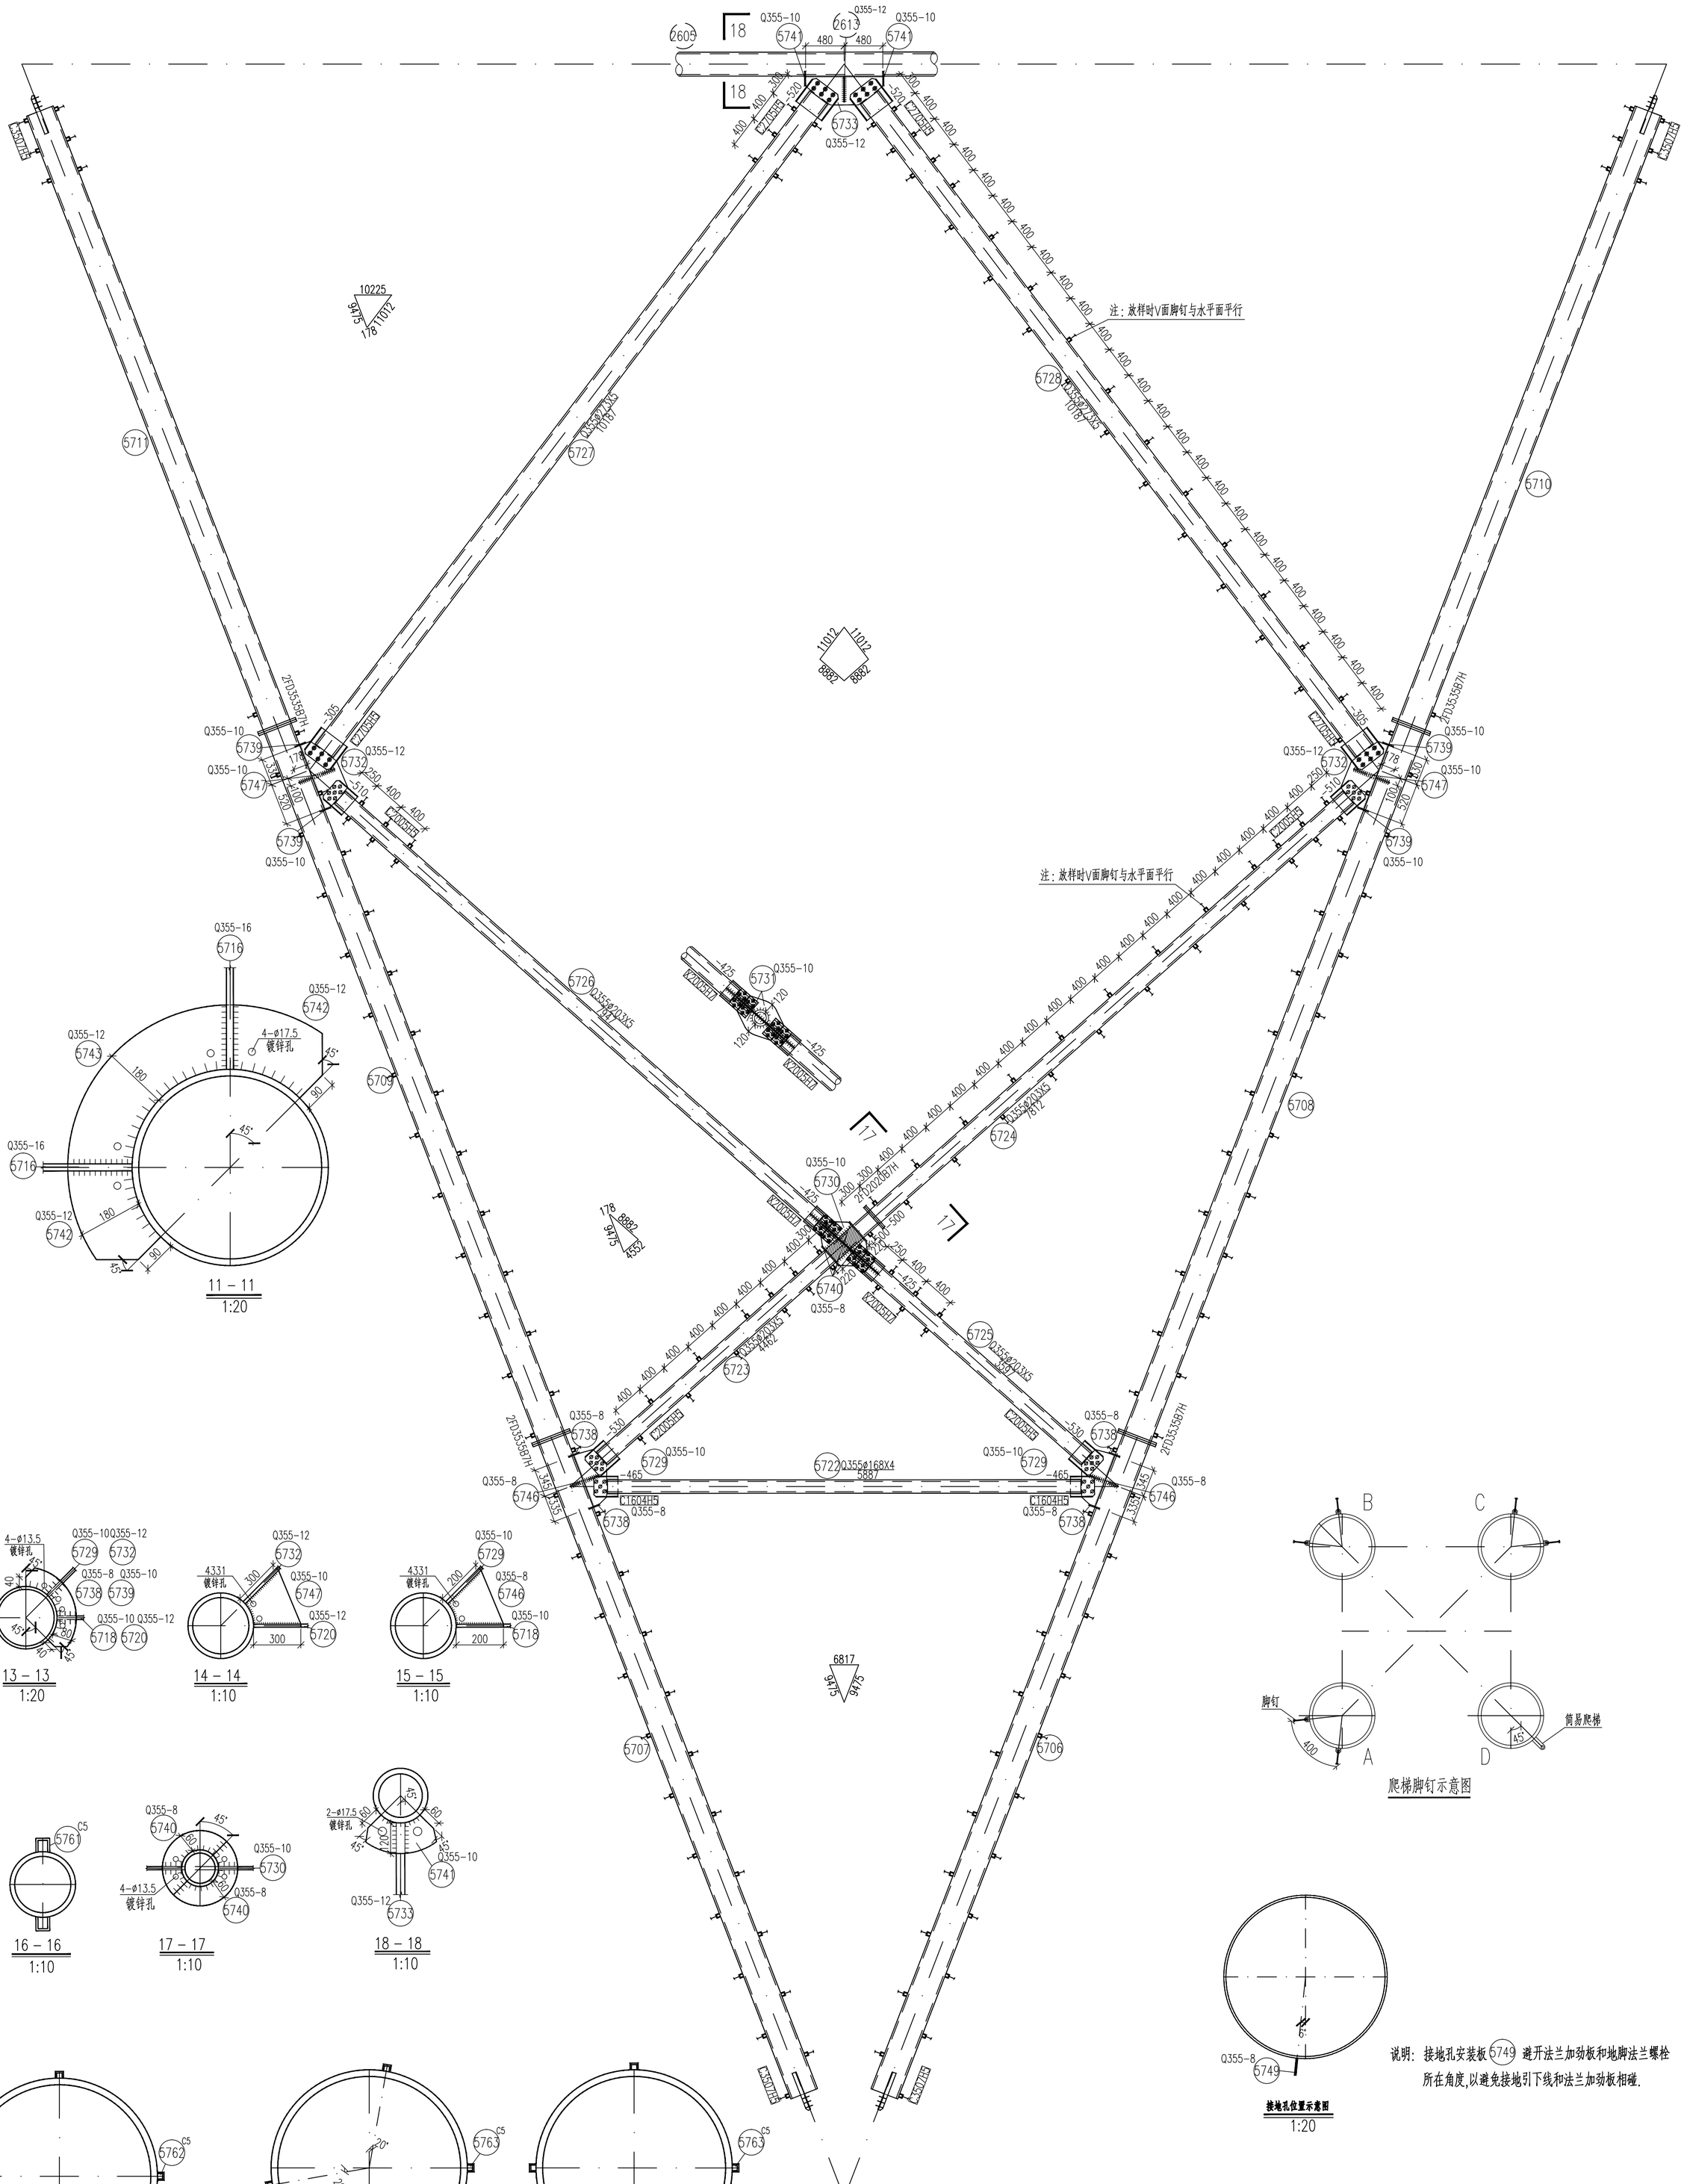

13 – 13
1:20

14 – 14
1:10

15 – 15
1:10

爬梯脚钉示意图

16 – 16
1:10

17 – 17
1:10

18 – 18
1:10

接地孔位置示意图
1:20

说明：接地孔安装板 5749 避开法兰加劲板和地脚法兰螺栓所在角度,以避免接地引下线和法兰加劲板相碰.

安全带挂点示意
扶手设置示意

站位平台示意(一)

站位平台示意(二)

山东电力工程咨询院有限公司				浙江特高压交流环网工程线路 工程	施工图 设计阶段
批 准	曹强	校 核	刘一丹	SZK31102A双回路直线塔 123.0-1.5m呼高腿部结构图(2/2) 126.0-4.5m呼高腿部结构图(2/2)	57
审 核	高鹏鹏	设计/勘测	潘祖龙		
比 例	1:40	日 期	2026年 08月	图 号 37-SA36901S-T0121-128	版本