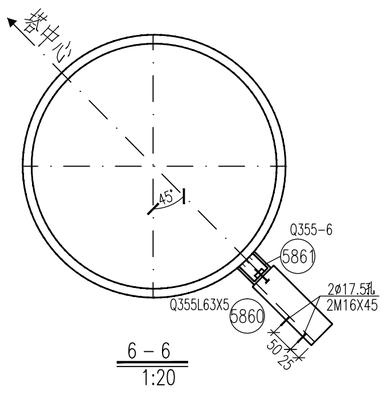
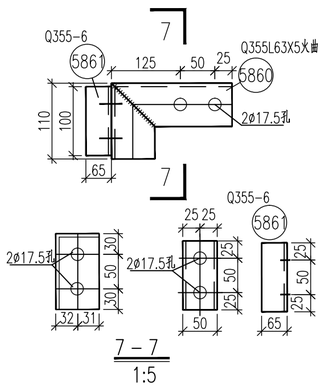
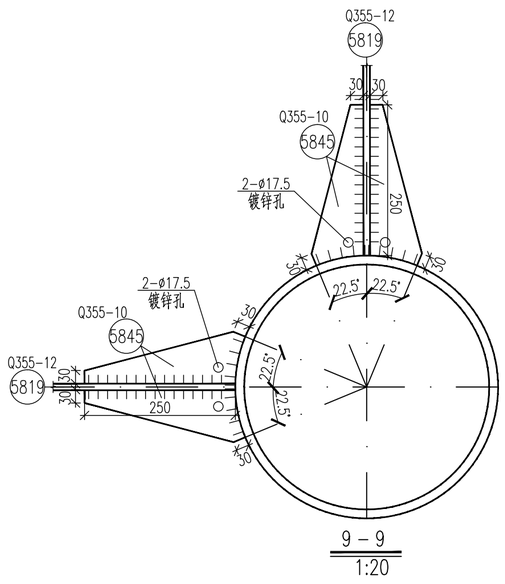


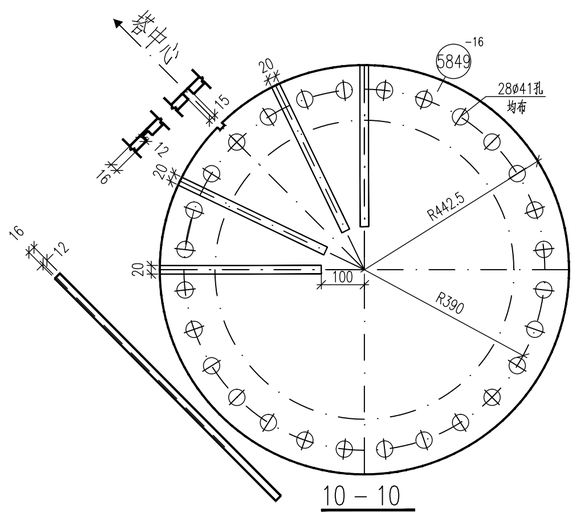

6 – 6
1:20



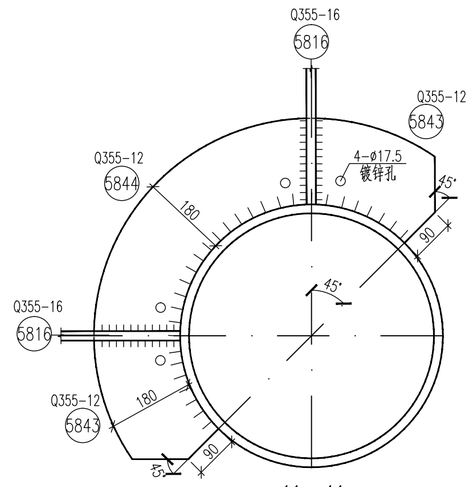

7 – 7
1:5



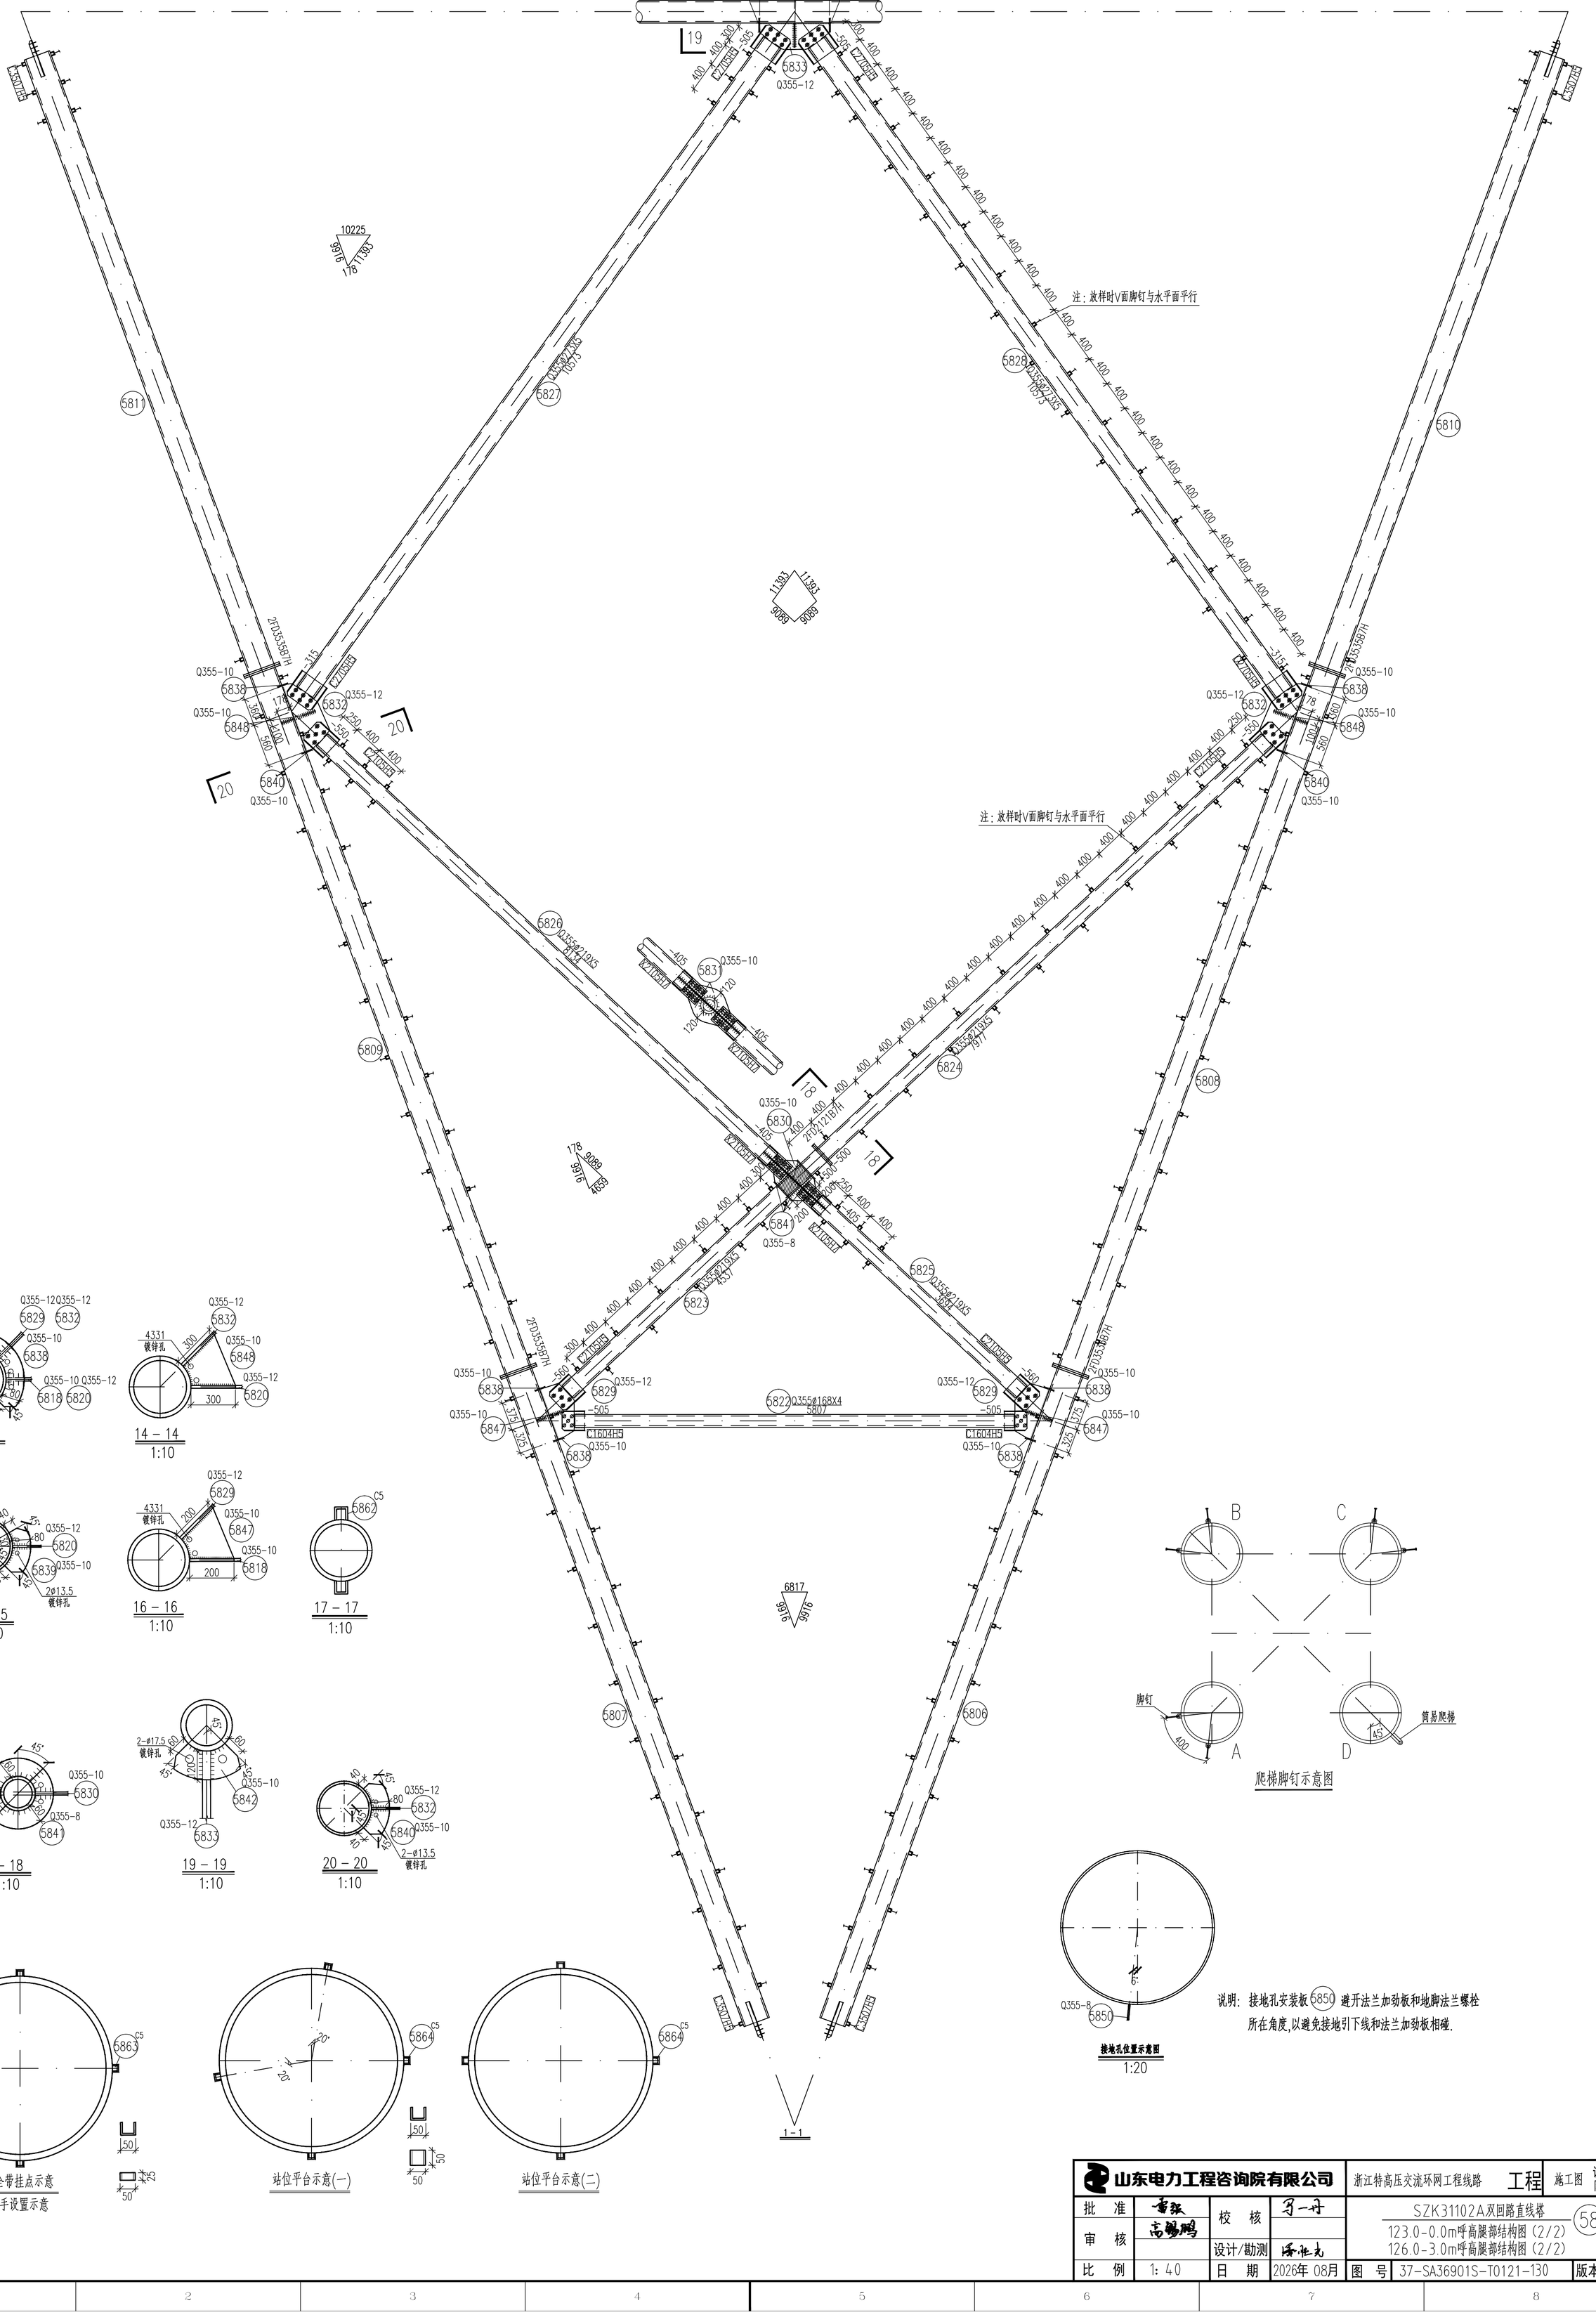

9 – 9
1:20




10 – 10
1:20




11 – 11
1:20



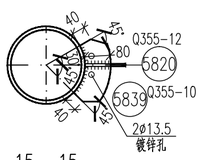




13 – 13
1:20




14 – 14
1:10




15 – 15
1:10




16 – 16
1:10




17 – 17
1:10




爬梯脚钉示意图




18 – 18
1:10




19 – 19
1:10

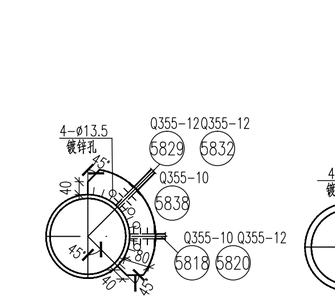



20 – 20
1:10




接地孔位置示意图
1:20

说明：接地孔安装板5850避开法兰加劲板和地脚法兰螺栓所在角度,以避免接地引下线和法兰加劲板相碰.




安全带挂点示意
扶手设置示意




站位平台示意(一)




站位平台示意(二)

| | | | | | |
|---|---|---|---|---|---|
| 山东电力工程咨询院有限公司 | | | | 浙江特高压交流环网工程线路 工程 | 施工图 设计阶段 |
| 批准 | 高鹏鹏 | 校核 | | SZK31102A双回路直线塔<br>123.0-0.0m呼高腿部结构图(2/2)<br>126.0-3.0m呼高腿部结构图(2/2) | 58 |
| 审核 | | 设计/勘测 | | | |
| 比例 | 1:40 | 日期 | 2026年08月 | 图号 37-SA36901S-T0121-130 | 版本 |