

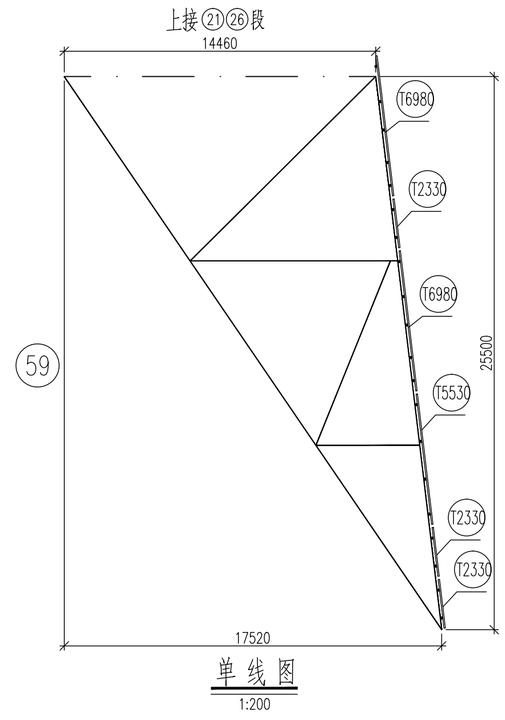



单线图
1:200

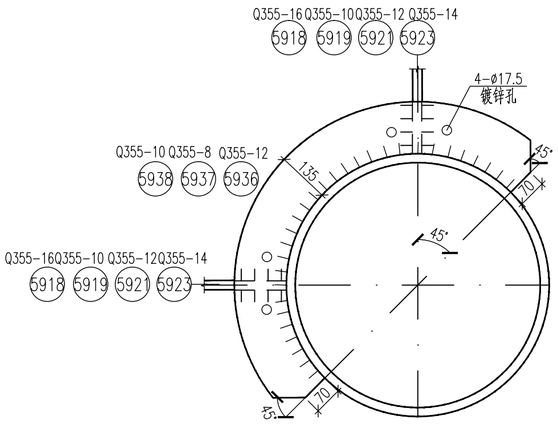


2 – 2
1:20

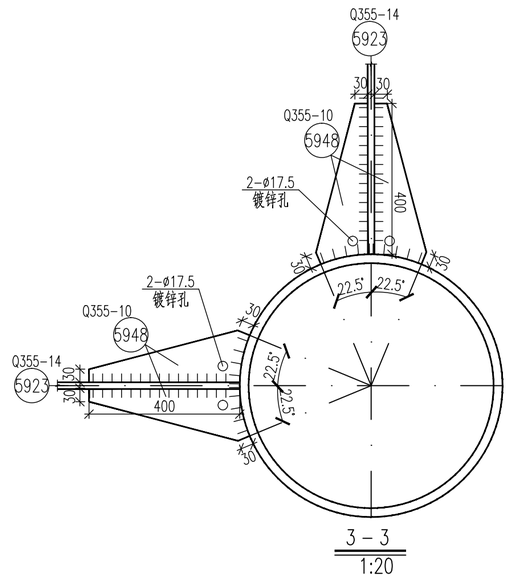


3 – 3
1:20

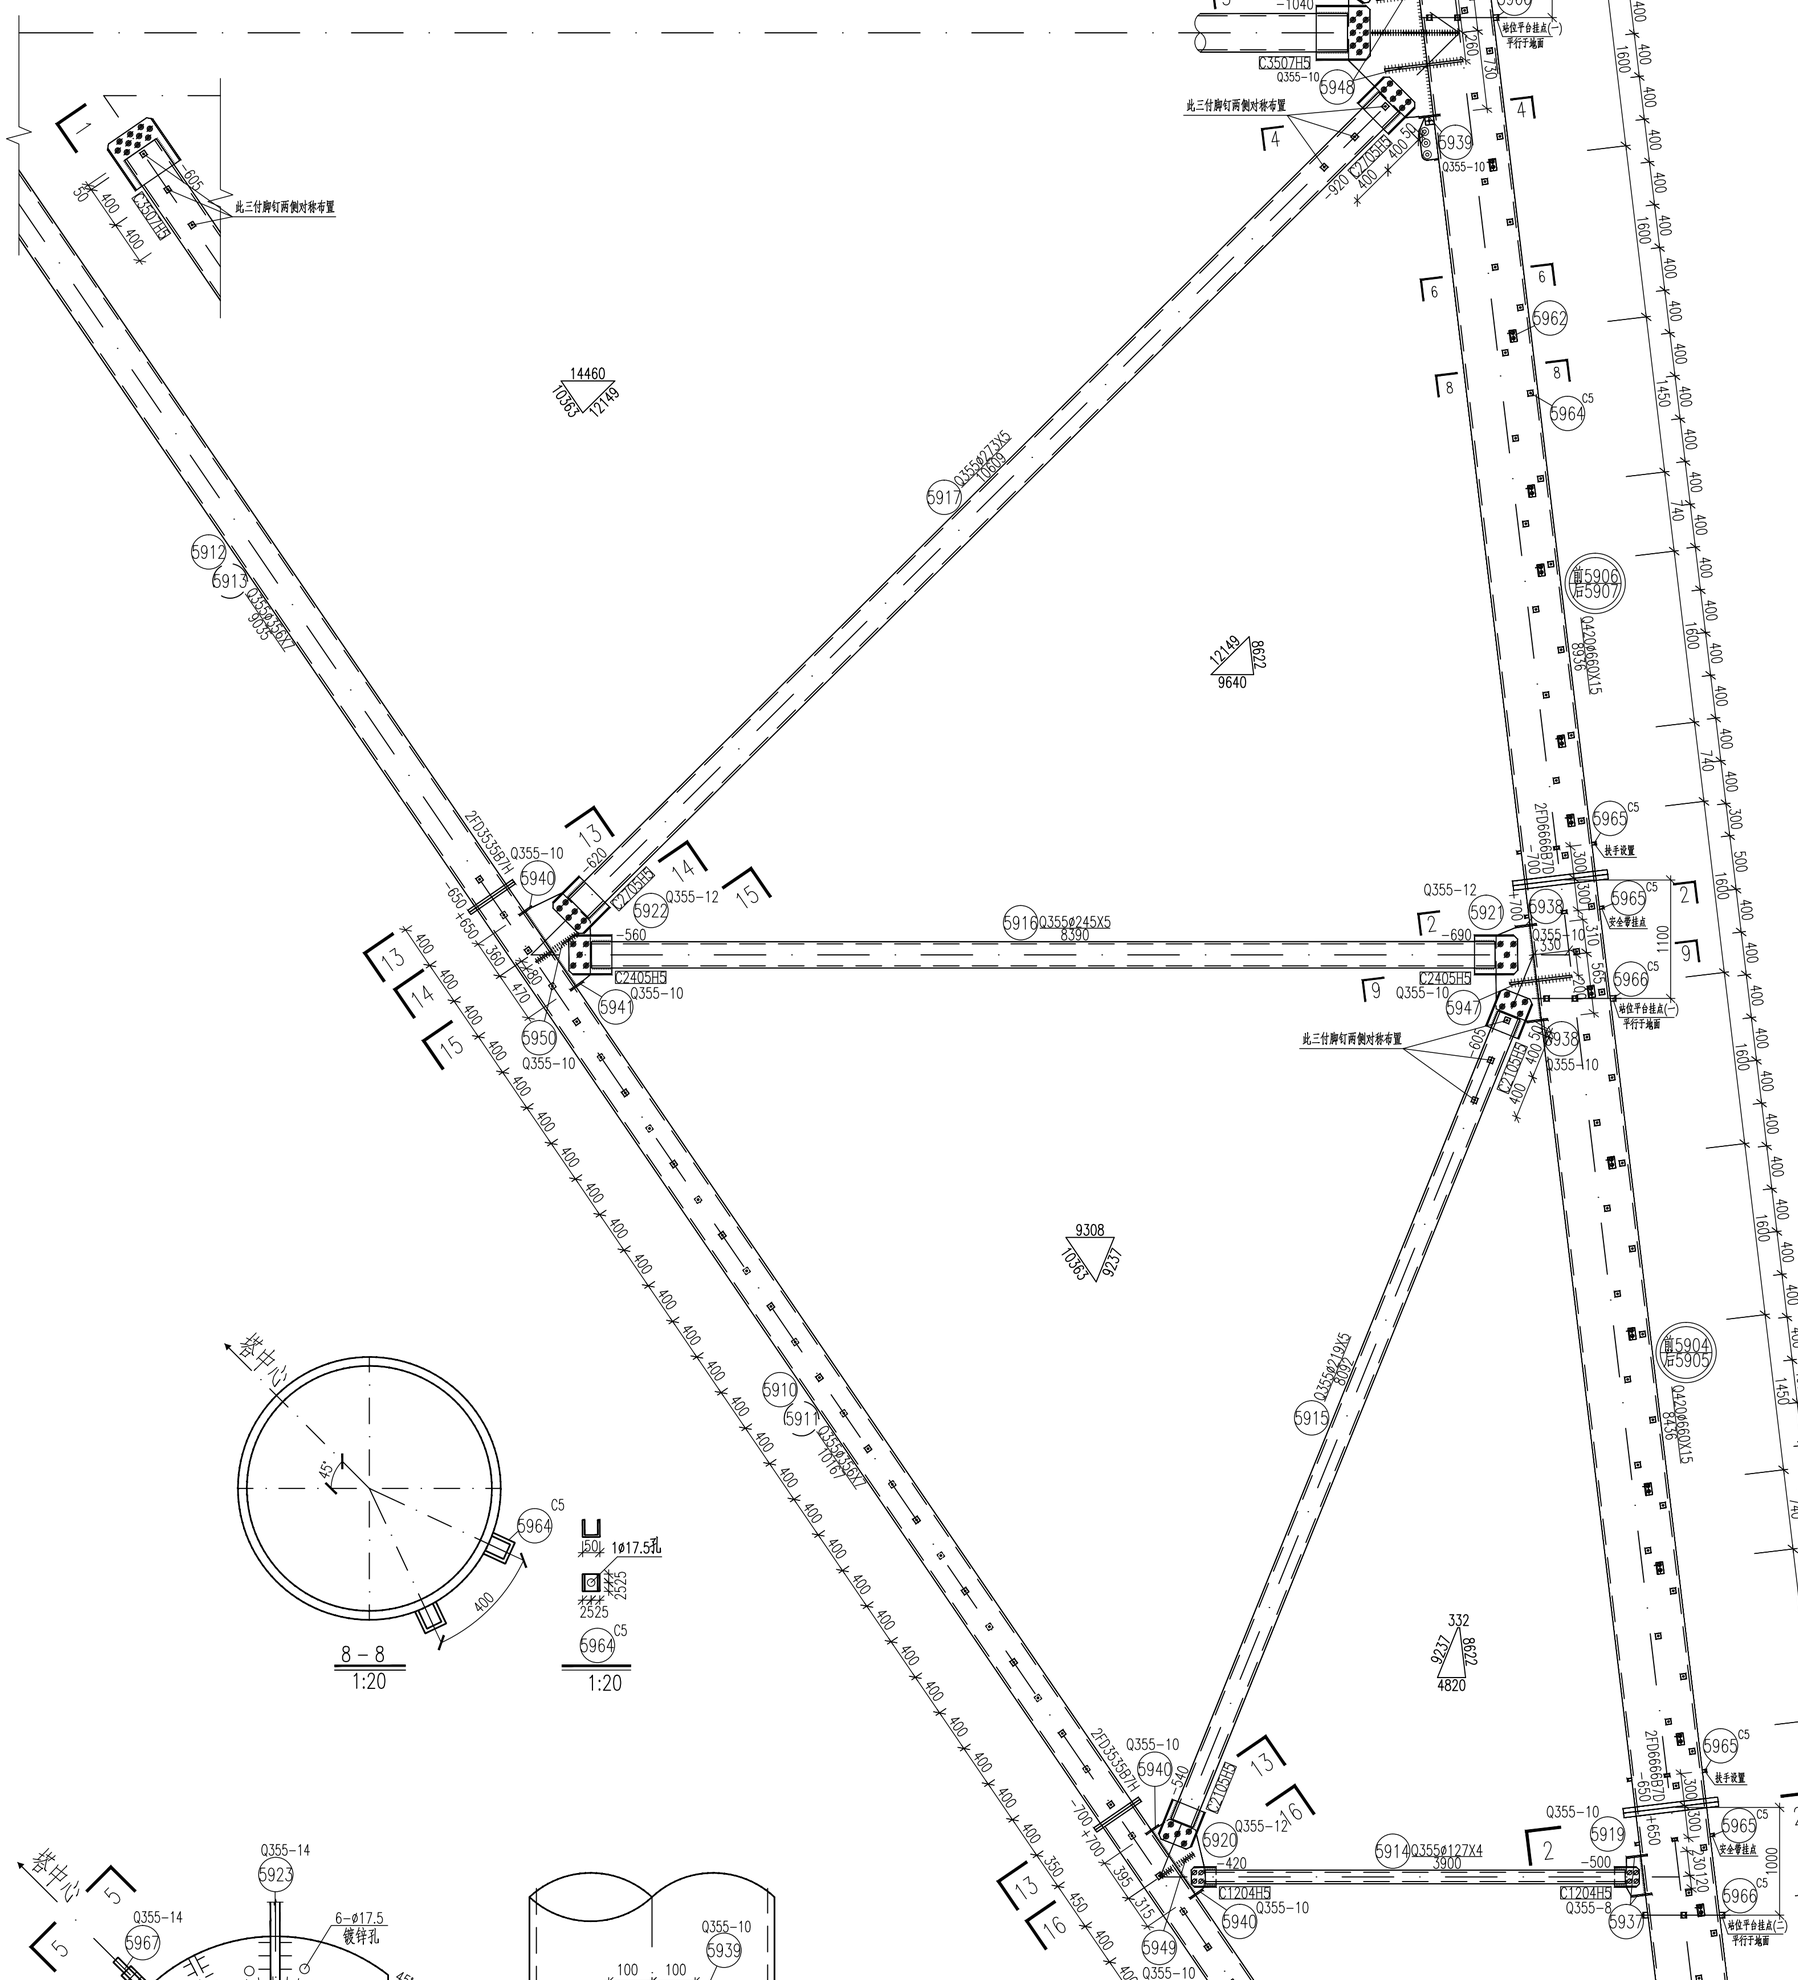

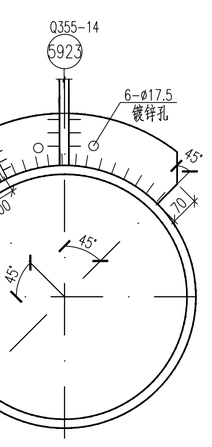


4 – 4
1:20

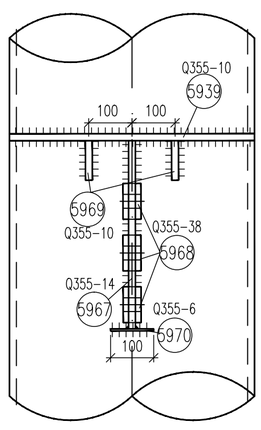

5 – 5
1:20

1:20

12 – 12
1:20

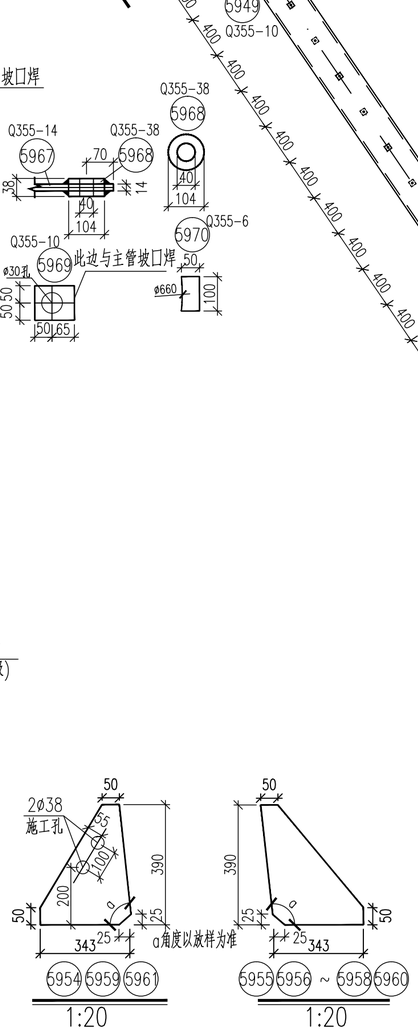

1:20 1:20

构件明细表

编号	规格	长度(mm)	数量	重量(kg) 一件	重量(kg) 小计	备注
5901	Q420ø660X15	2337	1	557.61	557.6	一端切弧 装爬梯
5901A	Q420ø660X15	2337	0	557.61	0.0	一端切弧 带脚钉
5902	Q420ø660X15	6620	1	1579.53	1579.5	装爬梯
5903	Q420ø660X15	6620	0	1579.53	0.0	带脚钉
5904	Q420ø660X15	8436	1	2012.83	2012.8	装爬梯
5905	Q420ø660X15	8436	0	2012.83	0.0	带脚钉
5906	Q420ø660X15	8936	1	2132.13	2132.1	装爬梯
5907	Q420ø660X15	8936	0	2132.13	0.0	带脚钉
5908	Q355ø356X7	9465	1	570.25	570.2	带脚钉
5909	Q355ø356X7	9465	1	570.25	570.2	带脚钉
5910	Q355ø356X7	10167	1	612.54	612.5	带脚钉
5911	Q355ø356X7	10167	1	612.54	612.5	带脚钉
5912	Q355ø356X7	9035	1	544.34	544.3	带脚钉
5913	Q355ø356X7	9035	1	544.34	544.3	带脚钉
5914	Q355ø127X4	3900	2	47.32	94.6	
5915	Q355ø219X5	8092	2	213.53	427.1	带脚钉
5916	Q355ø245X5	8390	2	248.29	496.6	
5917	Q355ø273X5	10609	2	350.59	701.2	带脚钉
5918	Q355-16X647	1612	2	131.00	262.0	
5919	Q355-10X128	385	2	3.87	7.7	
5920	Q355-12X392	781	2	28.84	57.7	
5921	Q355-12X446	963	2	40.46	80.9	
5922	Q355-12X503	913	2	43.26	86.5	
5923	Q355-14X793	1815	2	158.18	316.4	
5924	Q355ø168X4	5857	1	94.75	94.8	
5925	Q355ø219X5	4668	1	123.18	123.2	带脚钉
5926	Q355ø219X5	8182	1	215.91	215.9	带脚钉
5927	Q355ø219X5	3830	1	101.07	101.1	带脚钉
5928	Q355ø219X5	8344	1	220.18	220.2	带脚钉
5929	Q355ø273X5	10963	1	362.29	362.3	带脚钉
5930	Q355ø273X5	10963	1	362.29	362.3	带脚钉
5931	Q355-12X399	781	2	29.35	58.7	
5932	Q355-10X570	440	1	19.69	19.7	
5933	Q355-10X250	572	2	11.23	22.5	
5934	Q355-12X434	1023	2	41.82	83.6	
5935	Q355-12X376	990	1	35.07	35.1	
5936	Q355-12X135	1374	1	17.47	17.5	
5937	Q355-8X135	1374	2	11.65	23.3	
5938	Q355-10X135	1374	3	14.56	43.7	
5939	Q355-10X135	1374	1	14.56	14.6	
5940	Q355-10X80	565	6	3.55	21.3	
5941	Q355-10X80	314	2	1.97	3.9	
5942	Q355-10X80	376	2	2.36	4.7	
5943	Q355-8X60	454	4	1.71	6.8	
5944	Q355-10X120	362	2	3.41	6.8	
5945	Q355-12X180	330	2	5.60	11.2	
5946	Q355-12X180	660	1	11.19	11.2	
5947	Q355-10X150	344	4	4.05	16.2	
5948	Q355-10X150	509	8	5.99	47.9	
5949	Q355-10X200	241	2	3.78	7.6	
5950	Q355-10X300	284	2	6.69	13.4	
5951	-16X885	885	1	77.26	77.3	遮水板
5952	Q355-8X80	110	1	0.55	0.6	接地孔用
5953	Q420-32X1346	1346	1	272.50	272.5	
5954	Q355-16X343	390	1	16.80	16.8	
5955	Q355-16X343	390	2	16.80	33.6	
5956	Q355-16X343	390	2	16.80	33.6	
5957	Q355-16X343	390	2	16.80	33.6	
5958	Q355-16X343	390	2	16.80	33.6	
5959	Q355-16X343	390	2	16.80	33.6	
5960	Q355-16X343	390	2	16.80	33.6	
5961	Q355-16X343	390	1	16.80	16.8	
5962	Q355L63X5	310	19	1.49	28.3	火曲 (用于主材装爬梯)
5963	Q355-6X100	180	19	0.85	16.2	火曲 (用于主材装爬梯)
5964	C5	50	224	0.27	60.5	槽钢 (用于主材装爬梯)
5964	C5	50	288	0.27	77.8	槽钢 (用于主材带脚钉)
5965	C5	25	20	0.14	2.8	槽钢
5966	C5	50	12	0.27	3.2	槽钢
5967	Q355-14X210	550	1	12.69	12.7	
5968	Q355-38X104	104	3	3.23	9.7	
5969	Q355-10X100	115	2	0.90	1.8	
5970	Q355-6X50	100	1	0.24	0.2	
5971	Q355-12X100	548	2	5.16	10.3	
	C1204H5		4	4.19	16.8	
	C1604H5		2	7.12	14.2	
	C2105H5		8	14.54	116.3	
	C2405H5		4	17.27	69.1	
	C2705H5		8	18.10	144.8	
	X2105H7		2	22.90	45.8	
	C3507H5		4	36.27	145.1	
	FD2121B7H		2	9.20	18.4	
	FD3535B7H		8	22.10	176.8	
	FD6666B7D		7	116.50	815.5	
	T2330		3	12.40	37.2	(用于主材装爬梯)
	T5530		1	28.80	28.8	(用于主材装爬梯)
	T6980		2	36.20	72.4	(用于主材装爬梯)
合计	16483.1 kg(用于主材带脚钉)					
合计	16648.7 kg(用于主材装爬梯)					

螺栓、脚钉、垫圈明细表

名称	级别	规格	符号	数量	重量(kg)	备注
螺栓	6.8级	M16X45	◪	76	12.8	用于主材装爬梯
		M20X65	⊘	26	9.2	
		M20X75	⊠	32	12.1	
	8.8级	M24X75	⊘	172	102.0	
		M20X90	○	14	6.6	法兰螺栓
		M24X115	○	88	73.9	法兰螺栓
		M39X175	○	84	298.3	法兰螺栓
		M39X195	○	28	104.7	法兰螺栓 无扣长97mm
脚钉	6.8级	M16X200	⊕	224	98.2	用于主材装爬梯
		M16X200	⊕	288	126.2	用于主材带脚钉
垫圈	Q235		规格X个数			
合计				733.0 kg		(用于主材带脚钉)
合计				717.8 kg		(用于主材装爬梯)

说明：1.材料表为一个塔腿的重量。

2.本段塔腿为铁塔D腿，安装爬梯，
当为A、B、C腿时需焊接脚钉连接槽钢。

山东电力工程咨询院有限公司					浙江特高压交流环网工程线路	工程	施工图 设计阶段
批准	审核	校核			SZK31102A双回路直线塔 126.0-1.5m呼高腿部结构图(1/2) 129.0-4.5m呼高腿部结构图(1/2)		59
电气	2026.08	设计/勘测					
专业	会签	日期	比例	1:40	日期	2026年08月	图号 37-SA36901S-T0121-131 版本