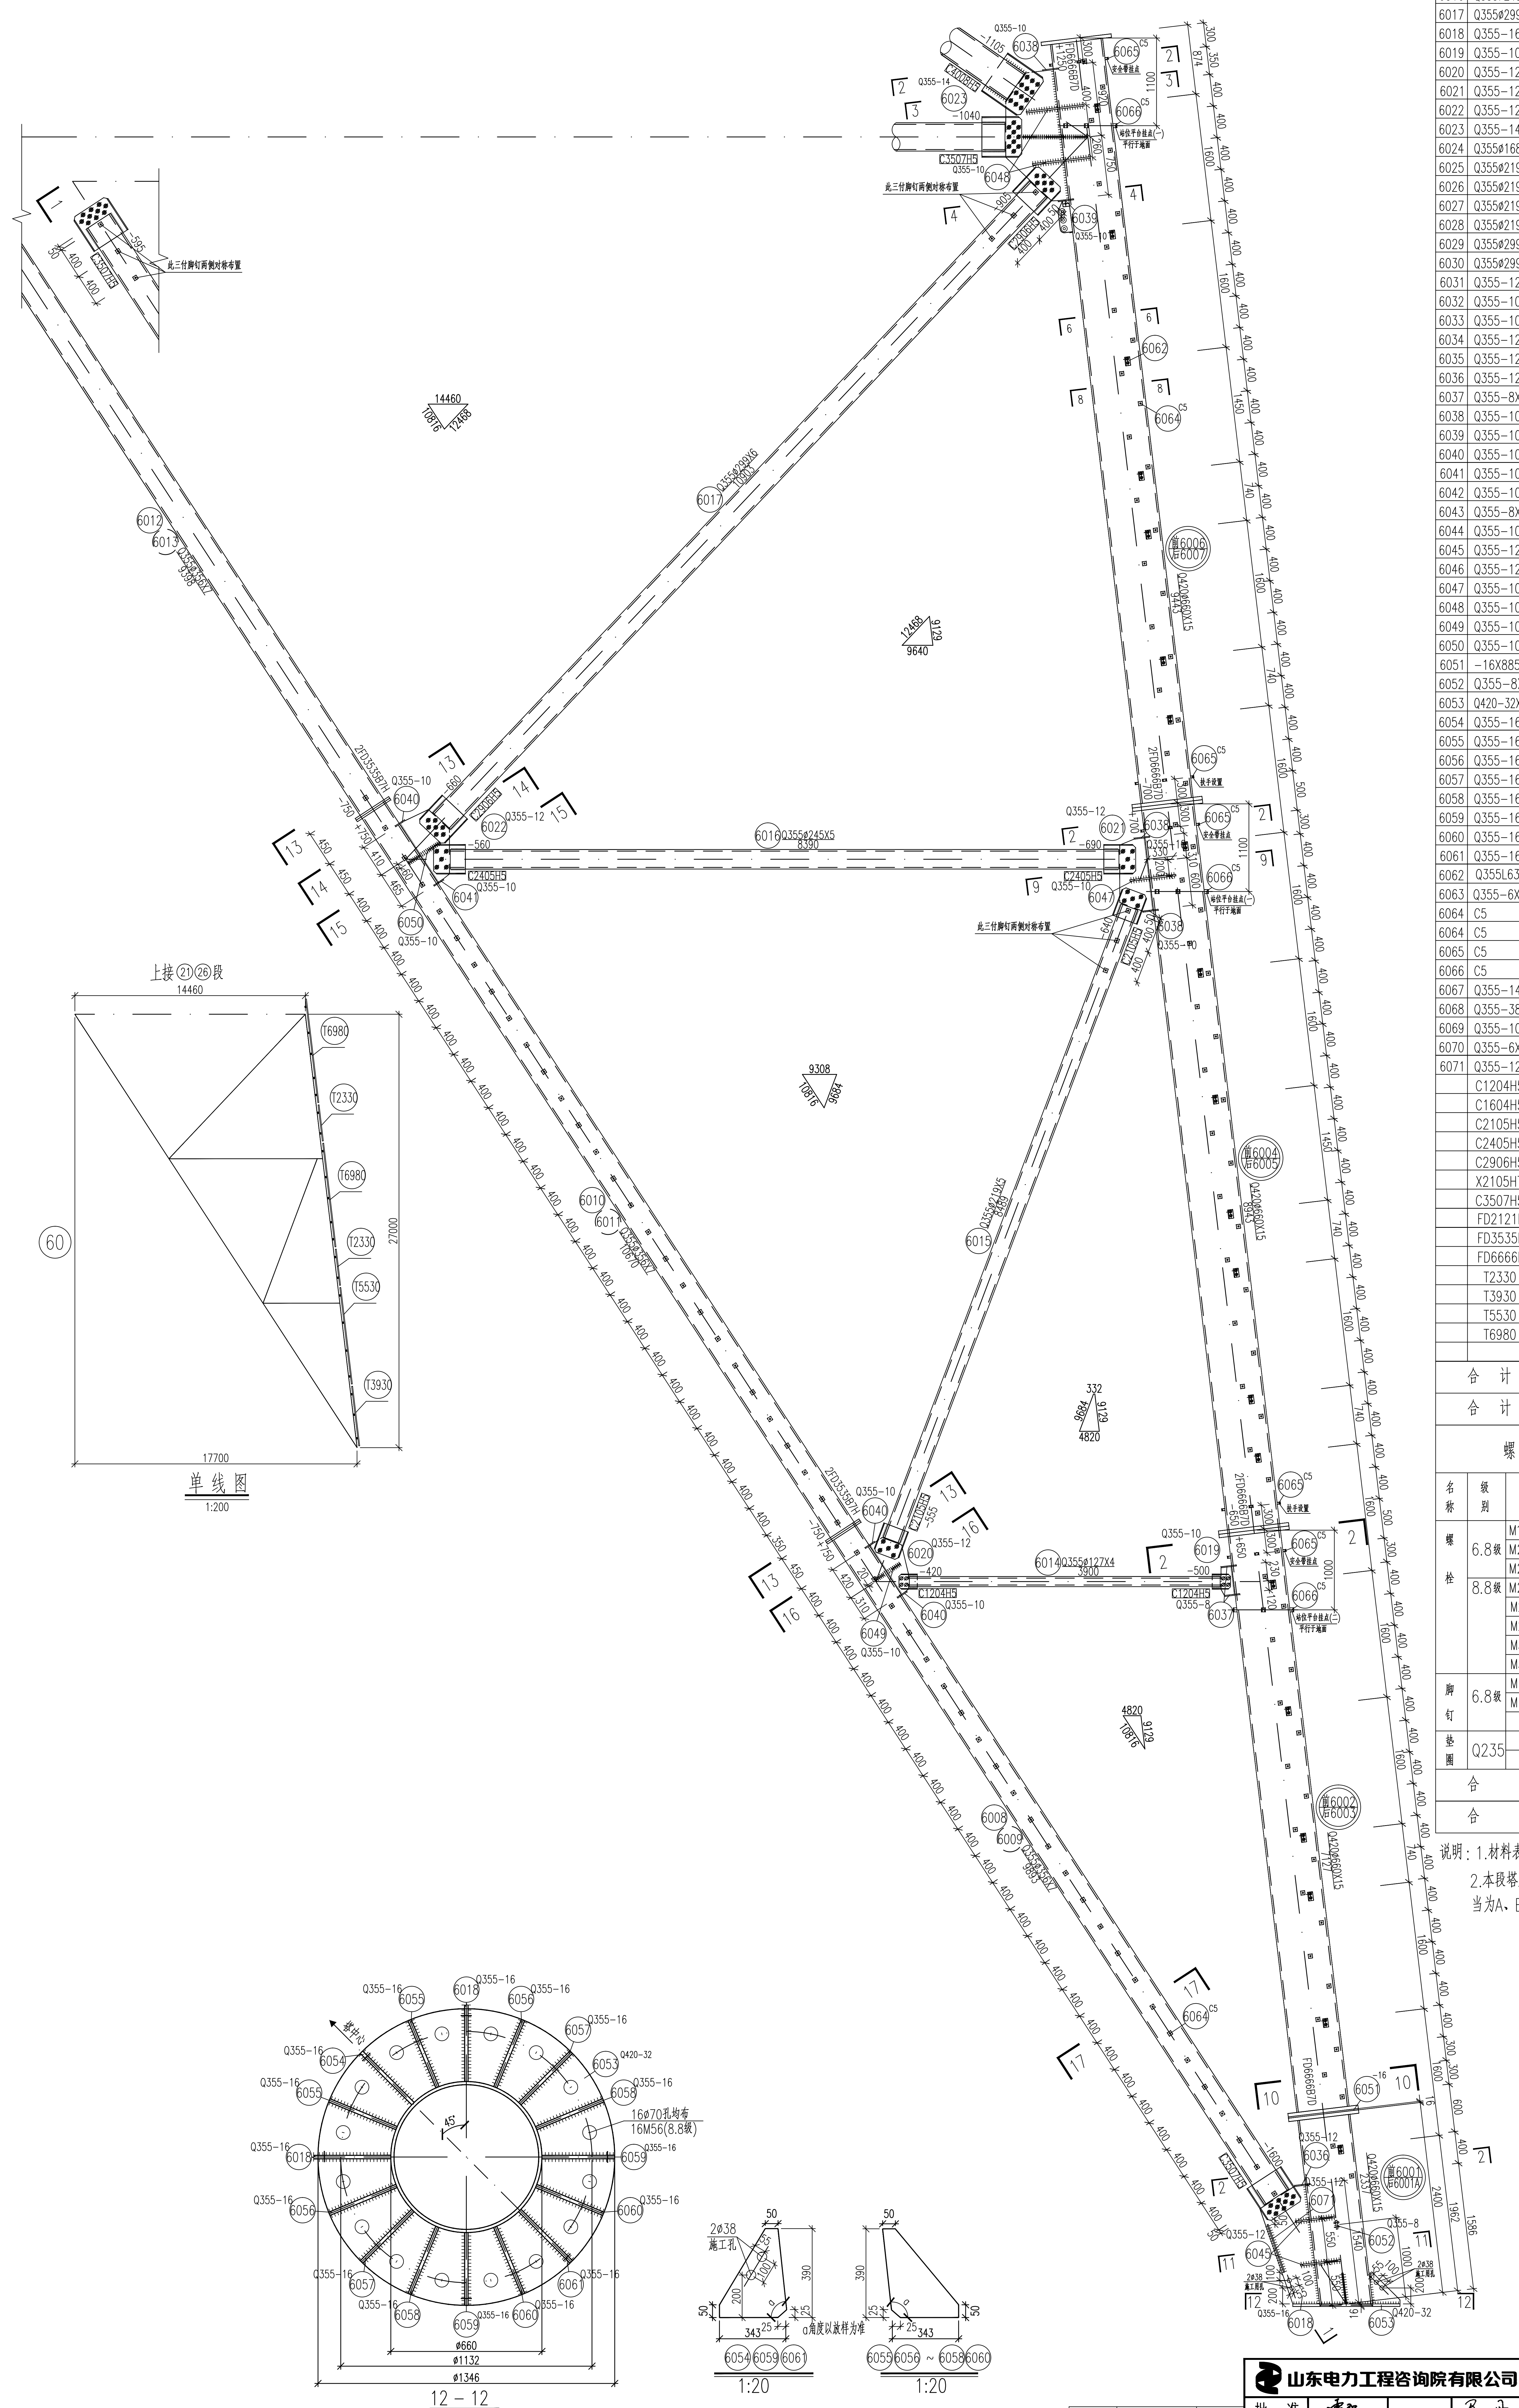
上接㉑㉖段
14460
T6980
T2330
T6980
T2330
T5530
T3930
27000
17700
60
此三付脚钉两侧对称布置
14460
12468
9640
9308
4820
9129
6001
6002
6003
6004
6005
6006
6007
6008
6009
6010
6011
6012
6013
6014
6015
6016
6017
6018
6019
6020
6021
6022
6023
6036
6037
6038
6039
6040
6041
6045
6047
6048
6049
6050
6051
6052
6053
6054
6055
6056
6057
6058
6059
6060
6061
6062
6064
6065
6066
Q355-10
Q355-12
Q355-14
Q355-16
Q420-32
C3507H5
C2405H5
C1204H5
C2906H5
FD6666B7D
FD3535B7H
安全带挂点
脚钉平台挂点
16φ70孔均布
16M56(8.8级)
45°
φ660
φ1132
φ1346
2φ38
施工孔
2φ38
施工用孔
α角度以放样为准
343
390
50

单线图

1:200

12－12

1:20

1:20

1:20


2φ17.5
接地孔
305030
5030
6052
Q355-8

1:20

编号	规　格	长度 (mm)	数量	重量(kg) 一件	重量(kg) 小计	备　注
6001	Q420φ660X15	2337	1	557.61	557.6	一端切弧 装爬梯
6001A	Q420φ660X15	2337	0	557.61	0.0	一端切弧 带脚钉
6002	Q420φ660X15	7127	1	1700.50	1700.5	装爬梯
6003	Q420φ660X15	7127	0	1700.50	0.0	带脚钉
6004	Q420φ660X15	8943	1	2133.80	2133.8	装爬梯
6005	Q420φ660X15	8943	0	2133.80	0.0	带脚钉
6006	Q420φ660X15	9443	1	2253.10	2253.1	装爬梯
6007	Q420φ660X15	9443	0	2253.10	0.0	带脚钉
6008	Q355φ356X7	9893	1	596.03	596.0	带脚钉
6009	Q355φ356X7	9893	1	596.03	596.0	带脚钉
6010	Q355φ356X7	10670	1	642.85	642.8	带脚钉
6011	Q355φ356X7	10670	1	642.85	642.8	带脚钉
6012	Q355φ356X7	9398	1	566.21	566.2	带脚钉
6013	Q355φ356X7	9398	1	566.21	566.2	带脚钉
6014	Q355φ127X4	3900	2	47.32	94.6	
6015	Q355φ219X5	8489	2	224.01	448.0	带脚钉
6016	Q355φ245X5	8390	2	248.29	496.6	
6017	Q355φ299X6	10903	2	472.70	945.4	带脚钉
6018	Q355-16X663	1694	2	141.06	282.1	
6019	Q355-10X188	385	2	5.68	11.4	
6020	Q355-12X382	803	2	28.90	57.8	
6021	Q355-12X450	1001	2	42.43	84.9	
6022	Q355-12X538	963	2	48.80	97.6	
6023	Q355-14X793	1837	2	160.10	320.2	
6024	Q355φ168X4	5877	1	95.08	95.1	
6025	Q355φ219X5	4792	1	126.45	126.4	带脚钉
6026	Q355φ219X5	8389	1	221.37	221.4	带脚钉
6027	Q355φ219X5	3954	1	104.34	104.3	带脚钉
6028	Q355φ219X5	8551	1	225.64	225.6	带脚钉
6029	Q355φ299X6	11252	1	487.83	487.8	带脚钉
6030	Q355φ299X6	11252	1	487.83	487.8	带脚钉
6031	Q355-12X379	803	2	28.67	57.3	
6032	Q355-10X570	440	1	19.69	19.7	
6033	Q355-10X250	572	2	11.23	22.5	
6034	Q355-12X436	1095	2	44.97	89.9	
6035	Q355-12X434	1056	1	43.17	43.2	
6036	Q355-12X135	1374	1	17.47	17.5	
6037	Q355-8X135	1374	2	11.65	23.3	
6038	Q355-10X135	1374	3	14.56	43.7	
6039	Q355-10X135	1374	1	14.56	14.6	
6040	Q355-10X80	565	6	3.55	21.3	
6041	Q355-10X80	314	2	1.97	3.9	
6042	Q355-10X80	376	2	2.36	4.7	
6043	Q355-8X60	454	4	1.71	6.8	
6044	Q355-10X160	396	2	4.97	9.9	
6045	Q355-12X180	330	4	5.60	22.4	
6046	Q355-12X180	660	2	11.19	22.4	
6047	Q355-10X150	344	4	4.05	16.2	
6048	Q355-10X150	509	8	5.99	47.9	
6049	Q355-10X200	241	2	3.78	7.6	
6050	Q355-10X300	284	2	6.69	13.4	
6051	-16X885	885	1	77.26	77.3	遮水板
6052	Q355-8X80	110	1	0.55	0.6	接地孔用
6053	Q420-32X1346	1346	1	272.50	272.5	
6054	Q355-16X343	390	1	16.80	16.8	
6055	Q355-16X343	390	2	16.80	33.6	
6056	Q355-16X343	390	2	16.80	33.6	
6057	Q355-16X343	390	2	16.80	33.6	
6058	Q355-16X343	390	2	16.80	33.6	
6059	Q355-16X343	390	2	16.80	33.6	
6060	Q355-16X343	390	2	16.80	33.6	
6061	Q355-16X343	390	1	16.80	16.8	
6062	Q355L63X5	310	20	1.49	29.8	火曲（用于主材装爬梯）
6063	Q355-6X100	180	20	0.85	17.0	火曲（用于主材装爬梯）
6064	C5	50	228	0.27	61.6	槽钢（用于主材装爬梯）
6064	C5	50	296	0.27	79.9	槽钢（用于主材带脚钉）
6065	C5	25	20	0.14	2.8	槽钢
6066	C5	50	12	0.27	3.2	槽钢
6067	Q355-14X210	550	1	12.69	12.7	
6068	Q355-38X104	104	3	3.23	9.7	
6069	Q355-10X100	115	2	0.90	1.8	
6070	Q355-6X50	100	1	0.24	0.2	
6071	Q355-12X100	633	2	5.96	11.9	
	C1204H5		4	4.19	16.8	
	C1604H5		2	7.12	14.2	
	C2105H5		8	14.54	116.3	
	C2405H5		4	17.27	69.1	
	C2906H5		8	23.31	186.5	
	X2105H7		2	22.90	45.8	
	C3507H5		4	36.27	145.1	
	FD2121B7H		2	9.20	18.4	
	FD3535B7H		8	22.10	176.8	
	FD6666B7D		7	116.50	815.5	
	T2330		2	12.40	24.8	（用于主材装爬梯）
	T3930		1	20.70	20.7	（用于主材装爬梯）
	T5530		1	28.80	28.8	（用于主材装爬梯）
	T6980		2	36.20	72.4	（用于主材装爬梯）
合　计	17662.5 kg（用于主材带脚钉）					
合　计	17837.7 kg（用于主材装爬梯）					

螺栓、脚钉、垫圈明细表

名称	级别	规　格	符　号	数量	重　量(kg)	备　注
螺栓	6.8级	M16X45	◍	80	13.5	用于主材装爬梯
		M20X65	∅	26	9.2	
		M20X75	⊗	32	12.1	
	8.8级	M24X75	⊘	180	106.7	
		M20X90	○	14	6.6	法兰螺栓
		M24X115	○	88	73.9	法兰螺栓
		M39X175	○	84	298.3	法兰螺栓
		M39X195	○	28	104.7	法兰螺栓 无扣长97mm
脚钉	6.8级	M16X200	⊖	228	99.9	用于主材装爬梯
		M16X200	┤	296	129.7	用于主材带脚钉
垫圈	Q235		规格X个数			
合　计			741.2 kg（用于主材带脚钉）			
合　计			724.9 kg（用于主材装爬梯）			

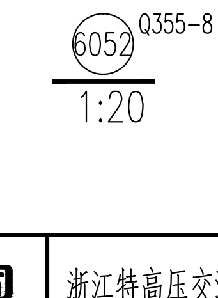说明：1.材料表为一个塔腿的重量。

2.本段塔腿为铁塔D腿，安装爬梯，

当为A、B、C腿时需焊接脚钉连接槽钢。

电气	赵庆周	2026.08
专业	会签	日期

山东电力工程咨询院有限公司

浙江特高压交流环网工程线路 工程

施工图 设计阶段

批　准	雷强	校　核	马一丹
审　核	高锡鹏		
		设计/勘测	潘旺光
比　例	1：40	日　期	2026年 08月

SZK31102A双回路直线塔

126.0-0.0m呼高腿部结构图（1/3）

129.0-3.0m呼高腿部结构图（1/3）

60

图　号 37-SA36901S-T012133

版本