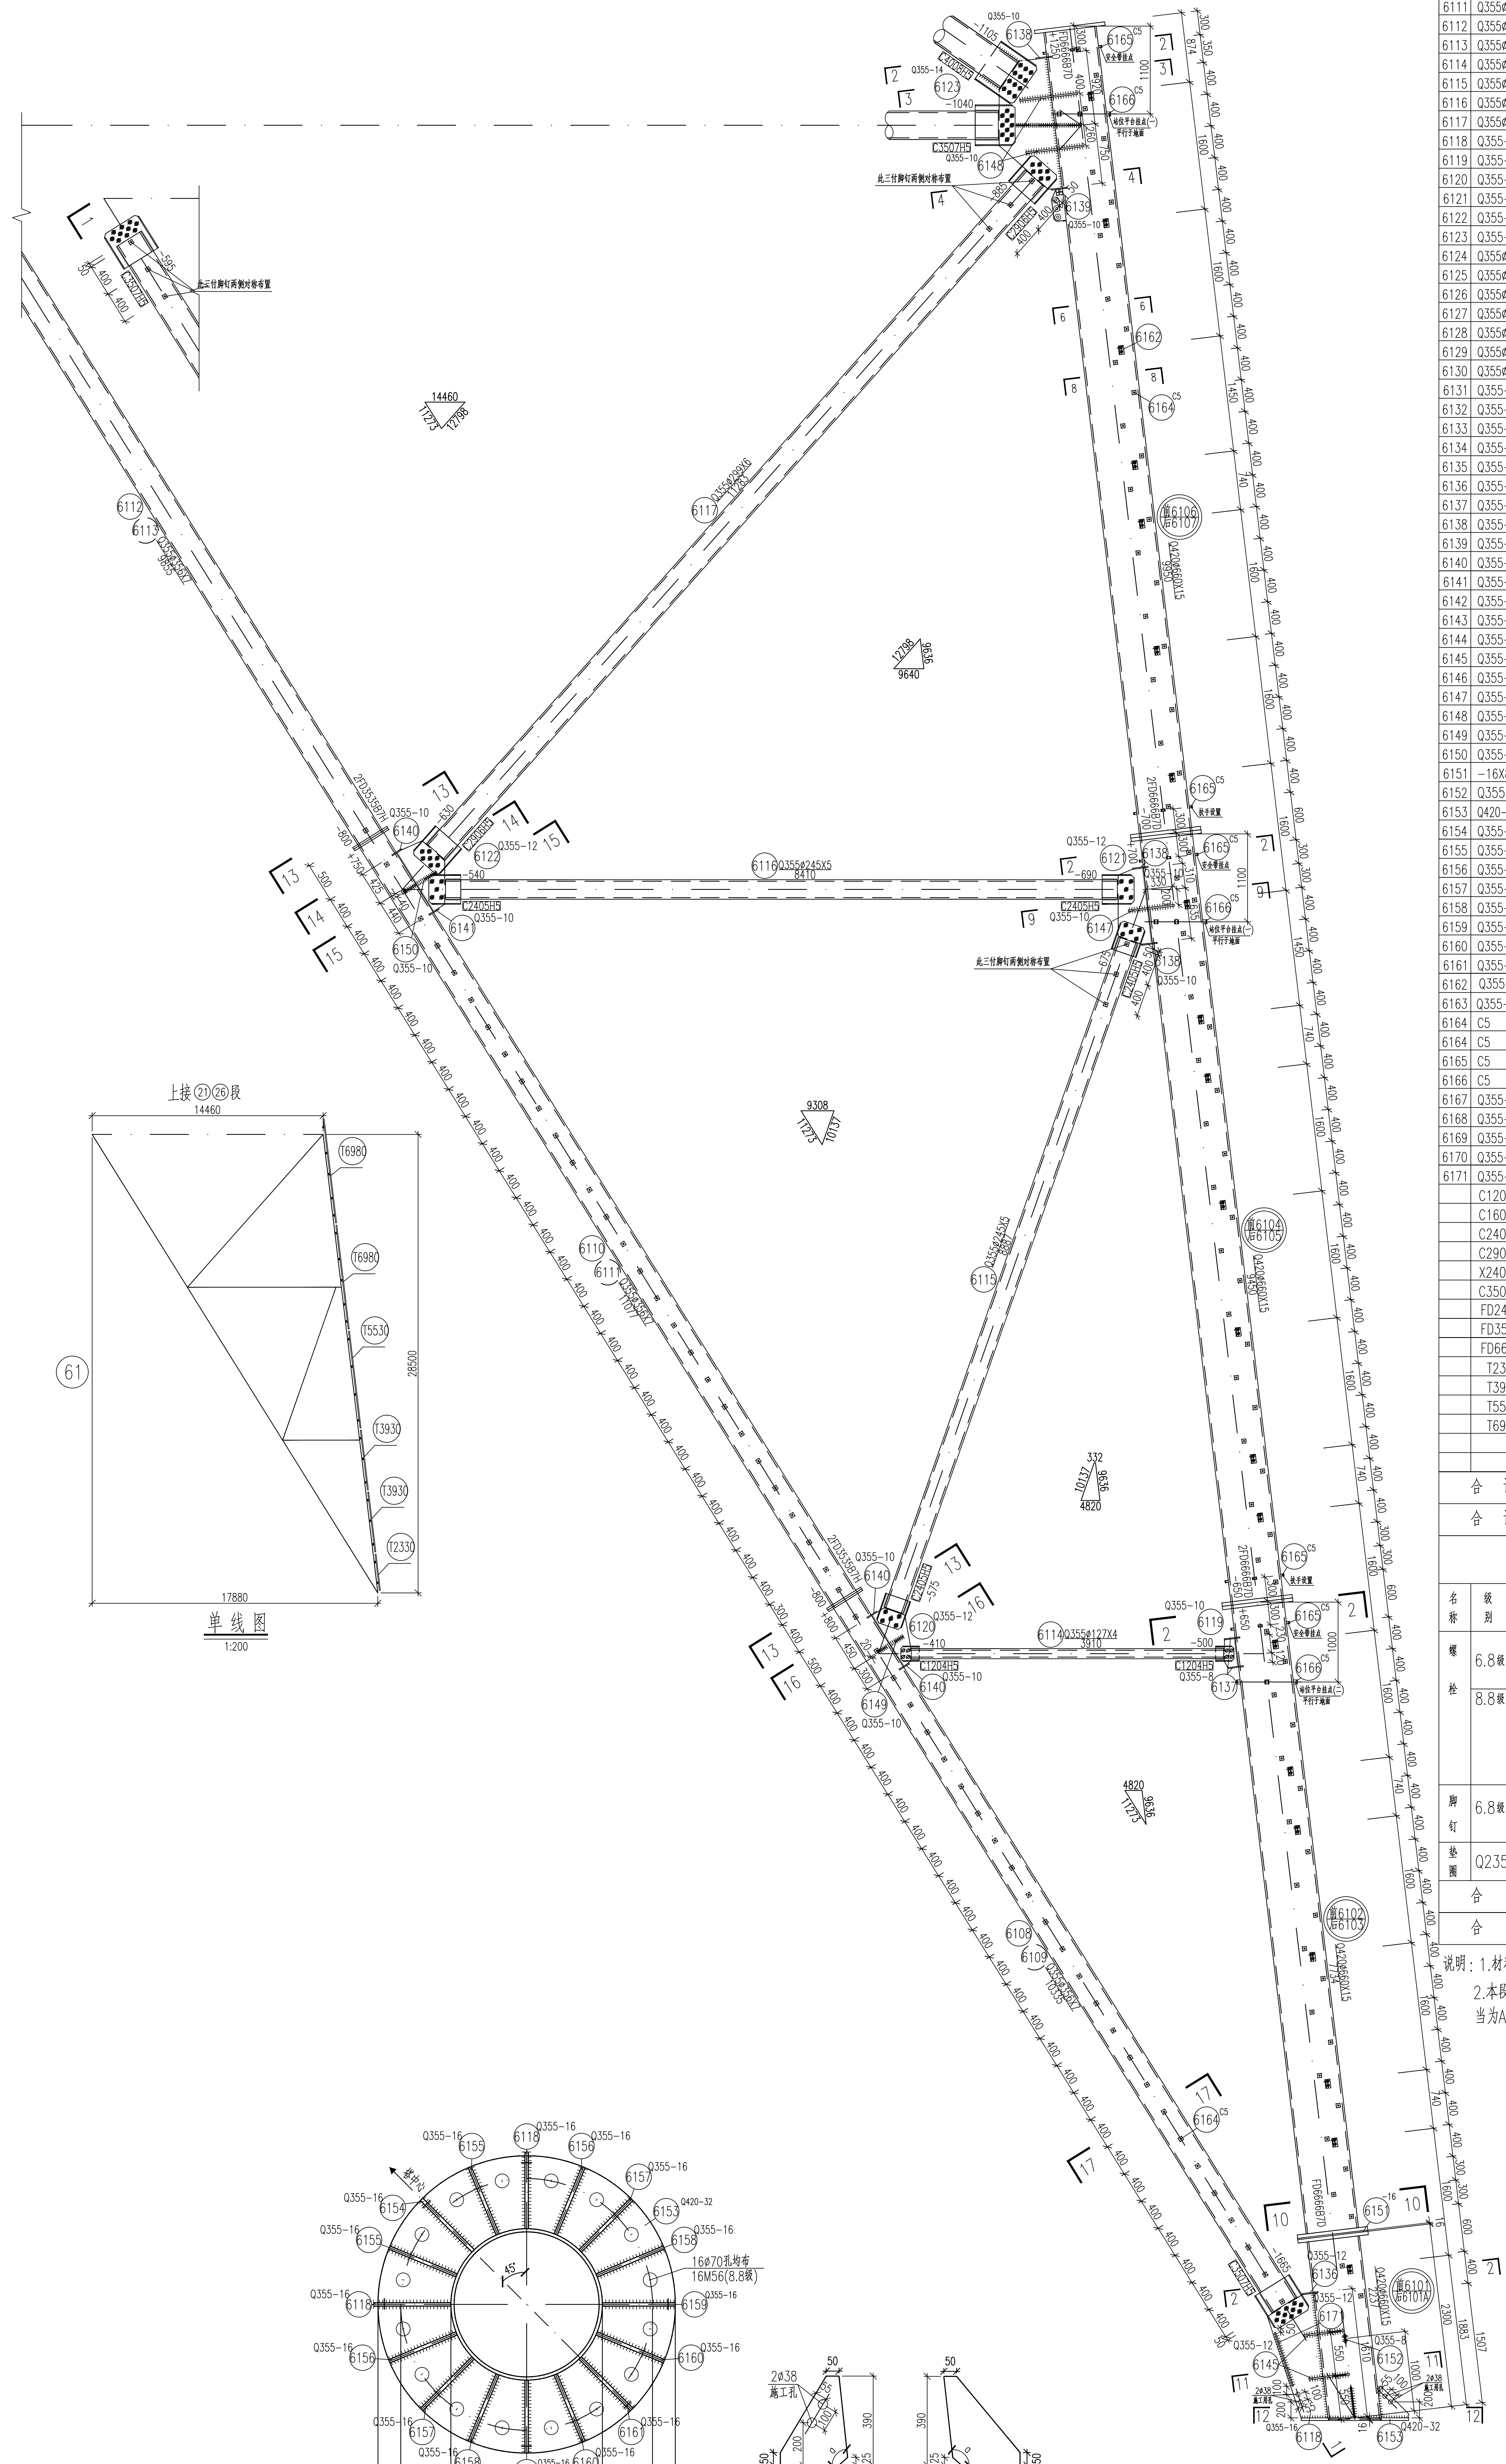

单线图
1:200

12－12
1:20

1:20

1:20

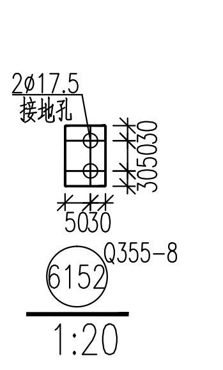

1:20

构　件　明　细　表

编号	规　格	长 度 (mm)	数量	重 量 (kg) 一 件	重 量 (kg) 小 计	备　注
6101	Q420⌀660X15	2237	1	533.75	533.8	一端切弧 装爬梯
6101A	Q420⌀660X15	2237	0	533.75	0.0	一端切弧 带脚钉
6102	Q420⌀660X15	7734	1	1845.33	1845.3	装爬梯
6103	Q420⌀660X15	7734	0	1845.33	0.0	带脚钉
6104	Q420⌀660X15	9450	1	2254.77	2254.8	装爬梯
6105	Q420⌀660X15	9450	0	2254.77	0.0	带脚钉
6106	Q420⌀660X15	9950	1	2374.07	2374.1	装爬梯
6107	Q420⌀660X15	9950	0	2374.07	0.0	带脚钉
6108	Q355⌀356X7	10335	1	622.66	622.7	带脚钉
6109	Q355⌀356X7	10335	1	622.66	622.7	带脚钉
6110	Q355⌀356X7	11077	1	667.37	667.4	带脚钉
6111	Q355⌀356X7	11077	1	667.37	667.4	带脚钉
6112	Q355⌀356X7	9855	1	593.74	593.7	带脚钉
6113	Q355⌀356X7	9855	1	593.74	593.7	带脚钉
6114	Q355⌀127X4	3910	2	47.44	94.9	
6115	Q355⌀245X5	8887	2	263.00	526.0	带脚钉
6116	Q355⌀245X5	8410	2	248.88	497.8	
6117	Q355⌀299X6	11283	2	489.17	978.3	带脚钉
6118	Q355-16X665	1771	2	147.92	295.8	
6119	Q355-10X188	385	2	5.68	11.4	
6120	Q355-12X394	825	2	30.62	61.2	
6121	Q355-12X455	1040	2	44.58	89.2	
6122	Q355-12X512	952	2	45.92	91.8	
6123	Q355-14X793	1837	2	160.10	320.2	
6124	Q355⌀168X4	5857	1	94.75	94.8	
6125	Q355⌀245X5	4889	1	144.68	144.7	带脚钉
6126	Q355⌀245X5	8577	1	253.83	253.8	带脚钉
6127	Q355⌀245X5	3951	1	116.93	116.9	带脚钉
6128	Q355⌀245X5	8639	1	255.66	255.7	带脚钉
6129	Q355⌀299X6	11619	1	503.74	503.7	带脚钉
6130	Q355⌀299X6	11619	1	503.74	503.7	带脚钉
6131	Q355-12X392	825	2	30.46	60.9	
6132	Q355-10X690	506	1	27.41	27.4	
6133	Q355-10X293	704	2	16.19	32.4	
6134	Q355-12X467	1161	2	51.07	102.1	
6135	Q355-12X461	1078	1	46.81	46.8	
6136	Q355-12X135	1374	1	17.47	17.5	
6137	Q355-8X135	1374	2	11.65	23.3	
6138	Q355-10X135	1374	3	14.56	43.7	
6139	Q355-10X135	1374	1	14.56	14.6	
6140	Q355-10X80	565	6	3.55	21.3	
6141	Q355-10X80	314	2	1.97	3.9	
6142	Q355-10X80	376	2	2.36	4.7	
6143	Q355-8X60	454	4	1.71	6.8	
6144	Q355-10X180	414	2	5.85	11.7	
6145	Q355-12X180	330	4	5.60	22.4	
6146	Q355-12X180	660	2	11.19	22.4	
6147	Q355-10X150	344	4	4.05	16.2	
6148	Q355-10X150	509	8	5.99	47.9	
6149	Q355-10X200	241	2	3.78	7.6	
6150	Q355-10X300	284	2	6.69	13.4	
6151	-16X885	885	1	77.26	77.3	遮水板
6152	Q355-8X80	110	1	0.55	0.6	接地孔用
6153	Q420-32X1346	1346	1	272.50	272.5	
6154	Q355-16X343	390	1	16.80	16.8	
6155	Q355-16X343	390	2	16.80	33.6	
6156	Q355-16X343	390	2	16.80	33.6	
6157	Q355-16X343	390	2	16.80	33.6	
6158	Q355-16X343	390	2	16.80	33.6	
6159	Q355-16X343	390	2	16.80	33.6	
6160	Q355-16X343	390	2	16.80	33.6	
6161	Q355-16X343	390	1	16.80	16.8	
6162	Q355L63X5	310	21	1.49	31.3	火曲 (用于主材装爬梯)
6163	Q355-6X100	180	21	0.85	17.8	火曲 (用于主材装爬梯)
6164	C5	50	234	0.27	63.2	槽钢 (用于主材装爬梯)
6164	C5	50	306	0.27	82.6	槽钢 (用于主材带脚钉)
6165	C5	25	20	0.14	2.8	槽钢
6166	C5	50	12	0.27	3.2	槽钢
6167	Q355-14X210	550	1	12.69	12.7	
6168	Q355-38X104	104	3	3.23	9.7	
6169	Q355-10X100	115	2	0.90	1.8	
6170	Q355-6X50	100	1	0.24	0.2	
6171	Q355-12X100	708	2	6.67	13.3	
	C1204H5		4	4.19	16.8	
	C1604H5		2	7.12	14.2	
	C2405H5		12	17.27	207.2	
	C2906H5		8	23.31	186.5	
	X2405H7		2	33.90	67.8	
	C3507H5		4	36.27	145.1	
	FD2424B7H		2	10.40	20.8	
	FD3535B7H		8	22.10	176.8	
	FD6666B7D		7	116.50	815.5	
	T2330		1	12.40	12.4	(用于主材装爬梯)
	T3930		2	20.70	41.4	(用于主材装爬梯)
	T5530		1	28.80	28.8	(用于主材装爬梯)
	T6980		2	36.20	72.4	(用于主材装爬梯)
合　计	18525.1 kg(用于主材带脚钉)					
合　计	18709.8 kg(用于主材装爬梯)					

螺栓、脚钉、垫圈明细表

名称	级别	规　格	符　号	数量	重 量(kg)	备　注
螺栓	6.8级	M16X45	◎	84	14.2	用于主材装爬梯
		M20X65	∅	26	9.2	
		M20X75	⊗	48	18.2	
	8.8级	M24X75	∅	180	106.7	
		M20X90	○	14	6.6	法兰螺栓
		M24X115	○	88	73.9	法兰螺栓
		M39X175	○	84	298.3	法兰螺栓
		M39X195	○	28	104.7	法兰螺栓 无扣长97mm
脚钉	6.8级	M16X200	⊖	234	102.6	用于主材装爬梯
		M16X200		306	134.1	用于主材带脚钉
垫圈	Q235		规格X个数			
合　计			751.7 kg			(用于主材带脚钉)
合　计			734.4 kg			(用于主材装爬梯)

说明：1.材料表为一个塔腿的重量。

2.本段塔腿为铁塔D腿，安装爬梯，
当为A、B、C腿时需焊接脚钉连接槽钢。

山东电力工程咨询院有限公司		浙江特高压交流环网工程线路	工程	施工图	设计阶段
批　准		校　核	马一丹	SZK31102A双回路直线塔 129.0-1.5m呼高腿部结构图 (1/3)	61
审　核	高锡鹏	设计/勘测			
比　例	1: 40	日　期	2026年 08月	图　号 37-SA36901S-T0121-136	版本

电 气	赵庆周	2026.08
专 业	会 签	日 期