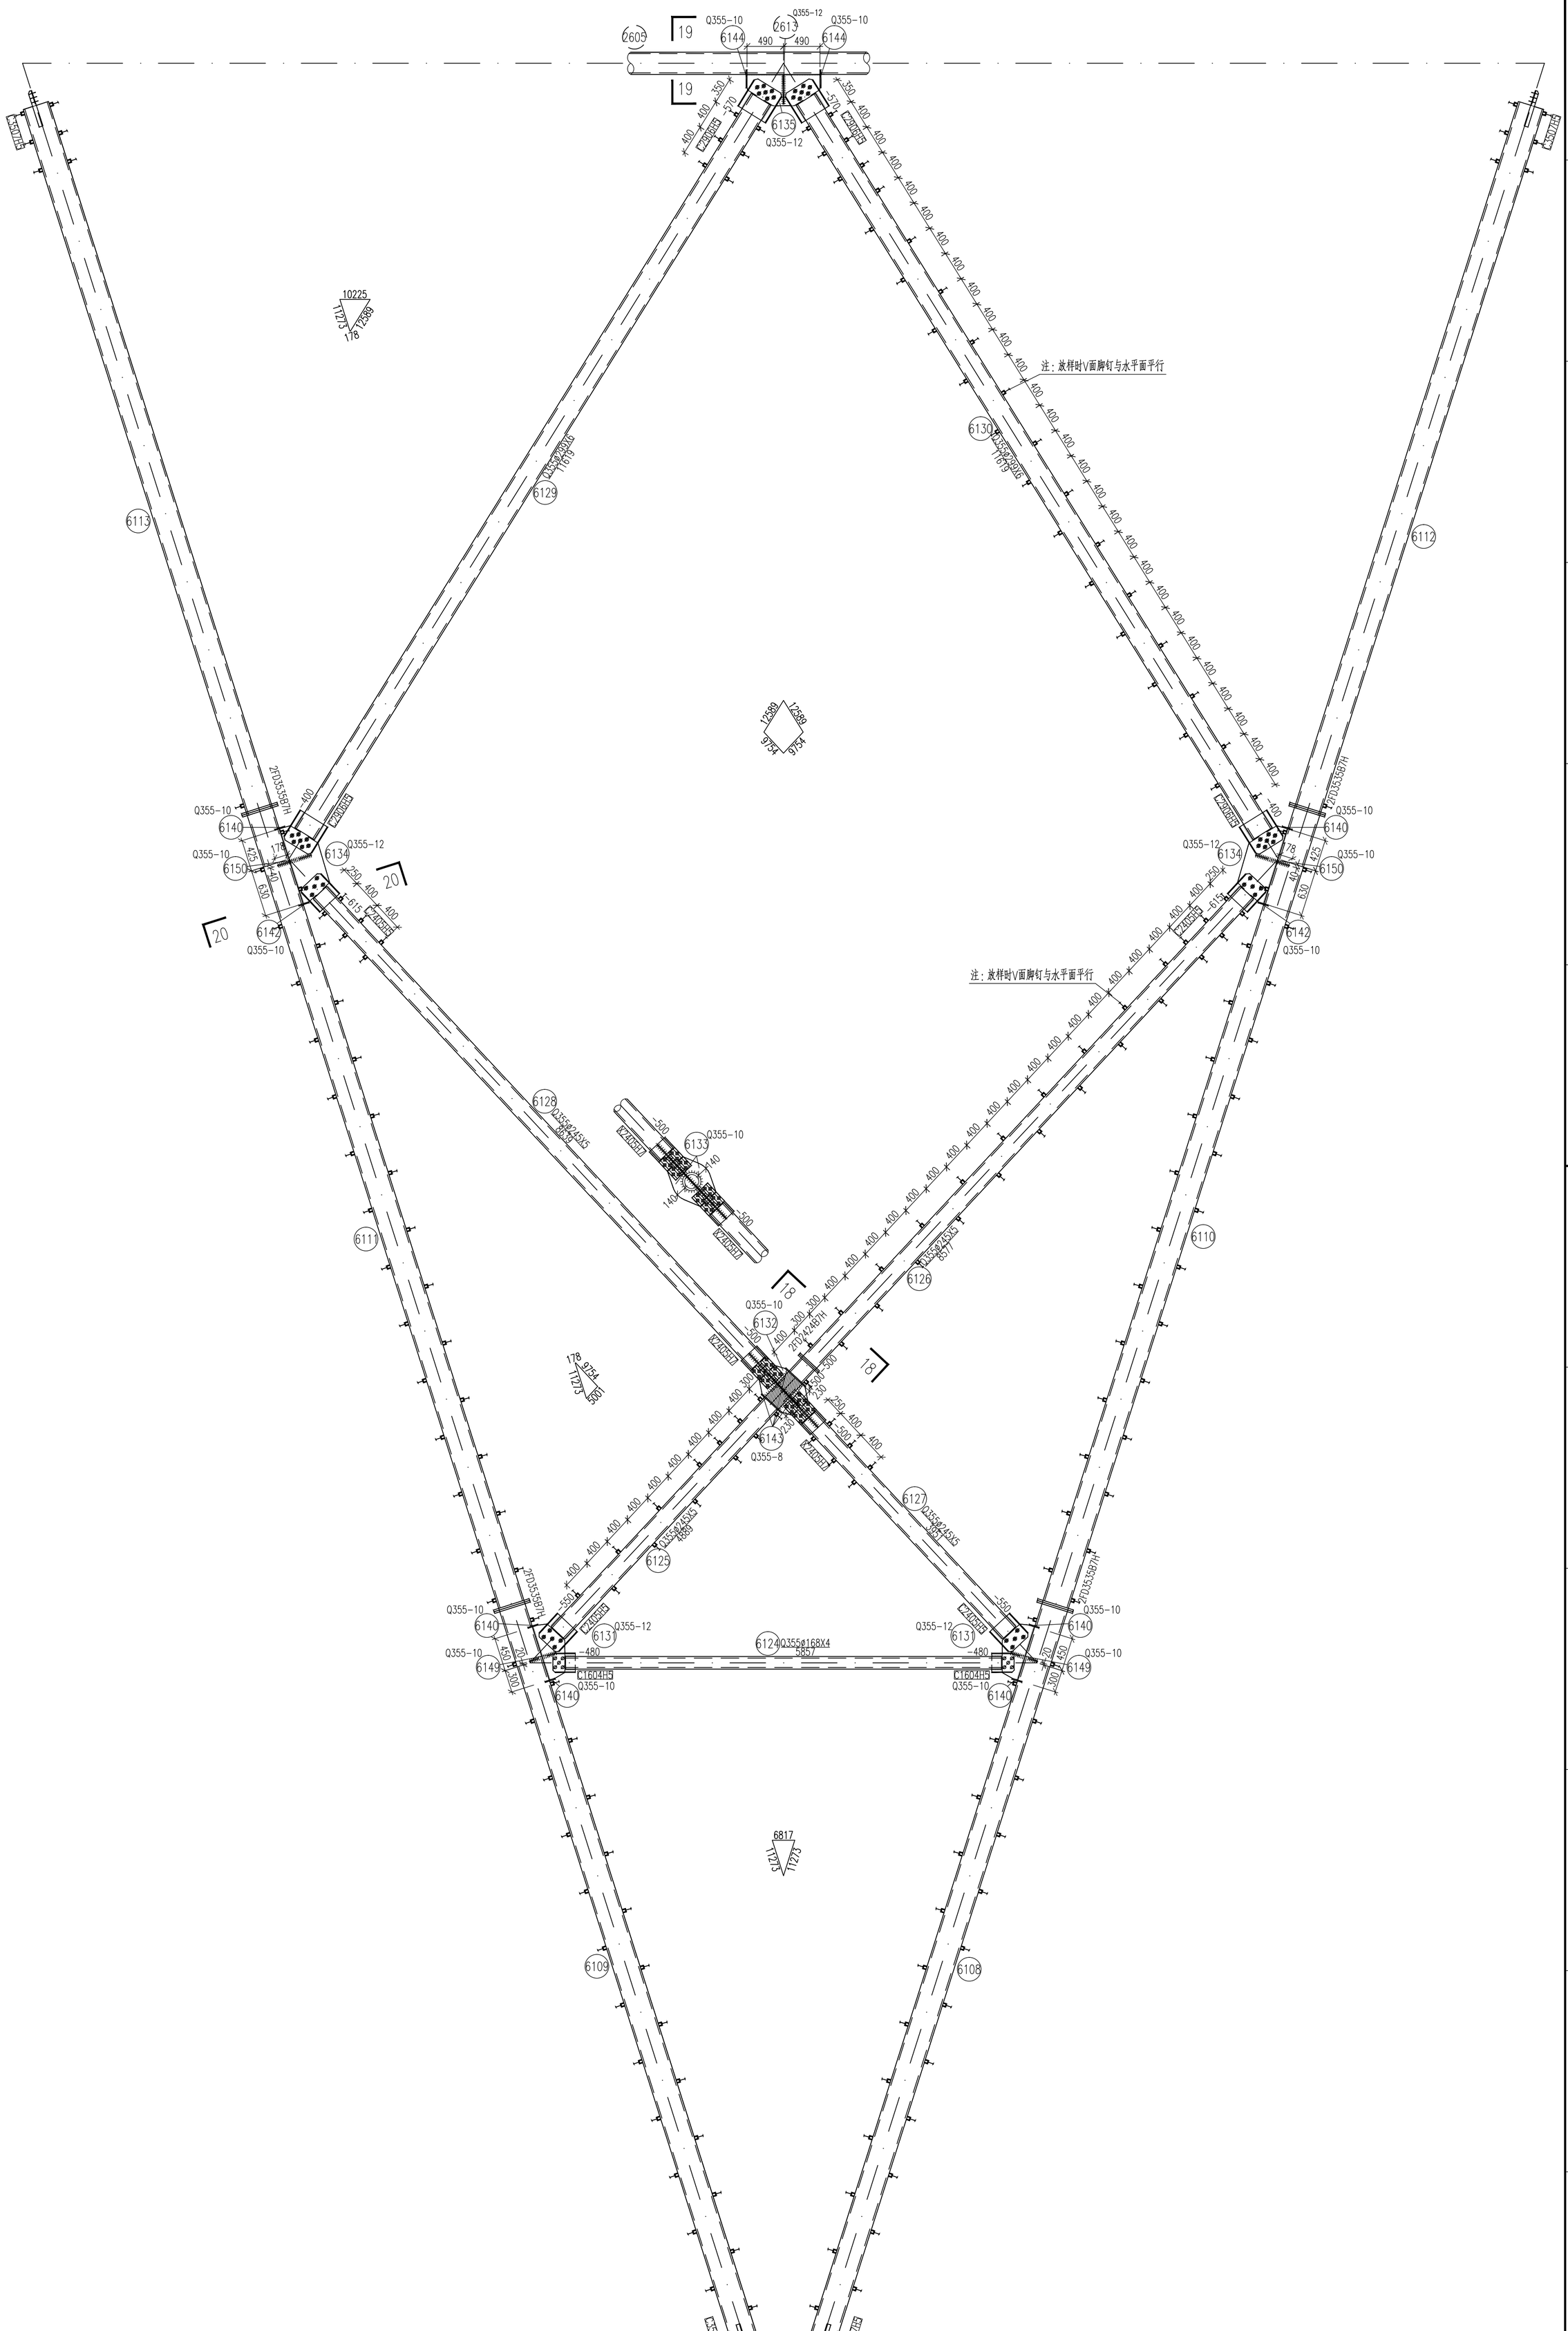


山东电力工程咨询院有限公司				浙江特高压交流环网工程线路 工程	施工图 设计阶段
批 准		校 核		SZK31102A双回路直线塔 129.0-1.5m呼高腿部结构图（2/3）	61
审 核		设计/勘测			
比 例	1:40	日 期	2026年 08月	图 号 37-SA36901S-T0121-137	版本