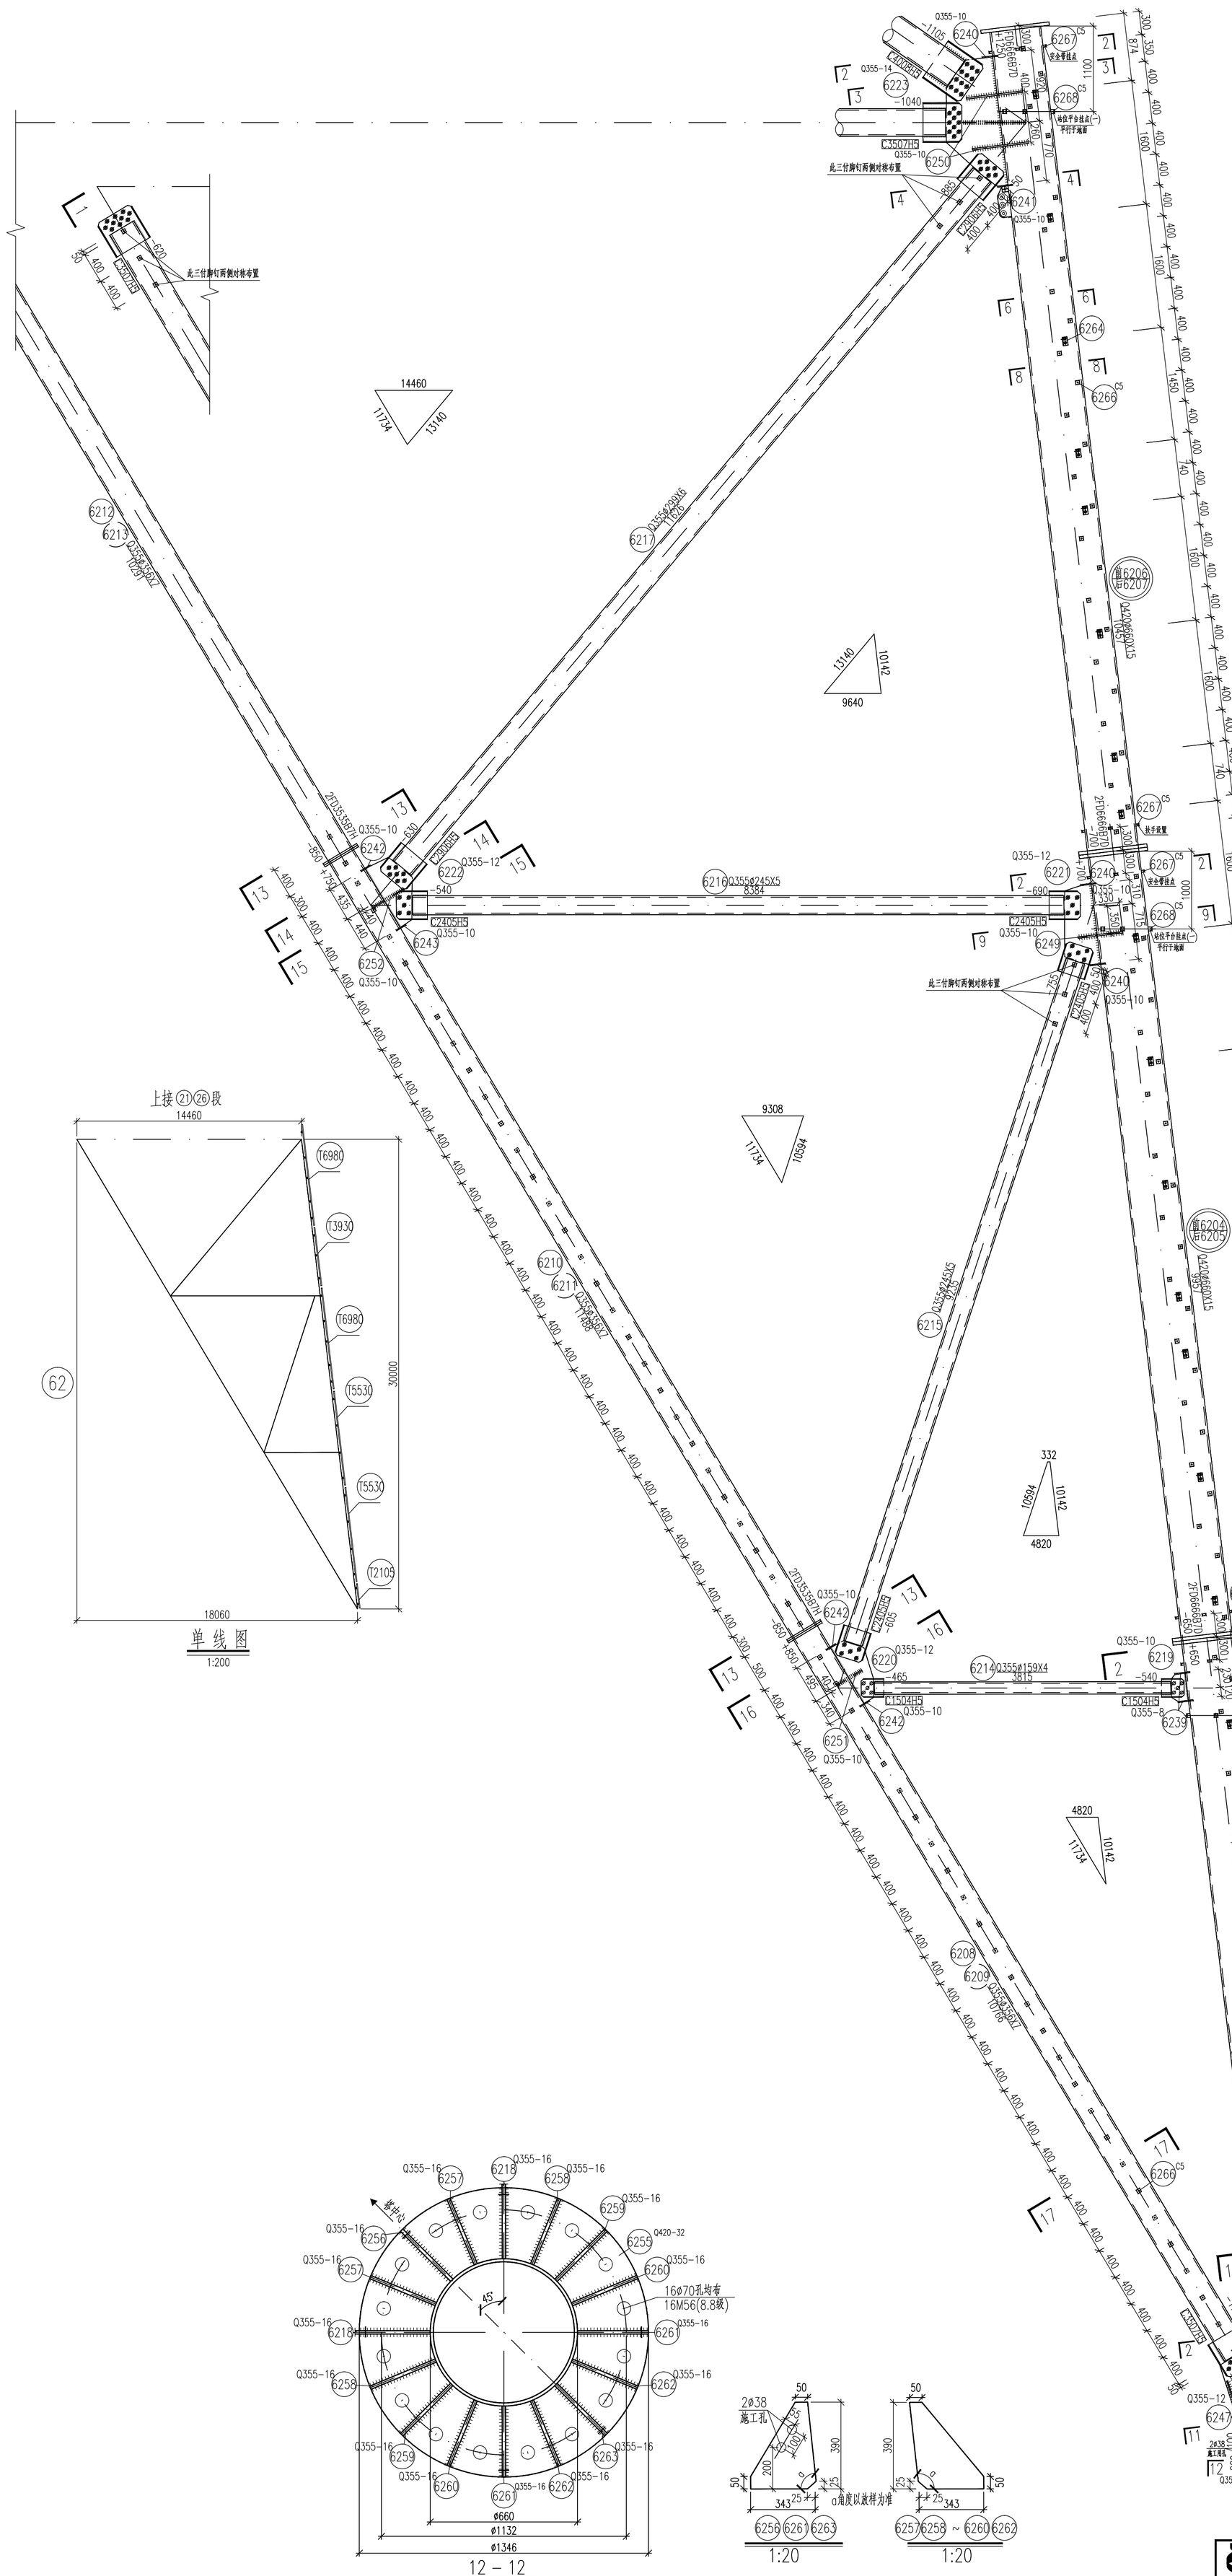


构 件 明 细 表

编号	规 格	长 度 (mm)	数量	重 量 (kg) 一 件	重 量 (kg) 小 计	备 注
6201	Q420@660X15	2337	1	557.61	557.6	一端切弧 装爬梯
6201A	Q420@660X15	2337	0	557.61	0.0	一端切弧 带脚钉
6202	Q420@660X15	8141	1	1942.44	1942.4	装爬梯
6203	Q420@660X15	8141	0	1942.44	0.0	带脚钉
6204	Q420@660X15	9957	1	2375.74	2375.7	装爬梯
6205	Q420@660X15	9957	0	2375.74	0.0	带脚钉
6206	Q420@660X15	10457	1	2495.04	2495.0	装爬梯
6207	Q420@660X15	10457	0	2495.04	0.0	带脚钉
6208	Q355@356X7	10766	1	648.63	648.6	带脚钉
6209	Q355@356X7	10766	1	648.63	648.6	带脚钉
6210	Q355@356X7	11488	1	692.13	692.1	带脚钉
6211	Q355@356X7	11488	1	692.13	692.1	带脚钉
6212	Q355@356X7	10291	1	620.01	620.0	带脚钉
6213	Q355@356X7	10291	1	620.01	620.0	带脚钉
6214	Q355@159X4	3815	2	58.33	116.7	
6215	Q355@245X5	9235	2	273.30	546.6	带脚钉
6216	Q355@245X5	8384	2	248.11	496.2	
6217	Q355@299X6	11626	2	504.04	1008.1	带脚钉
6218	Q355-16X673	1859	2	157.14	314.3	
6219	Q355-10X178	385	2	5.38	10.8	
6220	Q355-12X425	919	2	36.79	73.6	
6221	Q355-12X490	1128	2	52.07	104.1	
6222	Q355-12X518	963	2	46.99	94.0	
6223	Q355-14X793	1859	2	162.01	324.0	
6224	Q355@168X4	5877	1	95.08	95.1	
6225	Q355@245X5	5020	1	148.56	148.6	带脚钉
6226	Q355@245X5	8791	1	260.16	260.2	带脚钉
6227	Q355@245X5	4072	1	120.51	120.5	带脚钉
6228	Q355@245X5	8843	1	261.70	261.7	带脚钉
6229	Q355@299X6	1421	1	61.61	61.6	带脚钉
6230	Q355@299X6	1421	1	61.61	61.6	带脚钉
6231	Q355@299X6	10464	1	453.67	453.7	带脚钉
6232	Q355@299X6	10464	1	453.67	453.7	带脚钉
6233	Q355-12X390	919	2	33.76	67.5	
6234	Q355-10X730	506	1	29.00	29.0	
6235	Q355-10X293	726	2	16.70	33.4	
6236	Q355-12X472	1194	2	53.09	106.2	
6237	Q355-12X485	1056	1	48.25	48.2	
6238	Q355-12X135	1374	1	17.47	17.5	
6239	Q355-8X135	1374	2	11.65	23.3	
6240	Q355-10X135	1374	3	14.56	43.7	
6241	Q355-10X135	1374	1	14.56	14.6	
6242	Q355-10X80	565	6	3.55	21.3	
6243	Q355-10X80	314	2	1.97	3.9	
6244	Q355-10X80	376	2	2.36	4.7	
6245	Q355-8X60	454	4	1.71	6.8	
6246	Q355-10X140	380	2	4.18	8.4	
6247	Q355-12X180	330	4	5.60	22.4	
6248	Q355-12X180	660	2	11.19	22.4	
6249	Q355-10X150	344	4	4.05	16.2	
6250	Q355-10X150	509	8	5.99	47.9	
6251	Q355-10X200	241	2	3.78	7.6	
6252	Q355-10X300	284	2	6.69	13.4	
6253	-16X885	885	1	77.26	77.3	遮水板
6254	Q355-8X80	110	1	0.55	0.6	接地孔用
6255	Q420-32X1346	1346	1	272.50	272.5	
6256	Q355-16X343	390	1	16.80	16.8	
6257	Q355-16X343	390	2	16.80	33.6	
6258	Q355-16X343	390	2	16.80	33.6	
6259	Q355-16X343	390	2	16.80	33.6	
6260	Q355-16X343	390	2	16.80	33.6	
6261	Q355-16X343	390	2	16.80	33.6	
6262	Q355-16X343	390	2	16.80	33.6	
6263	Q355-16X343	390	1	16.80	16.8	
6264	Q355L63X5	310	22	1.49	32.8	火曲 (用于主材装爬梯)
6265	Q355-6X100	180	22	0.85	18.7	火曲 (用于主材装爬梯)
6266	C5	50	247	0.27	66.7	槽钢 (用于主材装爬梯)
6266	C5	50	323	0.27	87.2	槽钢 (用于主材带脚钉)
6267	C5	25	20	0.14	2.8	槽钢
6268	C5	50	12	0.27	3.2	槽钢
6269	Q355-14X210	550	1	12.69	12.7	
6270	Q355-38X104	104	3	3.23	9.7	
6271	Q355-10X100	115	2	0.90	1.8	
6272	Q355-6X50	100	1	0.24	0.2	
6273	Q355-12X100	797	2	7.51	15.0	
	C1504H5		4	6.52	26.1	
	C1604H5		2	7.12	14.2	
	C2405H5		12	17.27	207.2	
	C2906H5		8	23.31	186.5	
	X2405H7		2	33.90	67.8	
	C3507H5		4	36.27	145.1	
	FD2424B7H		2	10.40	20.8	
	FD2929B7H		4	15.70	62.8	
	FD3535B7H		8	22.10	176.8	
	FD6666B7D		7	116.50	815.5	
	T2105		1	11.50	11.5	(用于主材装爬梯)
	T3930		1	20.70	20.7	(用于主材装爬梯)
	T5530		2	28.80	57.6	(用于主材装爬梯)
	T6980		2	36.20	72.4	(用于主材装爬梯)
合 计		19296.6 kg(用于主材带脚钉)				
合 计		19489.8 kg(用于主材装爬梯)				

螺栓、脚钉、垫圈 明细表

名称	级别	规 格	符 号	数量	重量(kg)	备 注
螺栓	6.8级	M16X45		88	14.8	用于主材装爬梯
		M20X65		30	10.6	
		M20X75		48	18.2	
	8.8级	M24X75		180	106.7	
		M20X90		14	6.6	法兰螺栓
		M20X100		40	19.8	法兰螺栓
		M24X115		88	73.9	法兰螺栓
		M39X175		84	298.3	法兰螺栓
		M39X195		28	104.7	法兰螺栓 无扣长97mm
脚钉	6.8级	M16X200		247	108.3	用于主材装爬梯
		M16X200		323	141.6	用于主材带脚钉
垫圈	Q235		规格X个数			
合 计			780.4 kg (用于主材带脚钉)			
合 计			761.9 kg (用于主材装爬梯)			

说明：1.材料表为一个塔腿的重量。

2.本段塔腿为铁塔D腿，安装爬梯，
当为A、B、C腿时需焊接脚钉连接槽钢。

山东电力工程咨询院有限公司			浙江特高压交流环网工程线路	工程	施工图 设计阶段
批 准	高锡鹏	校 核		SZK31102A双回路直线塔	
审 核		设计/勘测		129.0-0.0m呼高腿部结构图(1/3)	62
电气 赵庆周	2026.08	比 例	1:40	日 期	2026年08月
专业 会签	日 期			图 号	37-SA36901S-T0121-139
				版本	