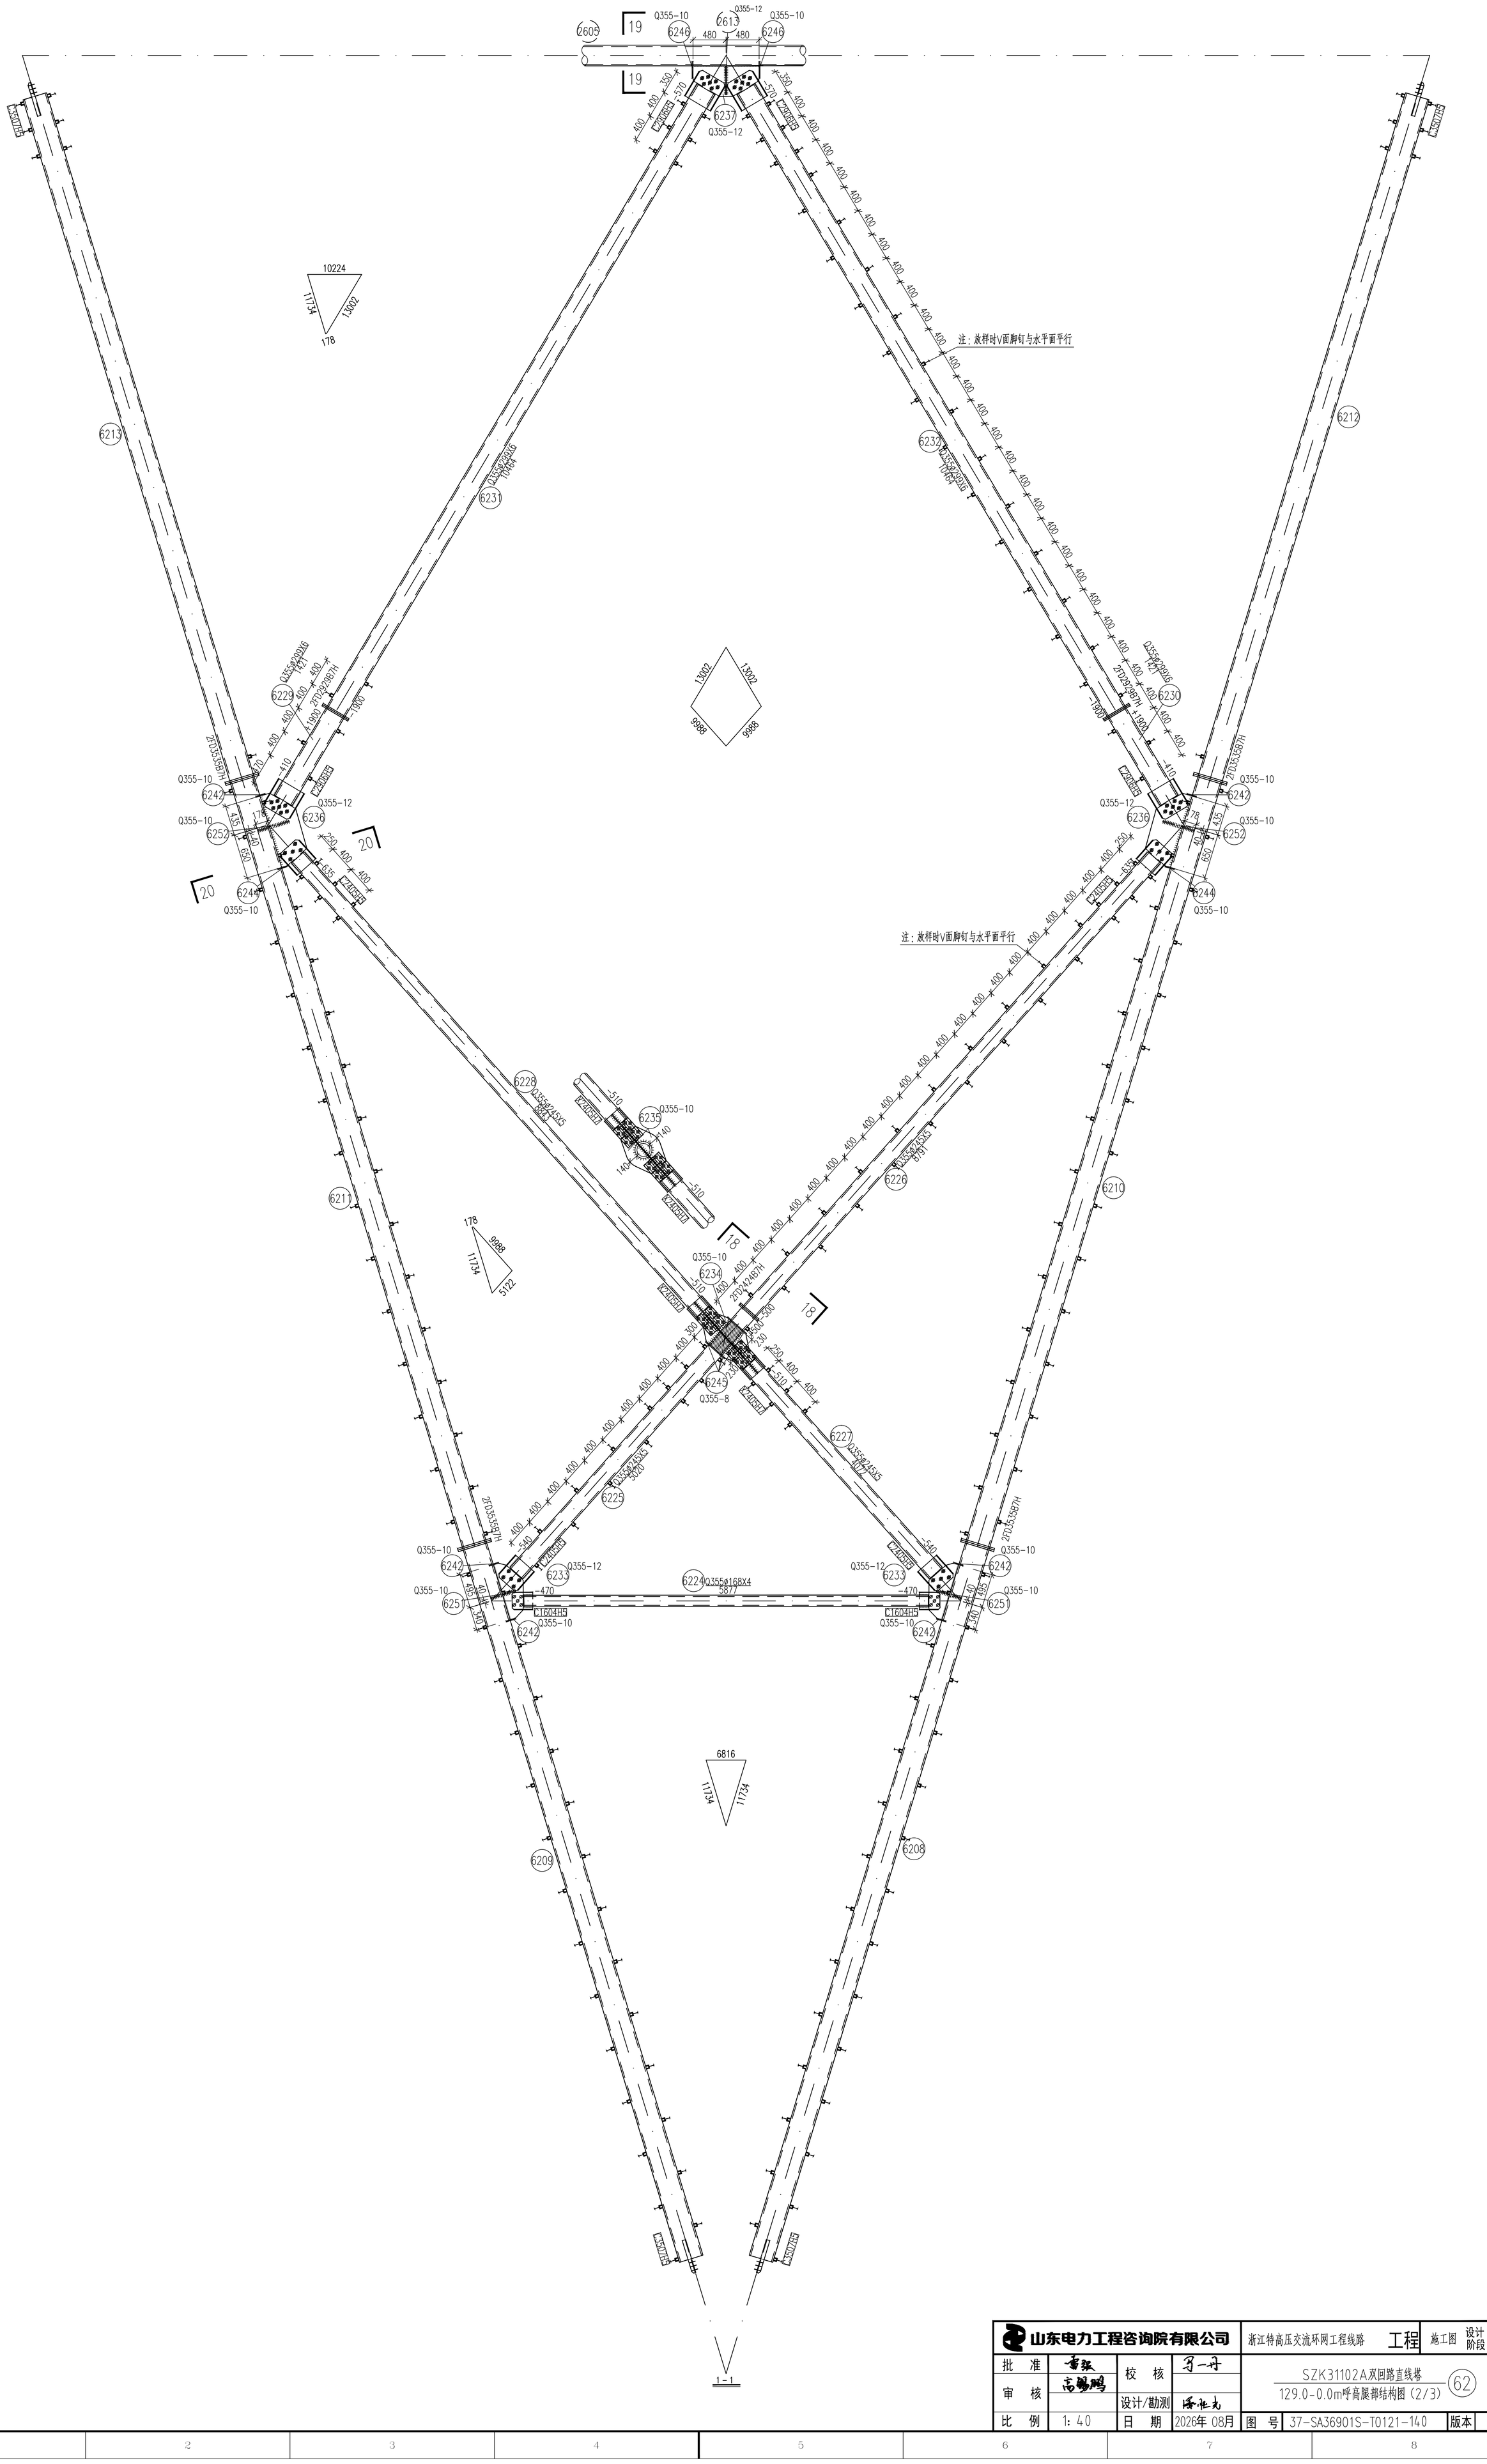


山东电力工程咨询院有限公司				浙江特高压交流环网工程线路 工程	施工图 设计阶段
批 准	雷强	校 核	习一舟	SZK31102A双回路直线塔 129.0-0.0m呼高腿部结构图（2/3）	62
审 核	高锡鹏				
		设计/勘测	潘世光		
比 例	1:40	日 期	2026年 08月	图 号 37-SA36901S-T0121-140	版本