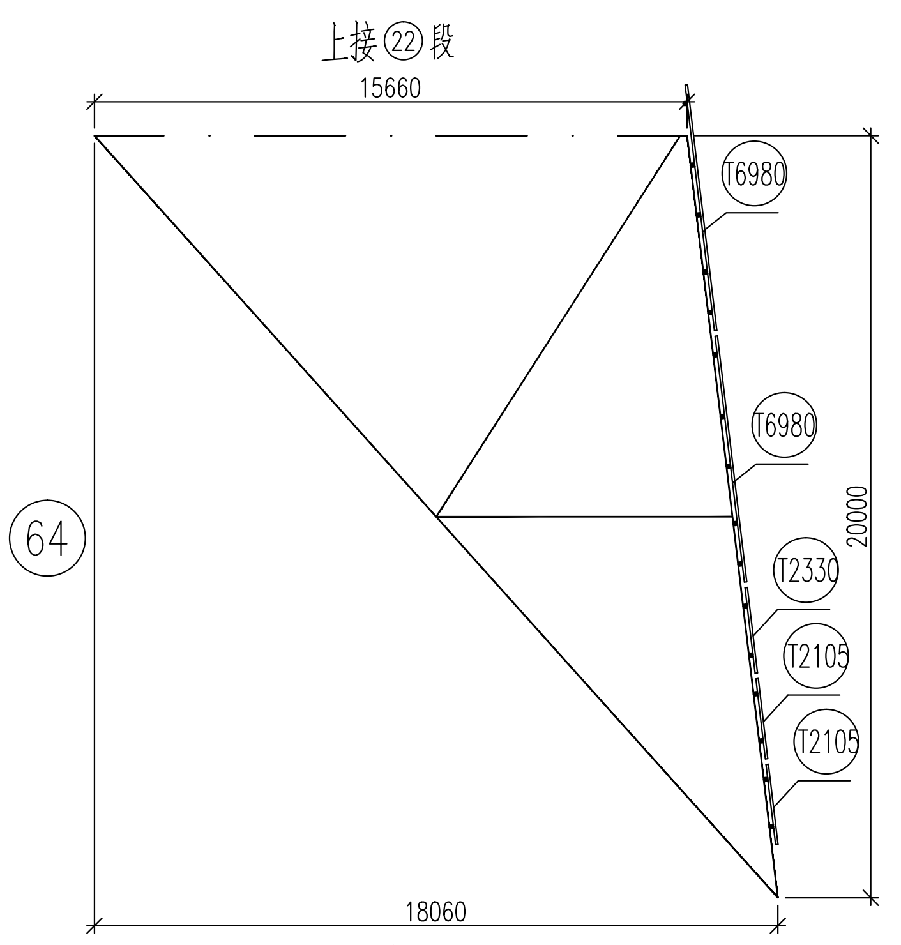
上接㉒段
15660
18060
20000
64
T6980
T6980
T2330
T2105
T2105

单线图
1:200

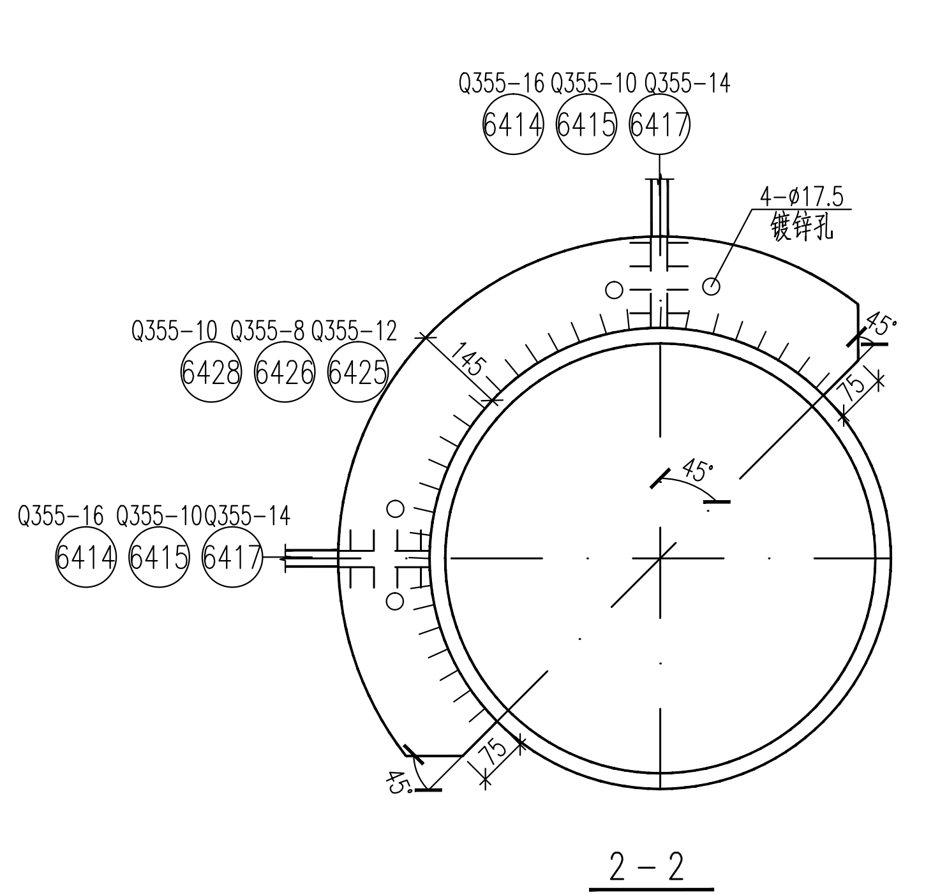
Q355-16 Q355-10 Q355-14
6414 6415 6417
4-ø17.5 镀锌孔
Q355-10 Q355-8 Q355-12
6428 6426 6425
Q355-16 Q355-10 Q355-14
6414 6415 6417
45°

2－2
1:20

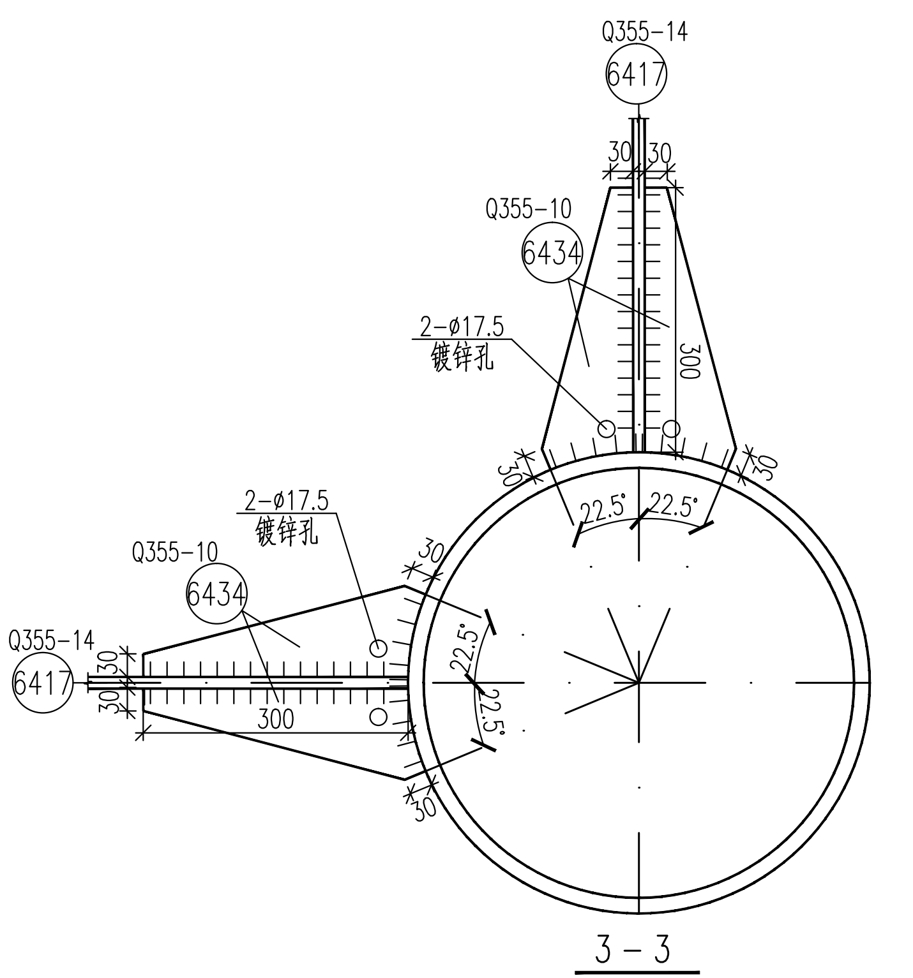
Q355-14
6417
Q355-10
6434
2-ø17.5 镀锌孔
300
22.5°

3－3
1:20

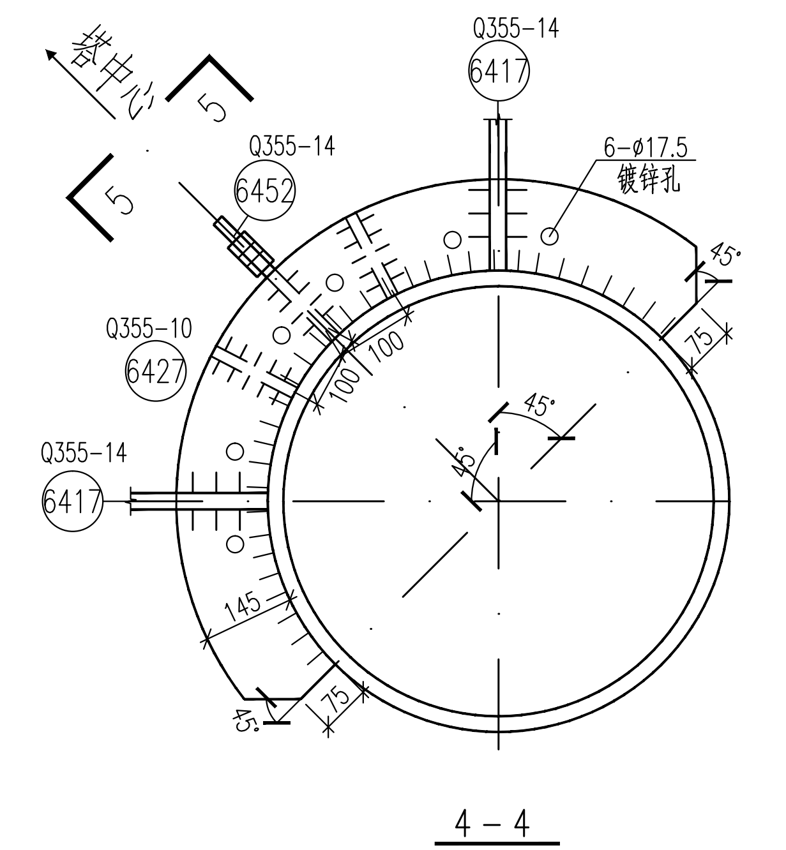
塔中心
Q355-14
6417
Q355-14
6452
6-ø17.5 镀锌孔
Q355-10
6427
Q355-14
6417
45°

4－4
1:20

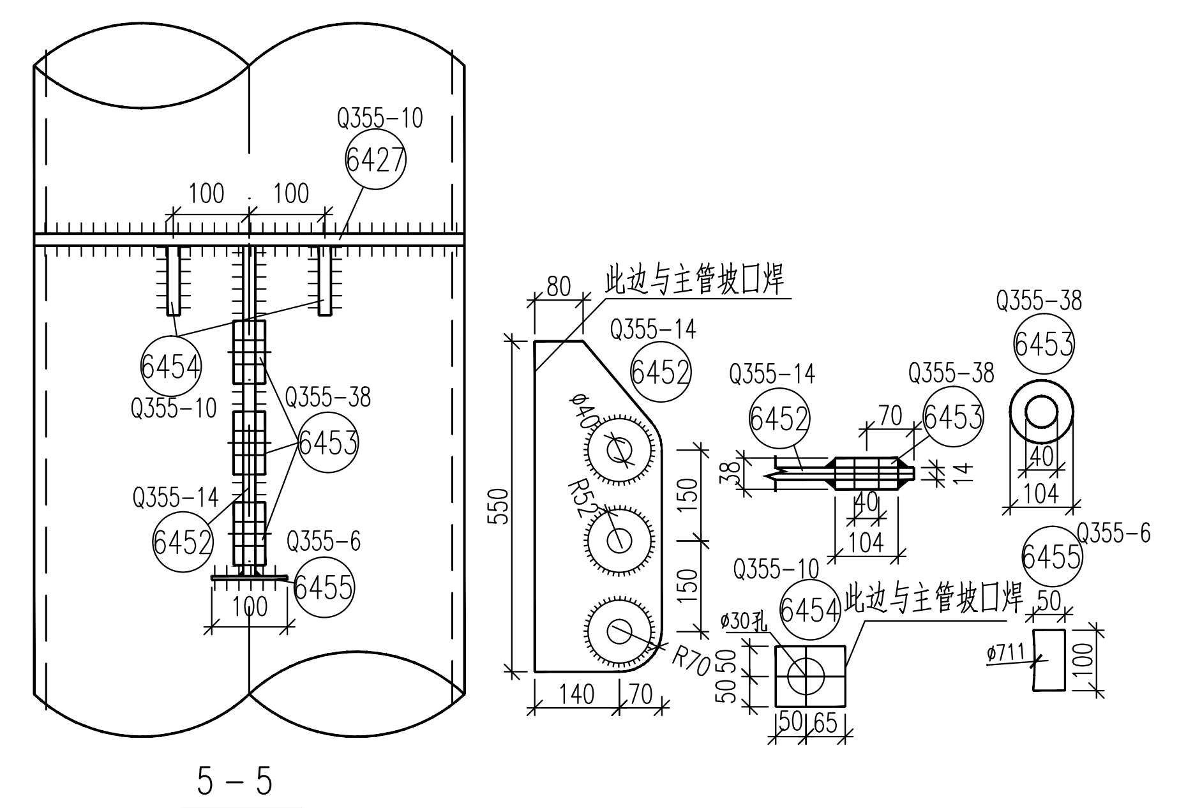
Q355-10
6427
100 100
6454
Q355-10
6453
Q355-38
6452
Q355-14
6455
Q355-6
此边与主管坡口焊
Q355-14
6452
Q355-38
6453
Q355-6
6455
Q355-10
6454
此边与主管坡口焊
550

5－5
1:20

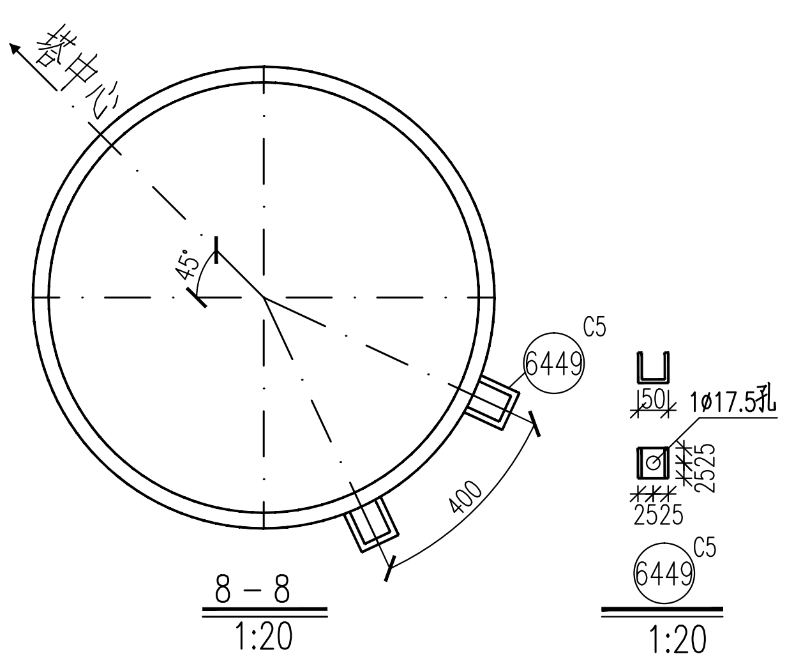
塔中心
C5
6449
1ø17.5孔
C5
6449
400
45°

8－8
1:20

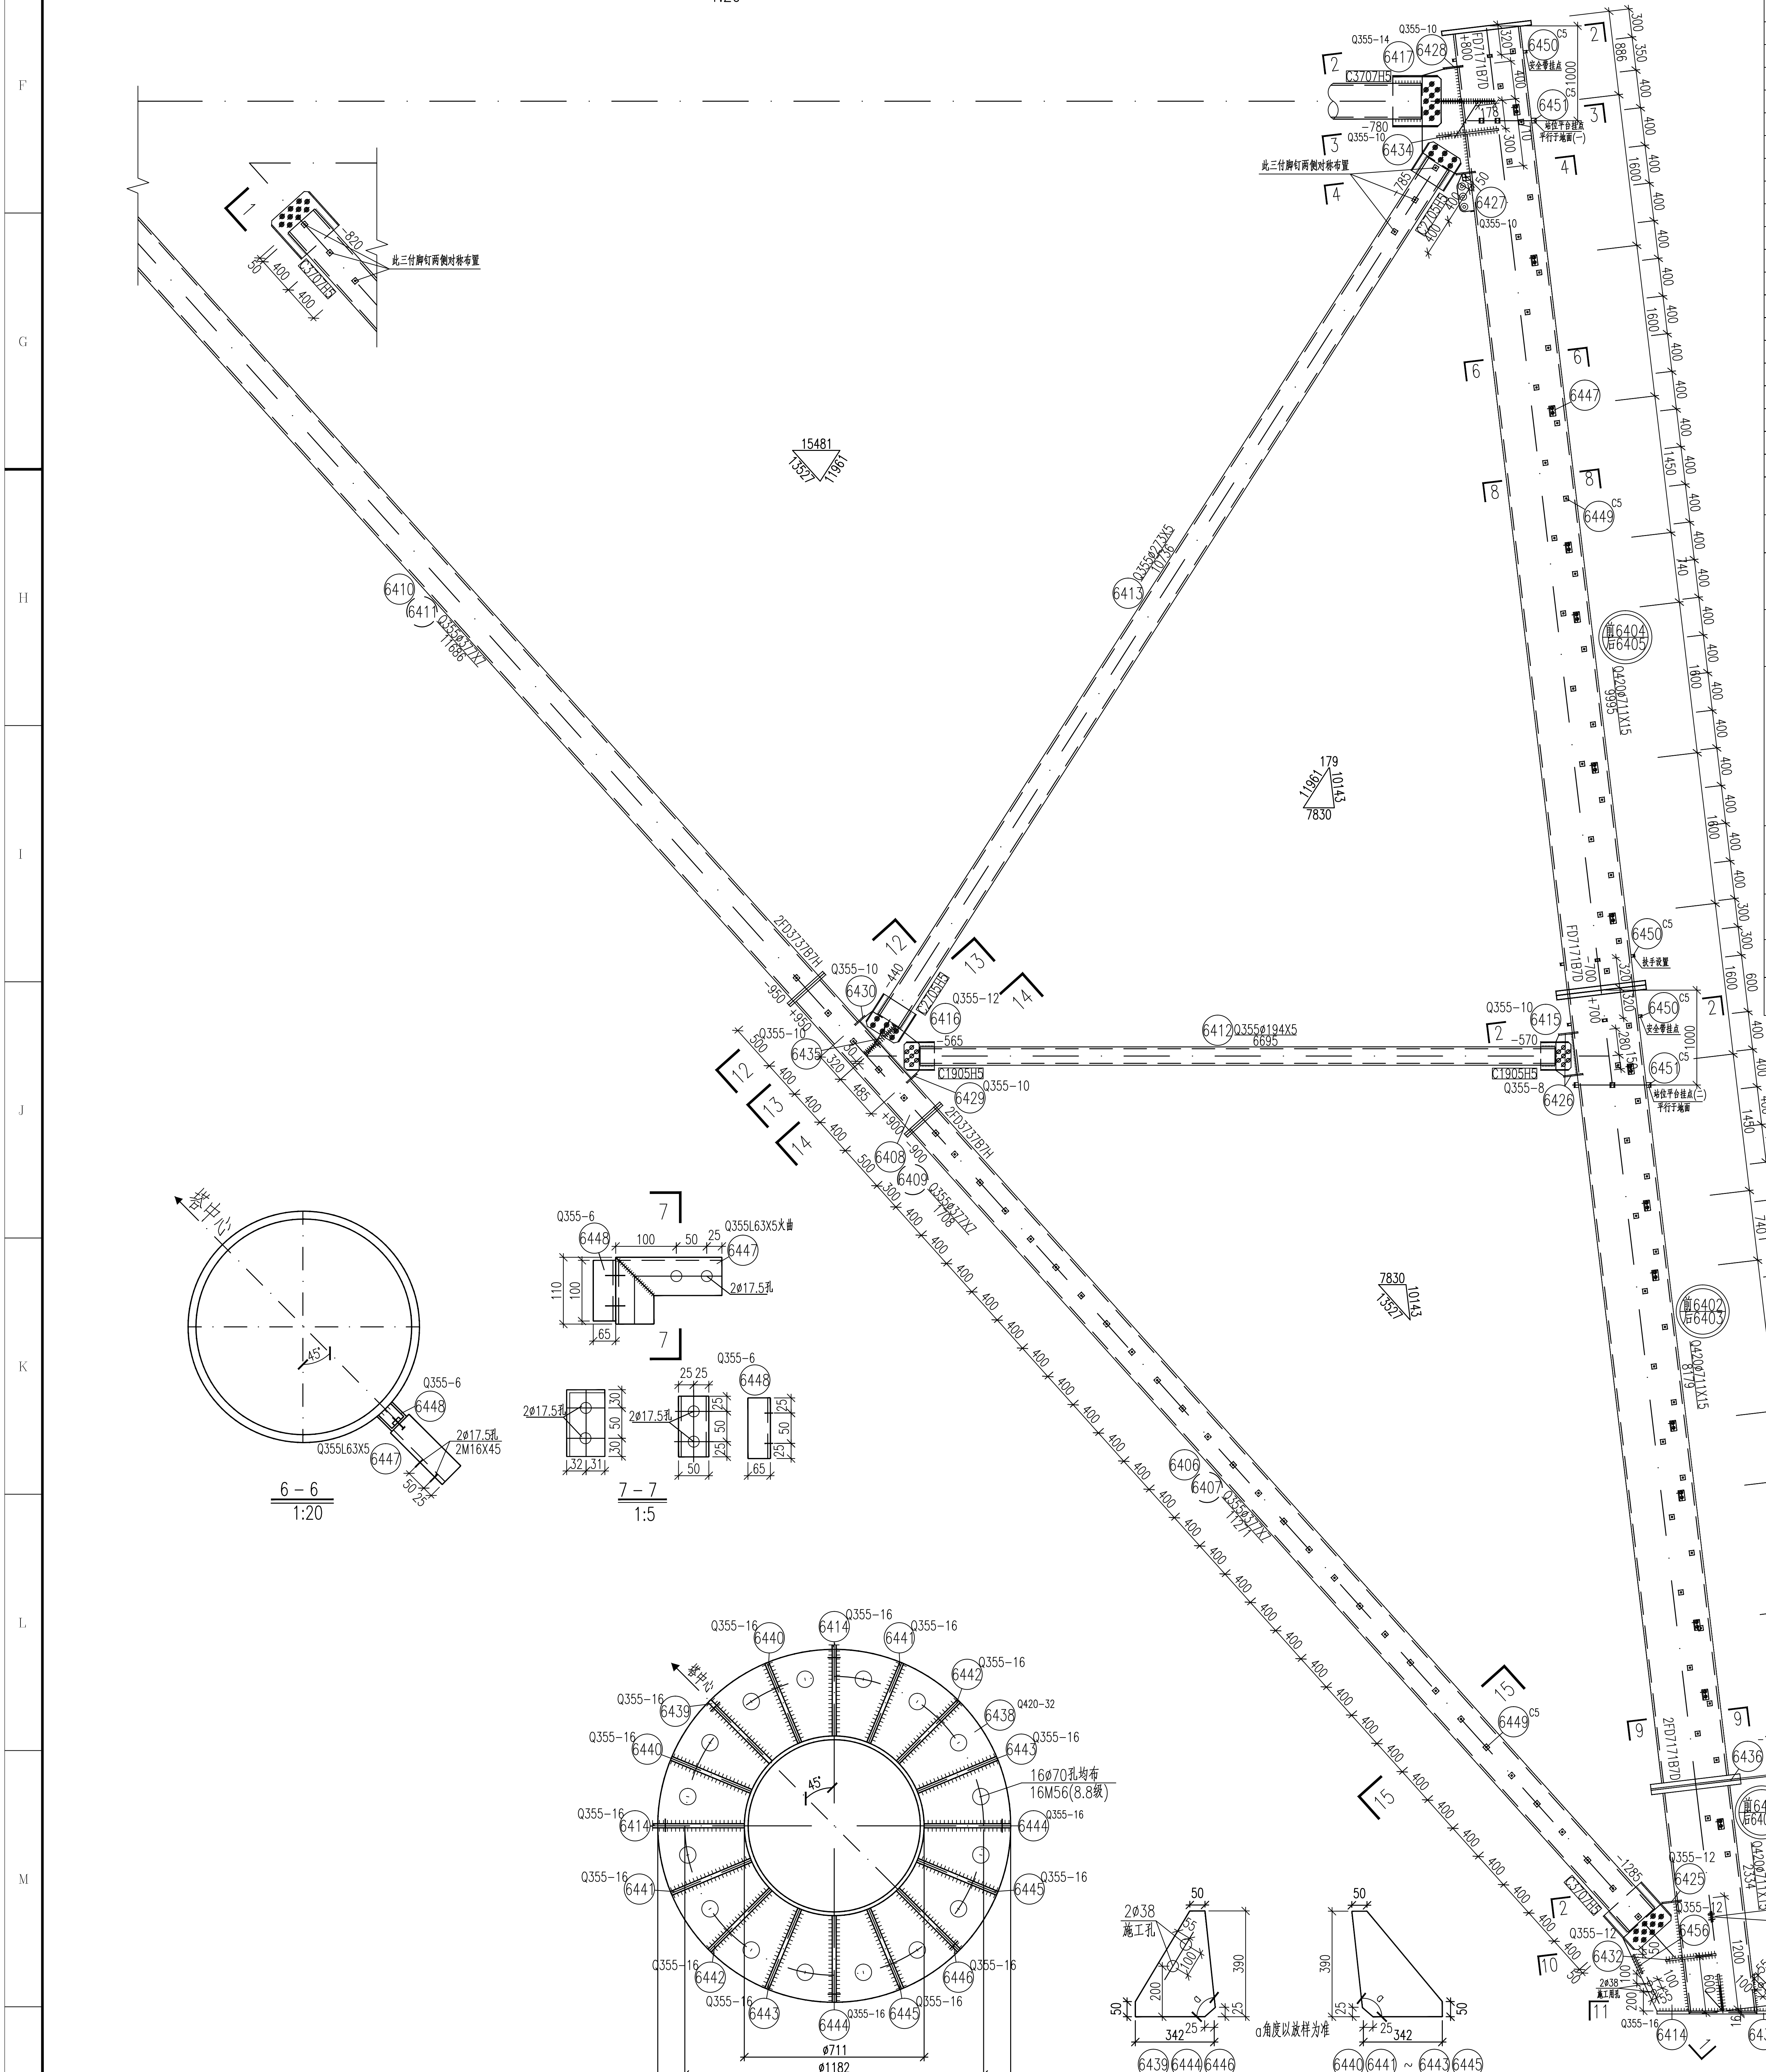
6410
6411
6413
6412 Q355ø194X5 6695
6406
6407
6408
6409
6402
6403
6404
6405
6401
6401A
FD3232B7H
FD3737B7H
FD7171B7D
C3707H5
C1905H5
C2705H5
15481
7830
此三付脚钉两侧对称布置
6-6
1:20
7-7
1:5
11-11
1:20
16ø70孔均布
16M56(8.8级)
ø711
ø1182
ø1396
2ø38 施工孔
α角度以放样为准
6439 6444 6446
6440 6441 ~ 6443 6445
1:20

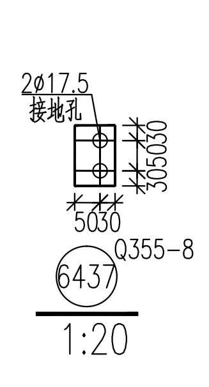
2ø17.5 接地孔
Q355-8
6437

1:20

构　件　明　细　表

编号	规格	长度(mm)	数量	重量(kg) 一件	重量(kg) 小计	备注
6401	Q420ø711X15	2334	1	600.93	600.9	一端切弧 装爬梯
6401A	Q420ø711X15	2334	0	600.93	0.0	一端切弧 带脚钉
6402	Q420ø711X15	8179	1	2105.82	2105.8	装爬梯
6403	Q420ø711X15	8179	0	2105.82	0.0	带脚钉
6404	Q420ø711X15	9995	1	2573.37	2573.4	装爬梯
6405	Q420ø711X15	9995	0	2573.37	0.0	带脚钉
6406	Q355ø377X7	11271	1	719.92	719.9	带脚钉
6407	Q355ø377X7	11271	1	719.92	719.9	带脚钉
6408	Q355ø377X7	1708	1	109.10	109.1	带脚钉
6409	Q355ø377X7	1708	1	109.10	109.1	带脚钉
6410	Q355ø377X7	11686	1	746.42	746.4	带脚钉
6411	Q355ø377X7	11686	1	746.42	746.4	带脚钉
6412	Q355ø194X5	6695	2	156.03	312.1	
6413	Q355ø273X5	10736	2	354.79	709.6	带脚钉
6414	Q355-16X658	1320	2	109.09	218.2	
6415	Q355-10X238	473	2	8.84	17.7	
6416	Q355-12X360	886	2	30.05	60.1	
6417	Q355-14X523	1221	2	70.18	140.4	
6418	Q355ø273X5	10113	1	334.20	334.2	
6419	Q355ø325X6	1256	1	59.29	59.3	带脚钉
6420	Q355ø325X6	1256	1	59.29	59.3	带脚钉
6421	Q355ø325X6	10865	1	512.85	512.8	带脚钉
6422	Q355ø325X6	10865	1	512.85	512.8	带脚钉
6423	Q355-14X507	1100	2	61.29	122.6	
6424	Q355-14X464	1144	1	58.34	58.3	
6425	Q355-12X145	1480	1	20.22	20.2	
6426	Q355-8X145	1480	2	13.48	27.0	
6427	Q355-10X145	1480	1	16.85	16.8	
6428	Q355-10X145	1480	1	16.85	16.8	
6429	Q355-10X80	395	4	2.48	9.9	
6430	Q355-10X80	329	4	2.07	8.3	
6431	Q355-10X180	437	2	6.17	12.3	
6432	Q355-12X180	350	2	5.93	11.9	
6433	Q355-12X180	700	1	11.87	11.9	
6434	Q355-10X150	399	4	4.70	18.8	
6435	Q355-10X200	252	2	3.96	7.9	
6436	-16X950	950	1	89.03	89.0	遮水板
6437	Q355-8X80	110	1	0.55	0.6	接地孔用
6438	Q420-32X1396	1396	1	284.75	284.8	
6439	Q355-16X342	390	1	16.75	16.8	
6440	Q355-16X342	390	2	16.75	33.5	
6441	Q355-16X342	390	2	16.75	33.5	
6442	Q355-16X342	390	2	16.75	33.5	
6443	Q355-16X342	390	2	16.75	33.5	
6444	Q355-16X342	390	2	16.75	33.5	
6445	Q355-16X342	390	2	16.75	33.5	
6446	Q355-16X342	390	1	16.75	16.8	
6447	Q355L63X5	285	15	1.37	20.6	火曲 (用于主材装爬梯)
6448	Q355-6X100	180	15	0.85	12.8	火曲 (用于主材装爬梯)
6449	C5	50	135	0.27	36.4	槽钢 (用于主材装爬梯)
6449	C5	50	184	0.27	49.7	槽钢 (用于主材带脚钉)
6450	C5	25	12	0.14	1.7	槽钢
6451	C5	50	8	0.27	2.2	槽钢
6452	Q355-14X210	550	1	12.69	12.7	
6453	Q355-38X104	104	3	3.23	9.7	
6454	Q355-10X100	115	2	0.90	1.8	
6455	Q355-6X50	100	1	0.24	0.2	
6456	Q355-12X100	221	2	2.08	4.2	
	C1905H5		4	8.80	35.2	
	C2705H5		6	18.10	108.6	
	C3206H5		4	31.43	125.7	
	C3707H5		4	39.39	157.6	
	FD3232B7H		4	16.80	67.2	
	FD3737B7H		8	21.70	173.6	
	FD7171B7D		5	142.30	711.5	
	T2105		2	11.50	23.0	(用于主材装爬梯)
	T2330		1	12.40	12.4	(用于主材装爬梯)
	T6980		2	36.20	72.4	(用于主材装爬梯)
合计	13780.7 kg(用于主材带脚钉)					
合计	13908.6 kg(用于主材装爬梯)					

螺栓、脚钉、垫圈明细表

名称	级别	规格	符号	数量	重量(kg)	备注
螺栓	6.8级	M16X45	◎	60	10.1	用于主材装爬梯
		M20X65	∅	28	9.9	
	8.8级	M24X75	∅	104	61.7	
		M20X100	○	44	21.8	法兰螺栓
		M24X110	○	88	72.4	法兰螺栓
		M42X190	○	56	250.7	法兰螺栓
		M42X205	○	28	131.5	法兰螺栓 无扣长101mm
脚钉	6.8级	M16X200	⊖	135	59.2	用于主材装爬梯
		M16X200	⊣	184	80.6	用于主材带脚钉
垫圈	Q235		规格X个数			
合计	628.6 kg (用于主材带脚钉)					
合计	617.3 kg (用于主材装爬梯)					

说明：1.材料表为一个塔腿的重量。

2.本段塔腿为铁塔D腿，安装爬梯，当为A、B、C腿时需焊接脚钉连接槽钢。

			山东电力工程咨询院有限公司				浙江特高压交流环网工程线路　工程	施工图 设计阶段
			批准		校核		SZK31102A双回路直线塔 132.0-3.0m呼高腿部结构图 (1/2)	64
			审核	高锡鹏	设计/勘测			
电气	赵庆周	2026.08						
专业	会签	日期	比例	1: 40	日期	2026年 08月	图号 37-SA36901S-T0121-144	版本