

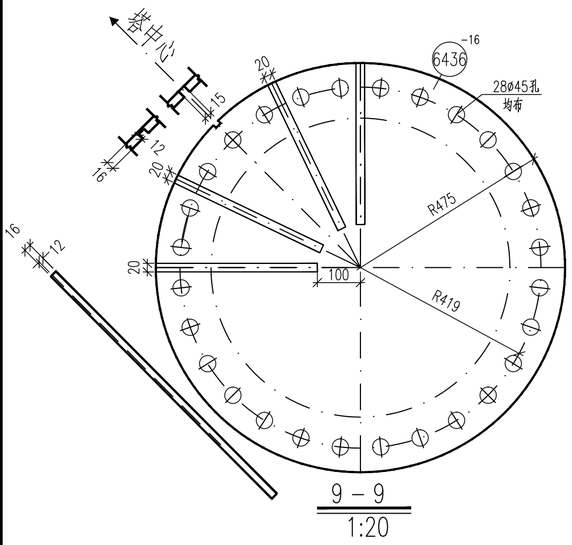



9 – 9
1:20

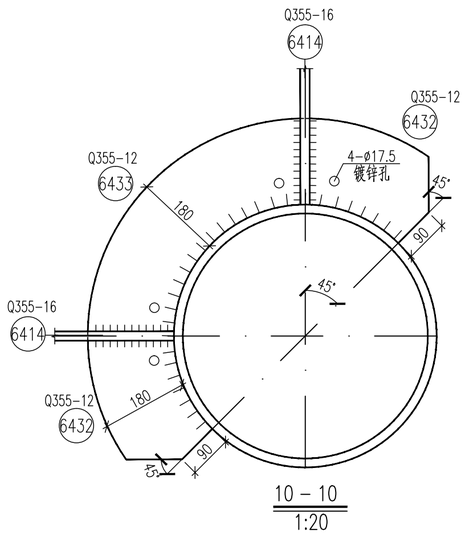


10 – 10
1:20

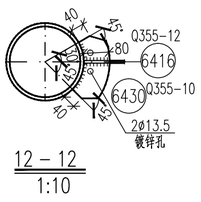


12 – 12
1:10

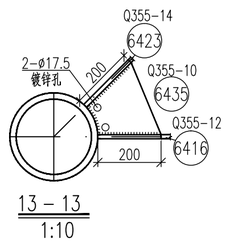


13 – 13
1:10

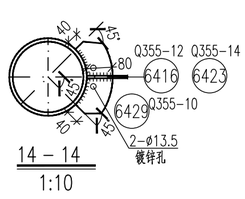


14 – 14
1:10

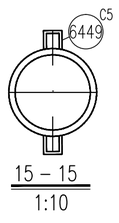


15 – 15
1:10

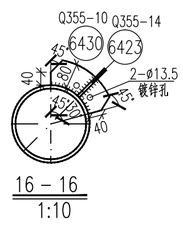


16 – 16
1:10

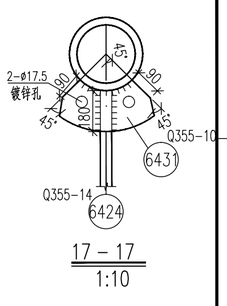

17 – 17
1:10

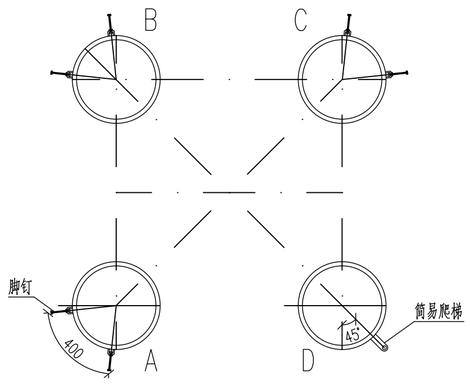


爬梯脚钉示意图

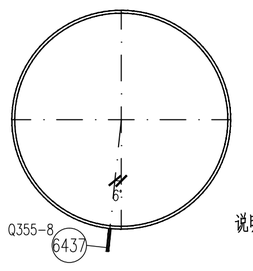


接地孔位置示意图
1:20


说明：接地孔安装板(6437)避开法兰加劲板和地脚法兰螺栓所在角度,以避免接地引下线和法兰加劲板相碰.

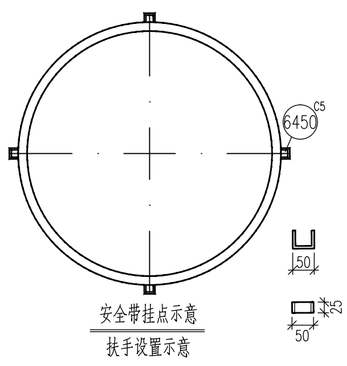


安全带挂点示意
扶手设置示意

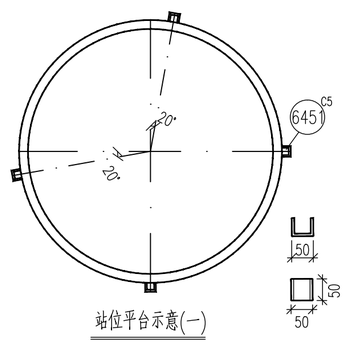

站位平台示意(一)

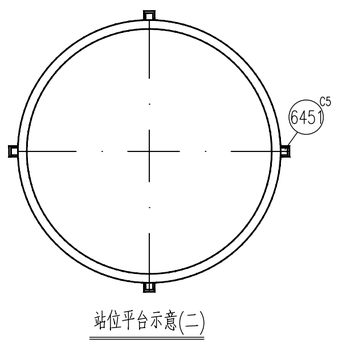

站位平台示意(二)

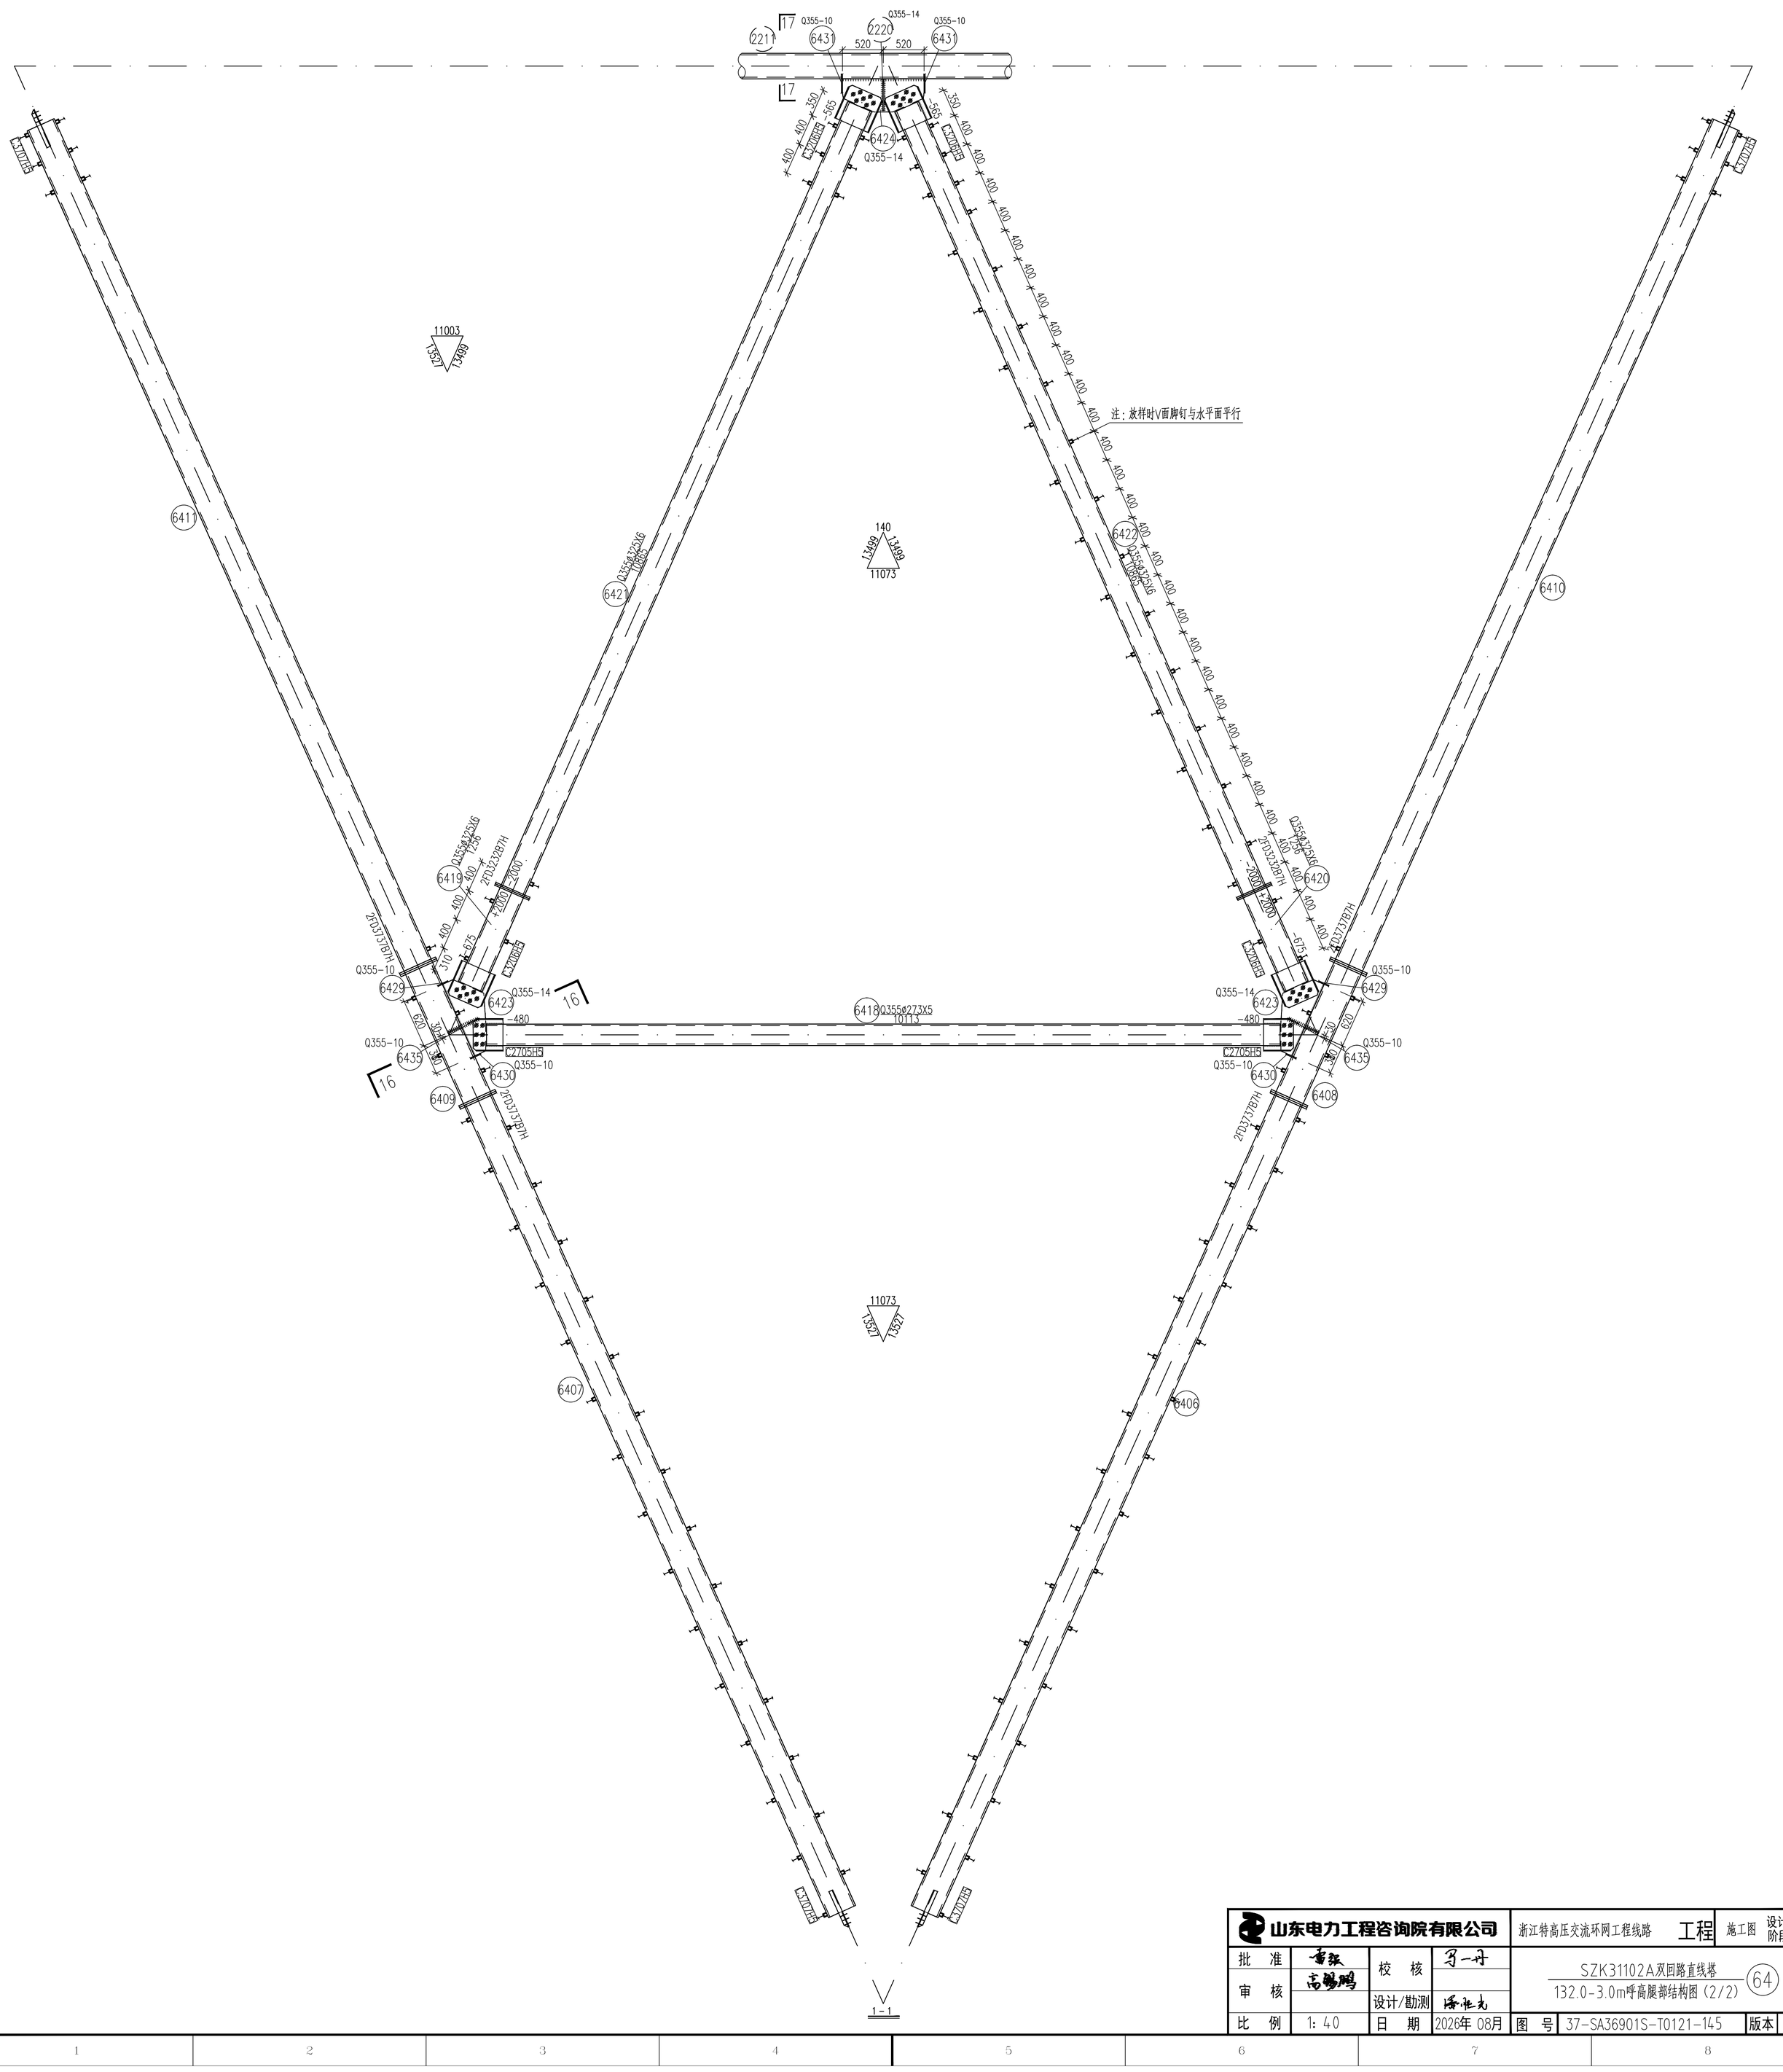

山东电力工程咨询院有限公司				浙江特高压交流环网工程线路 工程	施工图 设计阶段
批 准	雷强	校 核	习一舟	SZK31102A双回路直线塔 132.0-3.0m呼高腰部结构图（2/2）	64
审 核	高锡鹏	设计/勘测	潘世光		
比 例	1:40	日 期	2026年 08月	图 号 37-SA36901S-T0121-145	版本